


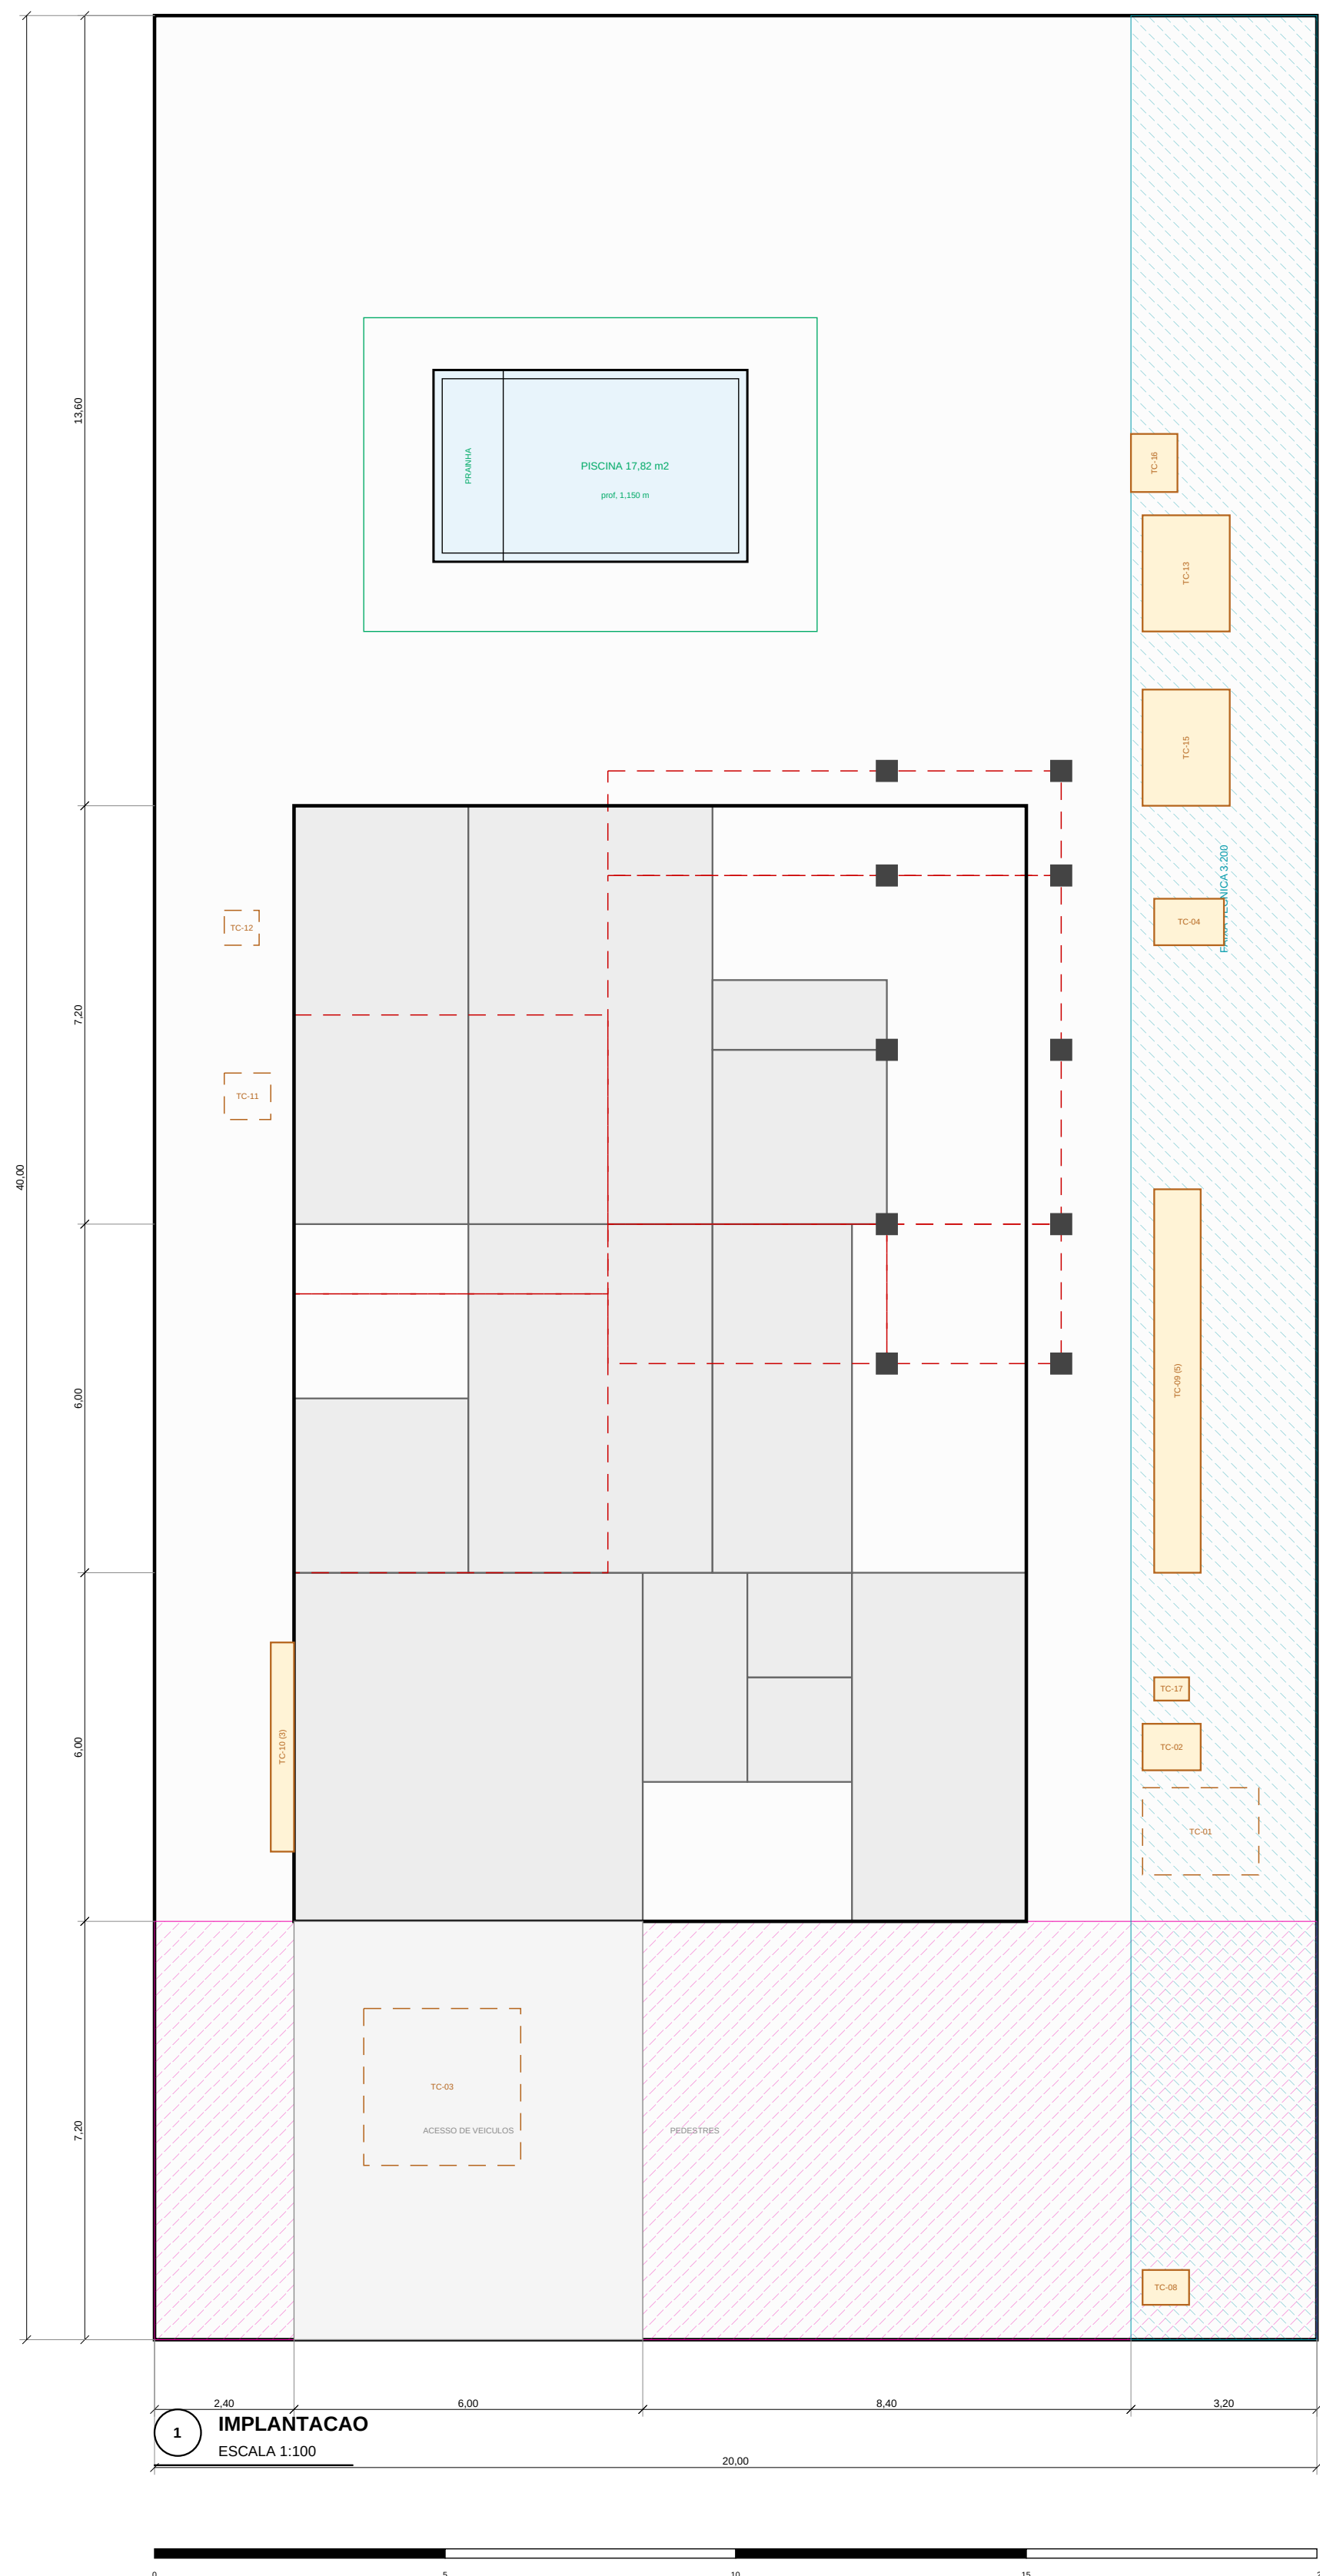

PARAMETRO	PROJETO	LIMITE	
Taxa de ocupação	32,21 %	max 50 %	OK
Coef. de aproveitamento	0,372	max 1,00	OK
Cobertura	2 pavimentos	max 4	OK
Recuo frontal	7000 mm	condomínio SGU2 (ii)	OK
Recuo lateral eqs.	2400 mm	sem parâmetro definido	OK
Faixa bruta de div.	3300 mm	min 3000 mm	OK
Recuo de fundo	13000 mm	min 5000 mm	OK

- Lote 20.000 x 40.000 mm = 800.00 m².
- Recuos: frontal 7.200 / lateral esq. 2.400 / faixa técnica de: 3.200 / fundo 13.600 mm.
- Parâmetros do SUDS Tarumã/Tarumã-Açu são hipóteses (H) – pendente certidão de uso do solo.
- Sem muro frontal, muros laterais e de fundo h = 2.200 mm.

RESIDÊNCIA UNIFAMILIAR | MANAUS - AM | SU16 TARUMA (H)

--	--

ESCALA

1:100

FORMATO A1

MALHA 606/300/250

PRANCHIA

01

de 43 REV R62