



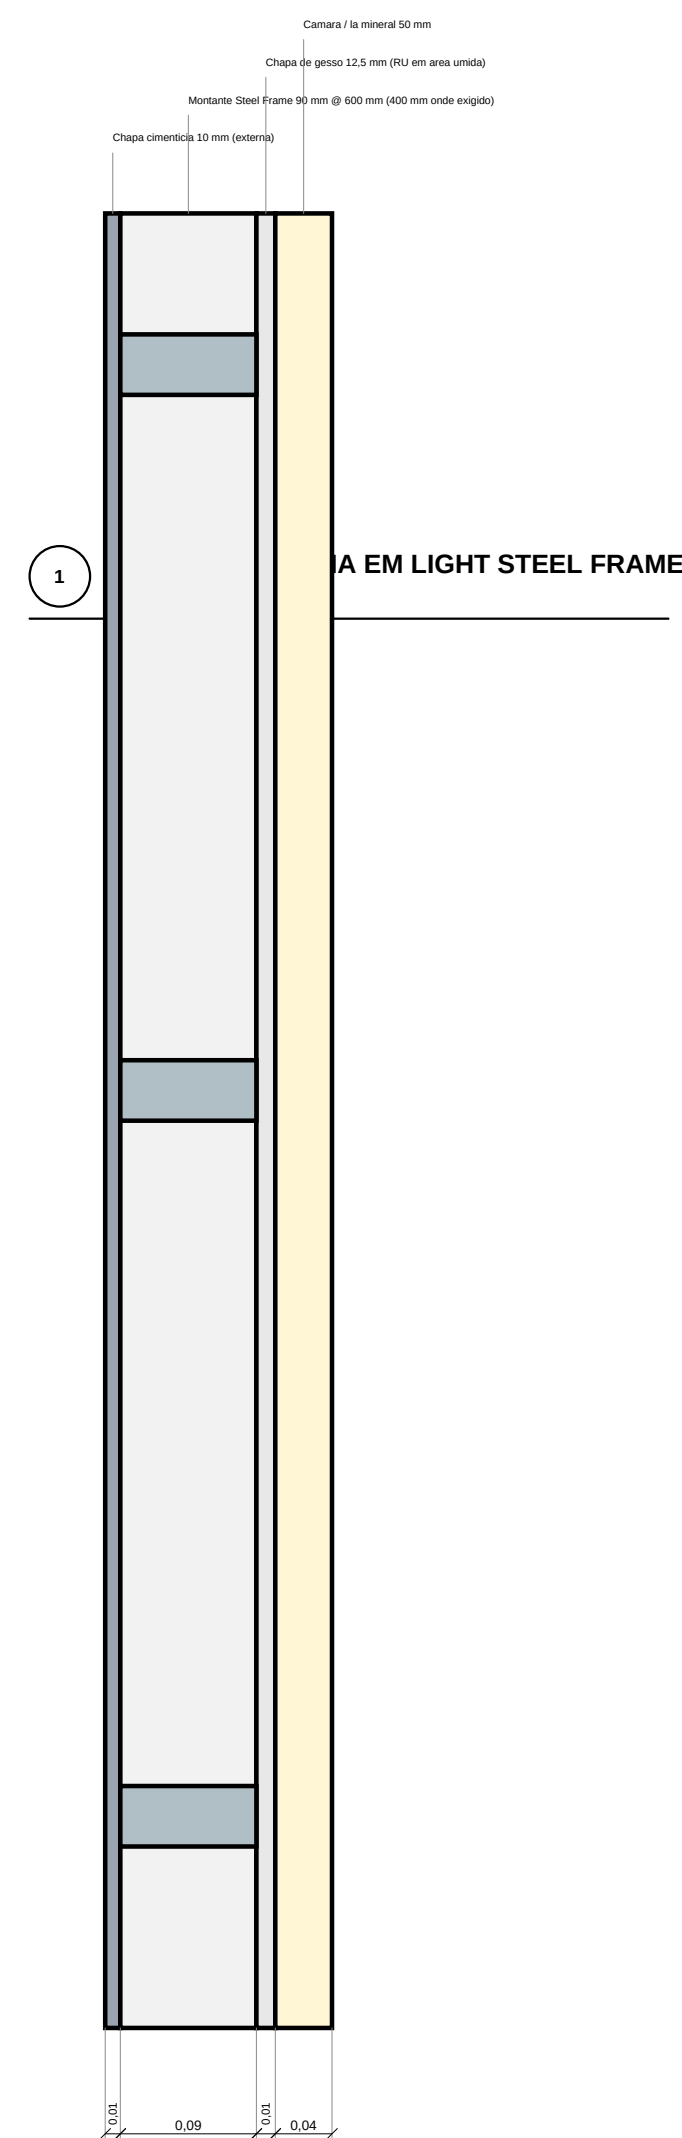


A EM LIGHT STEEL FRAME

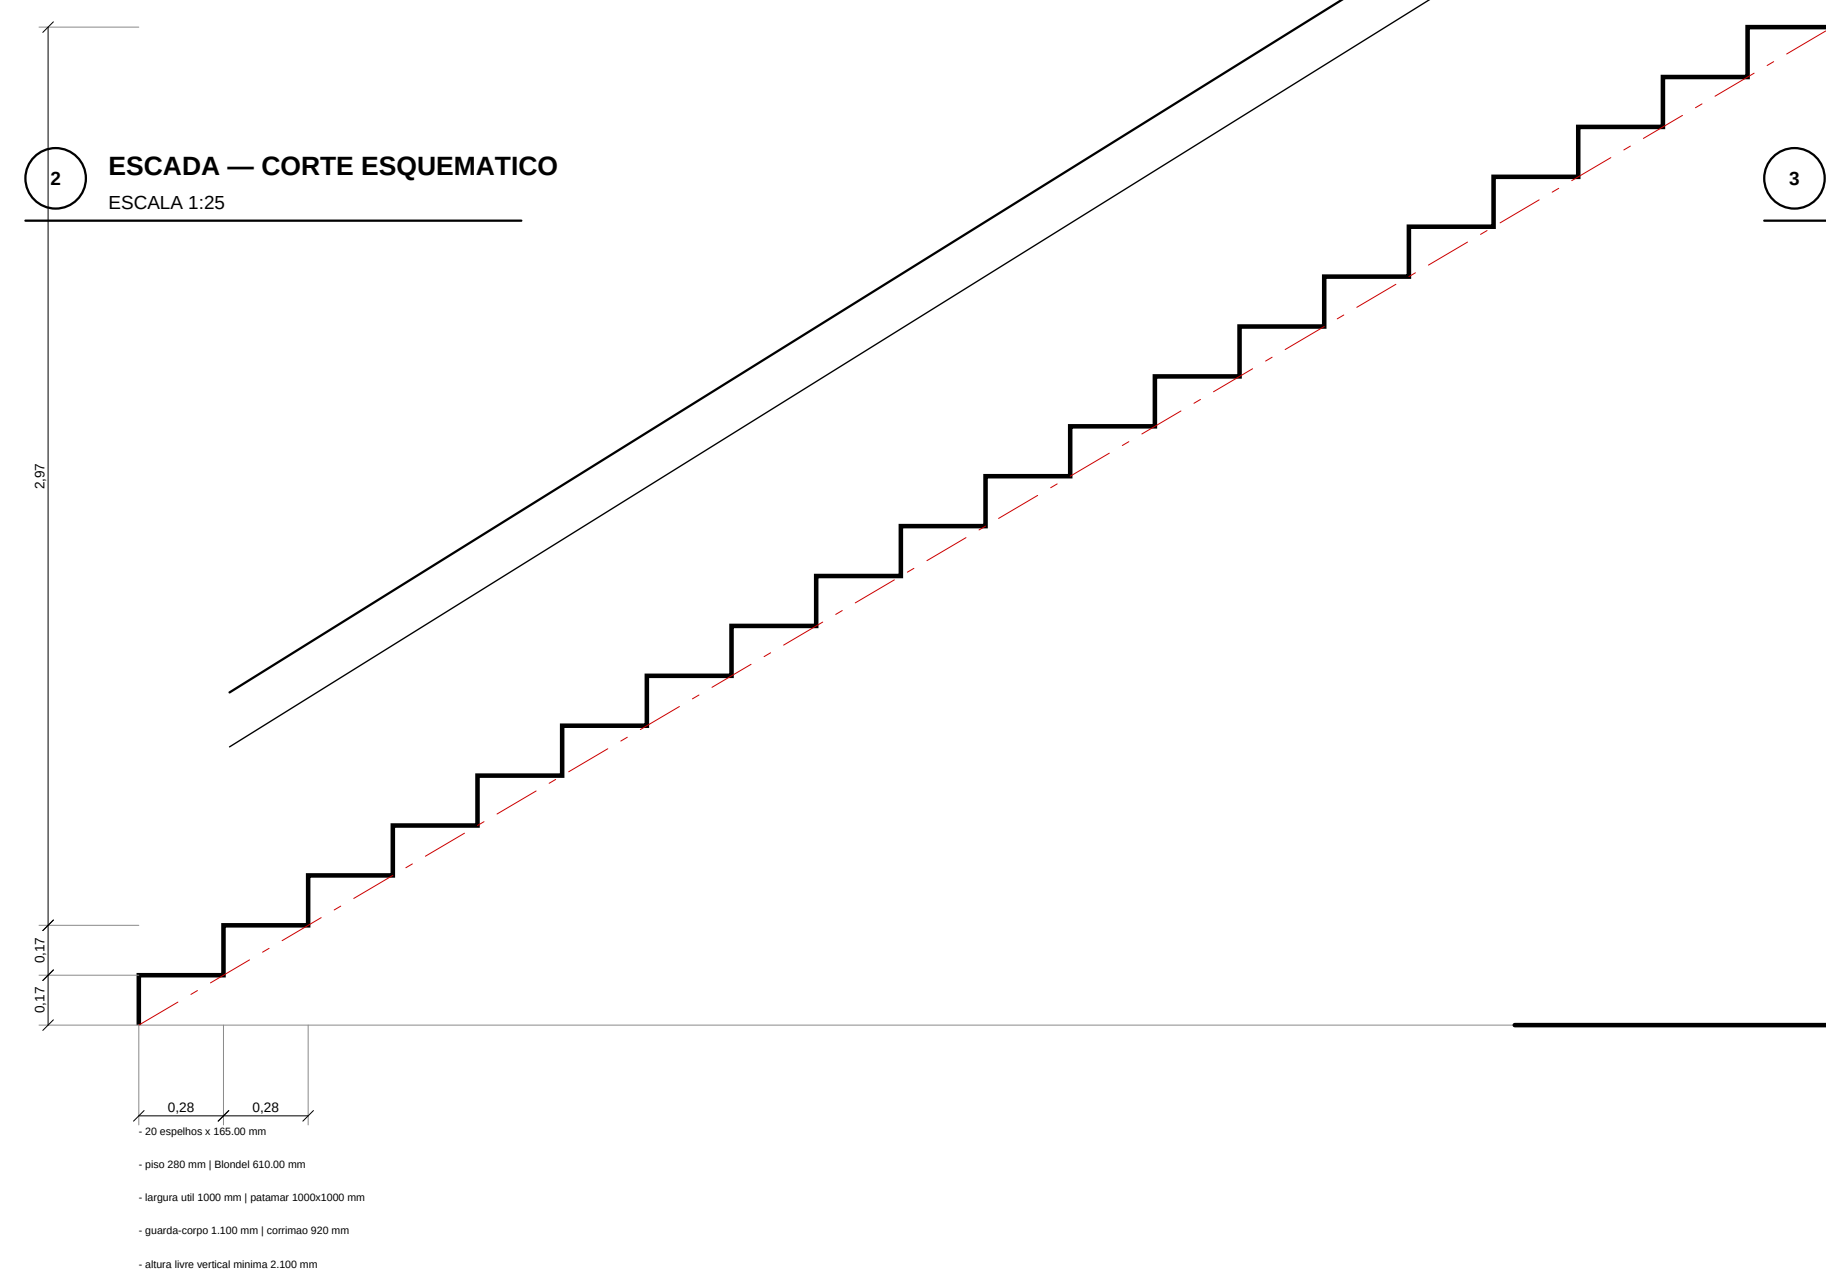

2 ESCADA — CORTE ESQUEMATICO
ESCALA 1:25



3 PISCINA — CORTE
ESCALA 1:25

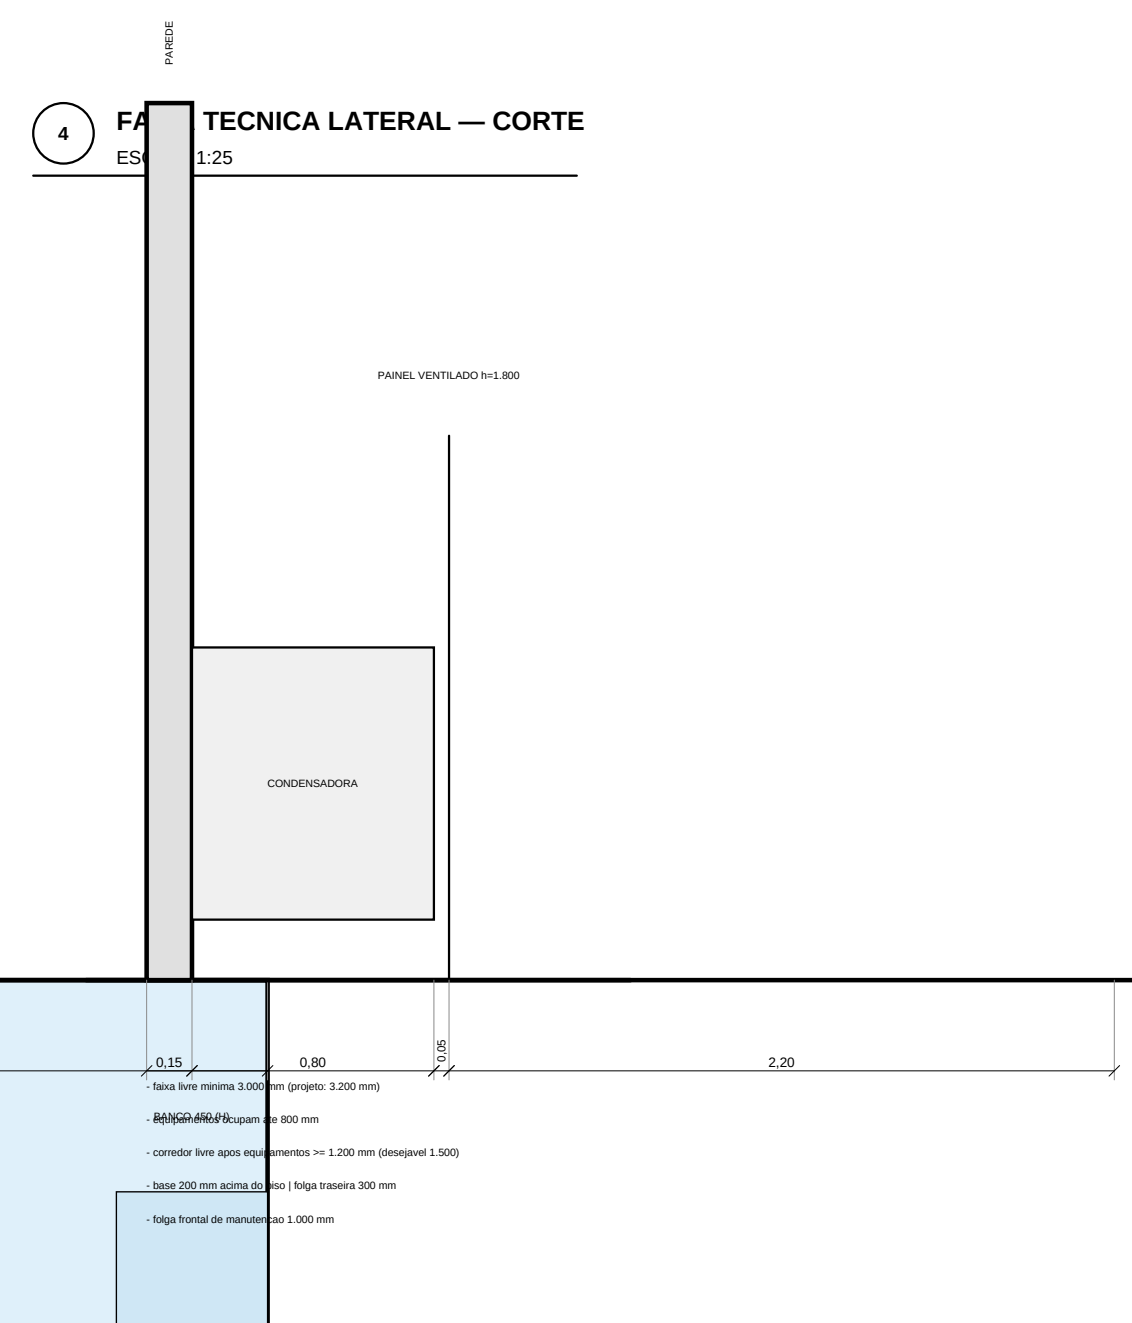

4 FA TECNICA LATERAL — CORTE
ES 1:25

esp. total 150 mm

NOTAS

- Detalhes de estudo — não liberados para fabricação ou corte (sem nesting codificado).
- Parede externa consolidada em 150 mm; divisória interna em 100 mm (½).
- Escada reconciliar com estrutura, guarda-corpo e espessura de acabamento antes de definitiva.

PROJETO PORTO REAL

RESIDENCIA UNIFAMILIAR | MARAULIS - AM | SOCS TANAPIRA-PS

PROJETO ARQUITETONICO

Detalhes Construtivos Ampliados

BASE GEOMETRICA

Linha Consolidada
pm-RS2 (greenview)

UNIDADE MESTRE: 06L

ESCALA

indicada

FORMATO A1
MILHA 900X800/300

CADASTRO

ESTUDO PRELIMINAR RIZ

NAO LIDERACAO PAGA OBDA

SEM ART / RBT

FRENTE

10

de 42 REV RZ