



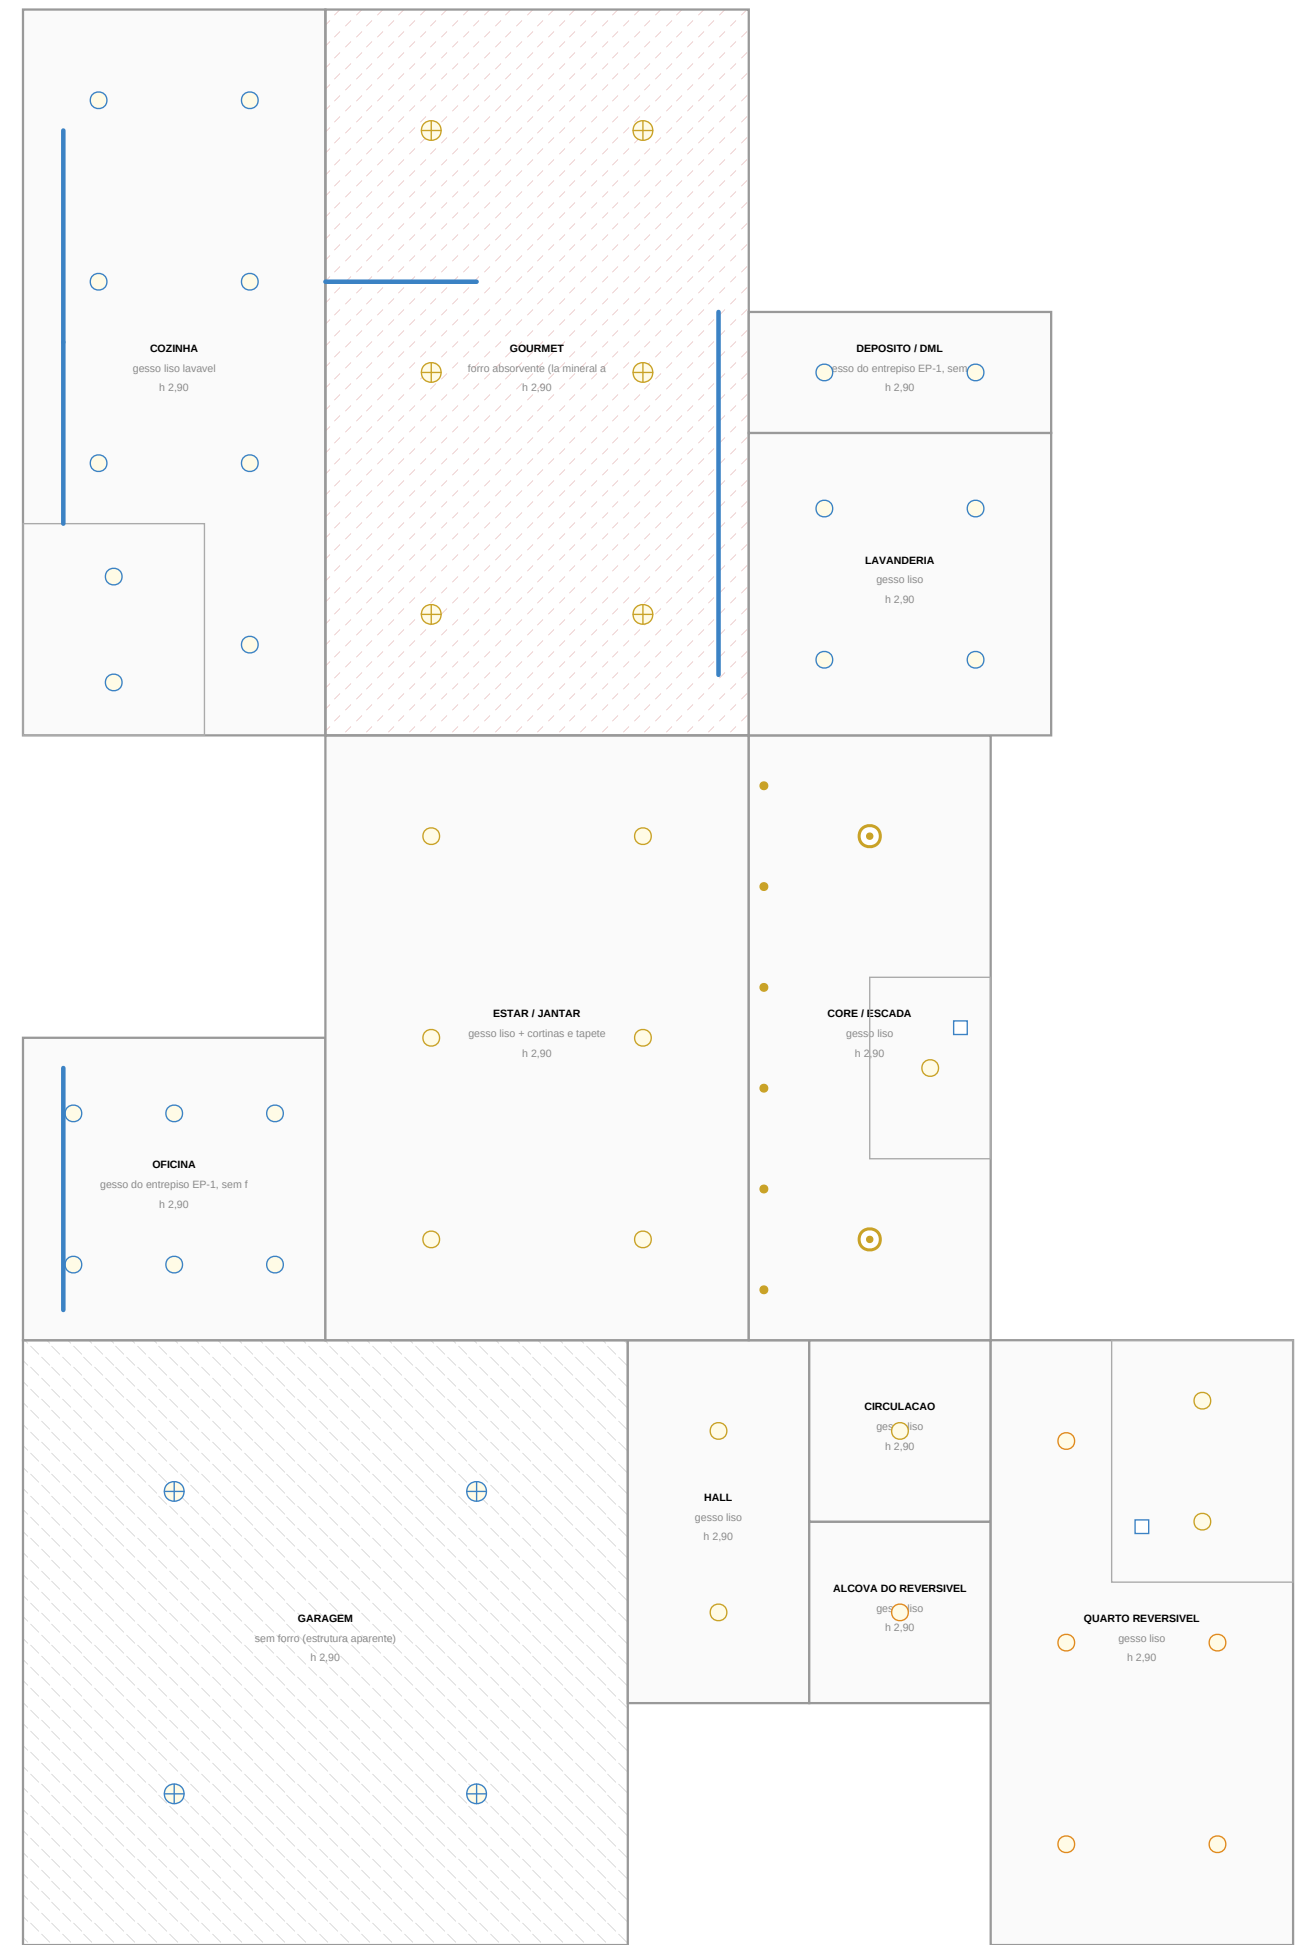

1 FORRO REFLETIDO — TERREO
ESCALA 1:75

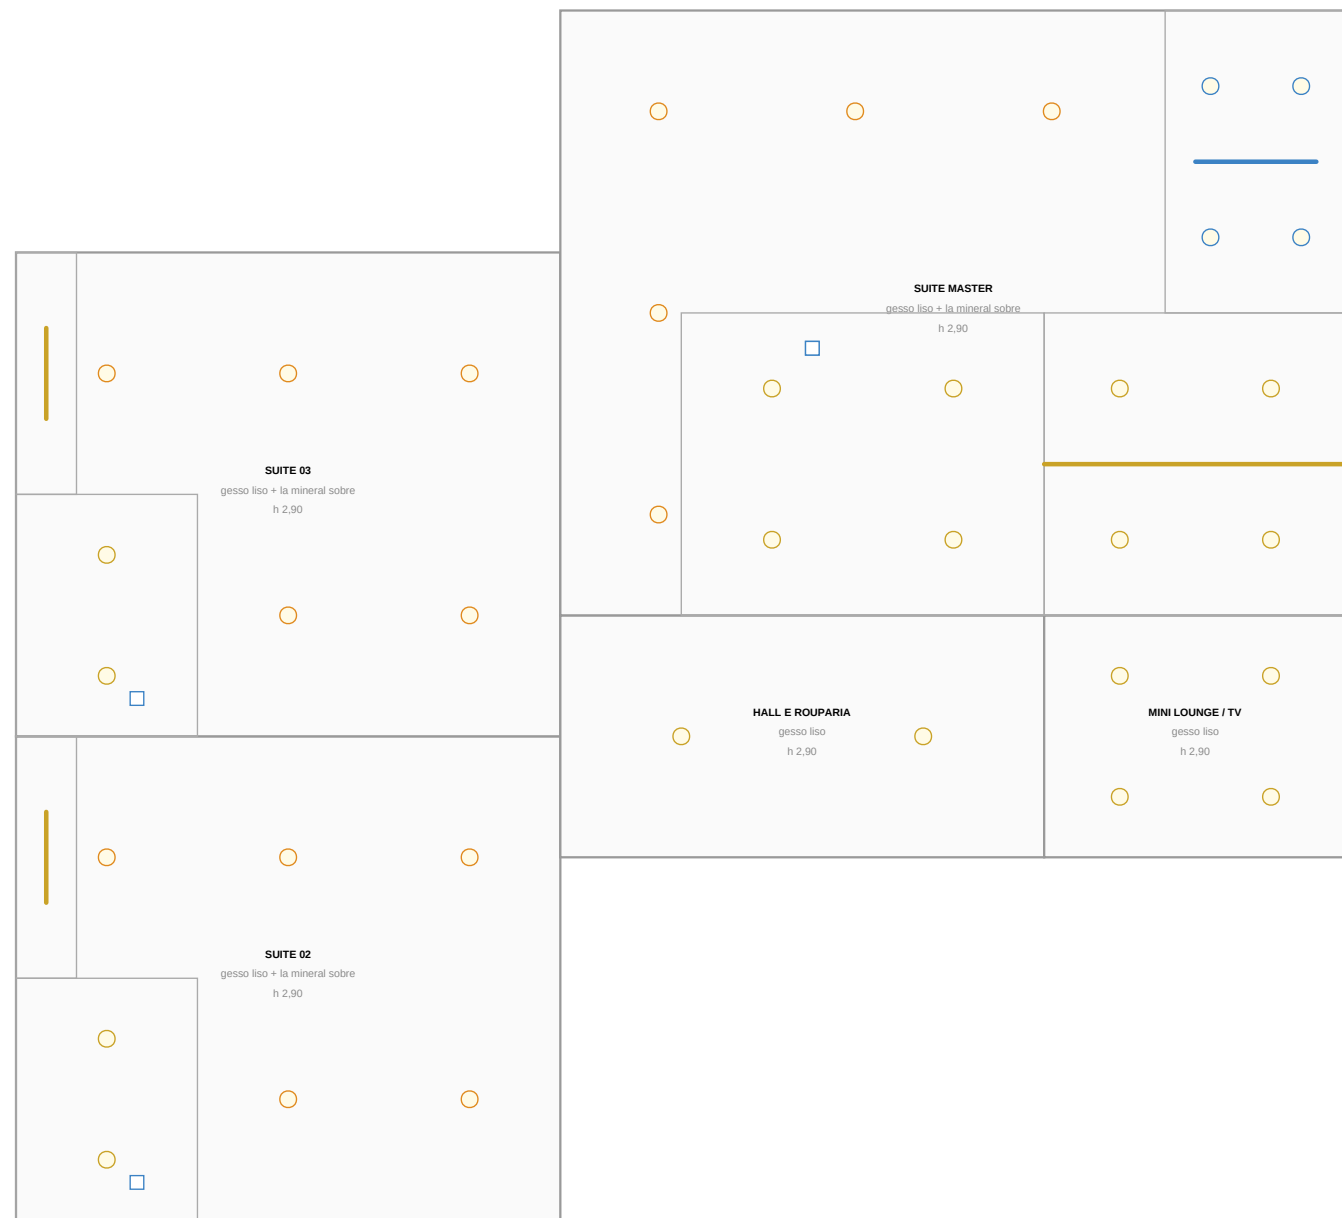

2 FORRO REFLETIDO — SUPERIOR
ESCALA 1:75



LUMINOTECNICA POR AMBIENTE — METODO DOS LUMENS

AMB	USO	m2	altura	aberto	LUMINARIA	cor	W
T-GAR	apoi	35,5	75	108	4 x Plafon LED de 24 W	4000 K	96
T-AL	circulacao	6,5	100	151	2 x Downlight LED embudo 18 W	3000 K	36
T-ALC	varia	3,2	100	151	1 x Downlight LED embudo 18 W	2700 K	18
T-CM	circulacao	3,2	100	151	1 x Downlight LED embudo 18 W	3000 K	18
T-DEV	varia	12,7	100	200	5 x Downlight LED embudo 18 W	2700 K	90
T-CM	aberto	9,9	100	151	4 x Downlight LED embudo 18 W	4000 K	144
T-SOC	soci	25,2	200	242	8 x Downlight LED embudo 24 W	3000 K	144
T-COR	escada	12,2	100	188	7 x Pendente LED de 18 W	3000 K	90
T-COE	circulacao	17,8	300	353	7 x Downlight LED embudo 24 W	4000 K	168
T-GOU	soci	30,2	200	208	6 x Plafon LED de 24 W	3000 K	144
T-LAV	varia	9,0	200	245	4 x Downlight LED embudo 18 W	4000 K	72
T-DEP	varia	3,9	200	272	2 x Downlight LED embudo 18 W	4000 K	36
S-SO1	varia	20,2	100	172	5 x Downlight LED embudo 18 W	2700 K	90
S-SO2	varia	20,2	100	172	5 x Downlight LED embudo 18 W	2700 K	90
S-AL	circulacao	11,5	100	120	2 x Downlight LED embudo 24 W	3000 K	40
S-LOU	soci	7,2	200	350	4 x Downlight LED embudo 24 W	3000 K	96
S-MA1	varia	21,6	100	160	6 x Downlight LED embudo 18 W	2700 K	90
S-SO1BANHO	banho	4,3	200	220	2 x Downlight LED embudo 18 W	3000 K	36
S-SO1CLOSET	closet	1,4	200	288	1xw 0,3 m	3000 K	16
S-SO2BANHO	banho	4,3	200	220	2 x Downlight LED embudo 18 W	3000 K	36
S-SO2CLOSET	closet	1,4	200	288	1xw 0,3 m	3000 K	16
T-CO1DESPENSA	varia	3,9	200	368	2 x Downlight LED embudo 24 W	4000 K	40
T-RE1BANHO	banho	4,3	200	220	2 x Downlight LED embudo 18 W	3000 K	36
T-CO1BANHO	banho	2,2	200	227	1 x Downlight LED embudo 18 W	3000 K	18
S-MA2BANHO	banho	10,8	200	250	4 x Downlight LED embudo 18 W	3000 K	72
S-MA2CLOSET	closet	9,0	200	242	4 x Downlight LED embudo 18 W	3000 K	72
S-MA2OFFICE	office	5,4	200	512	4 x Downlight LED embudo 24 W	4000 K	96

LUZ DE TAREFA

COD	ONDE	TIPO	QTD	cor
L7-BC-01	banhada BC-01 (T-CO1)	linear	2,1 m	4000 K
L7-BC-02	banhada BC-02 (T-CO2)	linear	1,8 m	4000 K
L7-BC-03	banhada BC-03 (T-CO3)	linear	1,5 m	4000 K
L7-BC-04	banhada BC-04 (T-CO4)	linear	3,8 m	4000 K
L7-BC-05	banhada BC-05 (T-CO5)	linear	2,4 m	4000 K
L7-AC-01	espelho do banheiro LC-01 (T-CO1)	arandela	1	4000 K
L7-AC-02	espelho do banheiro LC-02 (T-CO2)	arandela	1	4000 K
L7-AC-03	espelho do banheiro LC-03 (T-CO3)	arandela	1	4000 K
L7-AC-04	espelho do banheiro LC-04 (T-CO4)	arandela	1	4000 K
L7-AC-05	espelho do banheiro LC-05 (T-CO5)	arandela	2	4000 K
L7-AC-06	espelho do banheiro LC-06 (T-CO6)	arandela	3	4000 K
L7-AC-07	espelho do banheiro LC-07 (T-CO7)	arandela	3	4000 K
L7-AC-08	espelho do banheiro LC-08 (T-CO8)	arandela	3	4000 K
L7-AC-100	espelho do banheiro LC-100 (T-CO100)	arandela	3	4000 K

NOTAS

- Plano refletido: vista do forro projetada no plano horizontal, interno e superior.
- Luminarias pelo METODO DOS LUMENS por ambiente (NBR 9070:2005 / NBR 14133, multa de uniformidade 0,8). 1,2.
- 100 pontos por m². 12 pontos de teste, 2000 W (R, AL, 1000).
- Cor: 2.700 K interno / 3.000 K social e circulação / 4.000 K cozinha, banheiro e trabalho.