


VERIFICACAO NBR 9050

| ITEM                      | EXISTENTE           | PROJETO                   |          |
|---------------------------|---------------------|---------------------------|----------|
| Visão livre de porta      | 800 mm              | 940 mm (prof. de 900)     | OK       |
| Circulo de giro 360 graus | 1.500 mm            | hall, banheiro e quarto   | OK       |
| Desnivel sem rampas       | até 5 mm            | soluções niveladas        | OK       |
| Largura de circulação     | 900 mm              | 1.800 mm no hall          | OK       |
| Barra de apoio            | relevo no piso      | ambuido no PTE 1 e PTE 2  | OK       |
| Barreira acústica         | altura livre 130 mm | sem barreiras sob a calha | OK       |
| Contraste e interruptor   | 600 a 1.000 mm      | a definir no eletrico     | pendente |



FLUXOS — SEPARACAO DE CIRCUITOS

| CIRCUITO        | PERCURSO                                                                  | CIRCULO SOCIAL? |
|-----------------|---------------------------------------------------------------------------|-----------------|
| Servico         | garagem -> oficina -> lavanderia -> cozinha -> despensa                   | NAO             |
| Social          | entrada -> hall -> estar -> gourmet -> alameda -> piscina                 | —               |
| Intimo Intimo   | hall -> circulacao -> banheiro social (quarto reservado) (quarto privado) | NAO             |
| Intimo Superior | hall -> core -> hall superior -> suíte                                    | NAO             |
| Uso e carga     | cozinha -> despensa -> refeit hall                                        | NAO             |

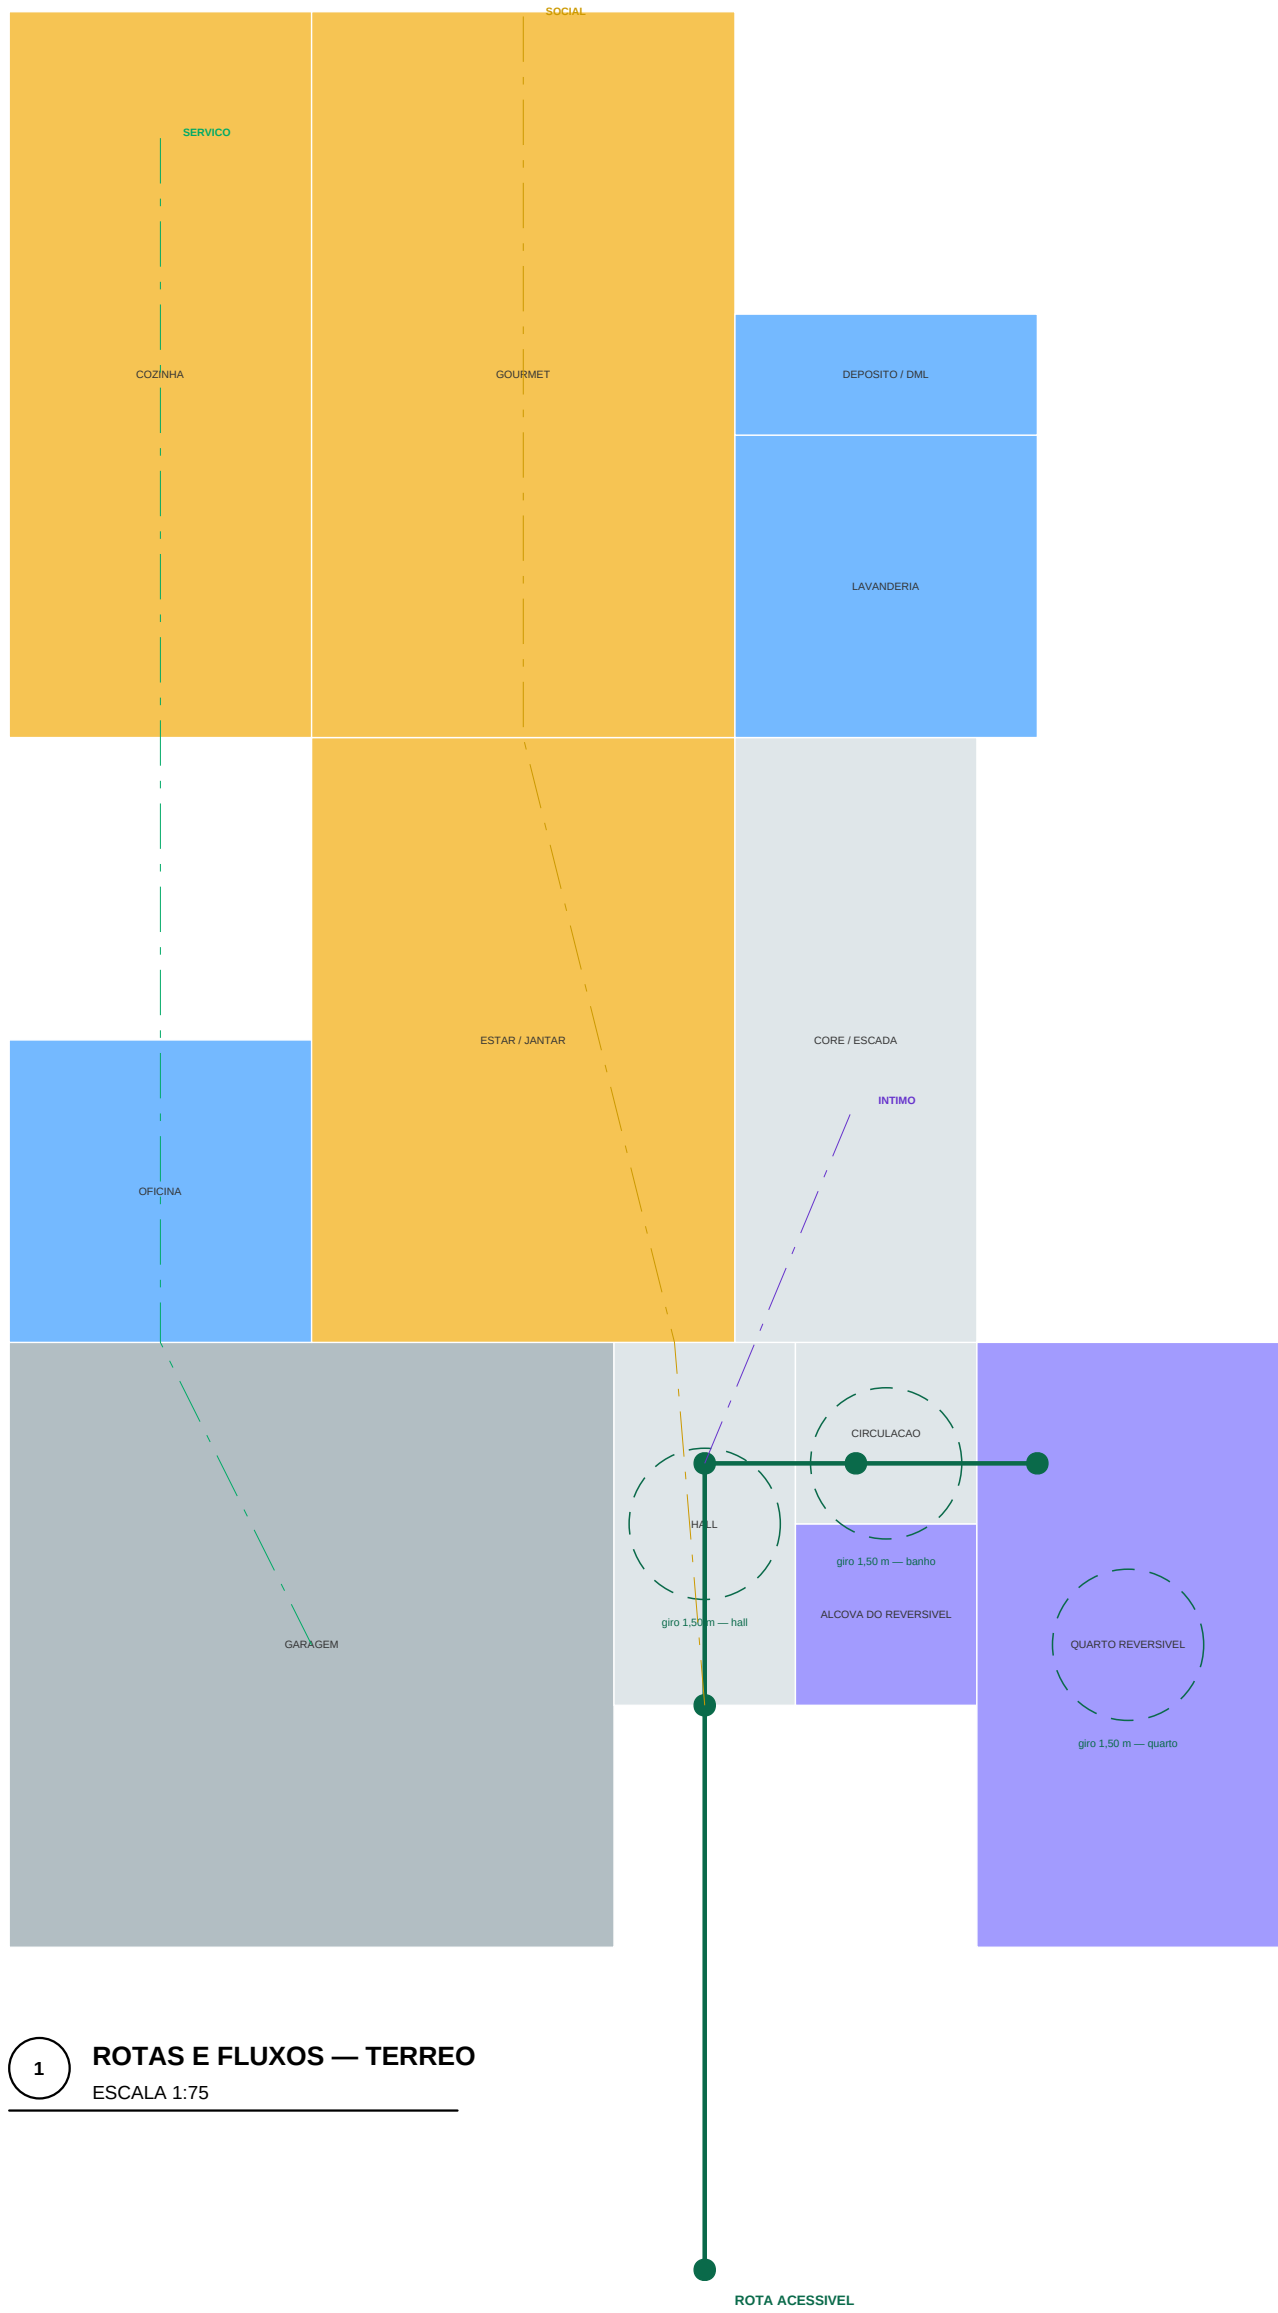

1 ROTAS E FLUXOS — TERREO  
ESCALA 1:75

- NOTAS
- \* Rota acessível do passeio ao quarto reservado e ao banheiro social.
  - \* Circulo de giro de 1.500 mm verificado nos pontos de manobra.
  - \* Porta de correr de 900 mm no banheiro social e area de manobra.
  - \* Refeitico para barra de apoio ambuido antes do fechamento das placas.

PROJETO PORTO REAL

RESIDENCIA UNIFAMILIAR (MANSÃO - AM) | SOBR TATIANA-PS

PROJETO ARQUITETONICO

ACESSIBILIDADE E FLUXOS

|                     |                     |                        |               |
|---------------------|---------------------|------------------------|---------------|
| BASE GEOMETRICA     | ESCALA              | EMISSAO                | PROJECION     |
| União Consolidada   | 1:75                | ESTUDO PRELIMINAR RIZ  | 17            |
| ISO-RIZ (previsão)  | FORMATO A1          | NAO LIBERADO PARA OBRA |               |
| UNIDADE METRICA: MM | MILIMETROS (1000MM) | SEM ART / RNT          | OK-43 REV RIZ |