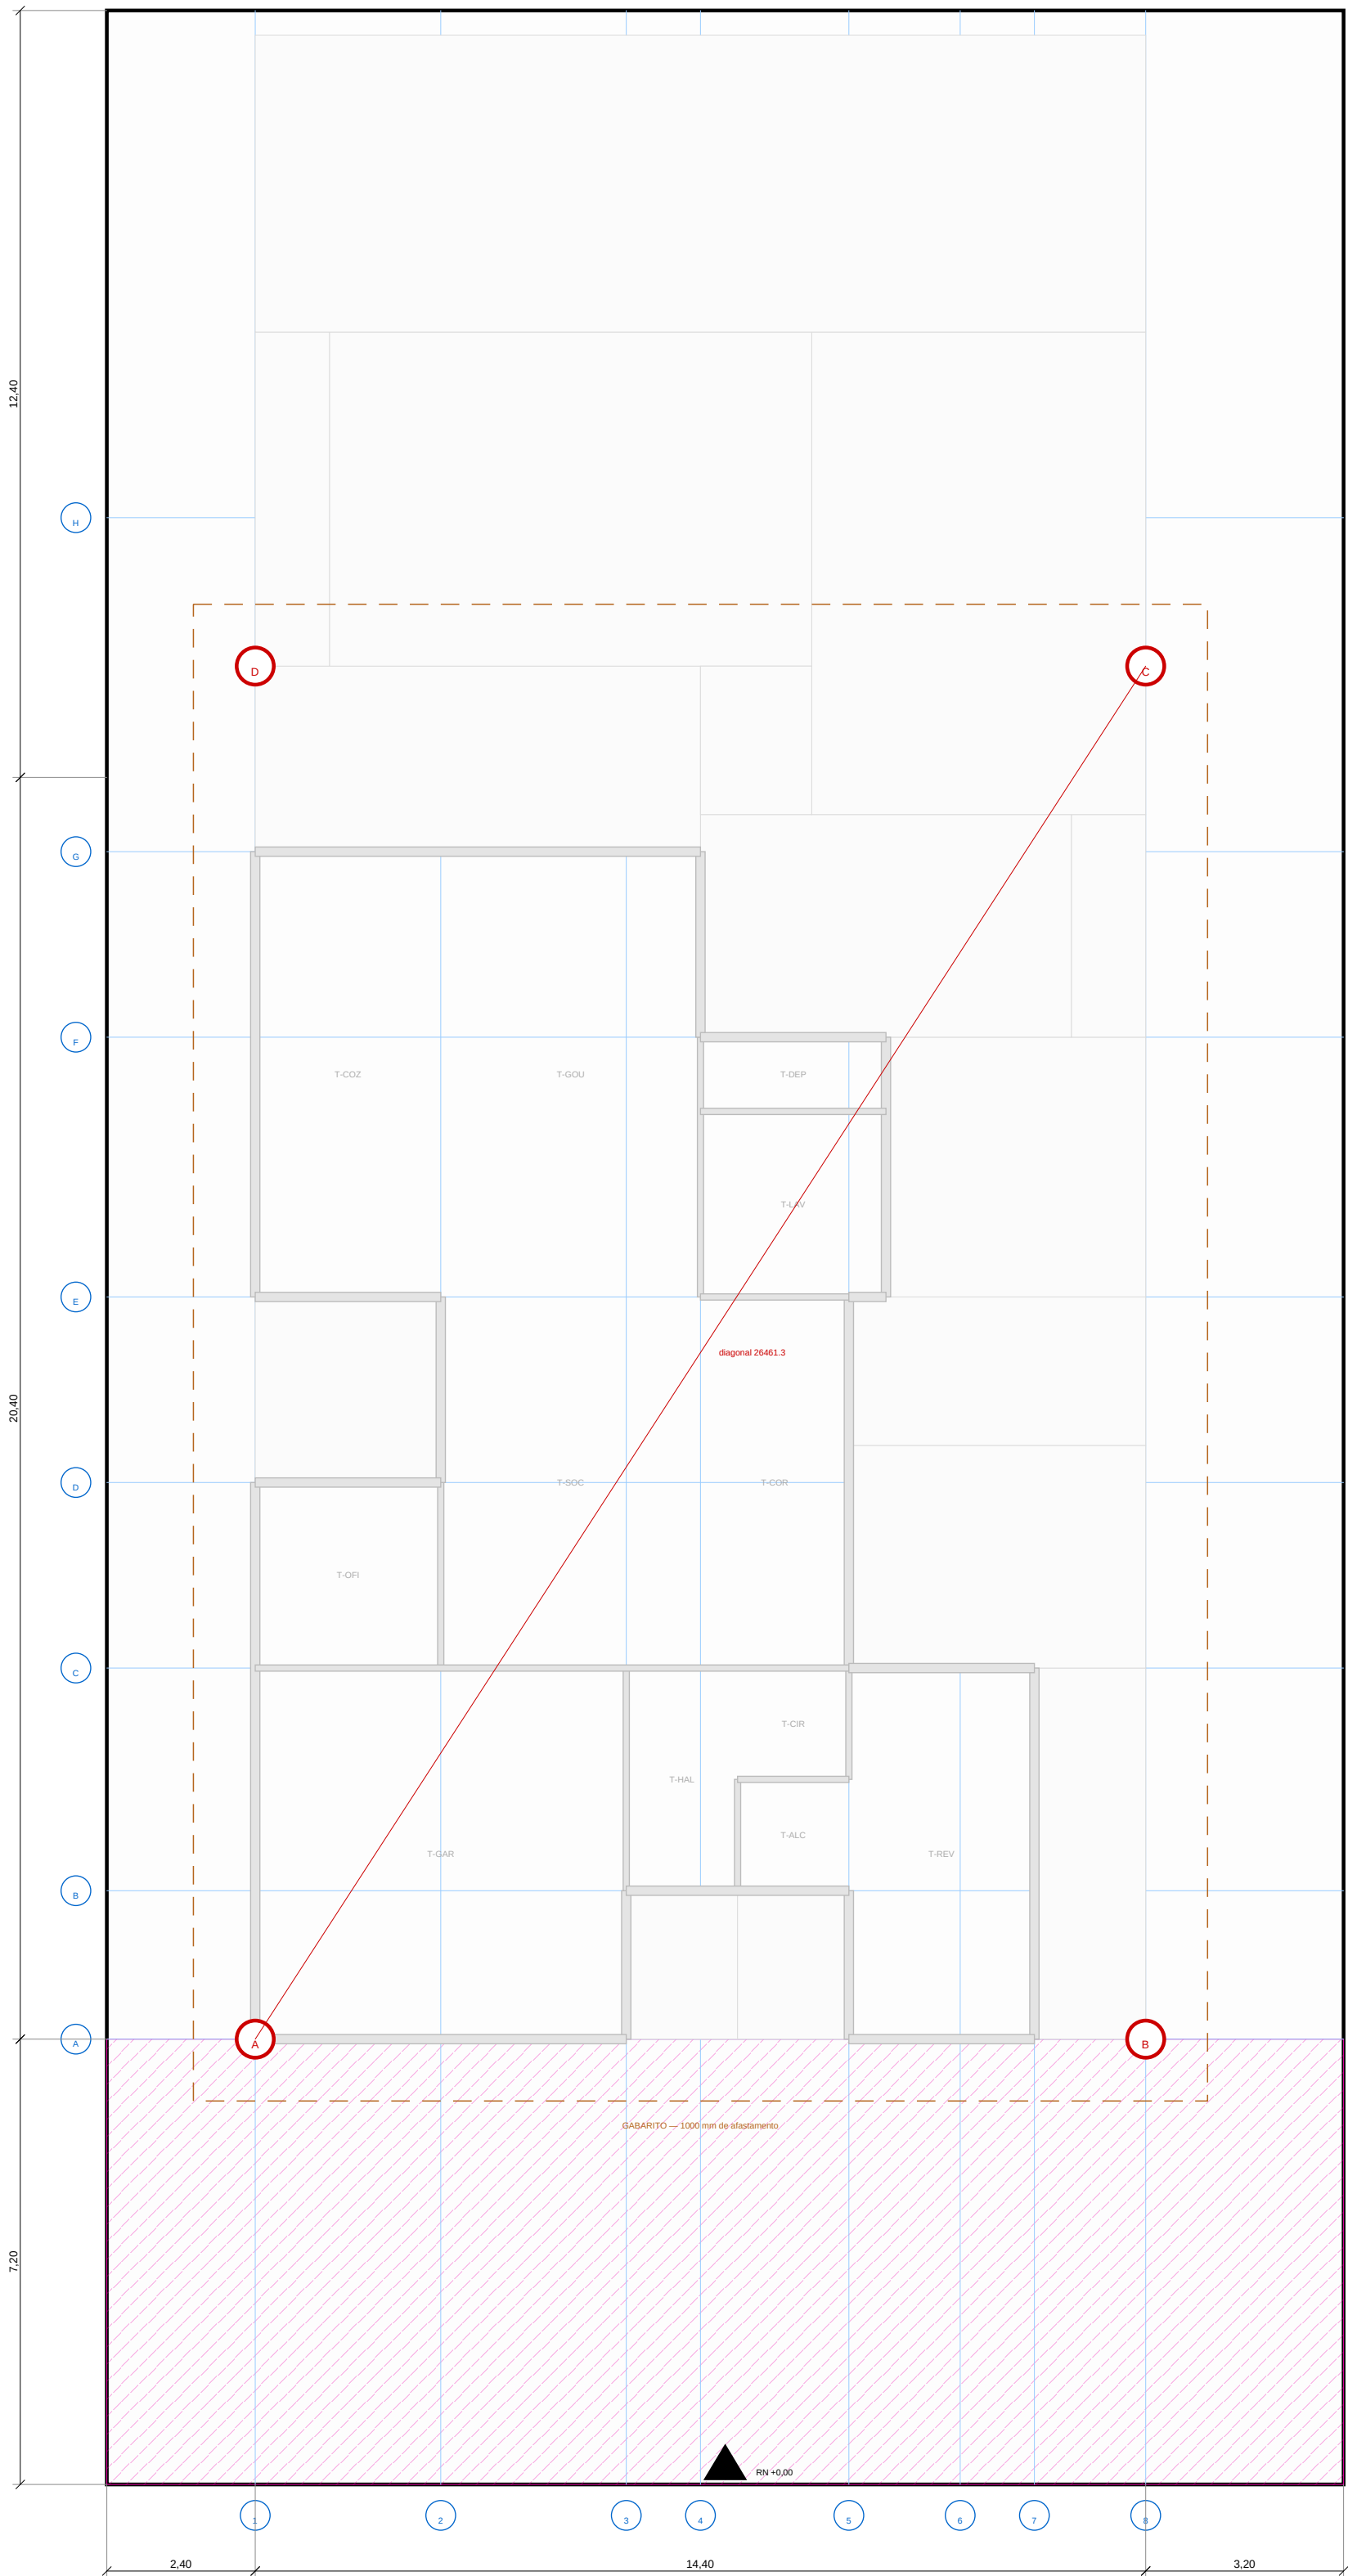


COORDENADAS DOS CANTOS (mm)

CANTO	X	Y	DIVISA SUL	DIVISA NORTE	TESTADA	QUIBO	DIAGONAL
A	2400	7200	2400	17600	7200	32800	26461,3
B	18800	7200	18800	3200	7200	32800	26461,3
C	18800	28400	18800	3200	28400	19600	26461,3
D	2400	28400	2400	17600	28400	19600	26461,3

PROCEDIMENTO DE LOCAÇÃO

#	PASSO	CRITÉRIO DE ACEITE
1	Conferir as divisas com o material de base	divergência acima de 10 mm interromper a locação
2	Instalar o PNA sobre o concreto 200 x 200 x 100 mm, fora da área de obra	fora da área de obra
3	Montar o gabarito a 1000 mm do cantoneiro	perguntas 75 x 75 e tubos 20 x 100
4	Marcar os eixos X (1) a (7) e Y (A) a (H) no gabarito	linha coordenada múltipla de 200 mm
5	Cortar sobre o eixo dos OLAS diretos	verificar em todos os eixos do eixo de base
6	Conferir a diagonal A-C	26461,3 mm com tolerância de 10 mm
7	Conferir o espaçamento por 3-6 mm em cada canto	antes de qualquer concretagem
8	Registrar em ata com foto e modelo	gabarito continuo nos dois lados da obra, conferência

EIXOS MODULARES

DIREÇÃO	VALORES (mm)
X (1) a (7)	2400 - 5400 - 8400 - 9600 - 12200 - 13800 - 15000 - 18800
Y (A) a (H)	7200 - 9600 - 13200 - 16200 - 19200 - 28400 - 28400 - 32800
Módulo	principal 600 mm - submódulo 300 mm
Origem	canto frontal esquerdo da base
Unidade	módulo

NOTAS

- Locação é o único documento em que o erro não tem contorno técnico e caso se dê lugar.
- Cada canto é o eixo dos OLAS diretos, nunca em cantos acumulados — erro de cada soma, erro de referência independente não.
- Conferência obrigatória para diagonal 26461,3 mm entre A e C antes de concretar o núcleo.
- Ata ou área de trabalho, alinhado ao eixo 10-00, com 0,00 (+) para acoberto do terreno.

PROJETO PORTO REAL

RESIDÊNCIA UNIFAMILIAR (MANSÃO) - AM | 100% TUBO (PI)

PROJETO ARQUITETÔNICO

LOCAÇÃO DE OBRA E GABARITO

BASE GEOMÉTRICA Linha Consolidada Projeto (previsão) Unidade: metro, mm	ESCALA 1:100 Formato A1 Módulo: 600/300/300	EXIBIÇÃO ESTUDO PRELIMINAR R2 Linha Libertada para Obra Sem Arte / Pint	PROJETO 31 06-43 REV R2
--	---	--	--------------------------------------