


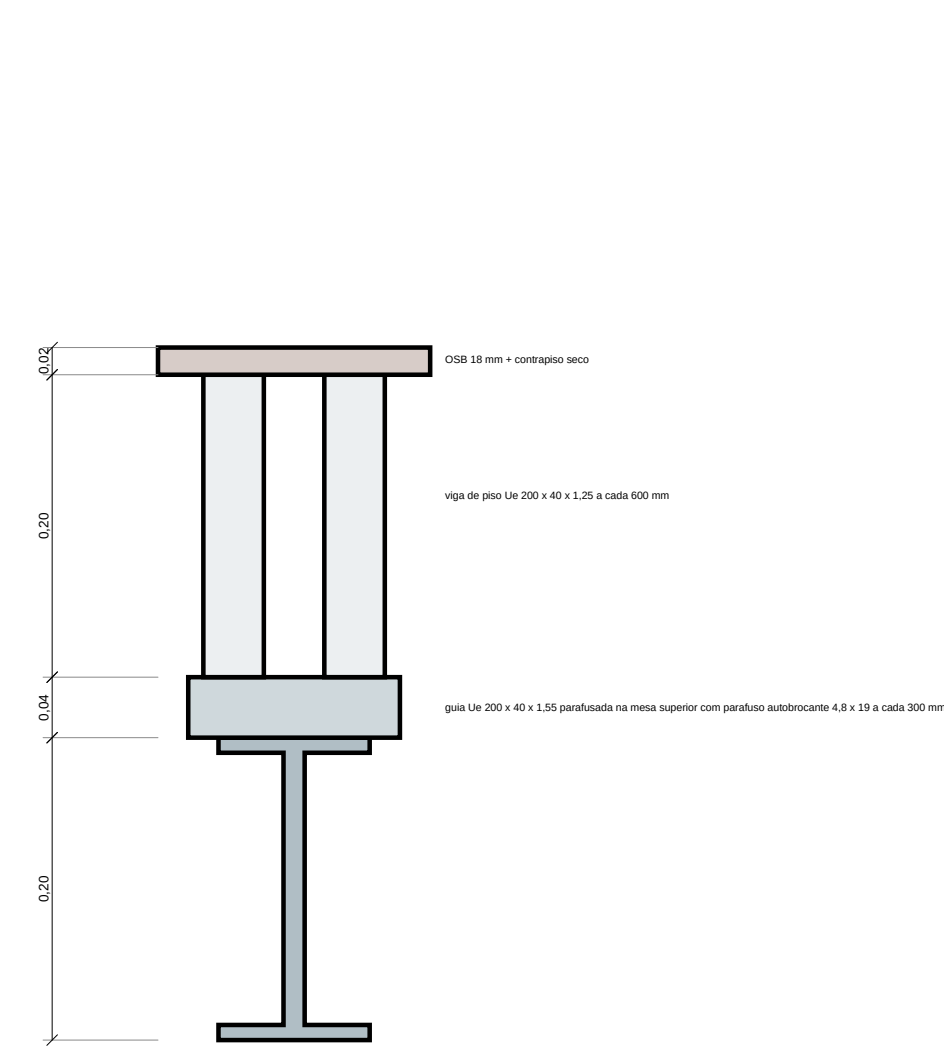

1 APOIO DO VIGAMENTO LSF SOBRE VIGA LAMINADA
ESCALA 1:5


A mesa da viga e ponto de apoio e assento - a

banda mediana de 5 mm sob a guia corta os dois

da parede, que o montador chama de megalpa

na chapa de apoio, fixação horizontal no topo

Sem esta junta, a flecha da viga deixa de ser

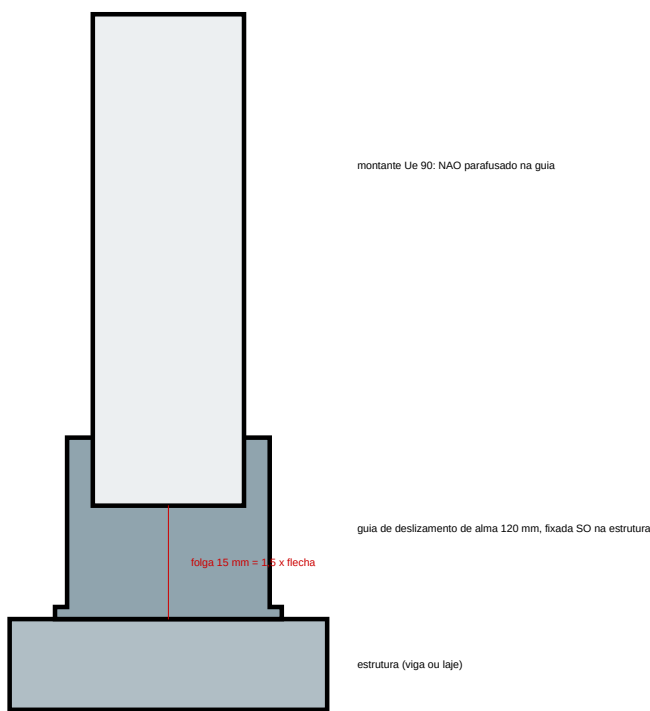

2 JUNTA DE DESLIZAMENTO NO TOPO DA PAREDE
ESCALA 1:5


relevo e ponto de apoio de (presto orden)

perfil e marca de la de flecha no centro (o ano)

para 200 mm, com montantes duplos horizontalmente

Cada dois acortam, a parede engrossa localmente

O pilar de 300 mm NAO cabe na parede de 250 mm

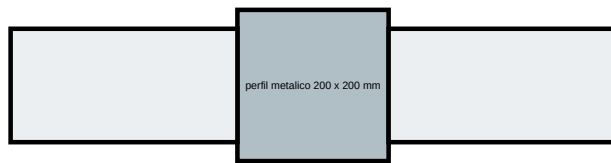

3 PILAR METALICO EMBUTIDO EM PAREDE LSF
ESCALA 1:10

perfil LSF 100 mm

DIMENSIONAMENTO DAS VIGAS — GOVERNADO PELA FLECHA, NAO PELA RESISTENCIA

VIGA	SOBRE	VAO (mm)	T88 (mm)	u (mm)	LIMITE	PERFIL	N (mm)	FLECHA	ADM (mm)	TENSAO (MPa)	SLP (mm)
V-01	T-100	3000	2700	0,08	L200	W100x45,0	1305	3,47	6,00	104 (95 %)	10
V-02	T-100	3000	2700	0,08	L200	W100x45,0	1305	7,94	10,43	70 (31 %)	—
V-03	T-100	3000	2700	0,08	L200	W100x45,0	1305	11,64	17,14	87 (28 %)	—
V-04	T-100	3000	1500	0,04	L100	W100x35,0	685	3,77	6,00	83 (37 %)	10
V-05	T-100	3000	3000	0,40	L200	W100x45,0	1305	3,80	6,00	113 (50 %)	10
V-06	T-100	3000	3000	0,40	L200	W100x45,0	1305	3,80	6,00	113 (50 %)	10
V-07	T-100	3000	1800	0,08	L100	W100x35,0	685	4,38	6,00	139 (61 %)	—
V-08	T-100	3000	900	0,18	L100	W100x35,0	685	3,14	6,00	89 (38 %)	—
V-09	T-100	3000	900	0,18	L100	W100x35,0	685	3,14	6,00	89 (38 %)	—
V-10	T-100	1200	3000	0,08	L100	W100x35,0	4340	7,25	10,38	57 (25 %)	10
V-11	T-100	1200	1500	0,12	L100	W100x35,0	685	5,74	6,00	93 (23 %)	—

POR QUE A FLECHA GOVERNA

GRANDICIA	FALTA NO PROJETO	LEITURA
Uso da resistencia a flexao	23 a 81 %	sofista resistencia - o perfil nao esta no limite em nenhuma viga
Flecha / flecha admissivel	37 a 73 %	e aqui que o perfil se aproxima do limite — e o que define a busca
Consequencia de erro a resistencia	colapso	evento raro, verificado por calculo e ART
Consequencia de erro a flecha	flexao excessiva no apoio	evento raro, tratado de outro e care de comentar para sempre
Custo de substituir um perfil	2 a 5 kg/m de aço	risco de que uma unica reparatura da parede flexada

CAIXA D'AGUA — CARGA CONCENTRADA

ITEM	VALOR	DECISAO
Volumen / carga	2000 L / 2000 kg	21 m em 7,20 m2
Posicao	abaco sobre 5 MAGS(MANCA)	abaco na parede do proprio andar, sem plataforma sobre o abaco
Barras	5000 mm	abaco de ferro do superior
Coluna no tercio	0,5 mca	grandes, fixadas
Coluna no superior	0,5 mca	analisando: TC-14 ou 0,5 m no normal superior
Apoio	2 perfis sob a base	dois perfis sob a base, transferindo para as paredes do com - a carga

NOTAS

- O perfil laminado flexa, a chapa de apoio sobre flexa. As duas medidas sao independentes e ambas obrigatorias.

- Flecha limitada a L/200 onde a viga sustenta vedacao fixa, contra L/200 de uso geral.

- Junta de deslocamento com flecha de 1,5 x flecha calculada, por viga.

- Pro-dimensionamento por flecha — calculo analitico e ART (permitecom pendencia

PROJETO PORTO REAL

RESIDENCIA UNIFAMILIAR (MANAUS - AM) | SOUZA TATIANA-PS

PROJETO ARQUITETONICO

INTERFACE LIGHT STEEL FRAME X PERFIL LAMINADO

BASE GEOMETRICA	ESCALA	EMISSAO	PROJETO
União Consolidada	indicada	ESTUDO PRELIMINAR RIO	
ISO-PT2 (previsto)	FORMATO A1	NAO LIBERADO PARA OBRA	
UNIDADE: METRO: mm	MAQUA: 60/50/50/50	SEM ART / RNT	

20

06-25 REV140