



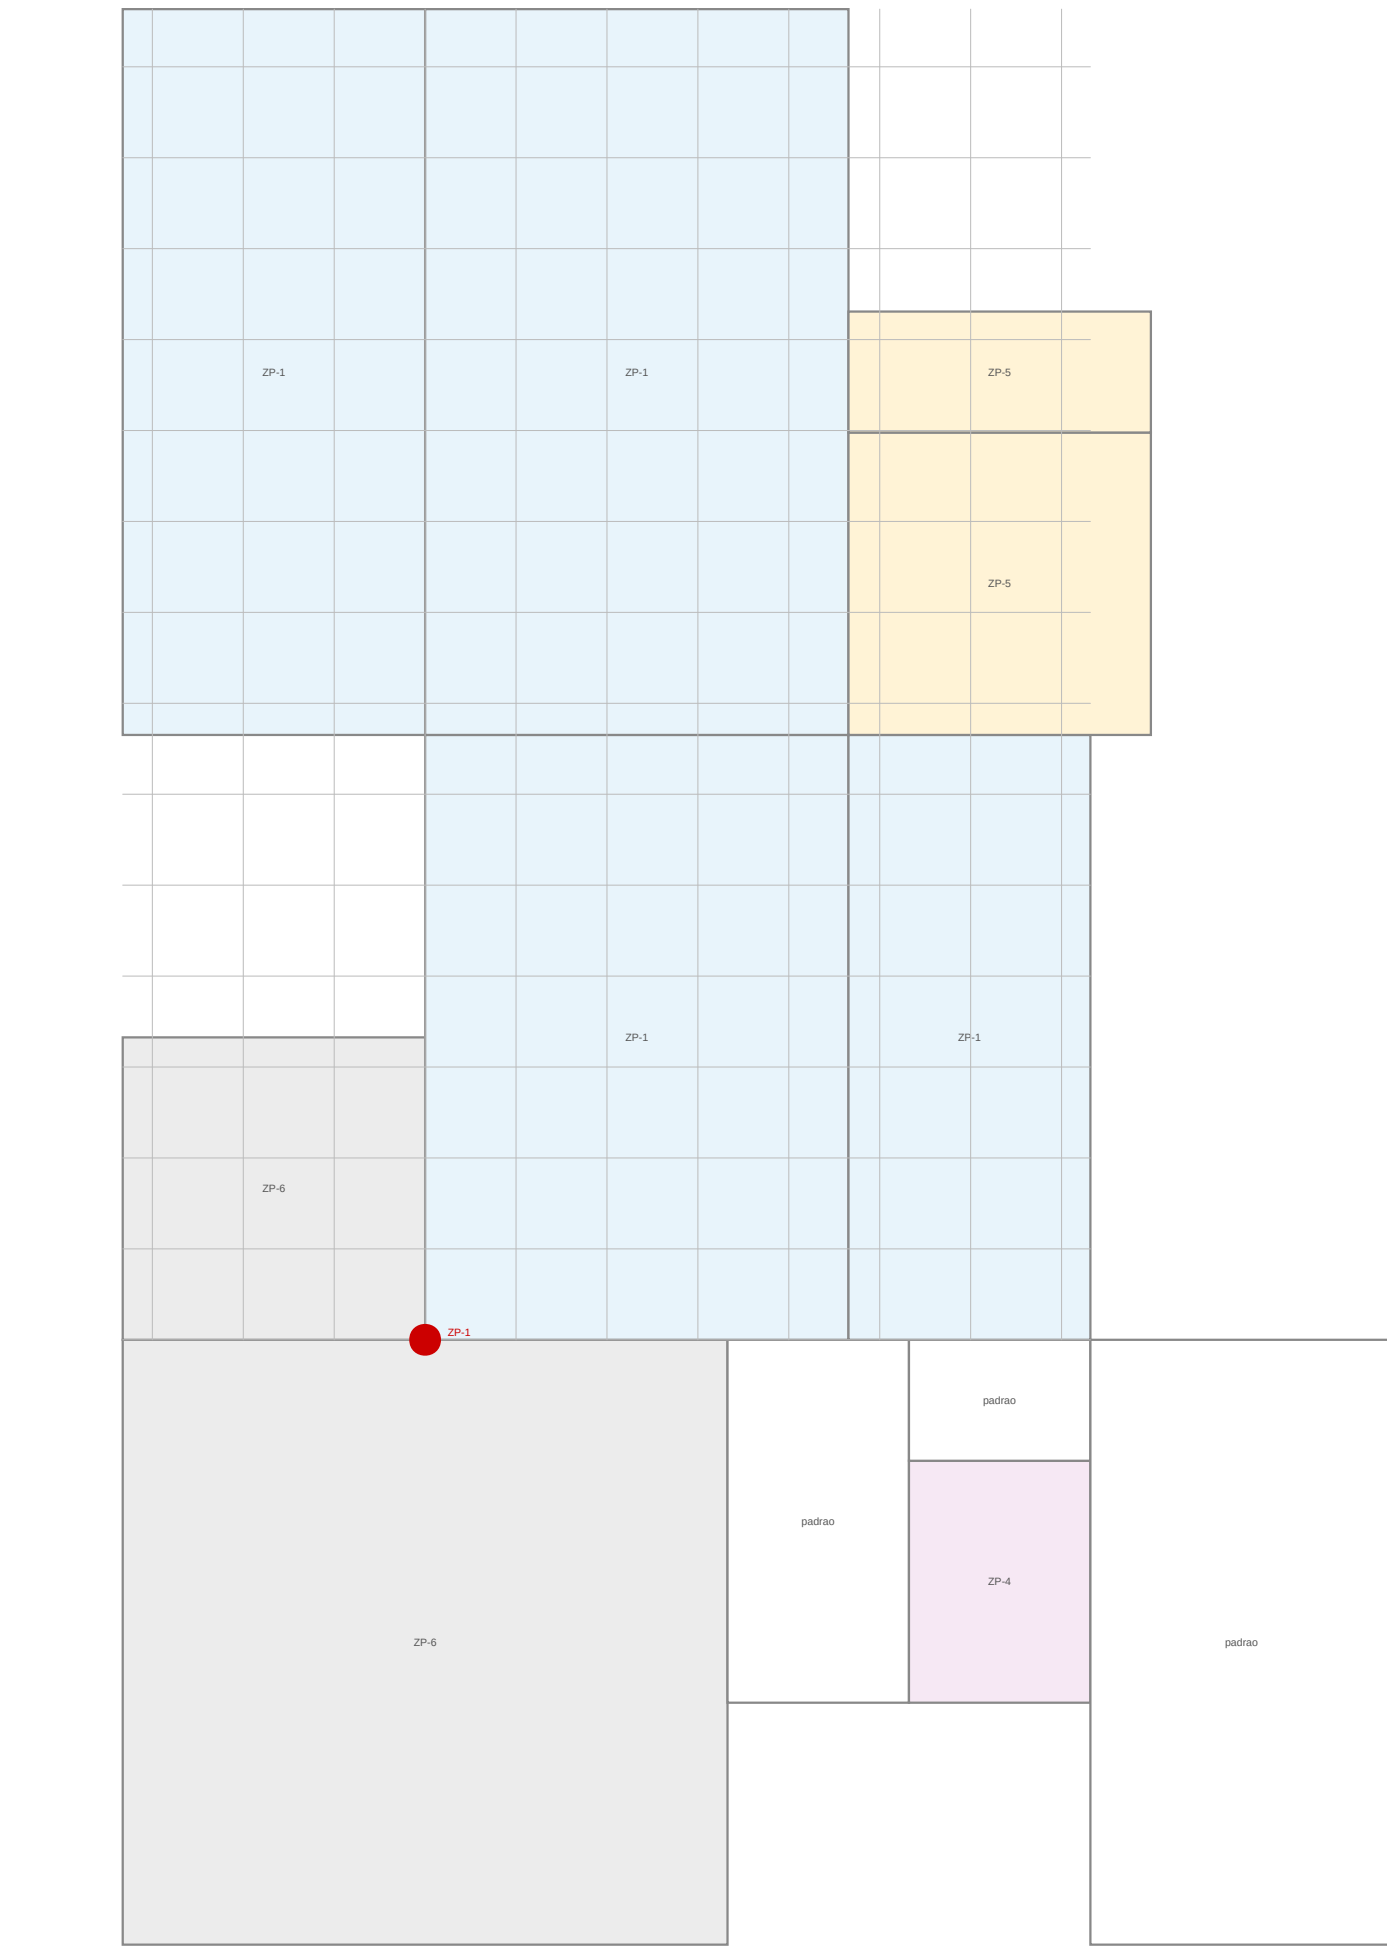

1 PAGINACAO — TERREO
ESCALA 1:75

ZONA	PEÇA	ORDEM	AMBIENTES	PEÇA ESPECIFICAÇÃO	PON RECORTE	COMENTÁRIO
ZP-1	piso	(5400, 12000)	T-SOL, T-CORR, T-GOL, T-COZ	porcelanato retificado 900 x 900	204	risco social interno em uma malha, origem no eixo da porta do n
ZP-2	piso	(7000, 10000)	S-MAS	porcelanato retificado 900 x 900	100	origem no eixo da porta do suite
ZP-3	piso	(2400, 12000)	S-SOL, S-SOL	porcelanato retificado 900 x 900	200	salto 12 e 15 na mesma malha, a parede entre eles é desliza
ZP-7	piso	(12000, 10000)	S-CORR	porcelanato retificado 900 x 900	202	o lounge tem porta e não é integrado a nada, pagina do projeto
ZP-4	parede	carro do ambiente	T-BAN	cerâmico retificado 300 x 600	208	em o bloco terminado de 2.400 (que se estende para a esquerda)
ZP-5	parede	carro do ambiente	T-LAV, T-DEP	cerâmico retificado 300 x 600	200	em o parede de 1.800 mm largo do banheiro, das máquinas e das p
ZP-6	revestimento	(5400, 12000)	T-GAR, T-GAR	cerâmico polido	—	piso cerâmico polido de alta resistência, sem paginação cora

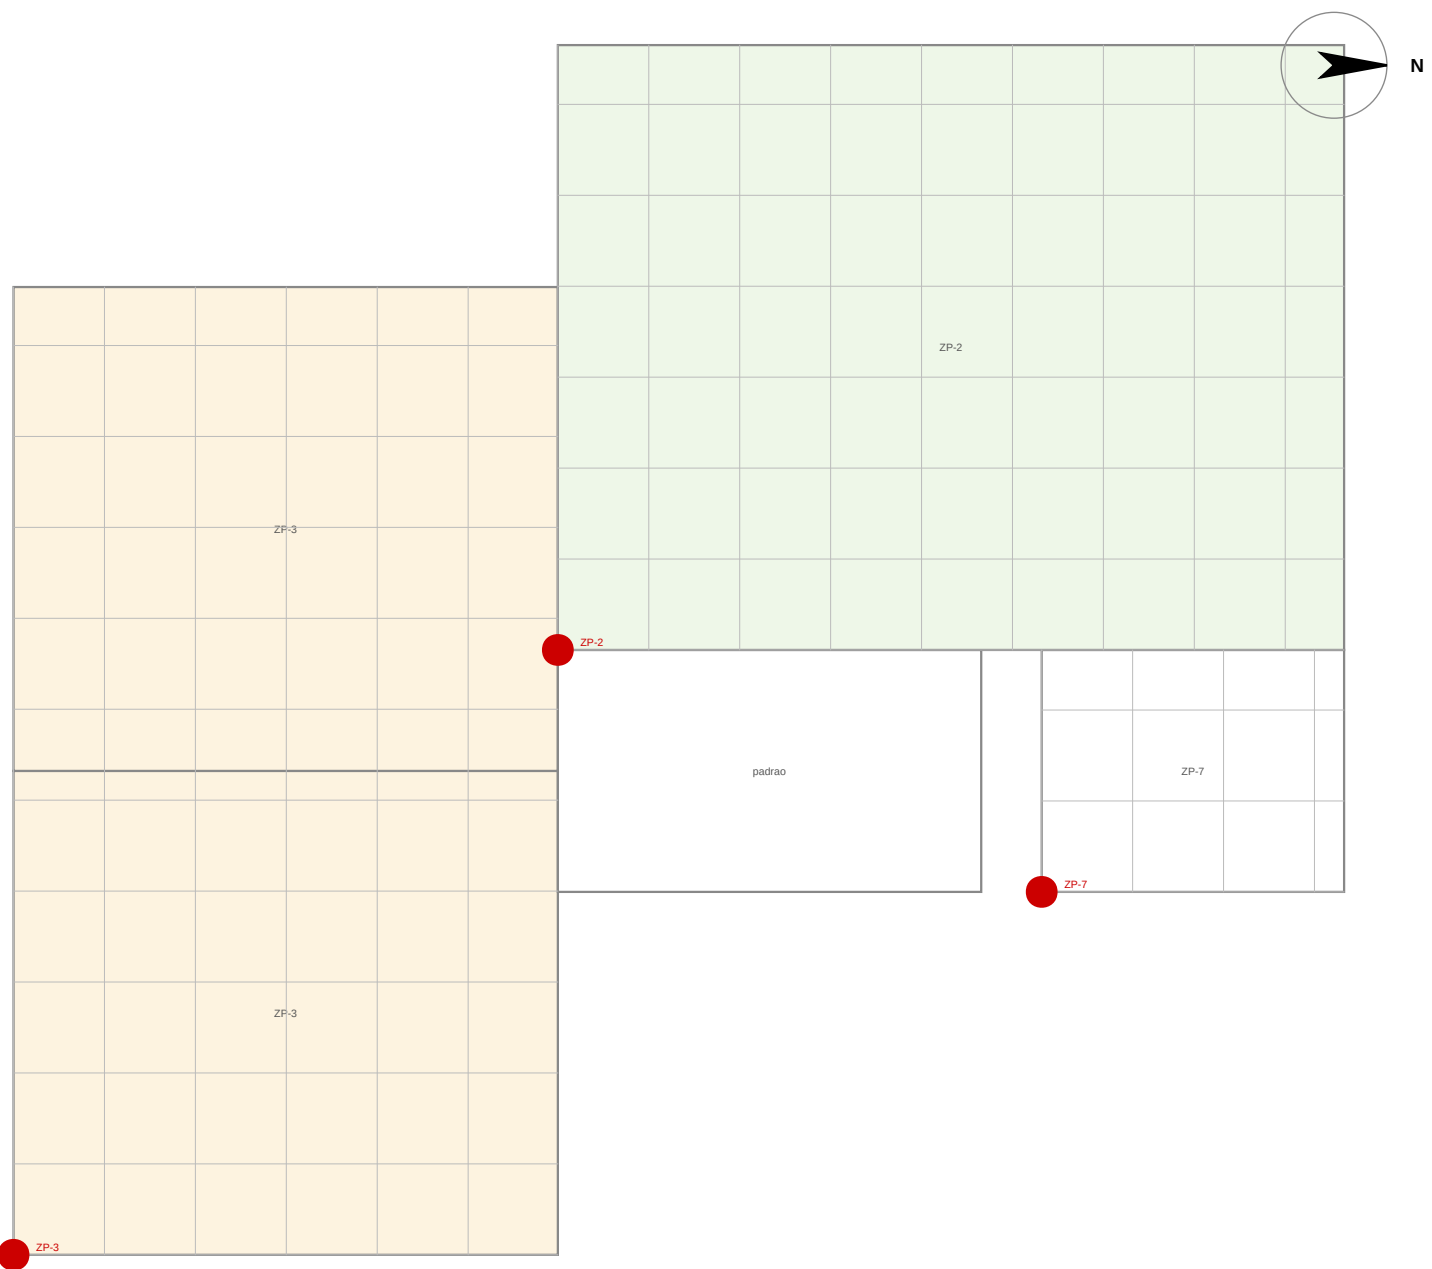

2 PAGINACAO — SUPERIOR
ESCALA 1:75

NOTAS

* Página no projeto e decida onde fica o corte. Não paginar e desenhe o corte aparecer no lugar mais visível.

* Ambientes integrados receberão uma malha, a porta deslizada no meio da sala não tem parede para diferenciar.

* Recorte interno acima 20% da peça, abaixo de 20% o recorte desliza e é reproduzido.

PROJETO PORTO REAL

RESIDENCIA UNIFAMILIAR (MANAUS - AM) | SUELE TATIANA-PS

PROJETO ARQUITETONICO

PAGINACAO DE PISO E ZONAS DE REVESTIMENTO

BASE GEOMETRICA

União Consolidada

PROJETO (previsão)

UNIDADE METRICA: MM

ESCALA

1:75

FORMATO A1

MALHA 600/600/600

EXIBICAO

ESTUDO PRELIMINAR RAO

NAO LIBERADO PARA OBRA

SEM ART / RNT

PROJECION

24

DE 25 REVIRAO