
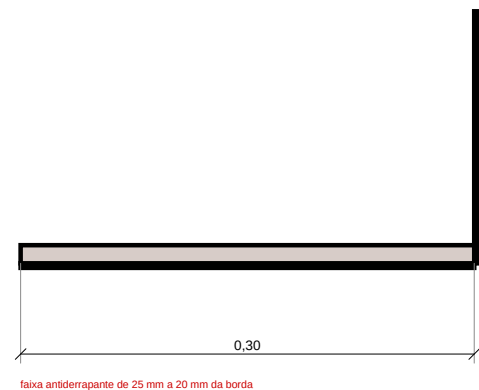
 
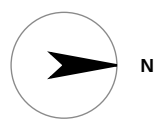


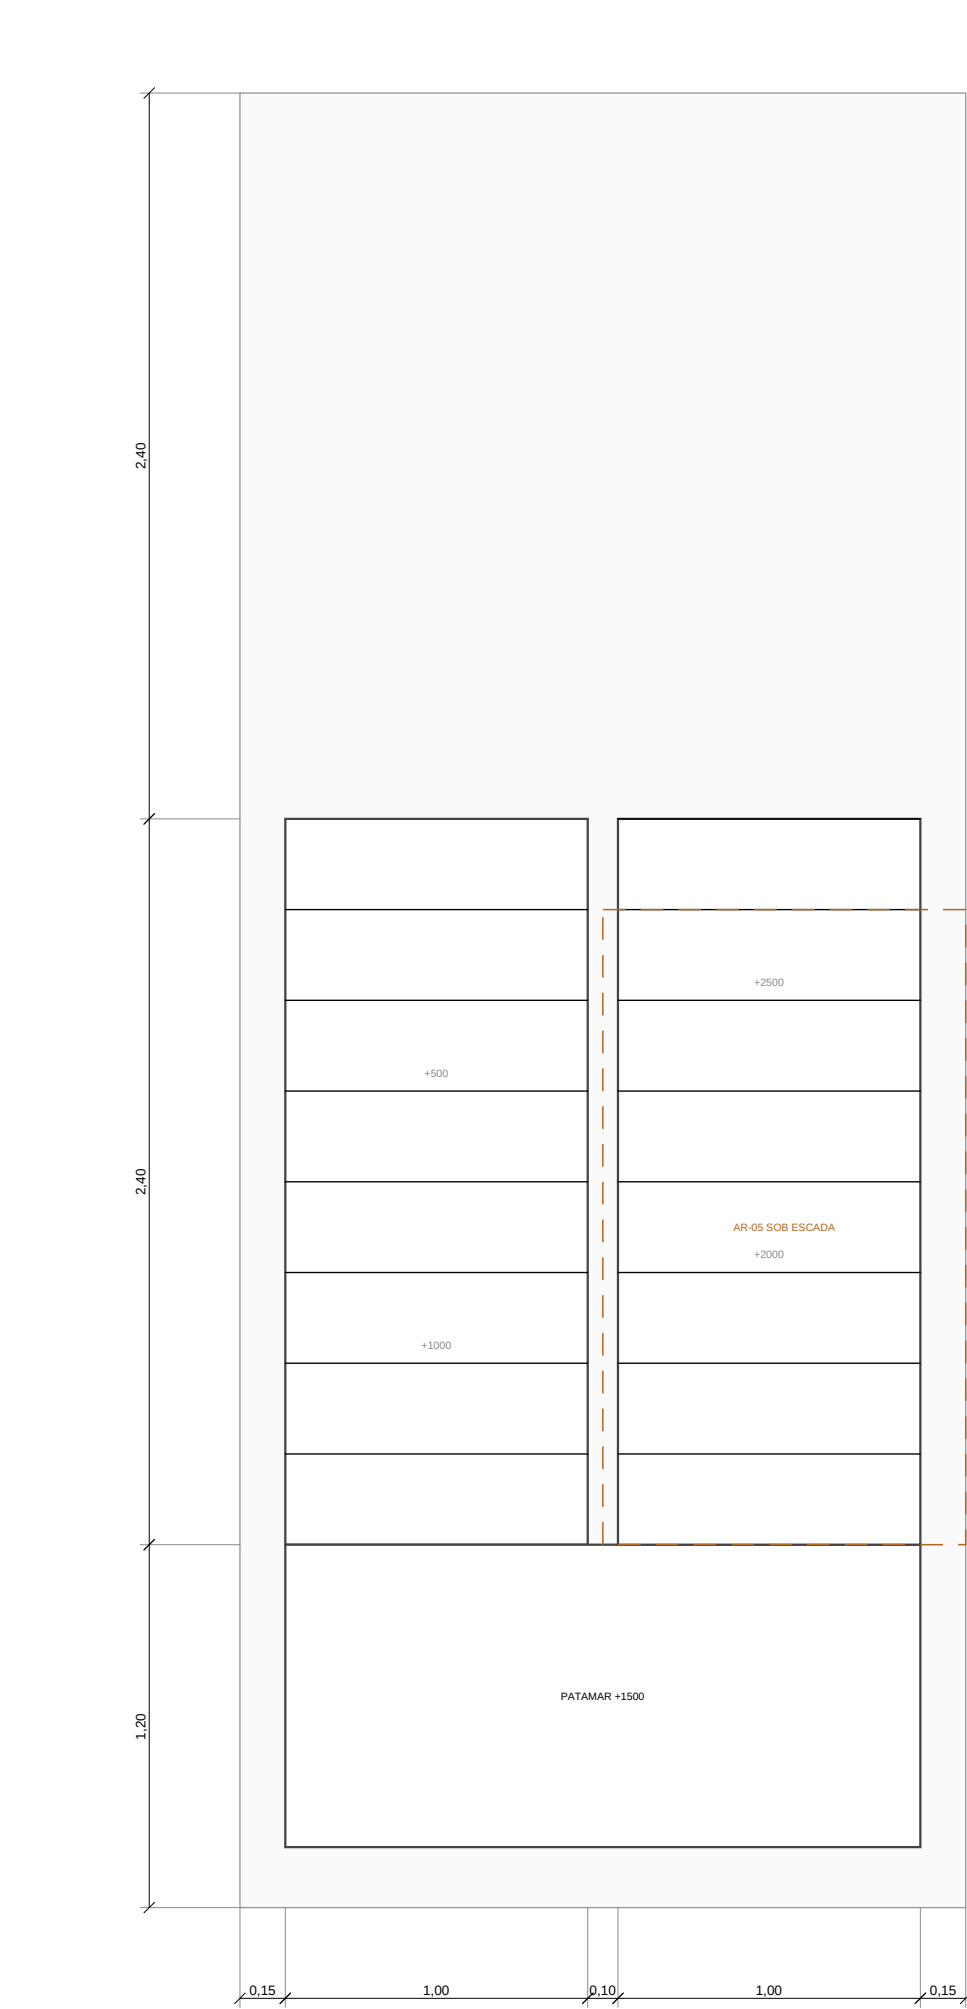

espelho fechado (NBR 9050)

chapa 80x80x3 mm - preenchido 90x x 300

1 PLANTA DA ESCADA

ESCALA 1:25

VERIFICACAO DA ESCADA

ITEM	PROPOSTO	NORMA	
Espelho	186,67 mm	18 a 18 cm (NBR 9077)	OK
Piso	300 mm	min 28 cm	OK
Bondex (2h + g)	623,3 mm	600 a 650 mm	OK
Largura útil do lance	1000 mm	min 1.200 mm (para edifícios) e 1.000 mm (para vilas)	OK
Platamar	1000 mm	min largura do lance	OK
Altura livre mínima	0 mm	min 2100 mm	RECU
Guarda-corpo	1100 mm	min 1.200 mm (NBR 14738)	OK
Corrimão	920 x 700 mm	Acabado 92 cm x 70 cm (NBR 9050)	OK
Espelho fechado	sem	conformidade com esta norma	OK
Desnível vencido	3000 mm	18 x 186,67 mm	OK

O QUE A PLANTA NAO MOSTRA

QUESTAO	RESPOSTA
Por que o primeiro espelho sobre o eixo é de 18,67 cm?	o primeiro espelho sobre o eixo de simetria da escada, com 1.000 mm de altura livre, é o mesmo que a altura da cobertura do primeiro lance.
Por que a verificação da altura livre é bidimensional?	altura livre da escada e o único critério que não aparece em planta horizontal, dependendo da cor da escada e da cor do que há acima dela.
O que há sob o segundo lance?	intergalo com altura útil variável, dimensionado como amarrado (NBR 9050) mas a circulação tem espaço livre.
Por que o espelho fechado?	degrau variado próximo à porta do pé de quem usa degrau ou tem mobilidade reduzida (NBR 9050).
Por que corrimão duplo?	920 mm para adulto e 700 mm para criança, em caso de escada aberta para a sala, o segundo corrimão é o que realmente se usa.

NOTAS

- 18 espelhos de 186,67 mm e piso de 300 mm. Bondex 2h + g = 623,3 mm (falso recomendado 600 a 650).
- Altura livre mínima 2100 mm (NBR 9077), verificada diagonalmente a degrau contra a tape e o vazio acima.
- Guarda-corpo 1100 mm, corrimão duplo em 920 x 700 mm (NBR 9050).
- dois perfis U 200 laterais com degrau em chapa dobrada 3 mm.

PROJETO PORTO REAL

RESIDENCIA UNIFAMILIAR (MARIAUS - AM) | SUEZ TATIANA-PS

PROJETO ARQUITETONICO

ESCADA — DESENHO EXECUTIVO

BASE GEOMETRICA	ESCALA	EMISSAO	PROJECION
Unidade Consolidada	indicada	ESTUDIO PRELIMINAR RAO	25
Projeto (previsão)	FORMATO A1	NAO LIBERADO PARA OBRA	SEM ART / RNT
Unidade (previsão)	MAQUETA 600x900	SEM ART / RNT	DE 25 REV RAO