


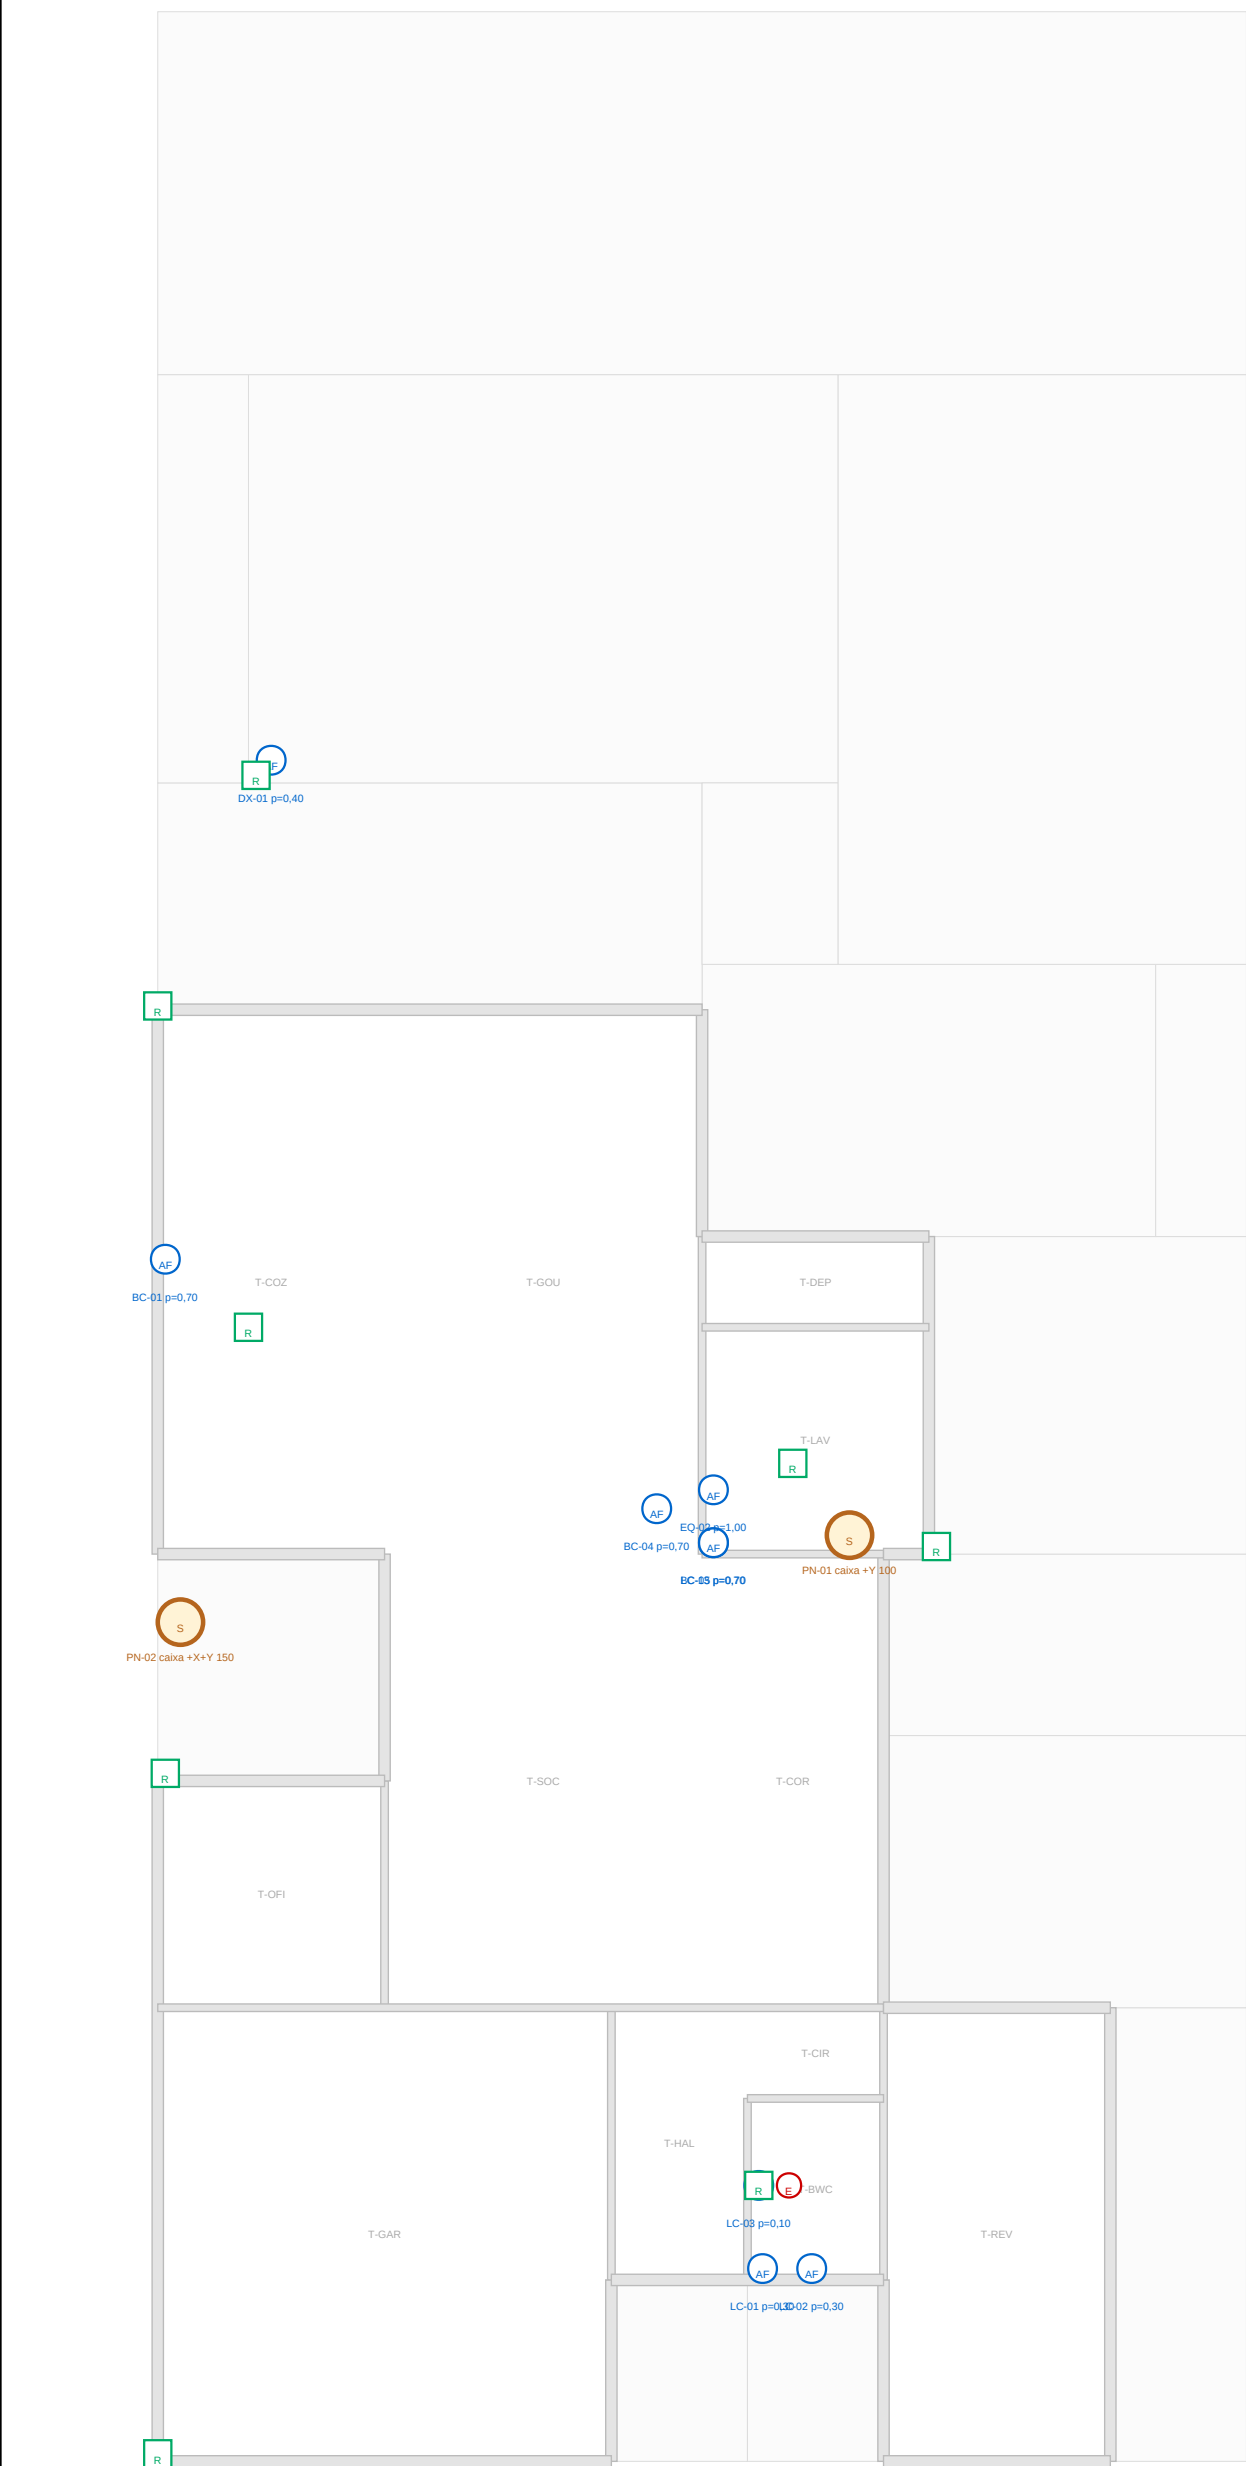


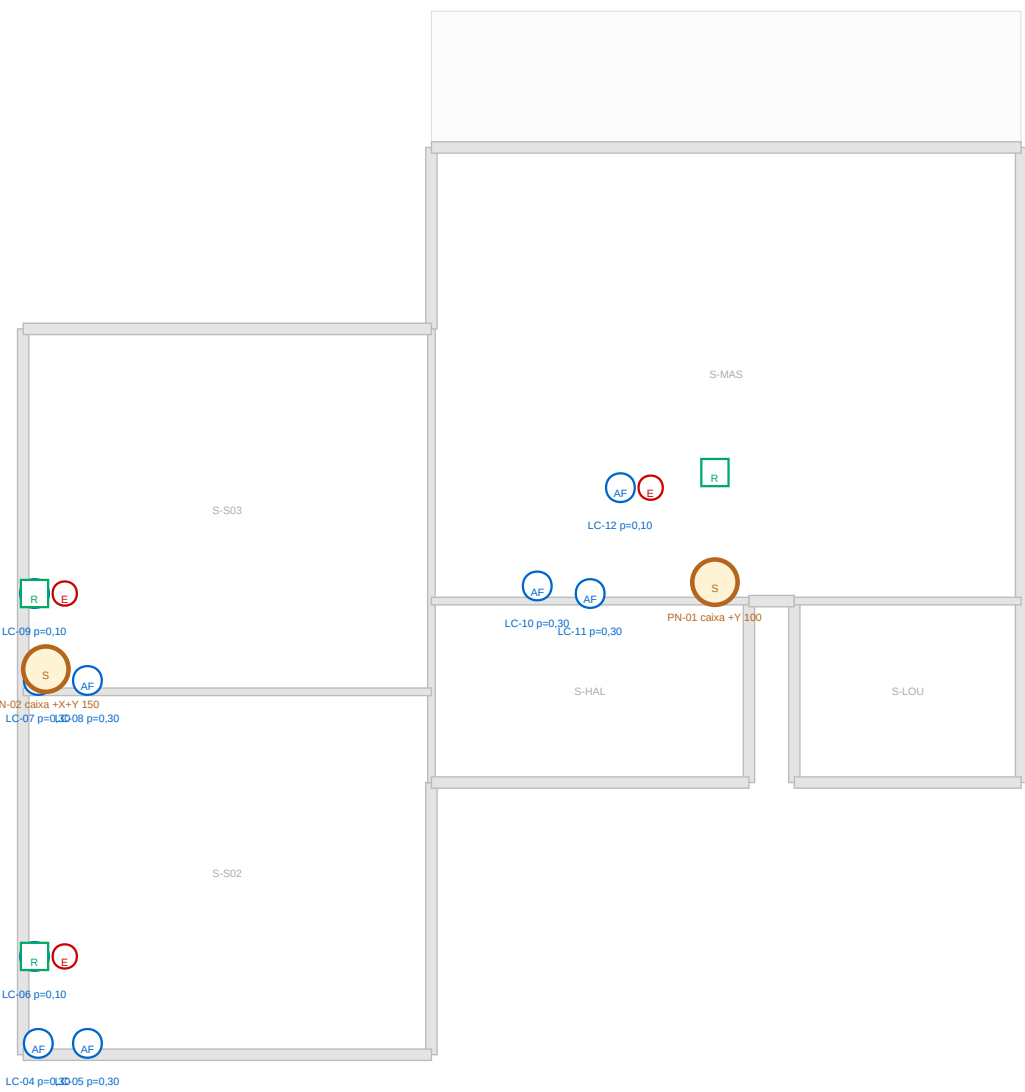

1 PONTOS HIDRAULICOS — TERREO
ESCALA 1:100

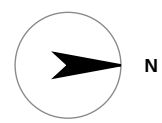

2 PONTOS HIDRAULICOS — SUPERIOR
ESCALA 1:100

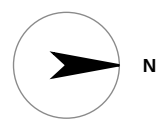

TRECHO	PECAS	PESOS	Q (L/s)	DN AGUA	V (m/s)	UMC	DN ESGOTO	REGIME
Superior	8	2,10	0,435	DN25	1,19	27	DN100	pressurizado
Terreo	9	4,80	0,884	DN25	1,81	36	DN100	gravidade
GERAL	18	7,00	0,794	DN32	1,31	33	DN100	gravidade

COD	AMB	TIPO	PESO	UMC	DN AF	DN ESG	QUENTE
LC-01	T.001C	vaso	0,30	6	DN25	DN40	—
LC-02	T.002C	lavatório	0,30	1	DN25	DN40	—
LC-03	T.003C	box	0,30	2	DN25	DN40	sim
LC-04	S-001	vaso	0,30	6	DN25	DN40	—
LC-05	S-002	lavatório	0,30	1	DN25	DN40	—
LC-06	S-003	box	0,30	2	DN25	DN40	sim
LC-07	S-004	vaso	0,30	6	DN25	DN40	—
LC-08	S-005	lavatório	0,30	1	DN25	DN40	—
LC-09	S-006	box	0,30	2	DN25	DN40	sim

COD	AMB	TIPO	PESO	UMC	DN AF	DN ESG	QUENTE
LC-01	S-001	vaso	0,30	6	DN25	DN40	—
LC-02	S-002	lavatório	0,30	1	DN25	DN40	—
LC-03	S-003	box	0,30	2	DN25	DN40	sim
LC-04	T.001C	vaso	0,30	6	DN25	DN40	—
LC-05	T.002C	lavatório	0,30	1	DN25	DN40	—
LC-06	T.003C	box	0,30	2	DN25	DN40	sim
LC-07	T.004C	vaso	0,30	6	DN25	DN40	—
LC-08	T.005C	lavatório	0,30	1	DN25	DN40	—
LC-09	T.006C	box	0,30	2	DN25	DN40	sim

DECISAO	CONSEQUENCIA HIDRAULICA
Chuveiro elétrico em vez de aquecimento central	peso 0,02 por chuveiro em vez de 0,40; a soma cai de 8,2 para 7,0 pesos e o alternador de DN40 para DN32
Limite de velocidade por conforto, não por norma	DN32 elevando a soma a 2,07 m/s e 3,0 m/s e não mais DN30. Causa alguns metros de tubo
Pressurizador na rede superior	0,5 mca por gravidade nos setores chuveiro elétrico, TC-14 entrega 12 mca
Redes pluviais sem ligação a valas	rede de rede e fisicamente separada, com cot e identificação próprias, não há pontos de conexão cruzada possíveis
Canal de grelhas antes da inspeção	cota 114 > TC-11 (DN-11) > TC-12 > rede, DN100 com cobertura de 2 m

NOTAS

- Água fria por metrado dos pesos (DN32) Q = 0,20 e vazante dos pesos = 0,794 L/s com 7,0 pesos.
- Alimentador DN32 a 1,32 m/s — limitado pelo conforto (2,0 m/s) não pela norma (3,0 m/s).
- Exigido por UMC (DN32) 33 UMC, tubo de queda DN32, ventilação DN40.
- Chuveiro ELA-TRACO sem peso 0,02, mas 0,40 a decisão de aquecimento aquece água com diâmetro menor em toda a casa.

PROJETO PORTO REAL

RESIDENCIA UNIFAMILIAR (MANSÃO - AM) | SOBR TATIANA-PS

PROJETO ARQUITETONICO

INSTALACOES HIDROSSANITARIAS

BASE GEOMETRICA

União Consolidada

Projeto (preliminar)

UNIDADE MESTRE: AM

ESCALA

1:100

FORMATO A1

MALHA 600/600/600

EMISSAO

ESTUDO PRELIMINAR RAO

NAO LIBERADO PARA OBRA

SEM ART / RNT

PROVA

26

IN-25 REV RAO