


luminária embuída, 3.000 K, RSC 90

afcapso técnico 600 x 600 mm

forro absorvente (alfa 0,70)

FORROS POR AMBIENTE

AMBIENTE	SOLUÇÃO	ÁREA	NOTAS
T.CC1	forro absorvente (α=0,70) aplicado no teto	36,24	único ponto que demanda a instalação de 3,20 x 3,20 x 1,20
T.BC2	gesso liso + cantoneira e lapinha	25,20	abertura para o mobiliário, forro técnico aqui não é
T.CC2	gesso liso branco	13,00	superfície de fácil limpeza sem necessidade de manutenção
S.BC2	gesso liso + la mineral sobre o forro	25,80	la sobre o forro absorve o ruído de ruído no parafuso
S.BC3	gesso liso + la mineral sobre o forro	25,80	idem
S.BC4	gesso liso + la mineral sobre o forro	25,80	idem
T.CC4	sem forro (estrutura aparente)	36,00	ambiente semi-industrial, acústica não é necessária
T.CC5	sem forro (estrutura aparente)	9,00	idem
T.CC6	sem forro (estrutura aparente)	3,00	idem

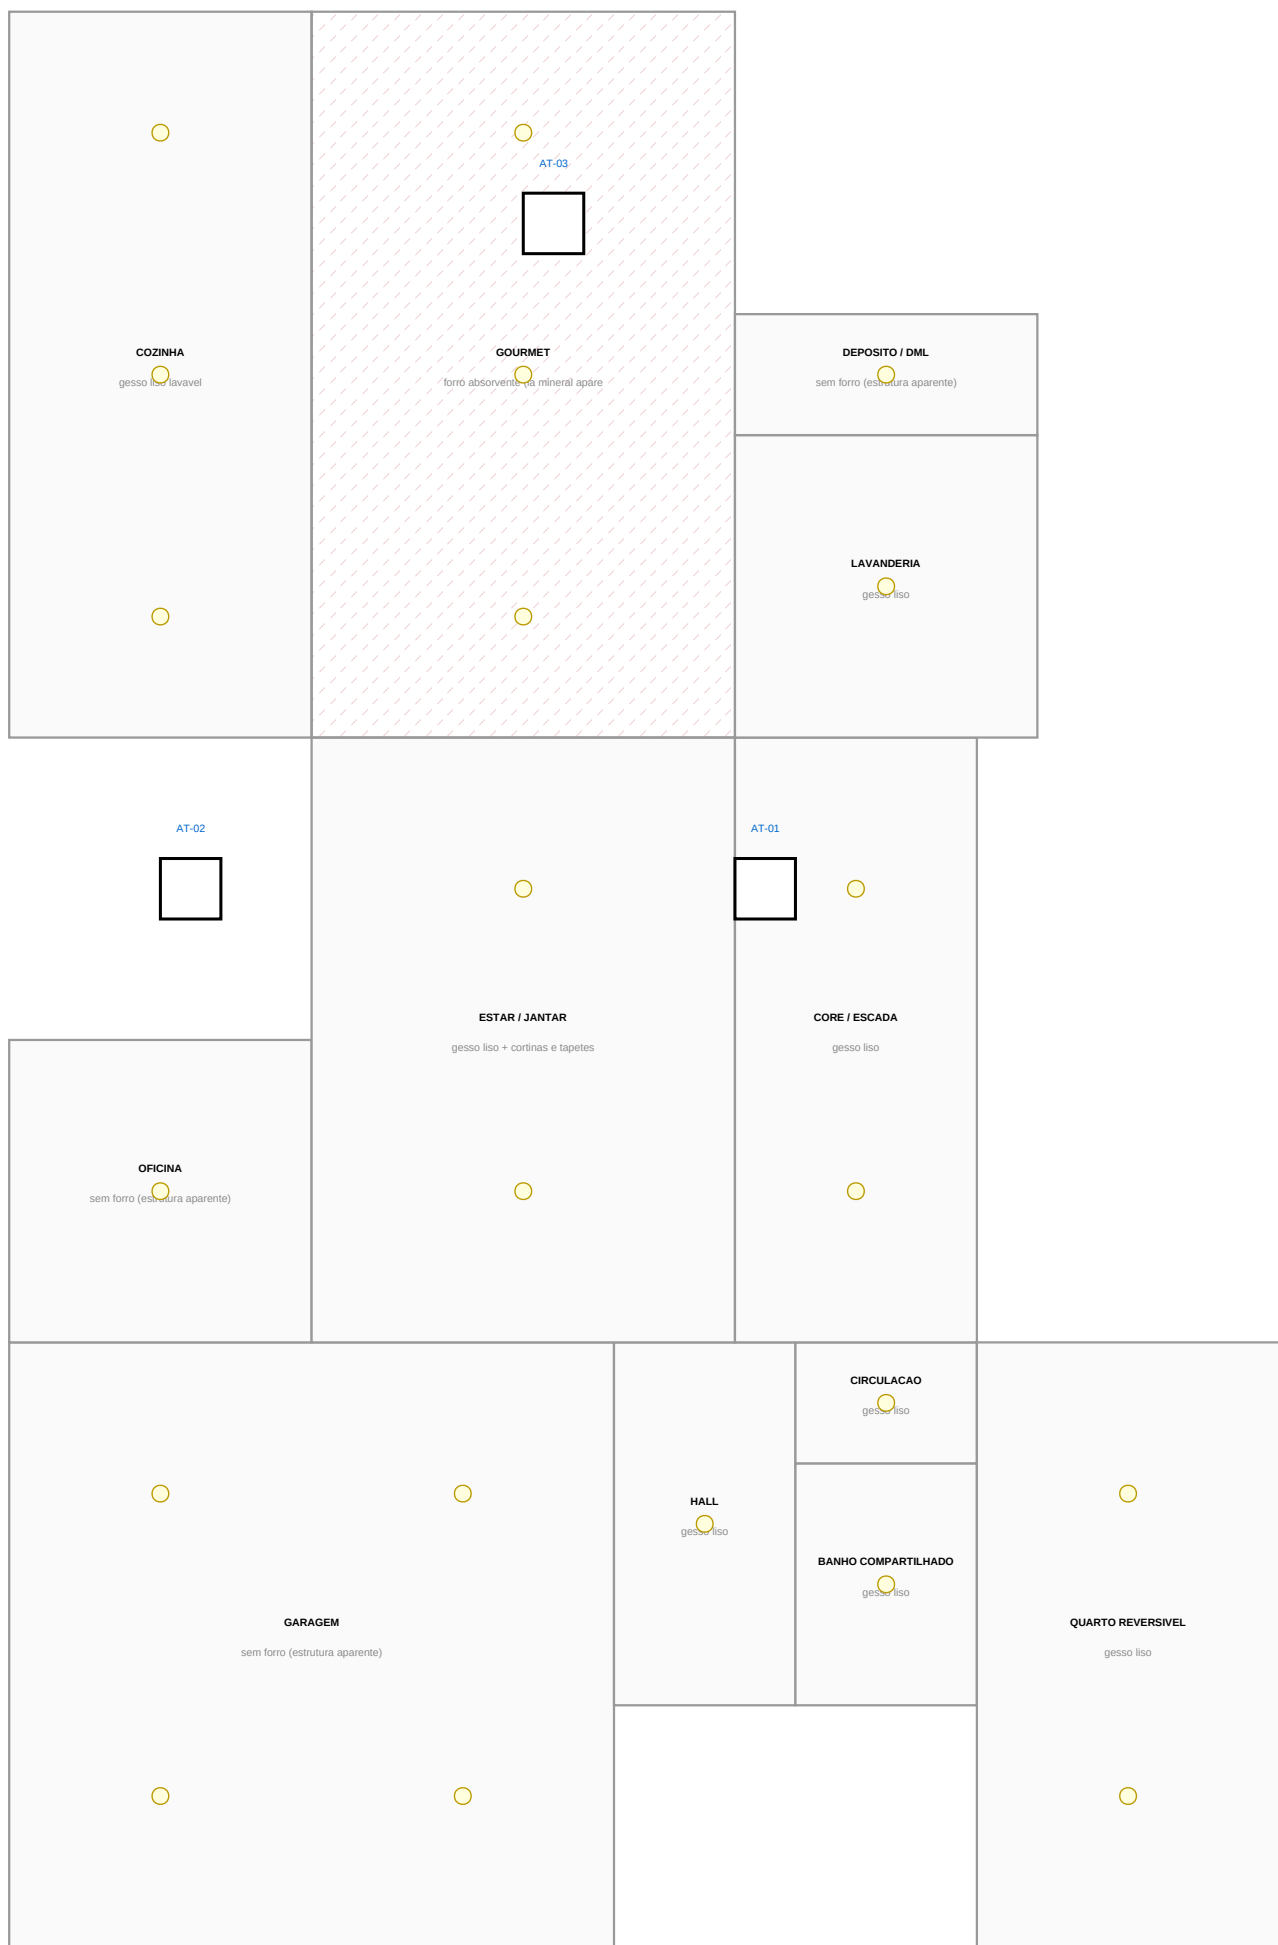

1 FORRO REFLETIDO — TERREO
ESCALA 1:75

NOTAS

- * Planta refletida: vista do forro projetada no plano horizontal.
- * Forro absorvente apenas no gourmet — único ponto com necessidade crítica.
- * Alcapso técnico de 600 x 600 mm, passando de cobertura de 600 mm.
- * Luminária para 3.000 K, RSC 90.

PROJETO PORTO REAL

RESIDÊNCIA UNIFAMILIAR (MANSÃO - AM) | SOBR TATIANA-PS

PROJETO ARQUITETÔNICO

PLANTA DE FORRO E ILUMINAÇÃO

BASE GEOMÉTRICA Linha Consolidada ISO 1572 (previsão) UNIDADE: METROS - MM	ESCALA 1:75 FORMATO A1 MÁQUINA 600/600/300	EMISSÃO ESTUDO PRELIMINAR RSO LADO LIBERADO PARA OBRAS SEM ART / RNT	PROVA 16 06-25 REV 000
---	--	---	-------------------------------------