




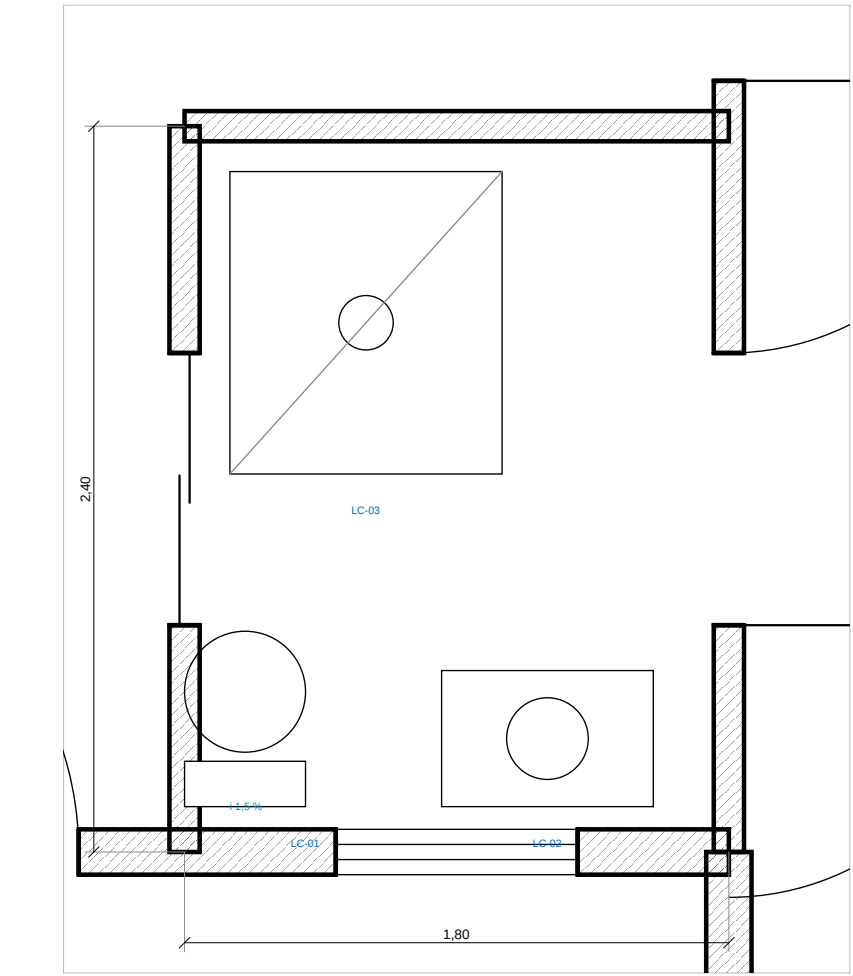


1 BANHO SOCIAL
ESCALA 1:25

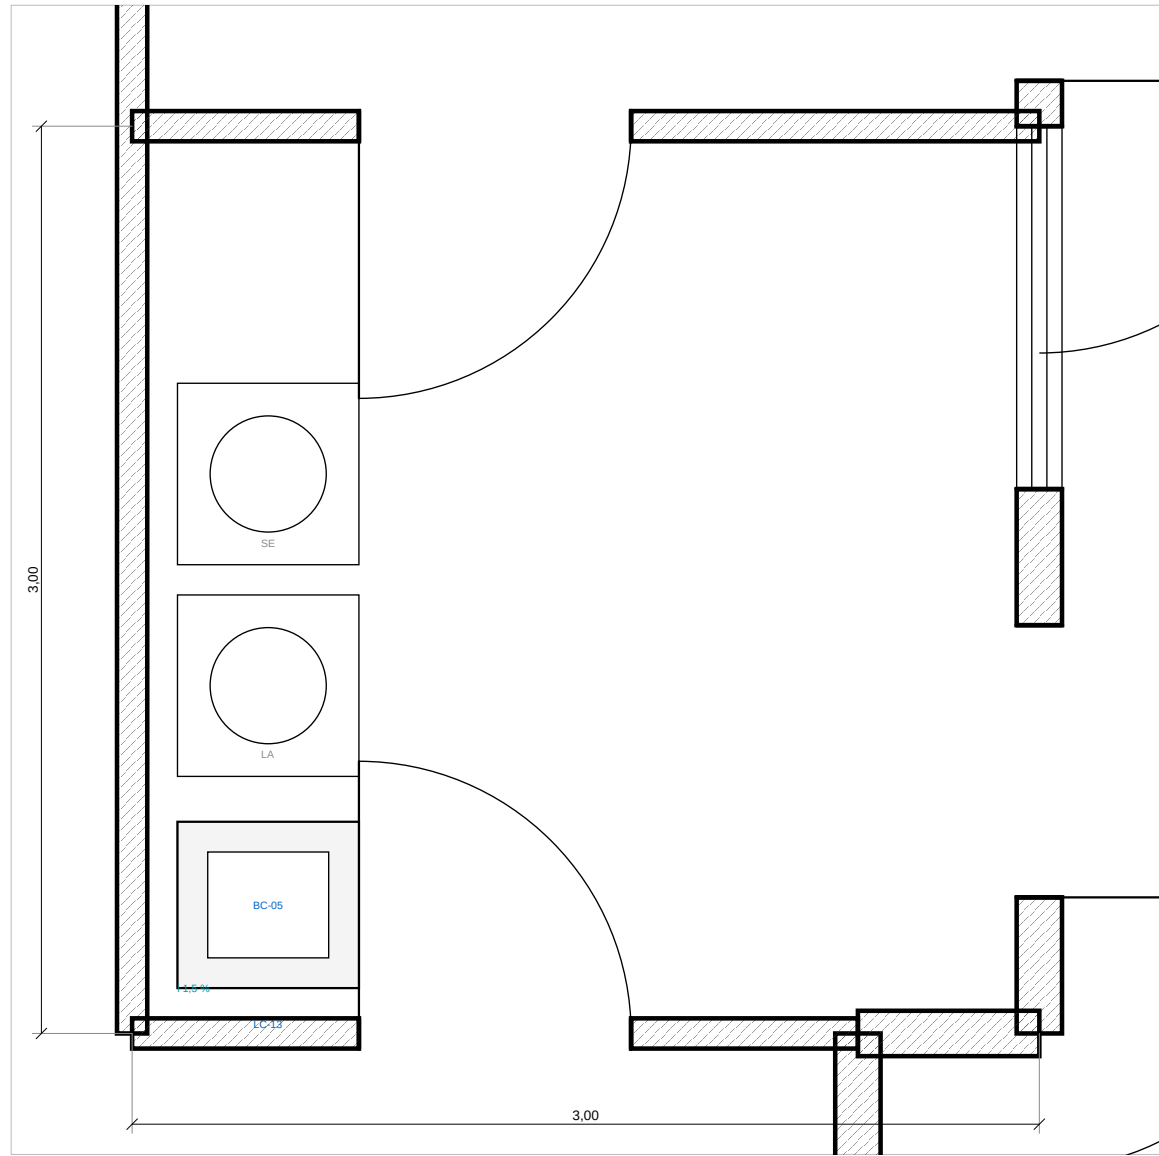

2 LAVANDERIA
ESCALA 1:25

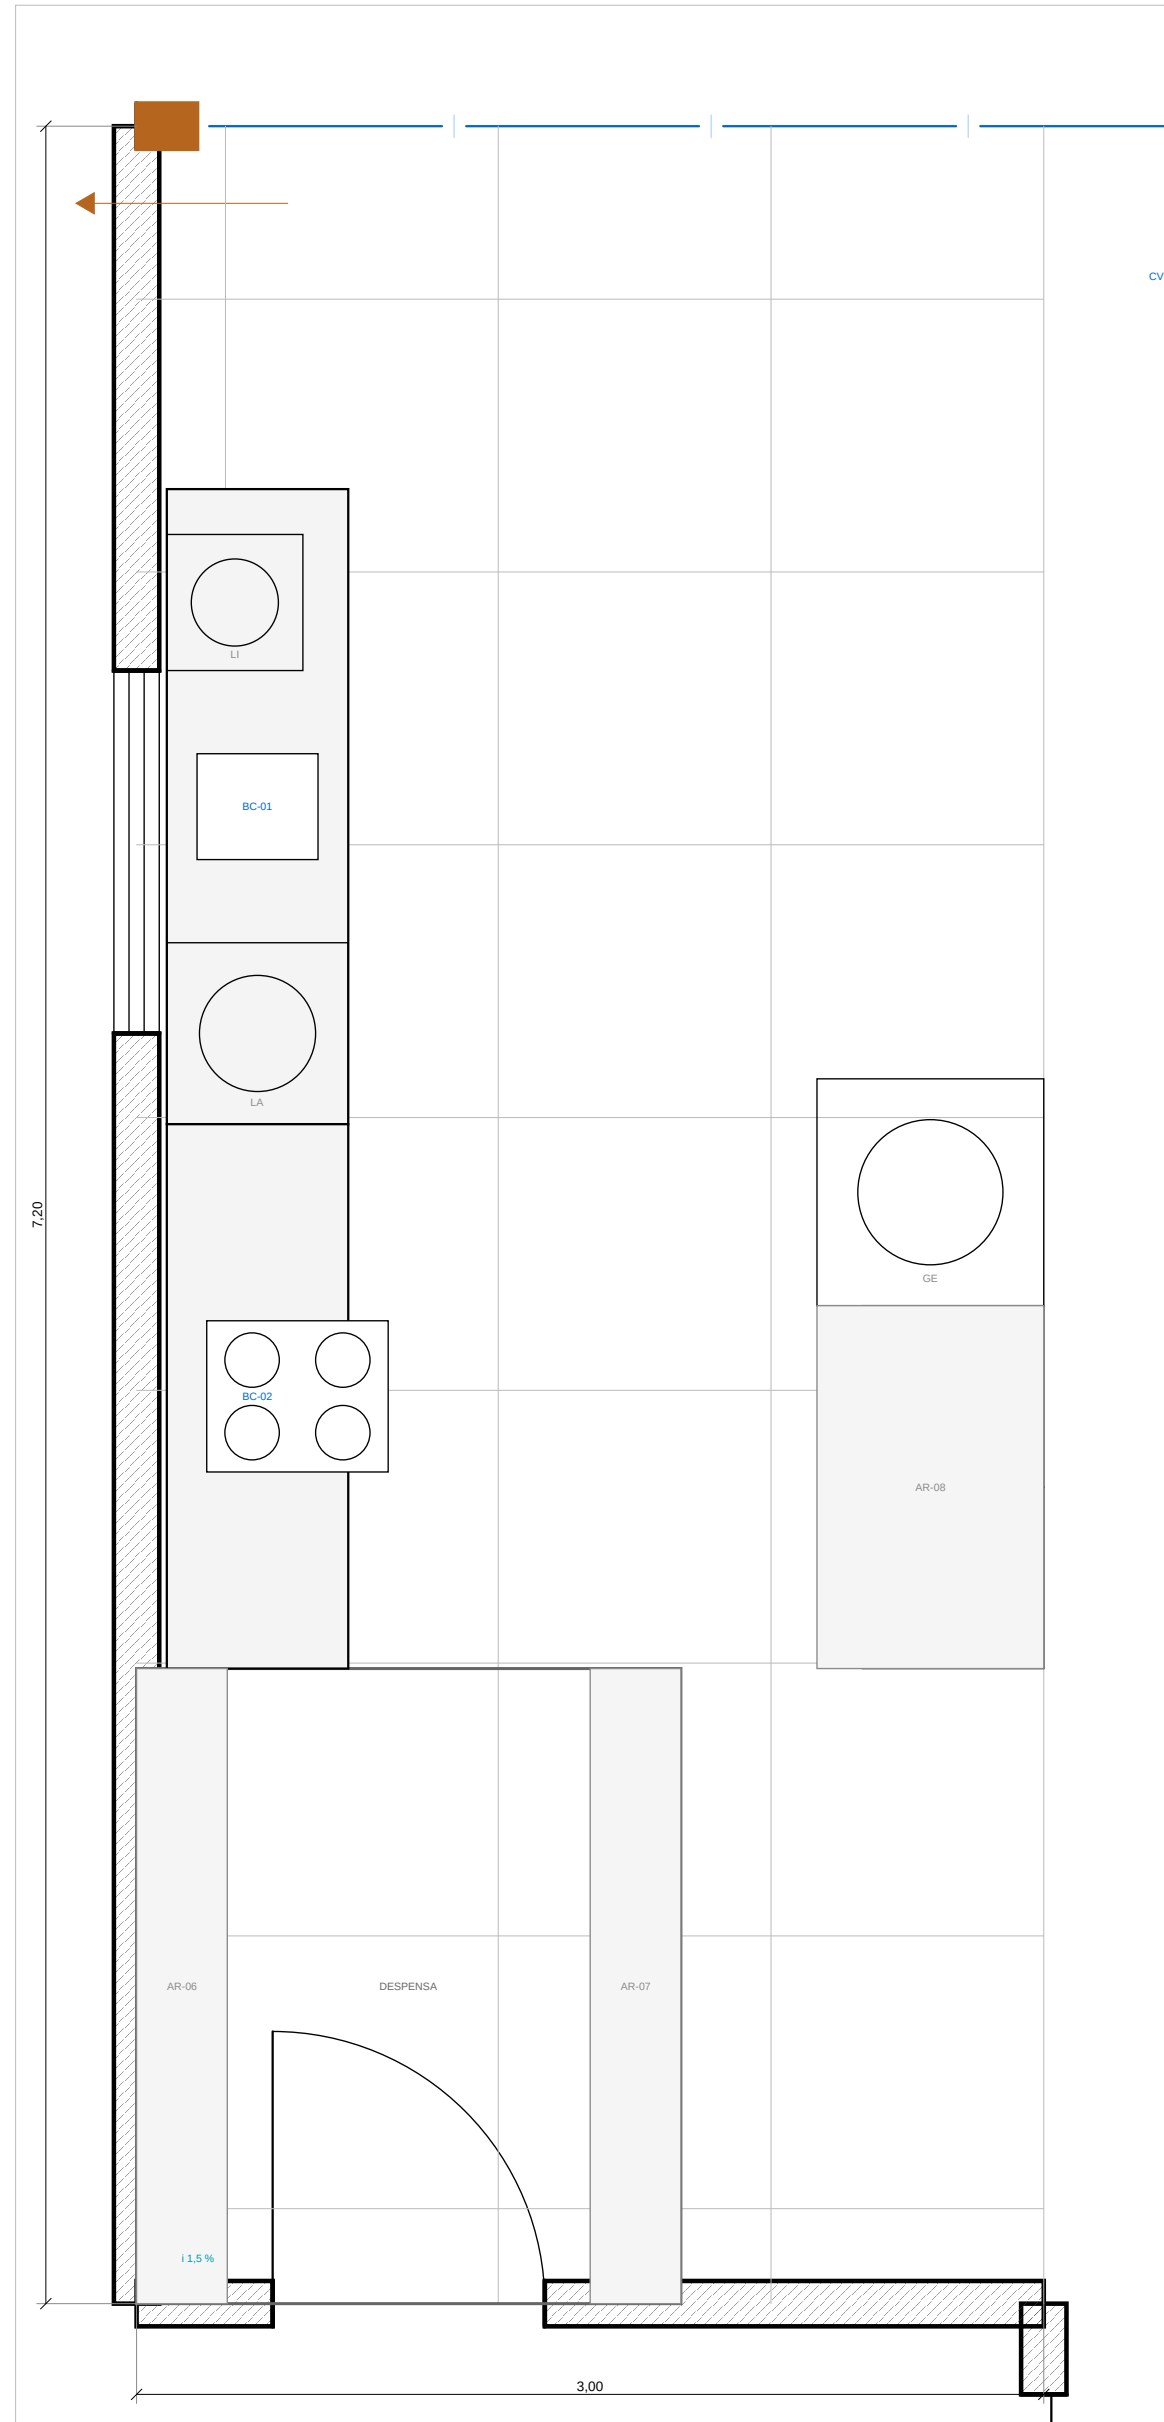

3 COZINHA
ESCALA 1:25

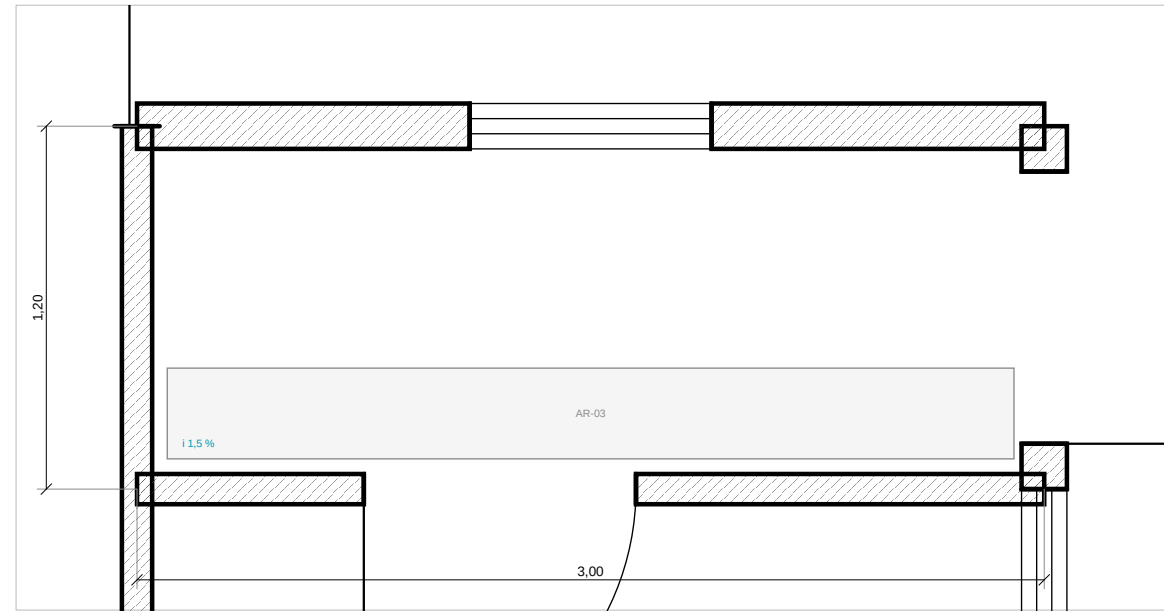

4 DEPOSITO / DML
ESCALA 1:25

PAGINACAO VERIFICADA — PECAS INTEIRAS + RECORTE EM CADA PONTA

AMB	AMBIENTE	ZONA	PEÇA	EXCISO X	EXCISO Y	ALTURA (mm)
T-BWC	BANHO SOCIAL	ZP-4	parede	3 + 0200	3 + 0000	2400 (2 Ruas + 100)
T-LAV	LAVANDERIA	ZP-5	parede	9 + 0200	4 + 0500	2400 (2 Ruas + 100)
T-COC	COZINHA	ZP-1	pis	3 + 0200	7 + 31010	—
T-DEP	DEPOSITO / DML	ZP-5	parede	9 + 0200	1 + 0500	2400 (2 Ruas + 100)

NOTAS

- * Pignificas de piso em linha fina, a malha vem da ZONA de pignificas, nao do canto do ambiente.
- * Peca de piso porcelanado retificado 300 x 300, parede ceramico retificado 300 x 600, porta 2 mm.
- * Camerito de 1.5 % para o piso em toda area molhada, solteira elevada 15 mm nos bicos.
- * Representacao: manta liquida em 2 demoes, subido 300 mm na parede e 1.800 mm nos bicos.

PROJETO PORTO REAL

RESIDENCIA UNIFAMILIAR (MANAUS - AM) | SOUZA TATIANA-PS

PROJETO ARQUITETONICO

AMPLIACOES DE AREA MOLHADA — TERREO

BASE GEOMETRICA Linha Consolidada Projeto (previsão) UNIDADE: METRO (m)	ESCALA 1:25 FORMATO: A1 MATERIAL: 60/60/60/60	EXIBICAO ESTUDIO PRELIMINAR RSO Linha Consolidada PARA OBRAS SEM ART / RNT	PROJECION 22 06-25 REV 000
--	--	---	----------------------------------