




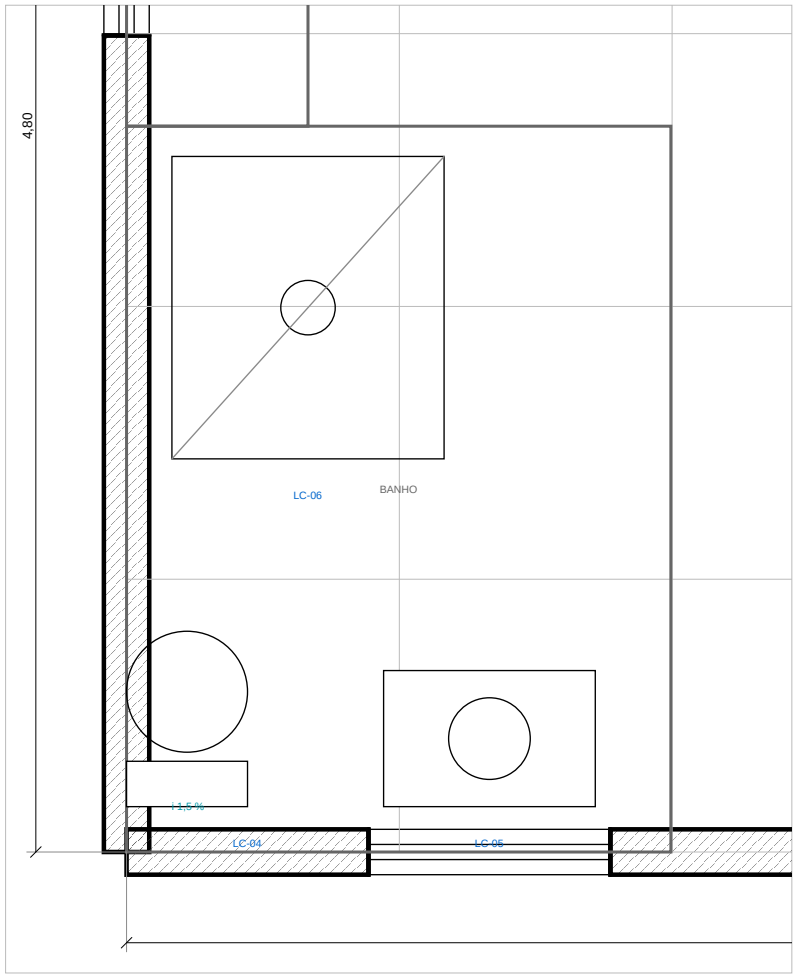


1 SUITE 02 — BANHO
ESCALA 1:25

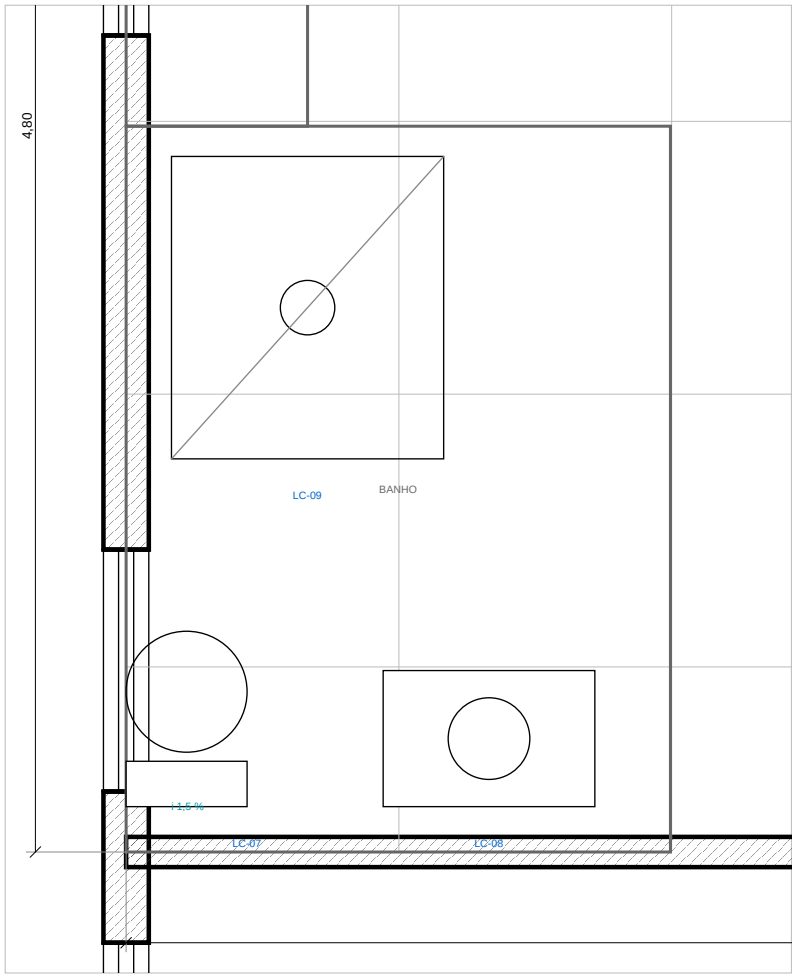

2 SUITE 03 — BANHO
ESCALA 1:25

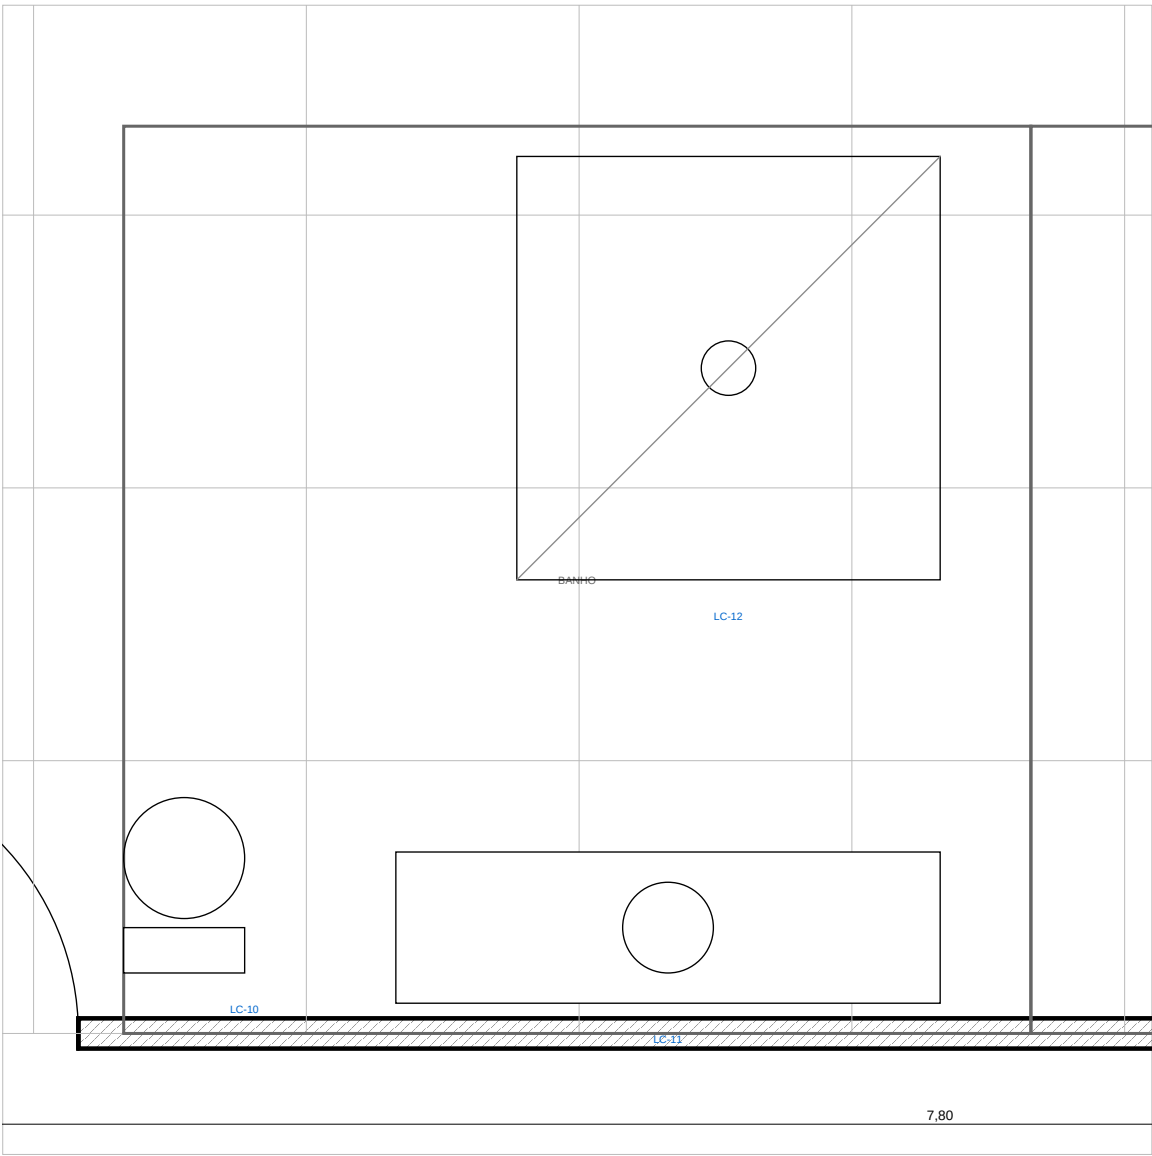

3 MASTER — BANHO
ESCALA 1:25

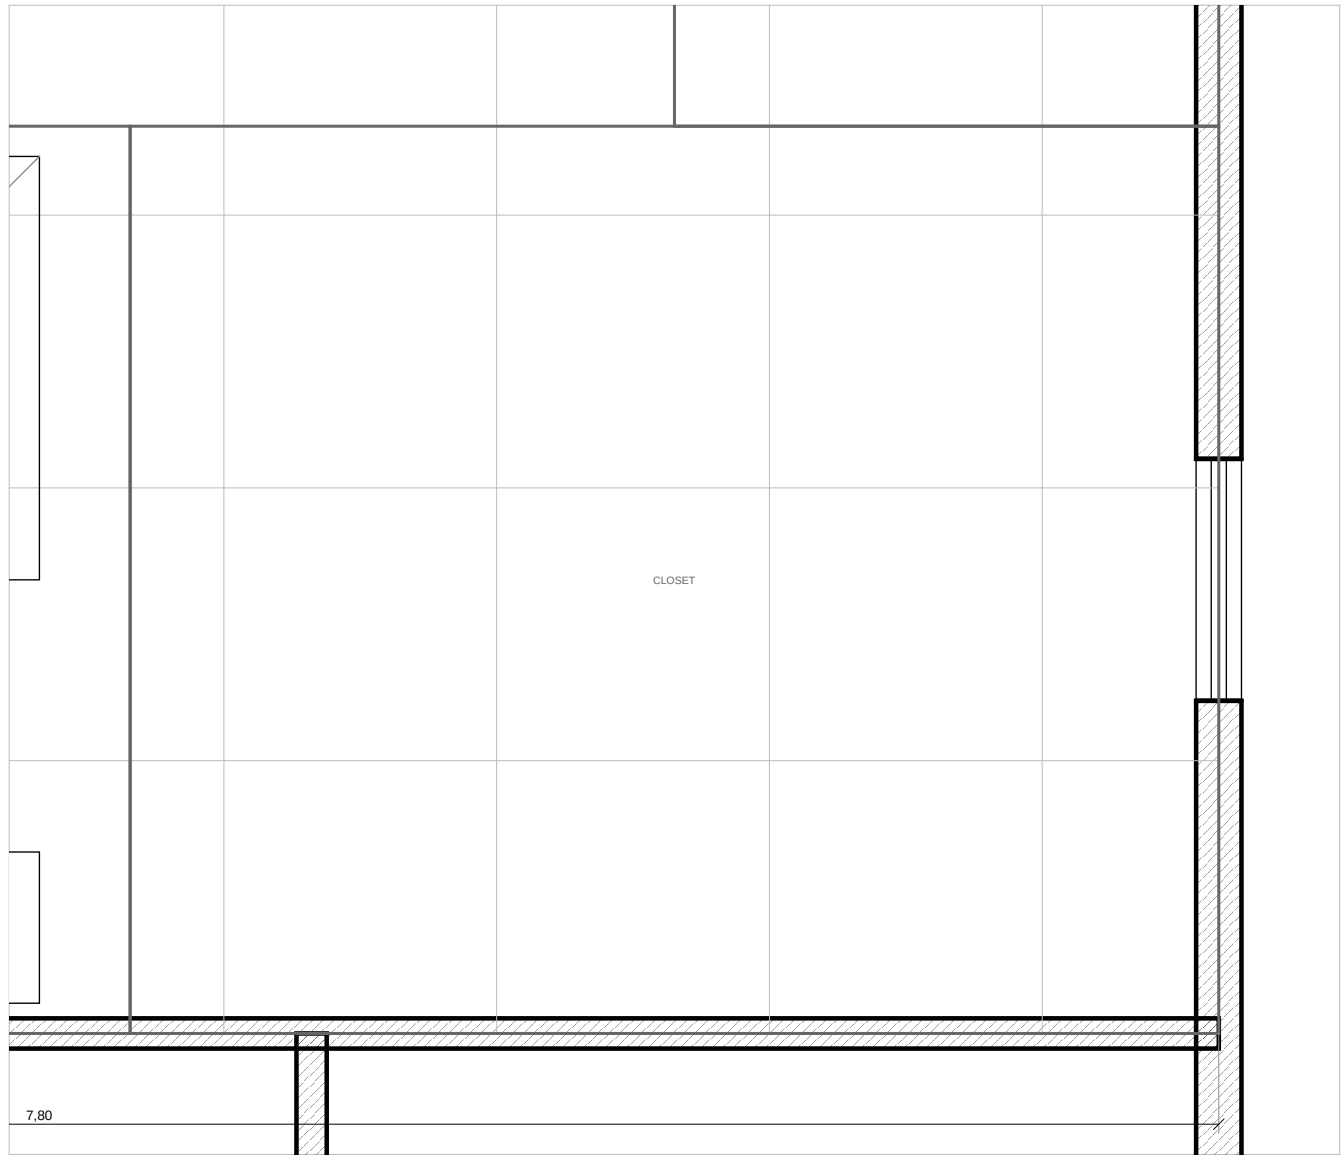

4 MASTER — CLOSET
ESCALA 1:25

PAGINACAO VERIFICADA — PECAS INTEIRAS + RECORTE EM CADA PONTA

AMB	AMBIENTE	ZONA	PEÇA	EXO X	EXO Y	ALTURA (mm)
S-002	SUITE 02 — BANHO	ZP-3	plb	S-002B	S-002B	---
S-003	SUITE 03 — BANHO	ZP-3	plb	S-003B	A-003D07B	---
S-005	MASTER — BANHO	ZP-2	plb	S-005D	C-005B	---
S-006	MASTER — CLOSET	ZP-2	plb	S-006D	C-006B	---

NOTAS

- * Pignonicus de piso em linha fina, a malha vem da ZONA de pignonicus, não do canto do ambiente.
- * Pignonicus de piso porcelanado retificado 300 x 300, parede cerâmico retificado 300 x 600, jato 2 mm.
- * Cimento de 1,5 kg para o piso em toda área molhada, soltura elevada 15 mm nos bicos.
- * Representação: manta líquida em 2 demãos, subido 300 mm na parede e 1.800 mm nos bicos.

PROJETO PORTO REAL

RESIDENCIA UNIFAMILIAR (MANAUS - AM) | SUITE TATIANA-PS

PROJETO ARQUITETONICO

AMPLIACOES DE AREA MOLHADA — SUPERIOR

BASE GEOMETRICA Linha Consolidada plb-RDZ (previsível) UNIDADE MESTRE: mm	ESCALA 1:25 FORMATO A1 MALHA 600/600/300	EMISSAO ESTUDO PRELIMINAR RSO TWO LIBERADO PARA ORCA SEM ART / RNT	PROJETA 23 06-25 REV 000
--	---	---	--------------------------------