


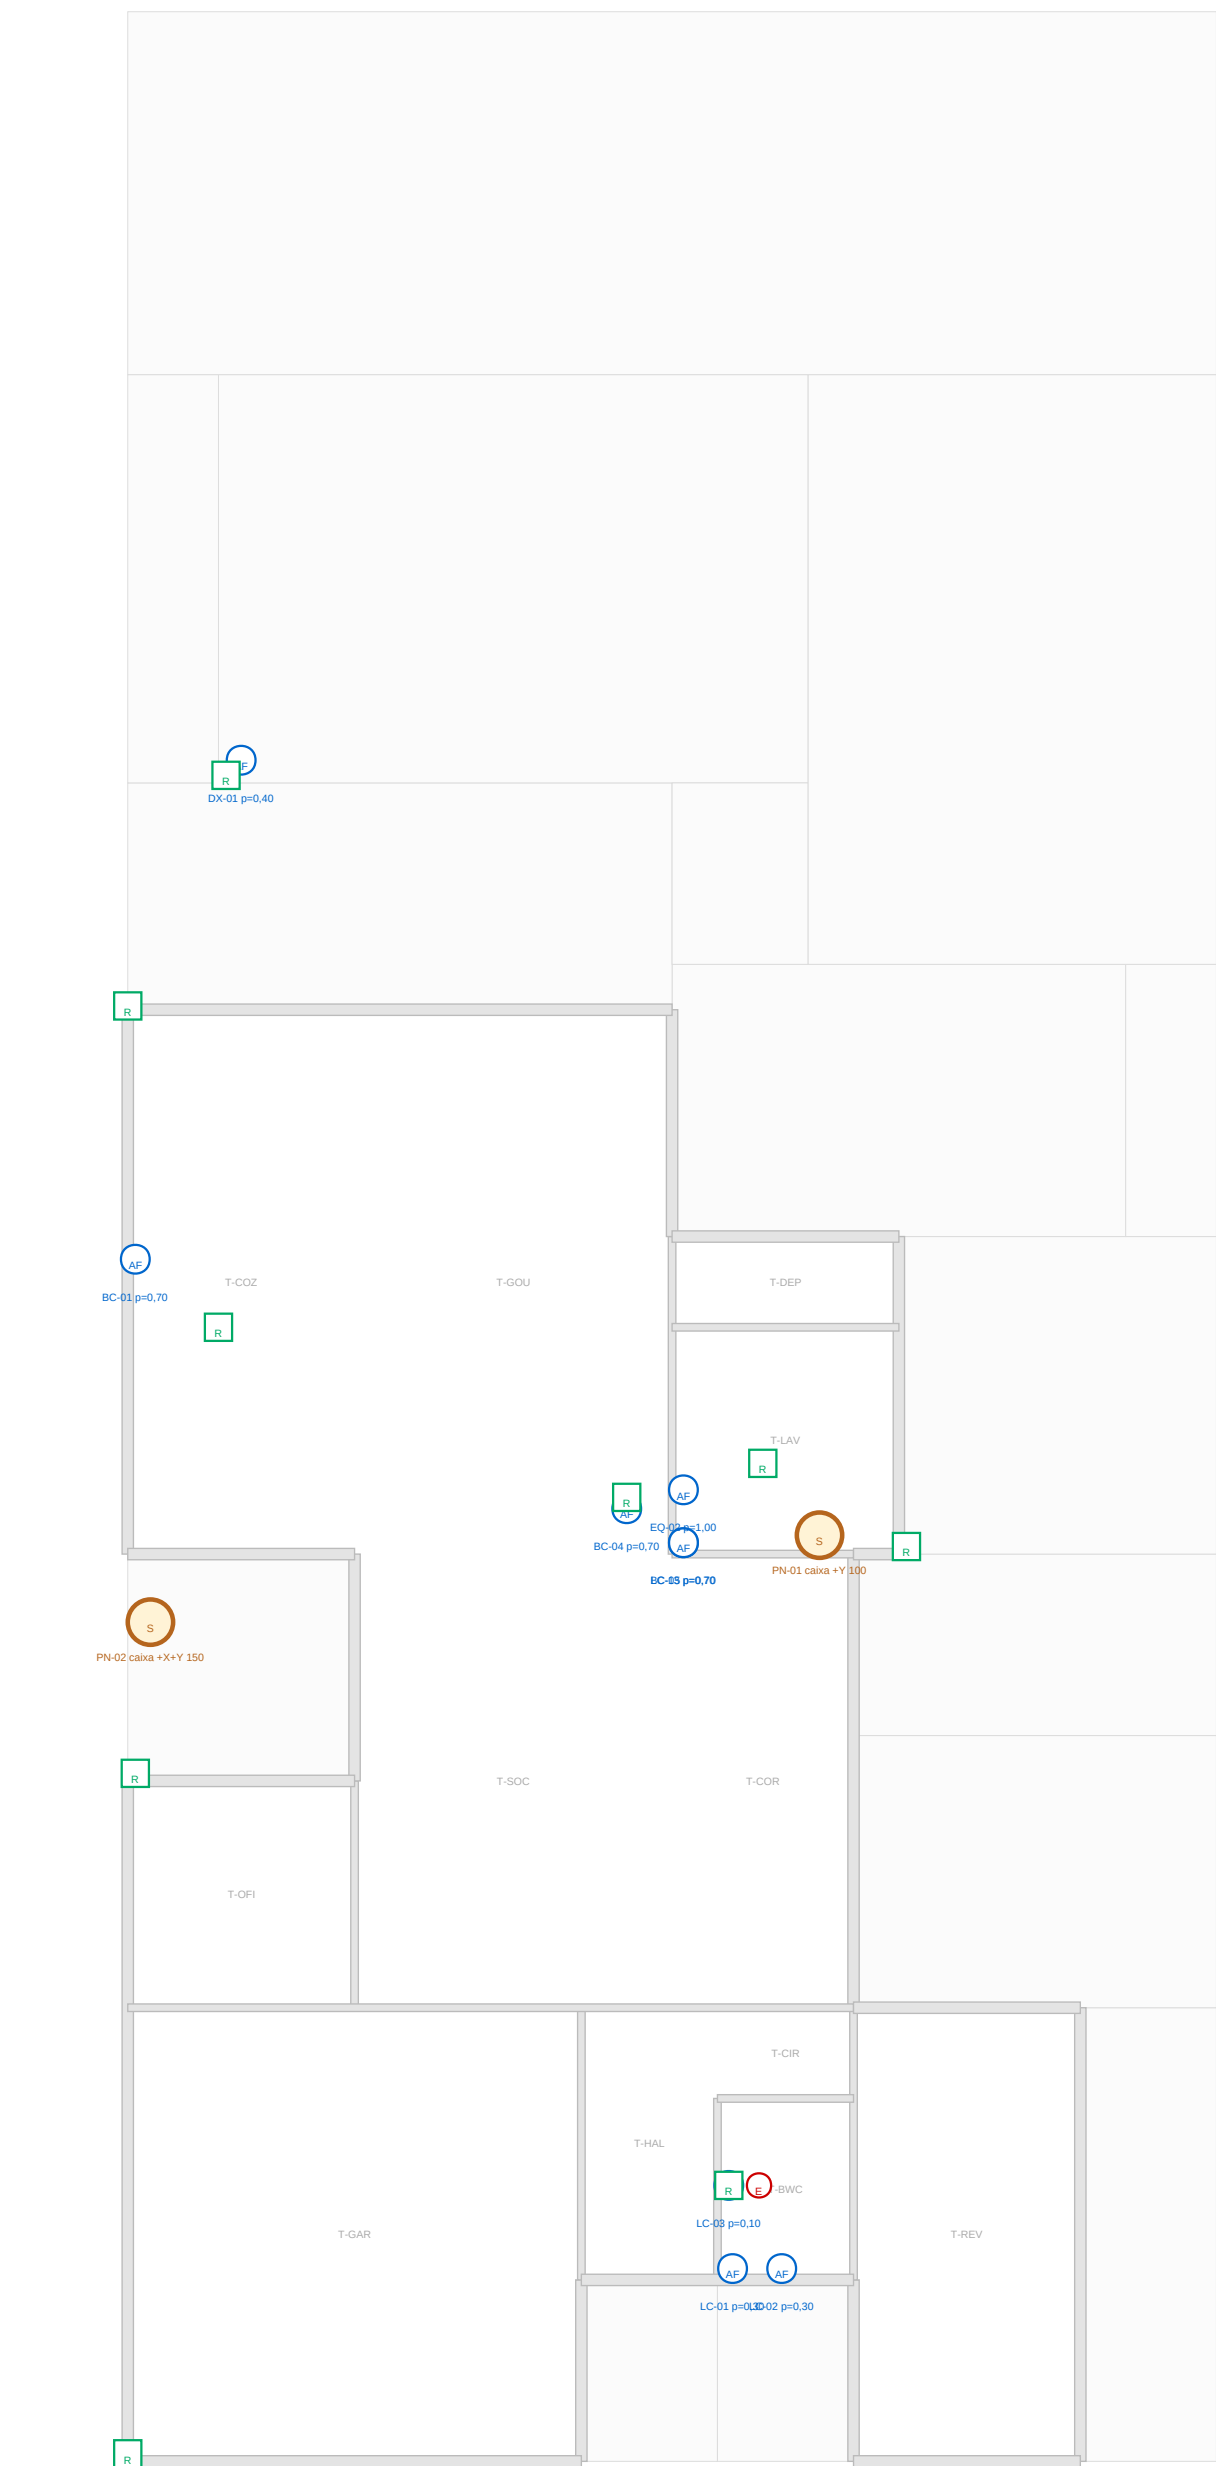


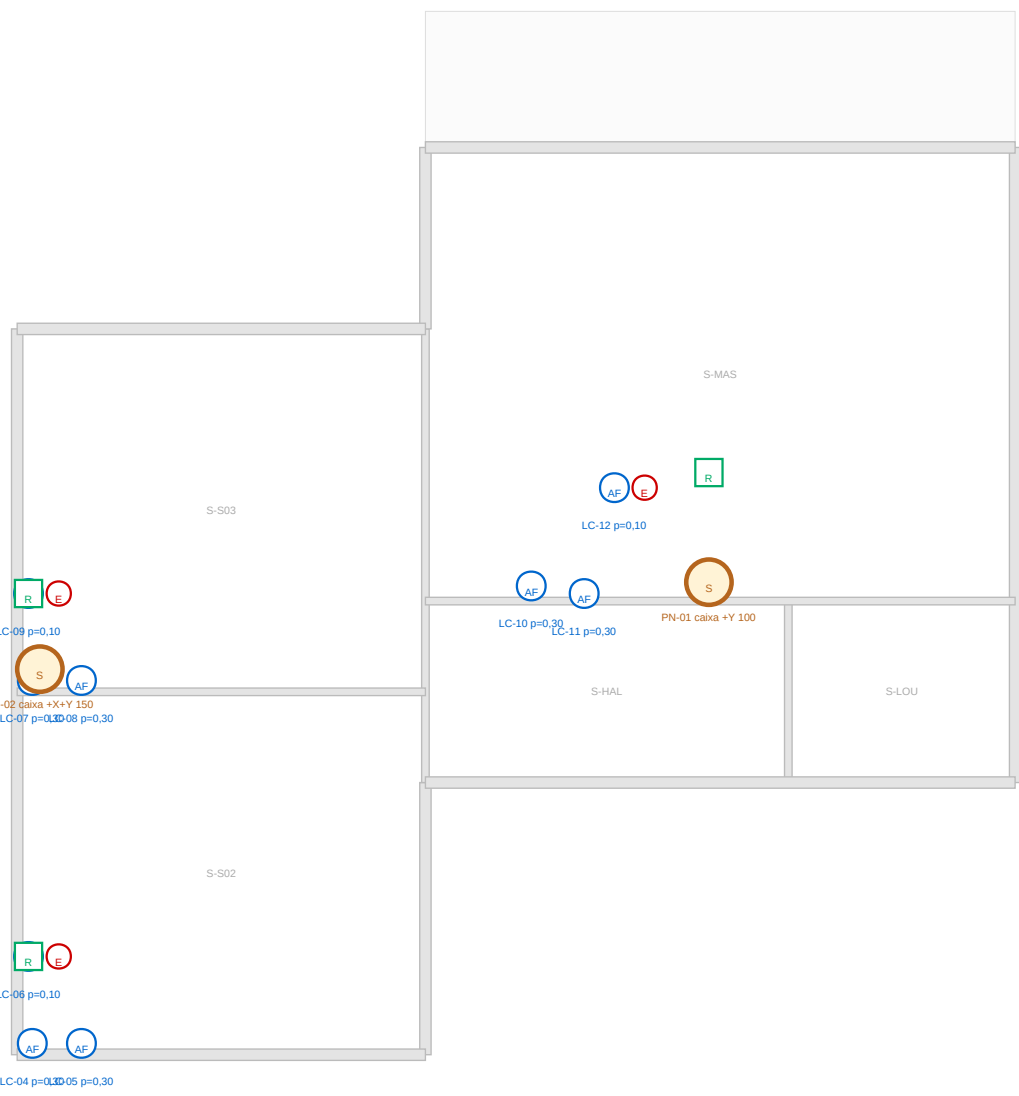

1 PONTOS HIDRAULICOS — TERREO
ESCALA 1:100

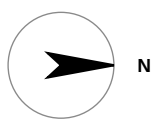

2 PONTOS HIDRAULICOS — SUPERIOR
ESCALA 1:100

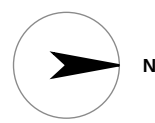

DIMENSIONAMENTO — AGUA FRIA E ESGOTO

TRECHO	PECAS	PESOS	Q (L/s)	DN AGUA	V (m/s)	UMC	DN ESGOTO	REGIME
Superior	8	2,10	0,435	DN25	1,19	27	DN100	pressurizado
Terreo	9	4,80	0,884	DN25	1,81	36	DN100	gravidade
GERAL	18	7,00	0,794	DN25	1,31	33	DN100	gravidade

PECAS DE UTILIZACAO

COD	AMB	TIPO	PESO	UMC	DN AF	DN ESG	QUENTE
LC-01	T-BWC	vaso	0,30	6	DN25	DN40	—
LC-02	T-BWC	lavatório	0,30	1	DN25	DN40	—
LC-03	T-BWC	box	0,30	2	DN25	DN40	sim
LC-04	S-S02	vaso	0,30	6	DN25	DN40	—
LC-05	S-S02	lavatório	0,30	1	DN25	DN40	—
LC-06	S-S02	box	0,30	2	DN25	DN40	sim
LC-07	S-S03	vaso	0,30	6	DN25	DN40	—
LC-08	S-S03	lavatório	0,30	1	DN25	DN40	—
LC-09	S-S03	box	0,30	2	DN25	DN40	sim

(continuacao)

COD	AMB	TIPO	PESO	UMC	DN AF	DN ESG	QUENTE
LC-01	S-MAS	vaso	0,30	6	DN25	DN40	—
LC-02	S-MAS	lavatório	0,30	1	DN25	DN40	—
LC-03	S-MAS	box	0,30	2	DN25	DN40	sim
LC-04	T-LAV	vaso	0,70	3	DN25	DN40	—
LC-05	T-CO2	pin	0,70	3	DN25	DN40	—
LC-06	T-CO2	pin	0,70	3	DN25	DN40	—
LC-07	T-LAV	pin	0,70	3	DN25	DN40	—
LC-08	T-LAV	lavatório	1,00	3	DN25	DN40	—
LC-09	T-DPA	banho, entrada	0,40	2	DN25	DN40	—

DECISOES QUE O DIAMETRO REVELA

DECISAO	CONSEQUENCIA HIDRAULICA
Chuveiro elétrico em vez de aquecimento central	peso 0,02 por chuveiro em vez de 0,40 a soma cai de 0,2 para 7,0 pesos e o diâmetro de DN40 para DN52
Limite de velocidade por conforto, não por norma	DN25 elevando a soma a 2,07 m/s a 3,0 m/s e tudo não bastou. Cade alguns metros de tubo
Pressurizador na rede superior	0,5 mca por gravidade nos setores chuveiro elétrico, TC-14 entrega 12 mca
Redes pluviais sem ligação a valas	rede de rede e fisicamente separada, com cot e identificação próprias, não há pontos de conexão cruzada possíveis
Canal de grelhas antes da inspeção	costuma > TC-11 [DN-1] > TC-12 < rede, DN100 com cobertura de 2 m

NOTAS

- Água fria por rede de dois pesos (DN25) Q = 0,20 e rede de dois pesos = 0,70 L/s com 7,0 pesos.
- Alimentador DN25 a 1,12 m/s — limitado pelo conforto (2,0 m/s) não pela norma (3,0 m/s).
- Exigido por LNC (DN25) 33 LNC, tubo de queda DN25, ventilação DN40.
- Chuveiro ELÉTRICO em peso 0,02, não 0,40 a decisão de aquecimento requerer água quente diâmetro menor em toda a casa.

PROJETO PORTO REAL

RESIDENCIA UNIFAMILIAR (MANSÃO - AM) (SOL TATIANA-PS)

PROJETO ARQUITETONICO

INSTALACOES HIDROSSANITARIAS

BASE GEOMETRICA Linha Consolidada por R22 (previsão) UNIDADE MESTRE: mm	ESCALA 1:100 FORMATO A1 MILHA 405/500/500	EMISSAO ESTUDO PRELIMINAR RSO TWO LIBERADO PARA OBRA SEM ART / RNT	PROVA 26 IN-25 REVISO
--	---	---	------------------------------------