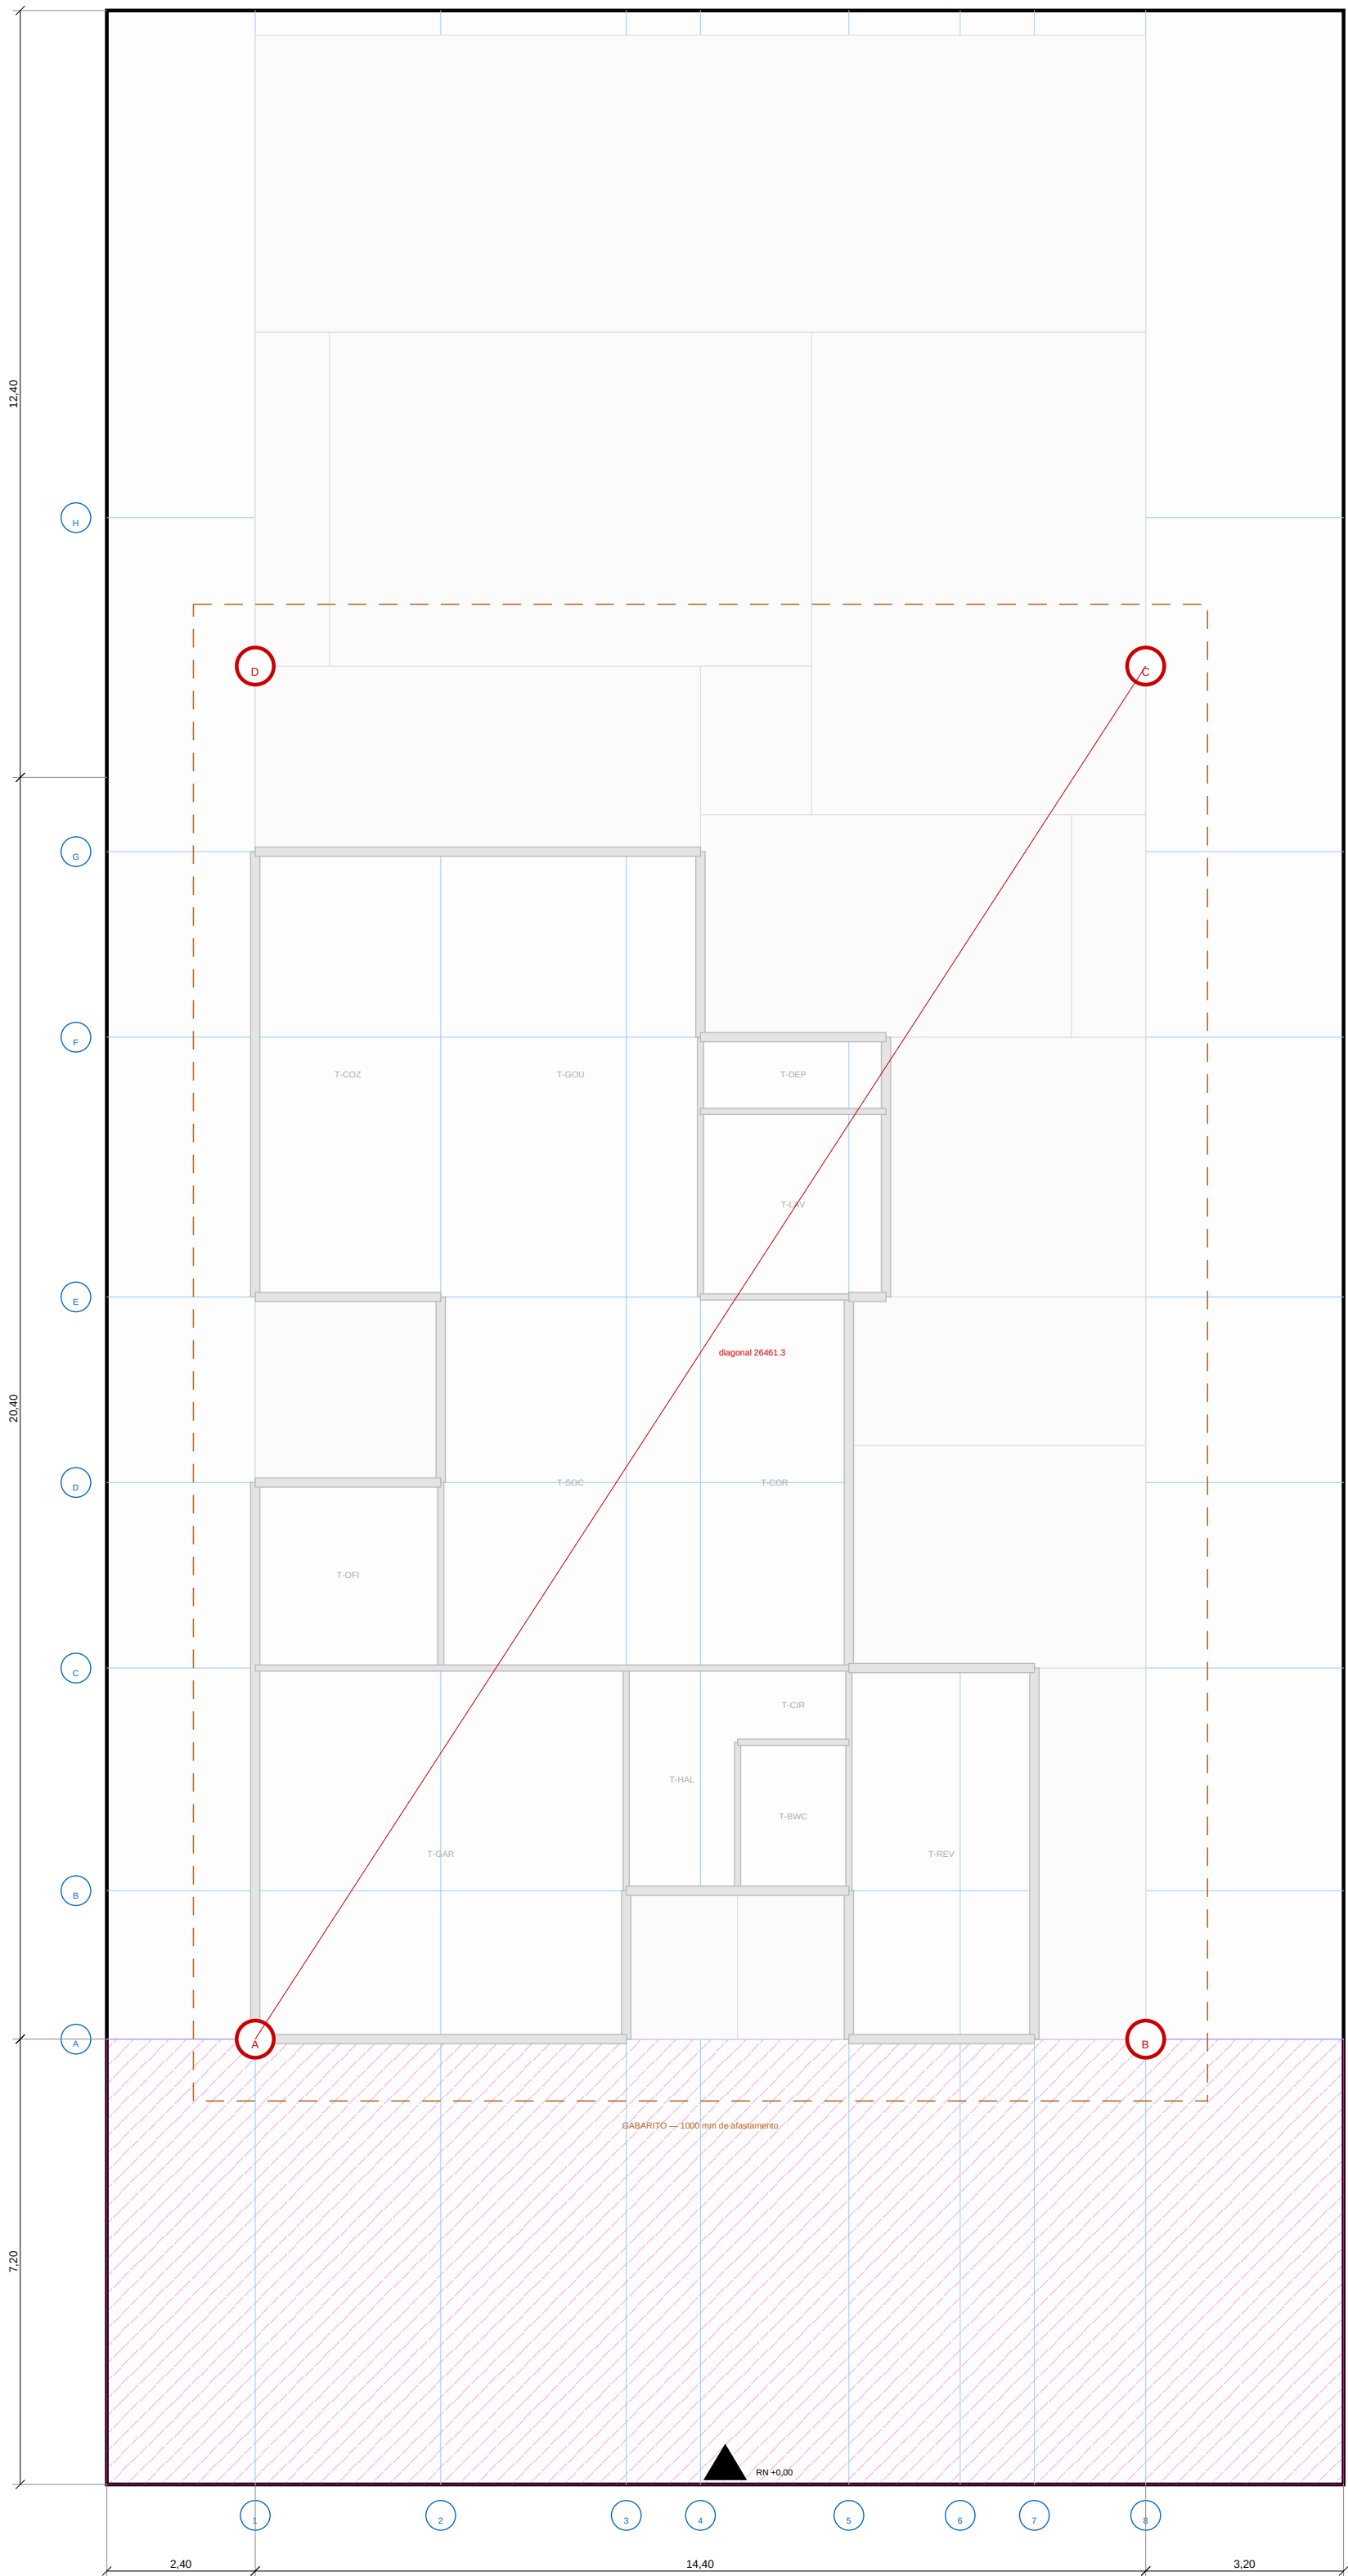


COORDENADAS DOS CANTOS (mm)

CANTO	X	Y	DIVISA SUL	DIVISA NORTE	TESTADA	QUIBO	DIAGONAL
A	2400	7200	2400	17600	7200	32800	26461,3
B	18800	7200	18800	3200	7200	32800	26461,3
C	18800	28400	18800	3200	28400	19600	26461,3
D	2400	28400	2400	17600	28400	19600	26461,3

PROCEDIMENTO DE LOCAÇÃO

#	PASSO	CRITÉRIO DE ACEITE
1	Conferir as divisas com o material de base	divergência acima de 10 mm interromper a locação
2	Instalar o RMC marca de concreto 100 x 200 x 100 mm, fora da área de obra	fora da área de obra
3	Montar o gabarito a 1000 mm do cantoneiro	perguntar 75 x 75 a tubos 20 x 100
4	Marcar os eixos X (1) a (8) e Y (A) a (H) no gabarito	linha coordenada múltipla de 200 mm
5	Cortar cabos com os OLARS diretos	verificar em cabos: erro de cabos soma
6	Conferir a diagonal A-C	26461,3 mm com tolerância de 10 mm
7	Conferir o quadrado por 3-4-5 em cada canto	antes de qualquer concretagem
8	Registrar em ata com foto e modelo	gabarito continuo nos dois lados da obra, conferência

EIXOS MODULARES

DIREÇÃO	VALORES (mm)
X (1 a 8)	2400 5400 8400 9600 12600 15600 18600
Y (A a H)	7200 9600 12600 15600 18600 21600 24600 27600
Malha	principal 600 mm - subgrid 300 mm
Origem	canto frontal esquerdo da base
Unidade	milímetros

NOTAS

- Locação é o único documento em que o erro não tem contorno tratado: a casa sai do lugar.
- Cada canto é o canto dos OLARS diretos, nunca em cabos acumulados — erro de cabos soma, erro de referência independente não.
- Conferência obrigatória pela diagonal 26461,3 mm entre A e C antes de concretar o radier.
- Ris no eixo da baseado, alinhado ao medidor TC-06, com 0,00 (+) para acabado do terreno.

PROJETO PORTO REAL

RESIDENCIA UNIFAMILIAR (MANSÃO - AM) | SOBR TATIANA-PS

PROJETO ARQUITETÔNICO

LOCAÇÃO DE OBRA E GABARITO

BASE GEOMÉTRICA Linha Consolidada Projeto (previsão) Unidade: milímetros (mm)	ESCALA 1:100 Formato A1 Malha: 600/300 (mm)	EMISSÃO ESTUDO PRELIMINAR RSO Linha Libertada para Obra Sem Arq / Pint	PROVA 31 de 35 REVISÃO
--	---	---	-------------------------------------