

- downlight embudo
- ⊕


plafon de sobrepor (forno perfurado / aparente)
- pendente (je-direito duplo)
- linear do tarefa (bancado, closet, mesa)
- arandela de espelho
- balizador de escada
- 2700 K
- 3000 K
- 4000 K
- forno absorvente perfurado (afa 0.70)
- sem forno (panel PPR aparente)

LUMINOTECNICA POR AMBIENTE — METODO DOS LUMENS

AMB	USO	h2	altura	aberto	LUMINARIA	cm	m
T-GAR	apoi	30.5	75	108	4 x Plafon LED de sobrepor 24 W	4000 K	96
T-AL	circulacao	6.5	100	151	2 x Downlight LED embudo 18 W	3000 K	36
T-ALC	varia	3.2	100	151	1 x Downlight LED embudo 18 W	2700 K	18
T-CM	circulacao	3.2	100	151	1 x Downlight LED embudo 18 W	3000 K	18
T-DEV	varia	12.7	100	200	5 x Downlight LED embudo 18 W	2700 K	90
T-CM	aberto	9.0	500	511	4 x Downlight LED embudo 18 W	4000 K	144
T-SOC	soci	25.2	200	242	8 x Downlight LED embudo 24 W	3000 K	144
T-COR	escada	12.2	100	188	2 x Pendente LED de je-direito dup	3000 K	90
T-COE	cocina	17.8	300	303	7 x Downlight LED embudo 24 W	4000 K	108
T-GOU	soci	30.2	200	208	6 x Plafon LED de sobrepor 24 W	3000 K	144
T-LAV	varia	9.0	200	245	4 x Downlight LED embudo 18 W	4000 K	72
T-DEP	varia	3.0	200	272	2 x Downlight LED embudo 18 W	4000 K	36
S-S01	varia	21.6	100	182	5 x Downlight LED embudo 18 W	2700 K	90
S-S03	varia	21.6	100	182	5 x Downlight LED embudo 18 W	2700 K	90
S-APL	circulacao	11.5	100	120	2 x Downlight LED embudo 24 W	3000 K	40
S-LOU	soci	7.2	200	300	4 x Downlight LED embudo 24 W	3000 K	96
S-MAS	varia	21.6	100	182	6 x Downlight LED embudo 18 W	2700 K	90
S-S03BANHO	banho	4.3	200	233	2 x Downlight LED embudo 18 W	3000 K	36
S-S03BANHO	banho	4.3	100	233	2 x Downlight LED embudo 18 W	3000 K	36
T-CLOSET-DEPENSA	varia	9.0	200	398	2 x Downlight LED embudo 24 W	4000 K	48
T-BEVEBANHO	banho	4.3	200	233	2 x Downlight LED embudo 18 W	3000 K	36
T-COM-LAVABO	banho	2.1	200	227	1 x Downlight LED embudo 18 W	3000 K	18
S-MASBANHO	banho	10.8	200	251	4 x Downlight LED embudo 18 W	3000 K	72
S-MAS-CLOSET	closet	9.0	200	245	4 x Downlight LED embudo 18 W	3000 K	72
S-MAS-OFFICE	office	5.4	300	512	4 x Downlight LED embudo 24 W	4000 K	96

LUZ DE TAREFA

COO	ONDE	TIPO	QTD	cm
L3-BC-01	bancada BC-01 (T-COZ)	linear	2.1 m	4000 K
L3-BC-02	bancada BC-02 (T-COZ)	linear	1.8 m	4000 K
L3-BC-03	bancada BC-03 (T-GOU)	linear	1.5 m	4000 K
L3-BC-04	bancada BC-04 (T-GOU)	linear	3.0 m	4000 K
L3-BC-05	bancada BC-05 (T-GOU)	linear	2.4 m	4000 K
L3-LC-02	espelho do banheiro LC-02 (T-COR)	arandela	1	4000 K
L3-LC-05	espelho do banheiro LC-05 (T-REV)	arandela	1	4000 K
L3-LC-06	espelho do banheiro LC-06 (S-S02)	arandela	1	4000 K
L3-LC-08	espelho do banheiro LC-08 (S-S03)	arandela	1	4000 K
L3-LC-11	espelho do banheiro LC-11 (S-MAS)	arandela	2	4000 K
L3-S-MAS-CLOSET	closet do S-MAS	linear	3.0 m	3000 K
L3-S-MAS-OFFICE	mesa do office do S-MAS	linear	1.2 m	4000 K
L3-ENCADA	escada (banheiro)	balizador	6	3000 K

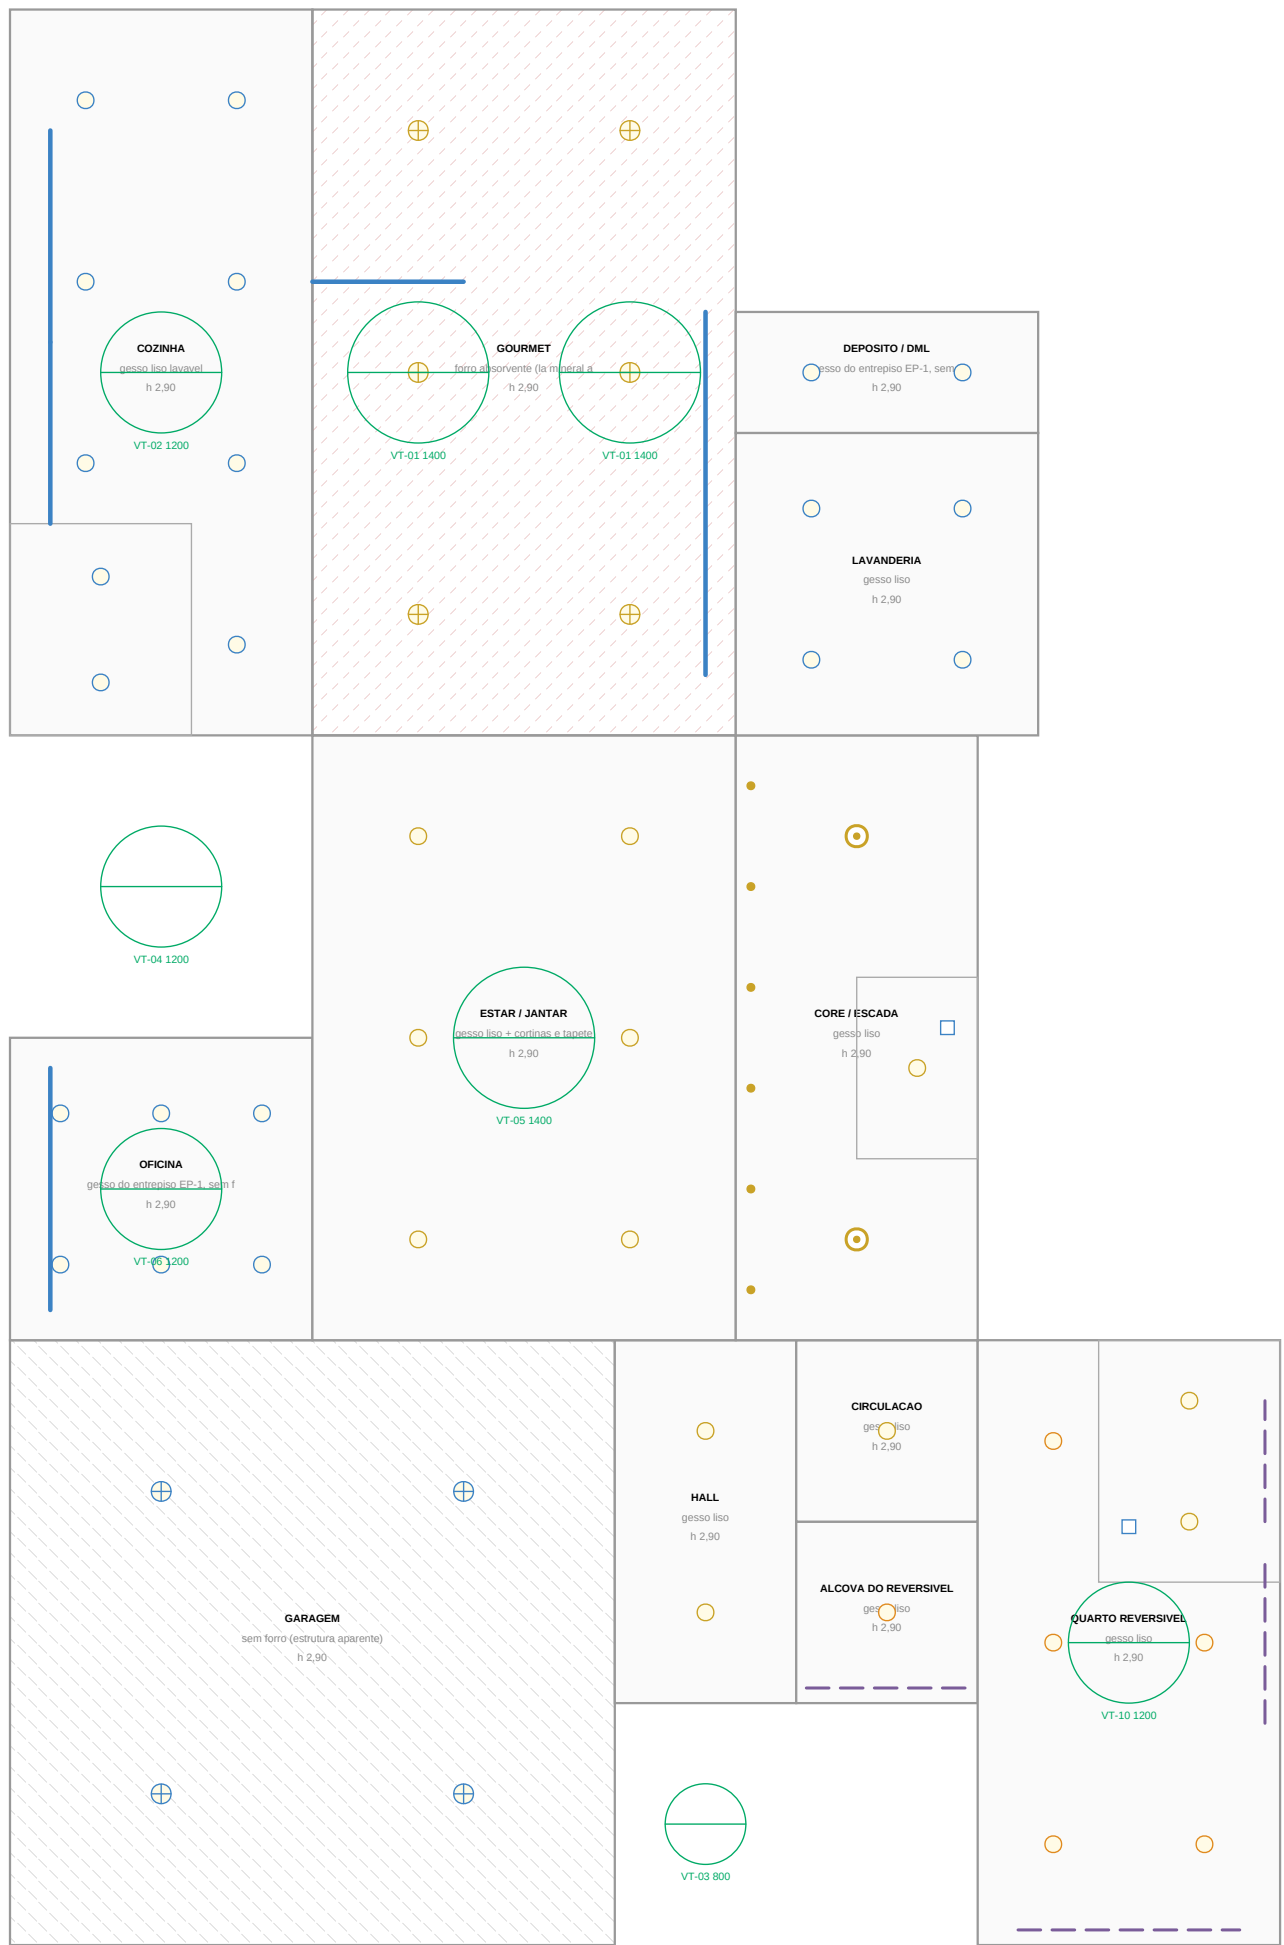

1 FORRO REFLETIDO — TERREO
ESCALA 1:75



2 FORRO REFLETIDO — SUPERIOR
ESCALA 1:75

- NOTAS
- Planta refletida: vista do forno projetada no plano horizontal, terreno e superior.
 - Luminarias pelo METODO DOS LUMENS por ambiente (NBR ISO/IEC 8955-1 / NBR 5413), medida de uniformidade SHI 1.2.
 - 18 pontos pontos, 12 pontos de tarefa, 3074 W (3.3 kWh).
 - Cor: 2.700 K interno - 3.000 K social e circulacao - 4.000 K cocina, banho e hall.
 - 11 embelezamento de teto (panel), diametro em mm.
 - Curtina (banheiro novo) instalada de 150 mm ao longo da janela de todo ambiente interno.

PROJETO PORTO REAL

RESIDENCIA UNIFAMILIAR (MANAUS - AM) | SUEZ TATIANA-PS

PROJETO ARQUITETONICO

PLANTA DE FORRO E ILUMINACAO

BASE GEOMETRICA	ESCALA	EMISSAO	PROJEC
União Consolidada	1:75	ESTUDO PRELIMINAR R75	
em R75 (previsão)	FORMATO A1	WAO LIBERADO PARA OBRA	16
UNIDADE MESTRE: AM	MALHA 600/600/600	SEM ART / RNT	06-09-REV-075