
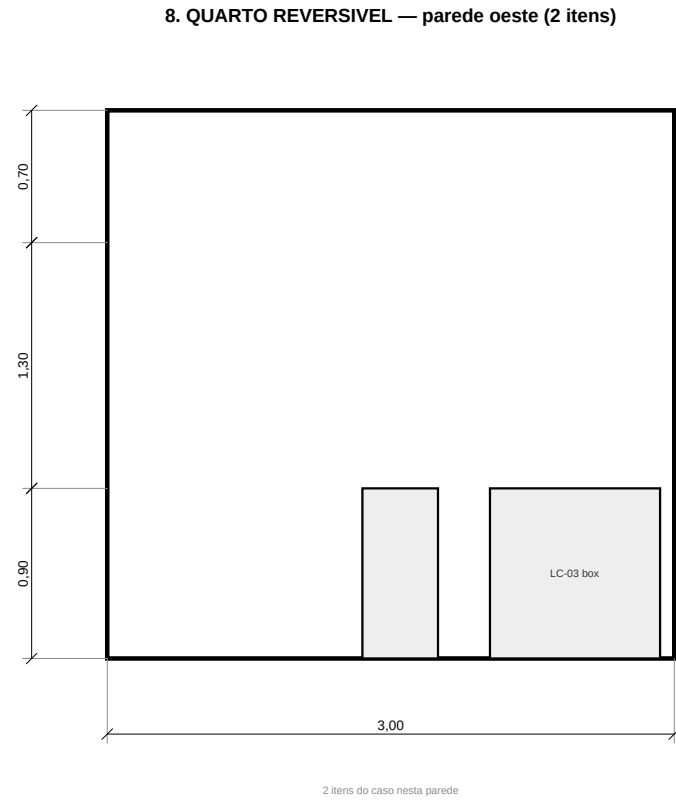
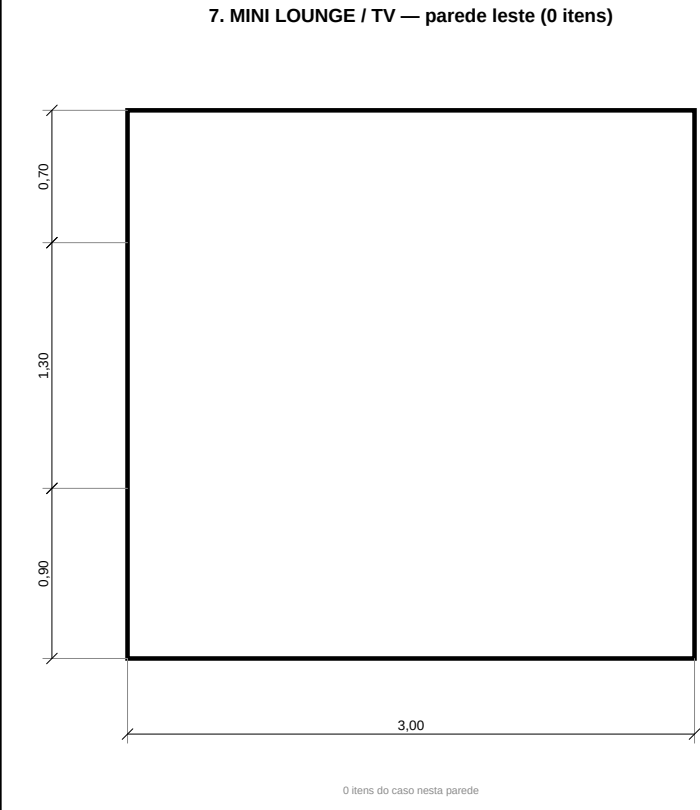
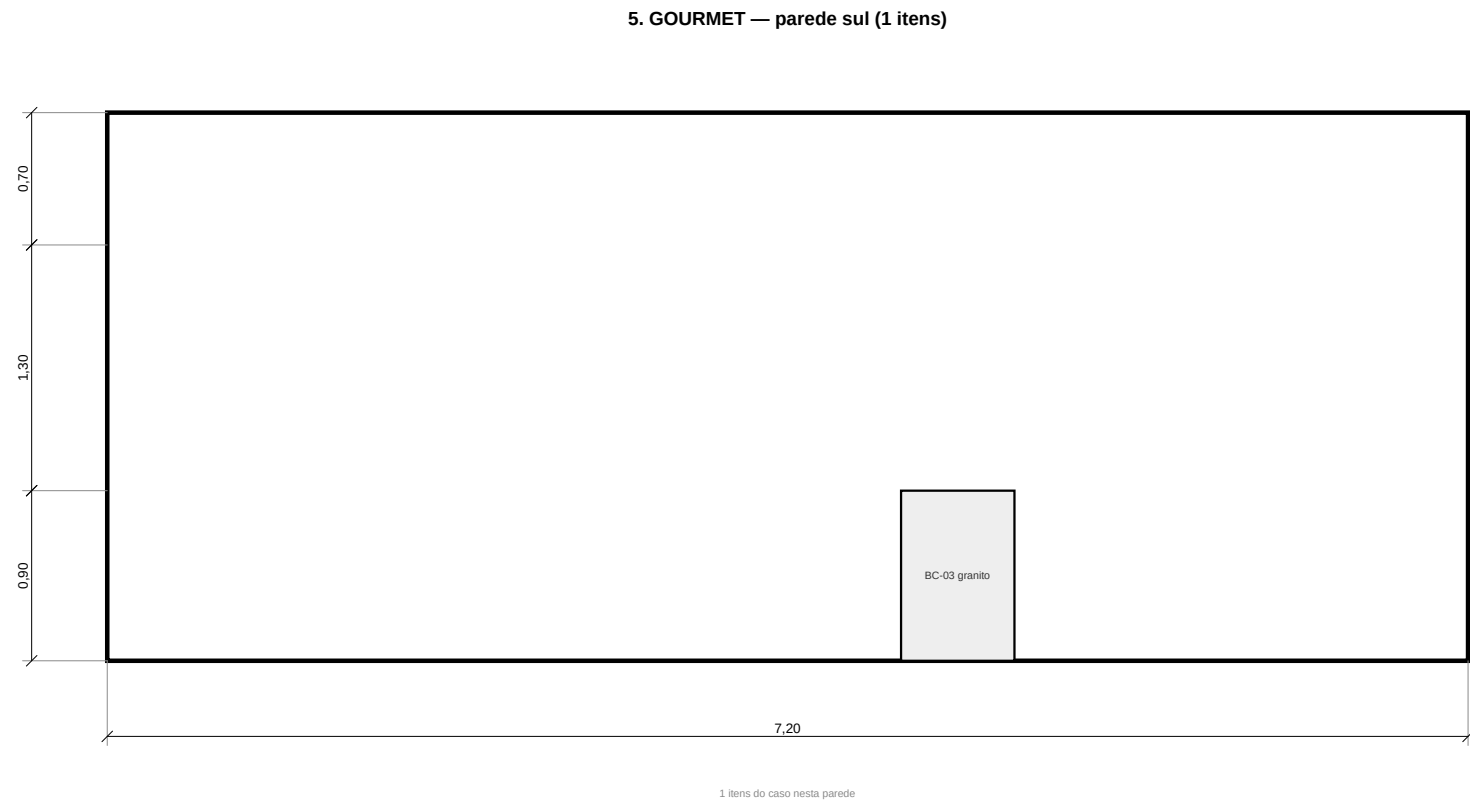


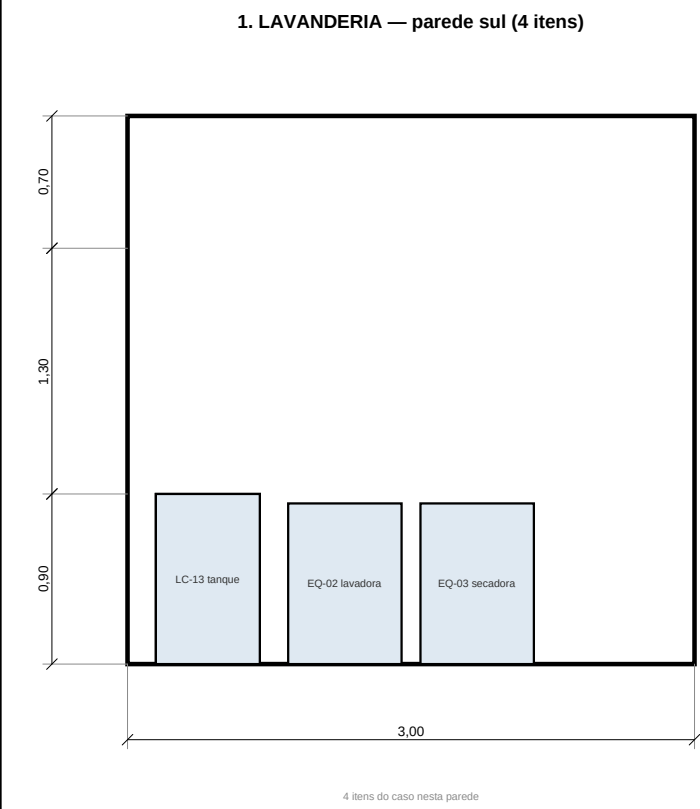

NOTAS

- Cada item desenvolvido vem de ARMARIOS, BANCADAS, LOCAIS, EQUIPAMENTOS ou LAYOUT do caso, pelo código, nenhum modular foi digitado nesta planilha.
- Um item está na parede quando encosta nela a menos de 200 mm. Abaixo por família (P).
- Janelas e portas da parede vem de VAOCL, com perfil e altura da esquadra.
- Complementos a P01-10 (piscina, gourmet, bar, banheiro master, oficina, lavanderia).

PROJETO PORTO REAL

RESIDENCIA UNIFAMILIAR (MARAU) - AM | SUITE TATIANA-PS

PROJETO ARQUITETONICO

ELEVACOES INTERNAS II — DERIVADAS DO MODELO

BASE GEOMETRICA	ESCALA	EMISSAO	PROJECION
União Consolidada	1:40	ESTUDO PRELIMINAR R7S	51
Projeto (previsão)	FORMATO A1	MAO LIBERADO PARA ORCA	SEM ART / INT
UNIDADE METRICA: mm	MAQUA: 600/500/300	SEM ART / INT	60 60 REV R7S