




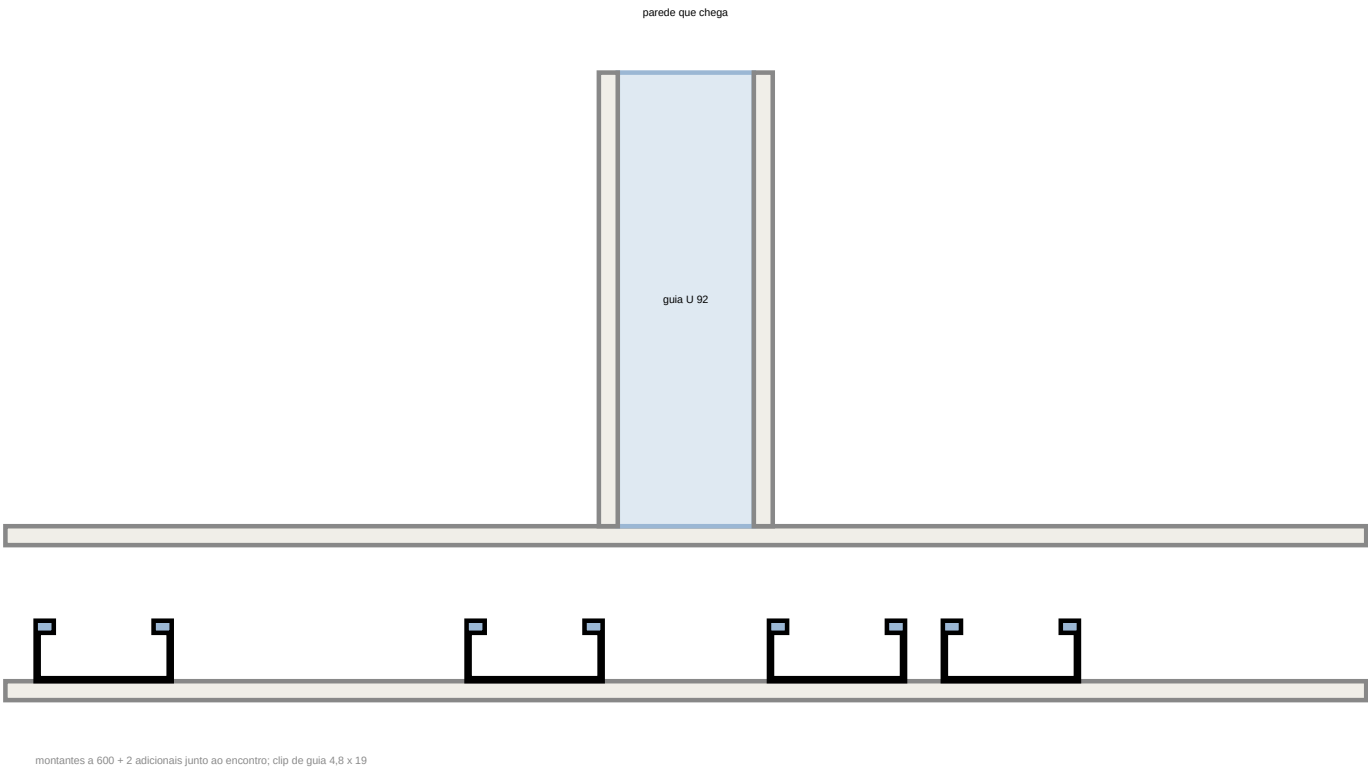


A ENCONTRO EM T — PLANTA
ESCALA 1:5

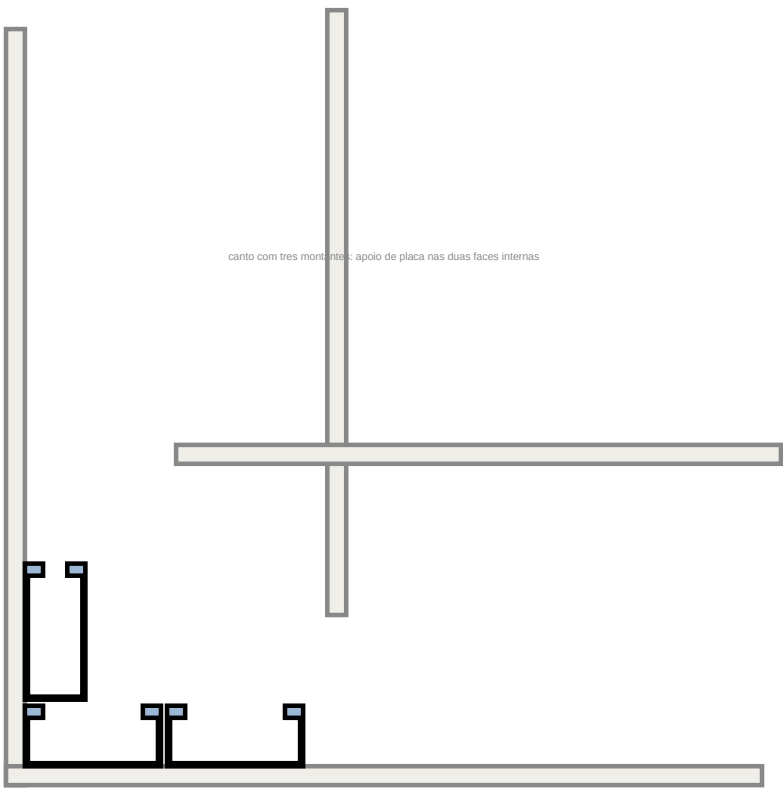


B CANTO EM L — PLANTA
ESCALA 1:5

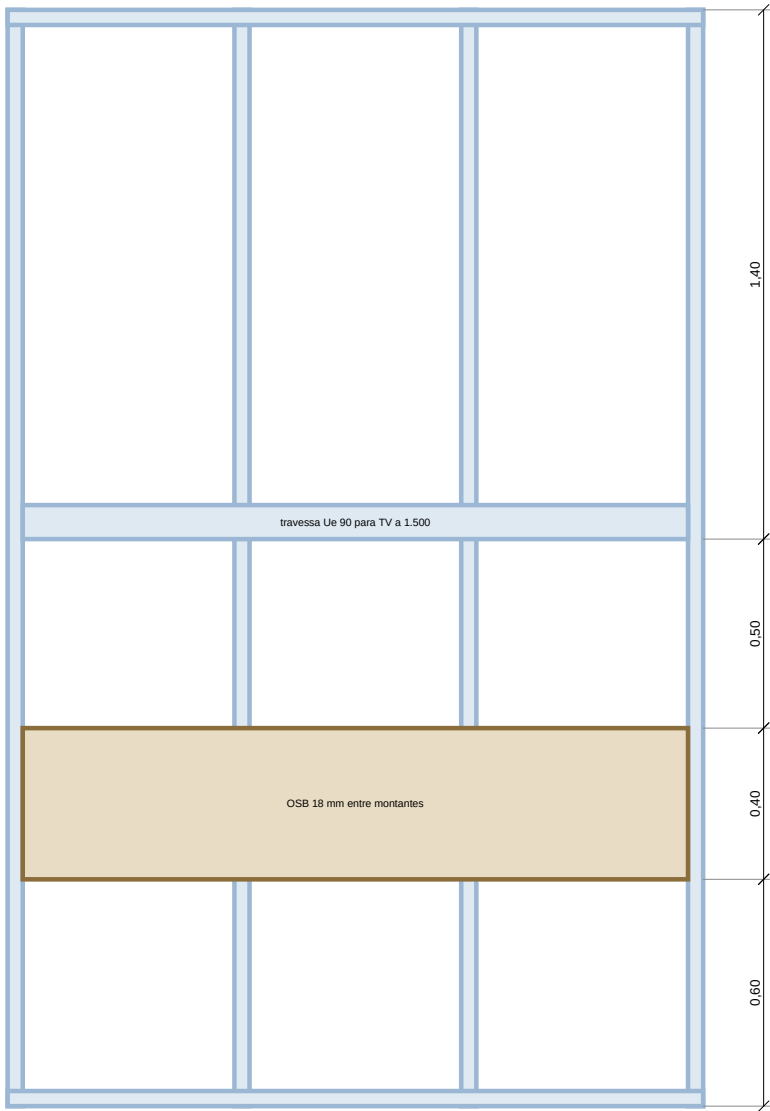

C REFORÇO PARA CARGA SUSPensa — ELEVACAO DA PAREDE
ESCALA 1:20

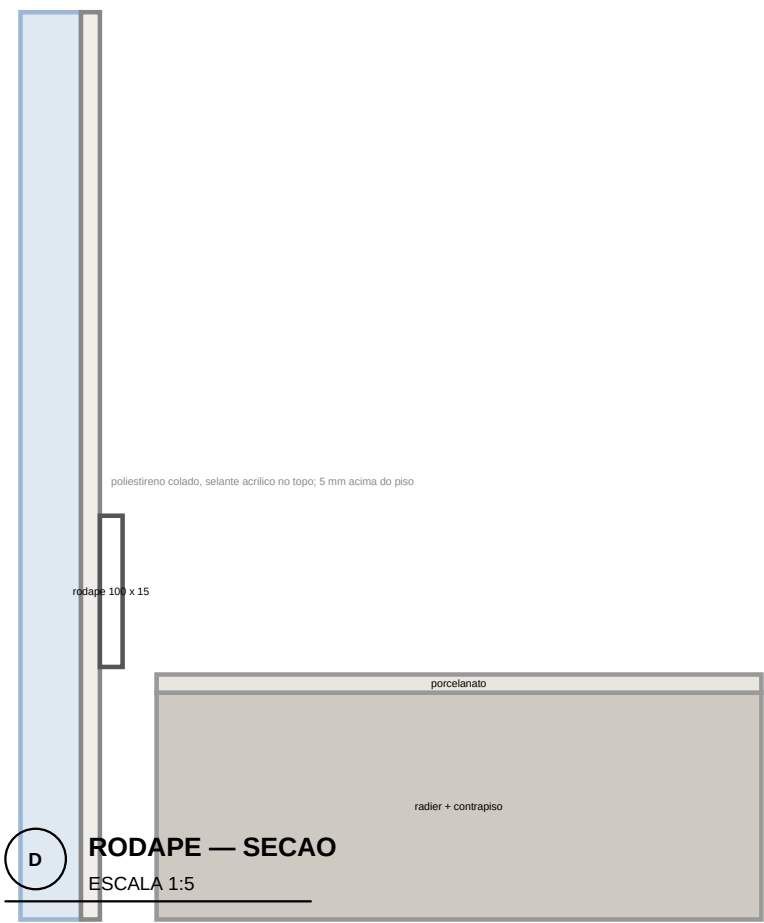

D RODAPE — SECAO
ESCALA 1:5

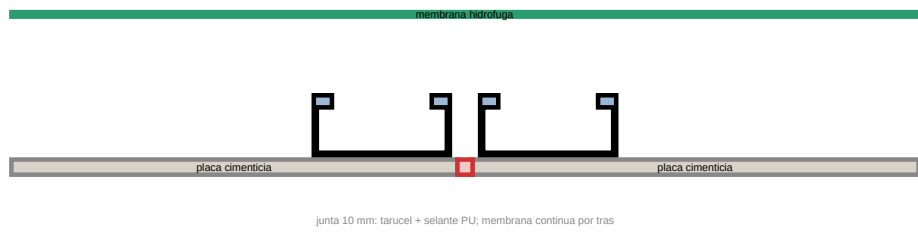

E JUNTA DE MOVIMENTACAO DE FACHADA — PLANTA (montante duplo)
ESCALA 1:5

CARGAS SUSPENSAS — ONDE E QUANTO

ITEM	Qtd	PARADA	Nº	PARADA	7 mm	MONI	Qtd/m²
LC-05-G	1.000	gabinete banho	90	V em 13000	600 13000	3	0.24
LC-05-G	1.000	gabinete banho	90	V em 13000	600 13000	3	0.28
LC-06-G	1.000	gabinete banho	90	H em 13000	600 13000	3	0.28
LC-06-G	1.000	gabinete banho	90	H em 13000	600 13000	3	0.28
LC-11-G	1.000	gabinete banho	90	H em 22000	600 13000	5	0.72
LV-03-P	1.000	panel tv	70	H em 13000	900 13000	5	2.52
LV-03-C	1.000	cabineira	25	V em 13000	300 13000	5	2.84
LV-03-C	1.000	cabineira	25	V em 17000	300 13000	5	2.84
LV-03-C	1.000	cabineira	25	V em 17000	300 13000	5	2.84
LV-03-C	1.000	cabineira	25	H em 22000	300 13000	5	3.54
LV-03-M	1.000	panel tv	70	H em 22000	900 13000	5	2.7
LV-03	1.000	tv	35	H em 13000	900 13000	4	0.96
LV-03	1.000	tv	35	H em 22000	900 13000	4	0.96

ENCONTROS EM T — 12

PRV	x	y	CONTINUA	EXTERNA
T	8400	13000	H	rua
T	8400	13000	H	rua
T	10000	8600	H	rua
T	2400	13000	V	rua
T	9000	22000	V	rua
S	12000	22000	V	rua
S	12000	18000	H	rua
S	13000	16000	H	rua
S	2400	18000	V	rua
S	7800	18000	V	rua
S	7800	10000	V	rua
S	12000	13000	V	rua

NOTAS

- Encontro em T: 12 na casa, derivado das paredes (junta de uma parede dentro de outra). Detalhe unico: montante adicional na parede continua, cda de gla. 4 parafusos 4.8 x 15 por metro.
- Carga suspensa: 12 barra (galvanizado de banho, painéis de TV, cabineiras e os dois TVs) localizados na parede que os recebe, refência de CSB 10 mm entre montantes na faixa de altura do item, 13.0 m2. Paredes de LSF não seguem banho, seguem montante e refência.
- Perfilado: perfil de polietileno 300 x 15 sobre a placa, 5 mm acima do piso, selado, nos montantes, o próprio perfilado recortado (acabamento).
- Junta de movimentação de fachada: 20 (a cada 6 m e em cada canto), 10 mm com polietileno com barreira sobre montante duplo, placas não passam pela junta.

PROJETO PORTO REAL

RESIDENCIA UNIFAMILIAR (MANSÃO - AM) | SOUS TATIANA-PS

PROJETO ARQUITETONICO

DETALHES DO LSF — ENCONTROS, CARGA SUSPensa, RODAPE E JUNTA DE FACHADA

BASE GEOMETRICA	ESCALA	EMISSAO	PROJECION
União Consolidada	1:5 • 1:20	ESTUDIO PRELIMINAR R75	68
PRV R75 (previsão)	FORMATO A1	NAO LIBERADO PARA OBRA	SEM ART / RNT
UNIDADE METRICA: mm	MAQUA: 600/500/300	SEM ART / RNT	68 REV 075