


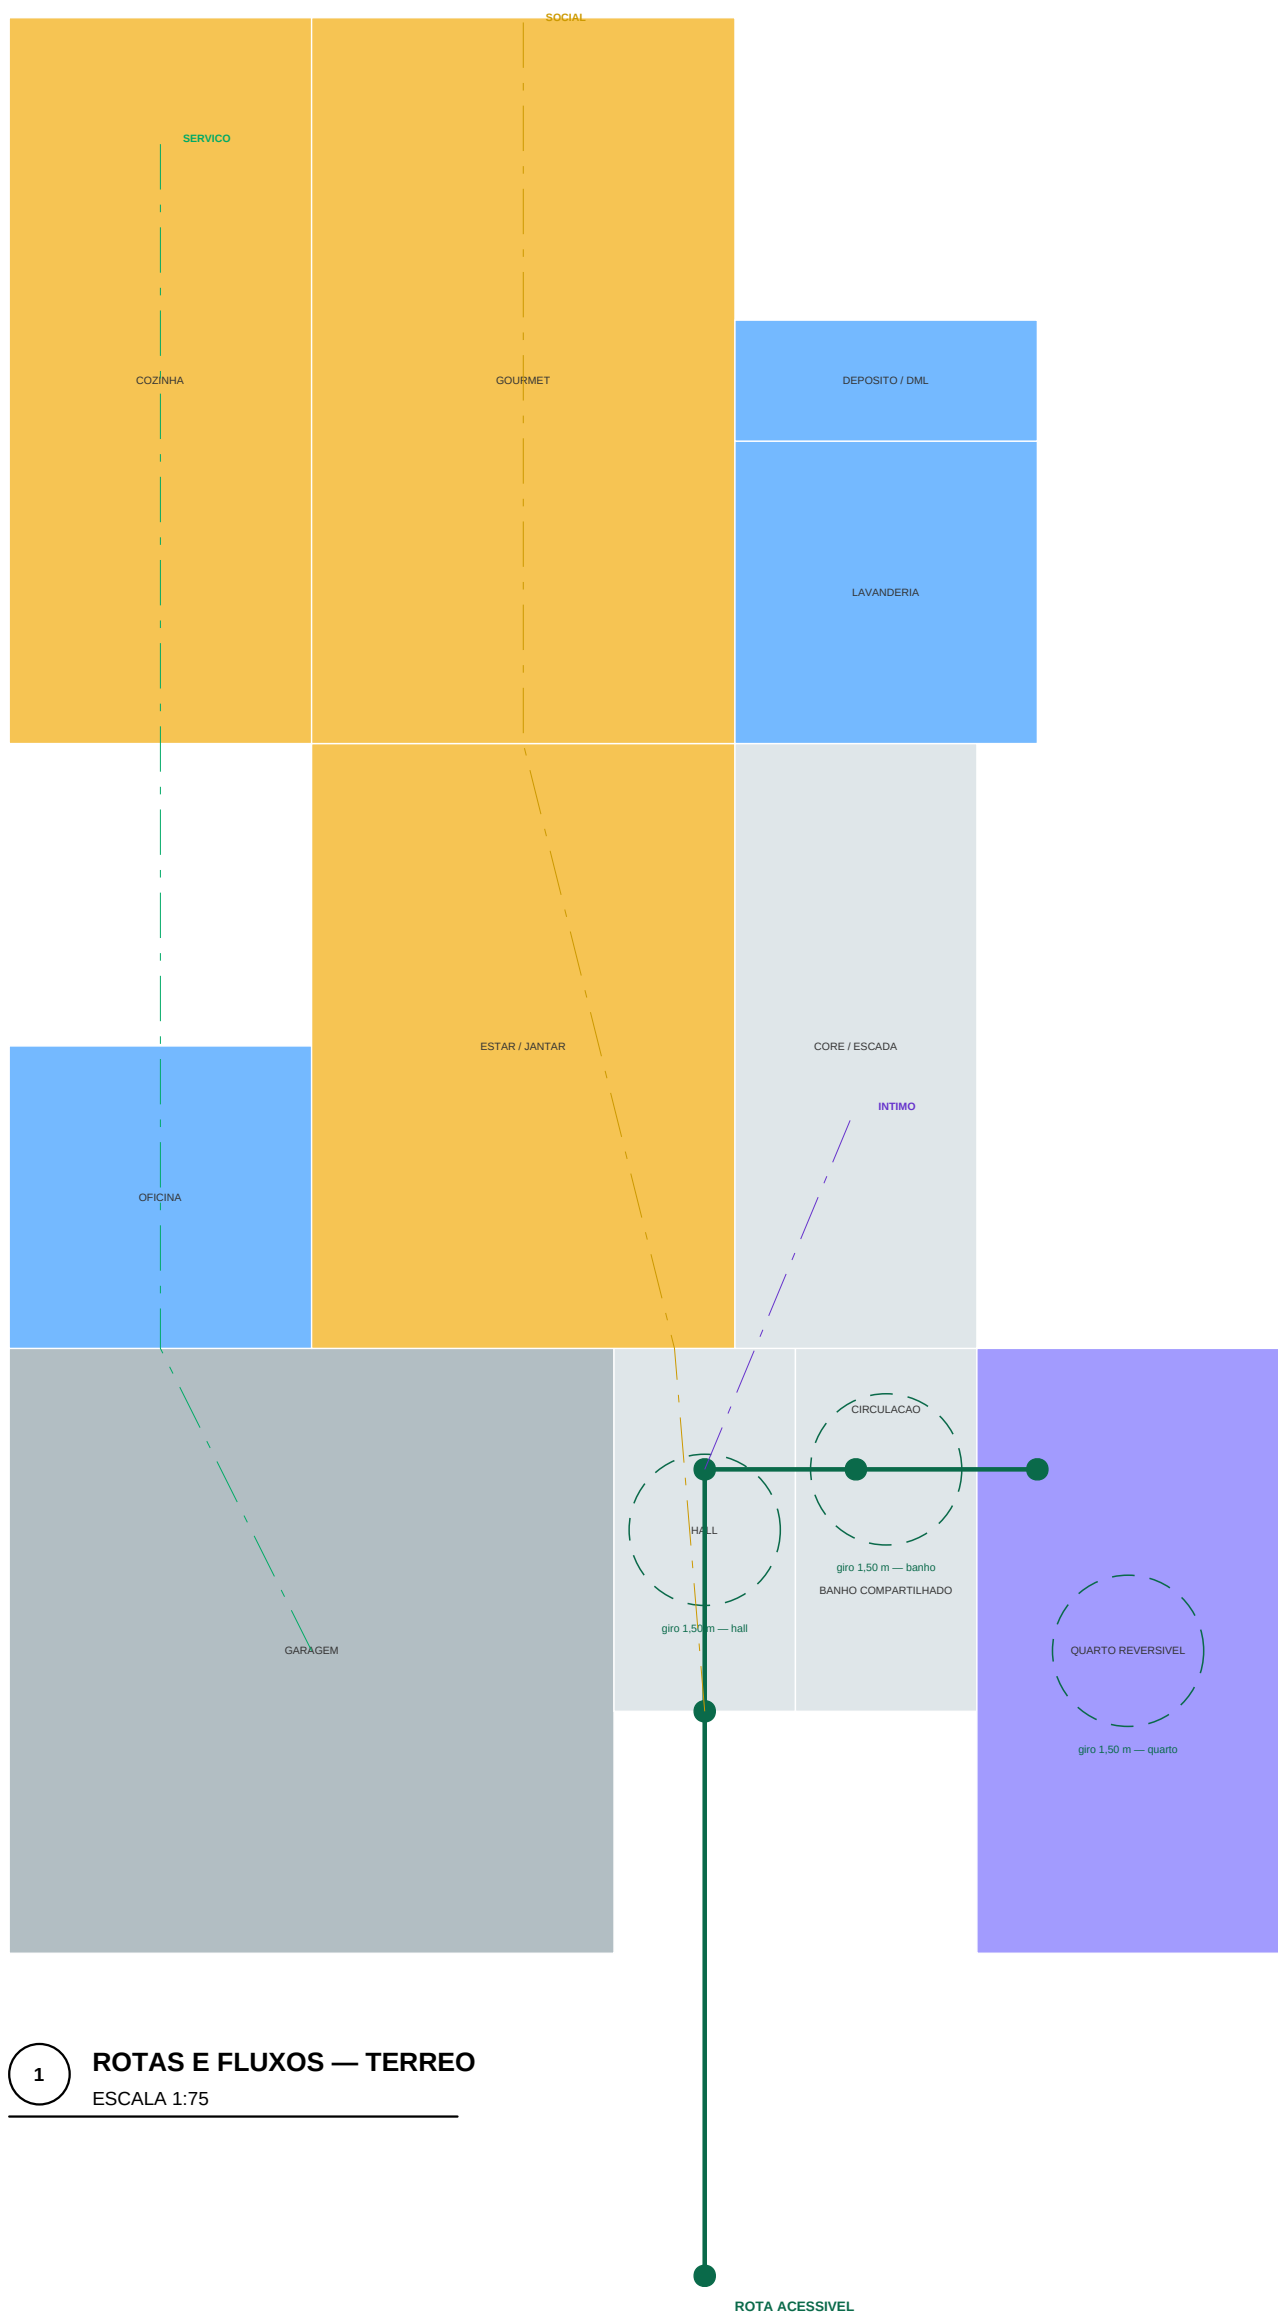


1 ROTAS E FLUXOS — TERREO
ESCALA 1:75

VERIFICACAO NBR 9050

ITEM	EXISTENTE	PROJETO	
Visão livre de porta	800 mm	940 mm (altura de 900)	OK
Circuito de giro 360 graus	1.500 mm	hall, banheiro e quarto	OK
Desnível sem rampas	até 5 mm	soluções niveladas	OK
Largura de circulação	900 mm	1.800 mm no hall	OK
Barras de apoio	relívios prévios	instalação no P1 e P10.1	OK
Barras de acesso	altura livre 750 mm	sem barreiras até a altura	OK
Corredor e interruptor	600 a 1.000 mm	a definir no relatório	pendente

FLUXOS — SEPARACAO DE CIRCUITOS

CIRCUITO	PERCURSO	CRUZAR O SOCIAL?
Serviço	garagem → oficina → lavanderia → cozinha → despensa	NÃO
Social	entrada → hall → estar → gourmet → alameda → piscina	—
Quarto reservado	hall → quarto compartilhado → quarto reservado	NÃO
Quarto superior	hall → corredor → hall superior → suíte	NÃO
Quarto e garagem	cozinha → despensa → reservado	NÃO

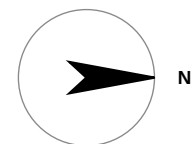

- NOTAS
- * Rota acessível do passeio ao quarto reservado e ao banheiro compartilhado.
 - * Circuito de giro de 1.500 mm verificado nos pontos de manobra.
 - * Porta de correr de 900 mm no banheiro libera a área de manobra.
 - * Relações para barras de apoio estabelecidas antes do fechamento das portas.

PROJETO PORTO REAL

RESIDENCIA UNIFAMILIAR (MANAUS - AM) | SUELE TATIANA-PS

PROJETO ARQUITETONICO

ACESSIBILIDADE E FLUXOS

BASE GEOMETRICA Linha Consolidada ISO 9122 (previsão) UNIDADE: METROS - MM	ESCALA 1:75 FORMATO A1 MILIMETROS (50/100/200)	EMISSAO ESTUDO PRELIMINAR R09 NÃO LIBERADO PARA OBRA SEM ART / RNT	PROJETO 17 06.05.2024
---	---	---	-----------------------------