


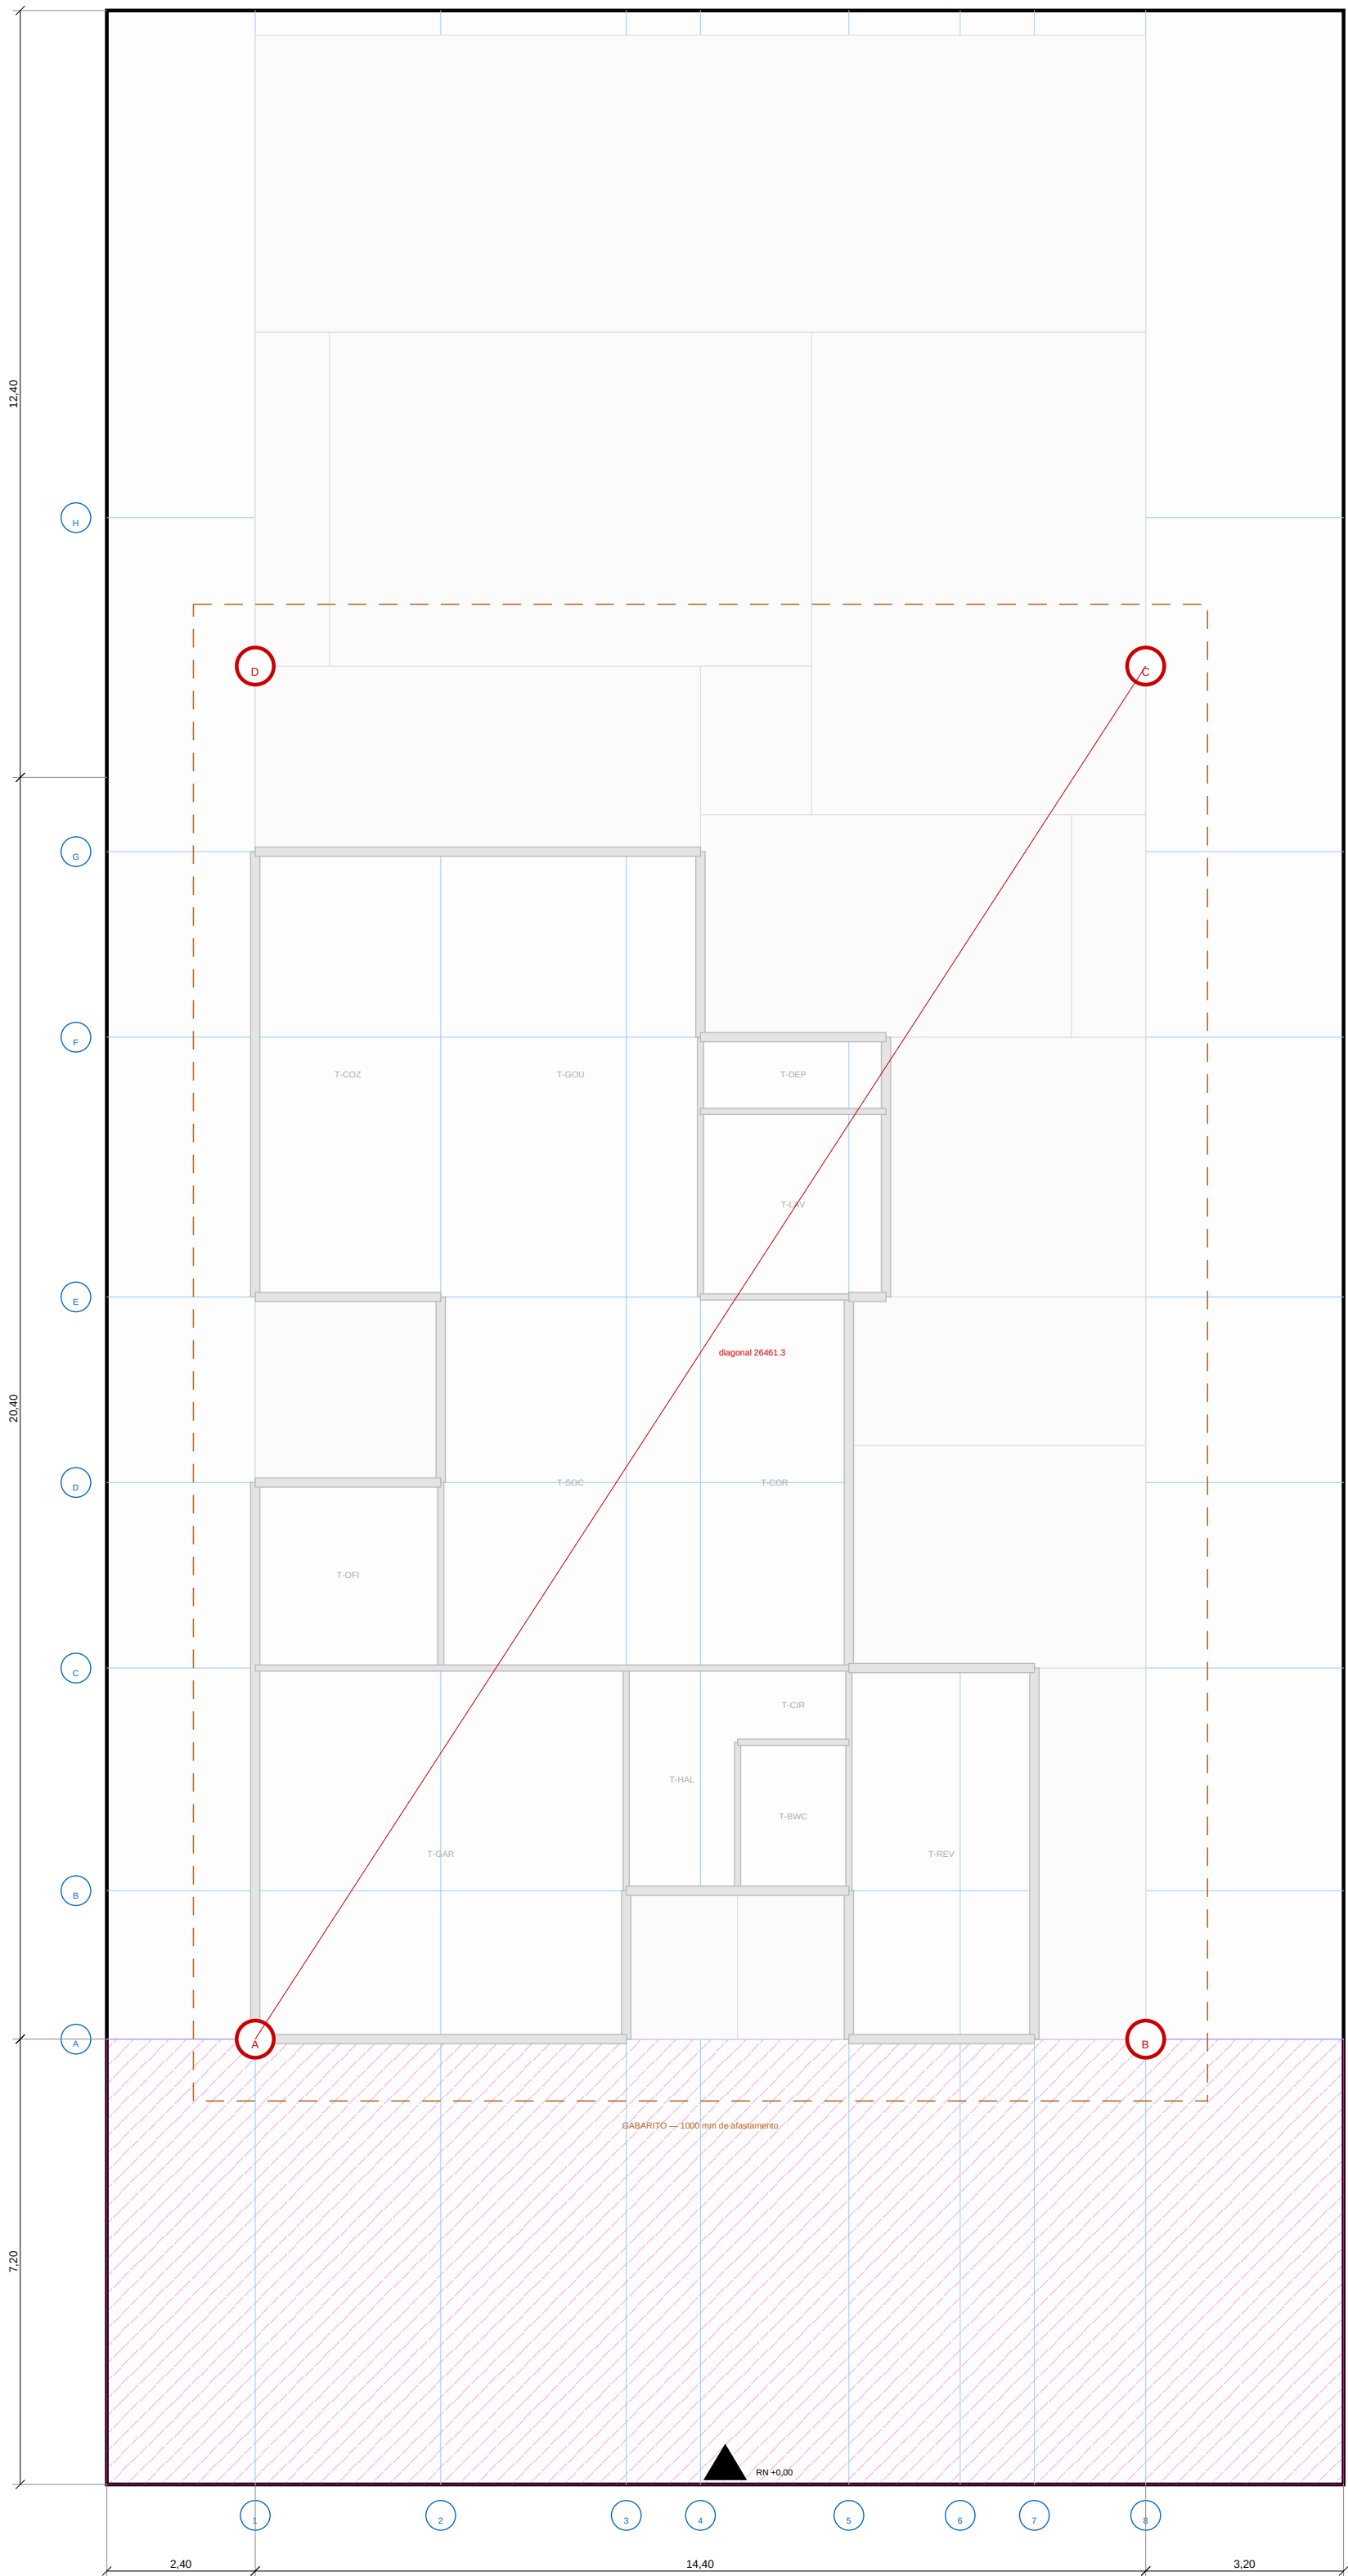

COORDENADAS DOS CANTOS (mm)

CANTO	X	Y	DIVISA SUL	DIVISA NORTE	TESTADA	QUIBO	DIAGONAL
A	2400	7200	2400	17600	7200	32800	26461,3
B	18800	7200	18800	3200	7200	32800	26461,3
C	18800	28400	18800	3200	28400	19600	26461,3
D	2400	28400	2400	17600	28400	19600	26461,3

PROCEDIMENTO DE LOCACAO

#	PASSO	CRITERIO DE ACERTO
1	Conferir as divisas com o matriculo e o memorial da obra	divergencia acima de 50 mm interrompe a locacao
2	Implantar o PNM: marcos de concreto 200 x 200 x 100 mm, fora da area da obra	fora da area da obra
3	Montar o gabarito a 1000 mm do cantoneiro	perpendicular 75 x 75 a toluda 20 x 100
4	Marcar os eixos X (L) e Y (L) e Y (L) a 10 m no gabarito	linha coordenada mltipla de 200 mm
5	Colar cado canto dos QUADs divulas	verifica em cadois: erro de cadois soma
6	Conferir a diagonal A-C	26461,3 mm com tolerancia de 20 mm
7	Conferir o quadrado por 3-4-5 em cada canto	antes de qualquer concretagem
8	Registrar em ata com foto e modelo	gabarito continuo nos dois lados da obra, conferenci

EIXOS MODULARES

DIRECAO	POSICAO (mm)
X (L) e Y (L)	2400 - 5400 - 8400 - 9600 - 12200 - 12800 - 15800 - 16800
Y (L) e X (L)	7200 - 9600 - 13200 - 14200 - 15200 - 18400 - 28400 - 32800
Matia	principal 800 mm - subgalo 300 mm
Origen	canto frontal esquerdo da obra
Unidade	milimetros

NOTAS

- Locacao e o unico desvio em que o erro nao tem consequncia fatal: o caso de erro de lugar.
- Cada canto e cadois dos QUADs divulas, nunca em cadois acumuladas — erro de cadois soma, erro de referencia independente nao.
- Conferencia obrigatoria pela diagonal 26461,3 mm entre A e C antes de concretar o mado.
- Nao se deve de brado, alinhado ao medidor TC-06, com 0,001 m por acabado do terreno.

PROJETO PORTO REAL

RESIDENCIA UNIFAMILIAR (MANSO) - AM | SOUS TATIANA-PS

PROJETO ARQUITETONICO

LOCACAO DE OBRA E GABARITO

BASE GEOMETRICA Linha Consolidada Projeto (previsao) Unidade: metro, mm	ESCALA 1:100 Formato A1 MILHA 405/500/500	EMISSAO ESTUDO PRELIMINAR R09 Nao liberado para obra SEM ART / RNT	PROJETA 31 06-25 REV 042
--	---	---	---------------------------------------