
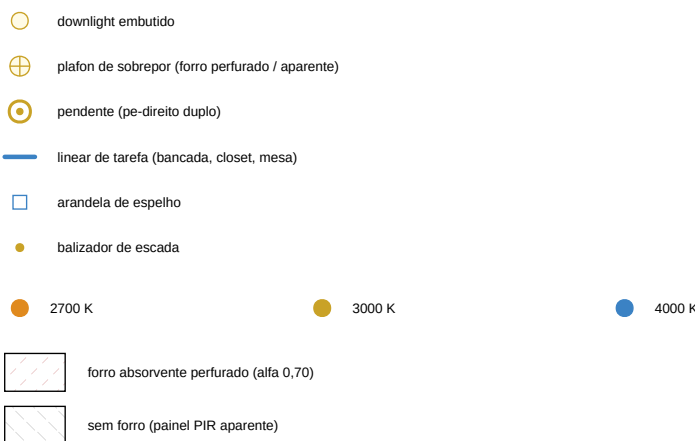


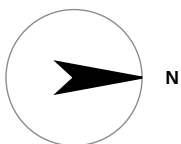

LUMINOTECNICA POR AMBIENTE — METODO DOS LUMENS


AMB	USO	h2	altura	aberto	LUMINARIA	cm	m
T-GAR	apoi	30.5	75	108	4 x Plafon LED de sobrepor 24 W	4000 K	96
T-AL	circulacao	6.5	100	151	2 x Downlight LED embudo 18 W	3000 K	36
T-ALC	varia	3.2	150	151	1 x Downlight LED embudo 18 W	2700 K	18
T-CM	circulacao	3.2	100	151	1 x Downlight LED embudo 18 W	3000 K	18
T-DEV	varia	12.7	150	200	5 x Downlight LED embudo 18 W	2700 K	90
T-CM	aberto	9.9	500	511	4 x Downlight LED embudo 18 W	4000 K	144
T-SOC	social	25.2	200	242	8 x Downlight LED embudo 24 W	3000 K	144
T-COR	escada	12.2	150	188	2 x Pendente LED de pe-direito dup	3000 K	90
T-COE	cocina	17.8	300	303	7 x Downlight LED embudo 24 W	4000 K	168
T-GOU	social	30.2	200	208	6 x Plafon LED de sobrepor 24 W	3000 K	144
T-LAV	servico	9.0	200	245	4 x Downlight LED embudo 18 W	4000 K	72
T-DEP	servico	3.0	200	272	2 x Downlight LED embudo 18 W	4000 K	36
S-S01	varia	21.6	150	182	5 x Downlight LED embudo 18 W	2700 K	90
S-S03	varia	21.6	150	182	5 x Downlight LED embudo 18 W	2700 K	90
S-APL	circulacao	11.5	100	120	2 x Downlight LED embudo 24 W	3000 K	40
S-LOU	social	7.2	200	300	4 x Downlight LED embudo 24 W	3000 K	96
S-MAS	varia	21.6	150	182	6 x Downlight LED embudo 18 W	2700 K	90
S-S03BANHO	banho	4.3	200	233	2 x Downlight LED embudo 18 W	3000 K	36
S-S03BANHO	banho	4.3	100	233	2 x Downlight LED embudo 18 W	3000 K	36
T-COULEIROPENSA	servico	9.9	200	398	2 x Downlight LED embudo 24 W	4000 K	48
T-BEUSBANHO	banho	4.3	200	233	2 x Downlight LED embudo 18 W	3000 K	36
T-CORRELAUNDO	banho	2.1	200	227	1 x Downlight LED embudo 18 W	3000 K	18
S-MASBANHO	banho	10.8	200	251	4 x Downlight LED embudo 18 W	3000 K	72
S-MASLOBBET	closet	9.0	200	245	4 x Downlight LED embudo 18 W	3000 K	72
S-MASLOBBET	office	5.4	300	512	4 x Downlight LED embudo 24 W	4000 K	96

LUZ DE TAREFA

COO	ONDE	TIPO	QTD	cm
L3-BC-01	bancada BC-01 (T-COZ)	linear	2.1 m	4000 K
L3-BC-02	bancada BC-02 (T-COZ)	linear	1.8 m	4000 K
L3-BC-03	bancada BC-03 (T-GOU)	linear	1.5 m	4000 K
L3-BC-04	bancada BC-04 (T-GOU)	linear	3.0 m	4000 K
L3-BC-05	bancada BC-05 (T-GOU)	linear	2.4 m	4000 K
L3-LC-02	espelho do banheiro LC-02 (T-COR)	arandela	1	4000 K
L3-LC-05	espelho do banheiro LC-05 (T-REV)	arandela	1	4000 K
L3-LC-06	espelho do banheiro LC-06 (S-S02)	arandela	1	4000 K
L3-LC-08	espelho do banheiro LC-08 (S-S03)	arandela	1	4000 K
L3-LC-11	espelho do banheiro LC-11 (S-MAS)	arandela	2	4000 K
L3-BANHO-CLOBBET	closet do S-MAS	linear	3.0 m	3000 K
L3-S-MAS-OFFICE	mesa do office do S-MAS	linear	1.2 m	4000 K
L3-ENCADIA	escada (Balcão/Vara)	balizadora	6	3000 K



1 FORRO REFLETIDO — TERREO
ESCALA 1:75

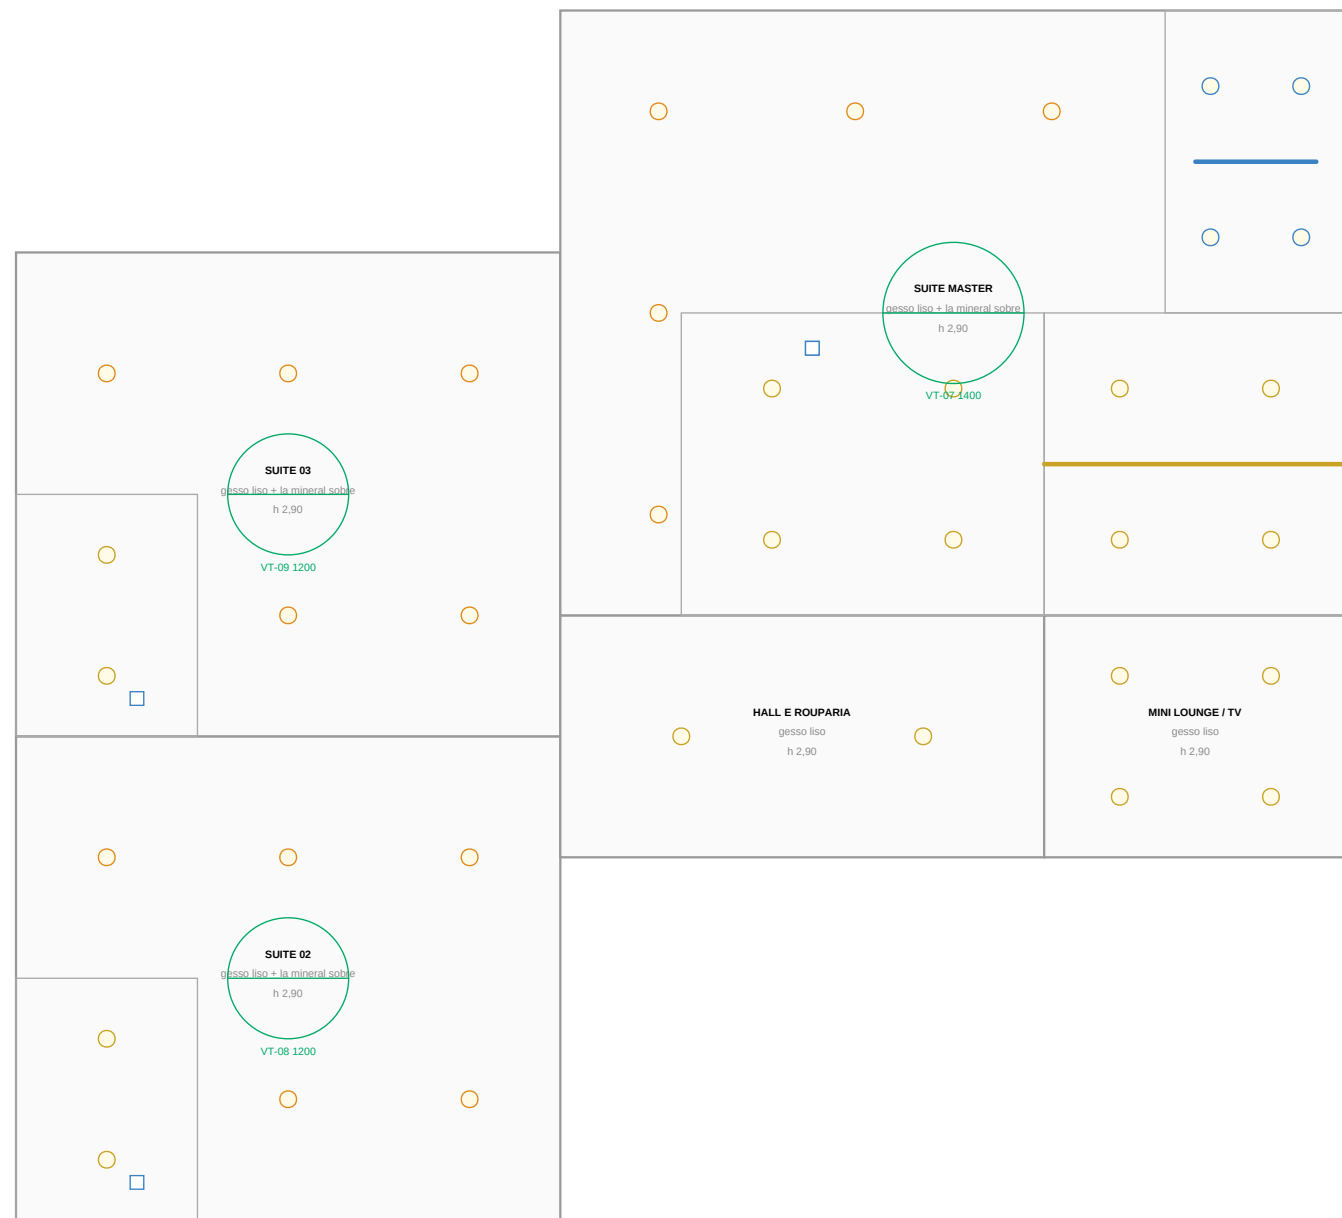

2 FORRO REFLETIDO — SUPERIOR
ESCALA 1:75

NOTAS

- Planta refletida, vista do forro projetada no plano horizontal, terreno e superior.
- Luminarias pelo METODO DOS LUMENS por ambiente (NBR ISO/IEC 8955-1 / NBR 5413), malha de uniformidade SHL 1.2.
- 18 pontos gerais, 12 pontos de tarefa, 3714 W (3.3 kW).
- Cor: 2.700 K interno - 3.000 K social e circulacao - 4.000 K cozinha, banheiro e trabalho.
- 11 unidades de teto (painel), diâmetro 400 mm.

PROJETO PORTO REAL

RESIDENCIA UNIFAMILIAR (MARAU - AM) | SUEZ TATIANA-PS

PROJETO ARQUITETONICO

PLANTA DE FORRO E ILUMINACAO

BASE GEOMETRICA União Consolidada Projeto (previsão) Unidade: METRO - MM	ESCALA 1:75 FORMATO A1 MILIMETROS (50/50/50)	EMISSAO ESTUDO PRELIMINAR R07 LIMITE LIBERADO PARA OBRA SEM ART / RNT	PROJECION 16 06-48 REV R07
---	--	---	---