




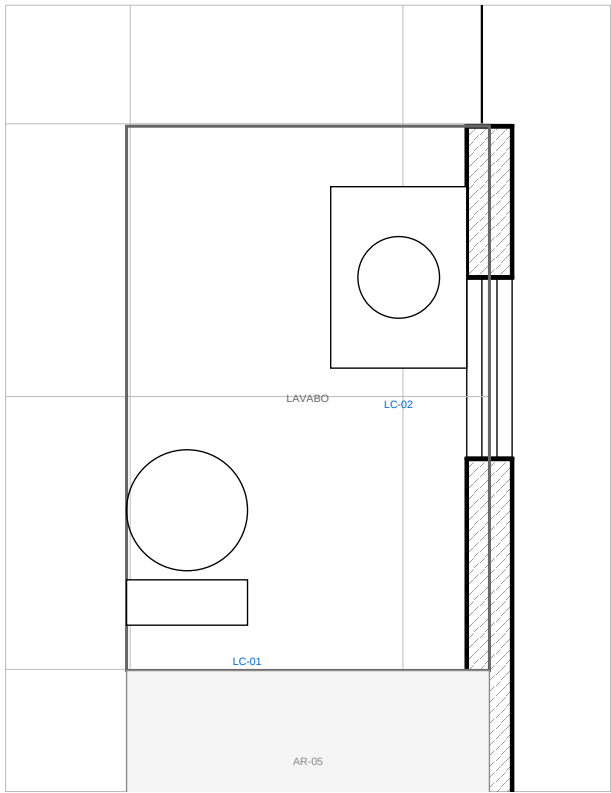


1 LAVABO SOB A ESCADA
ESCALA 1:25

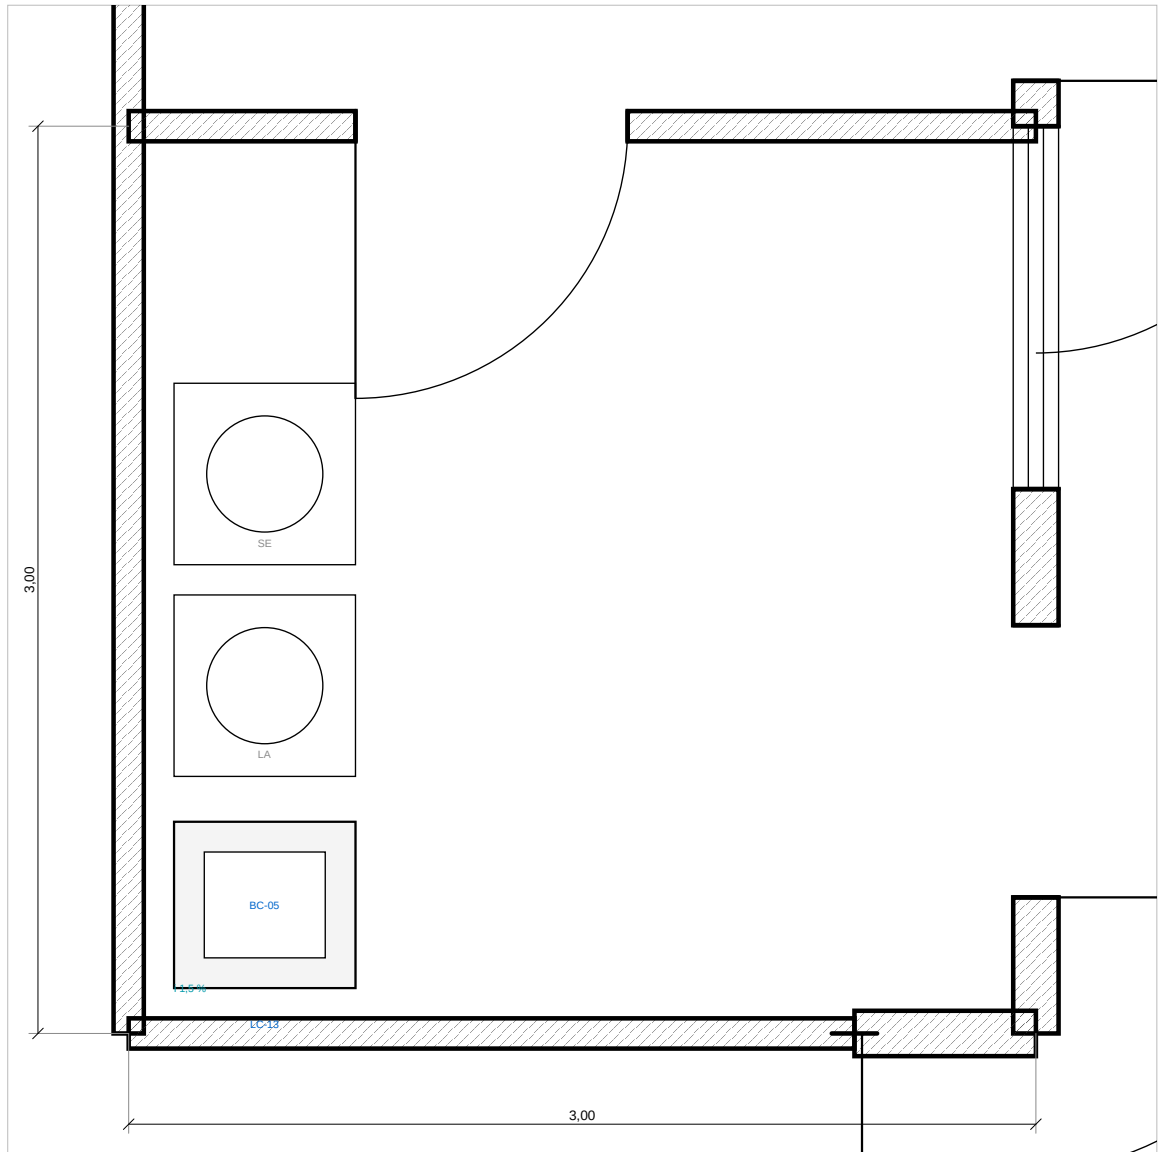

2 LAVANDERIA
ESCALA 1:25

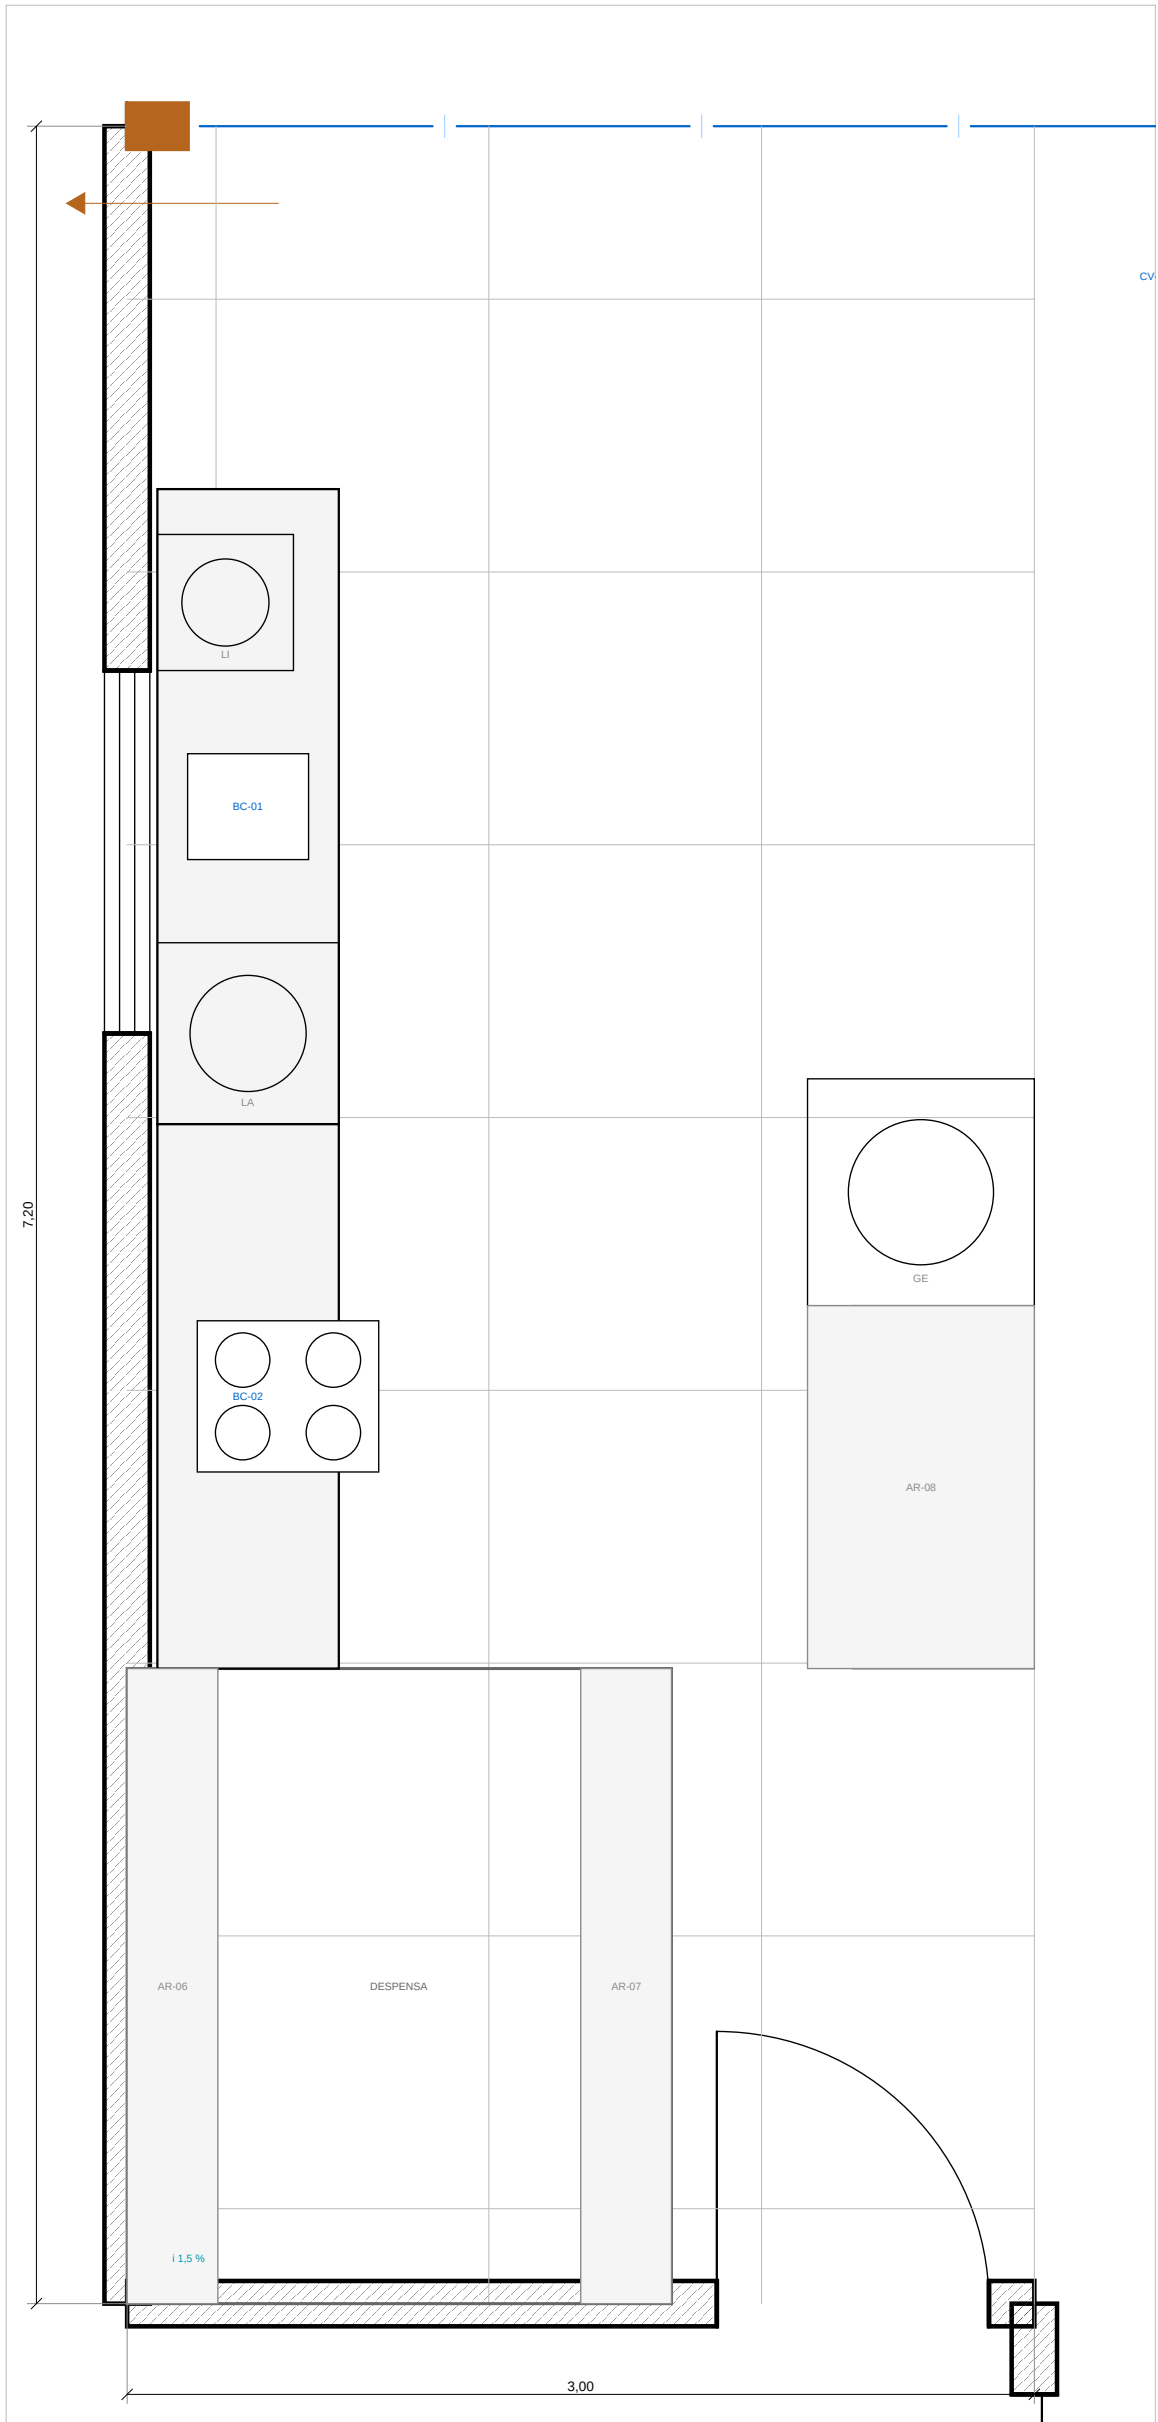

3 COZINHA
ESCALA 1:25

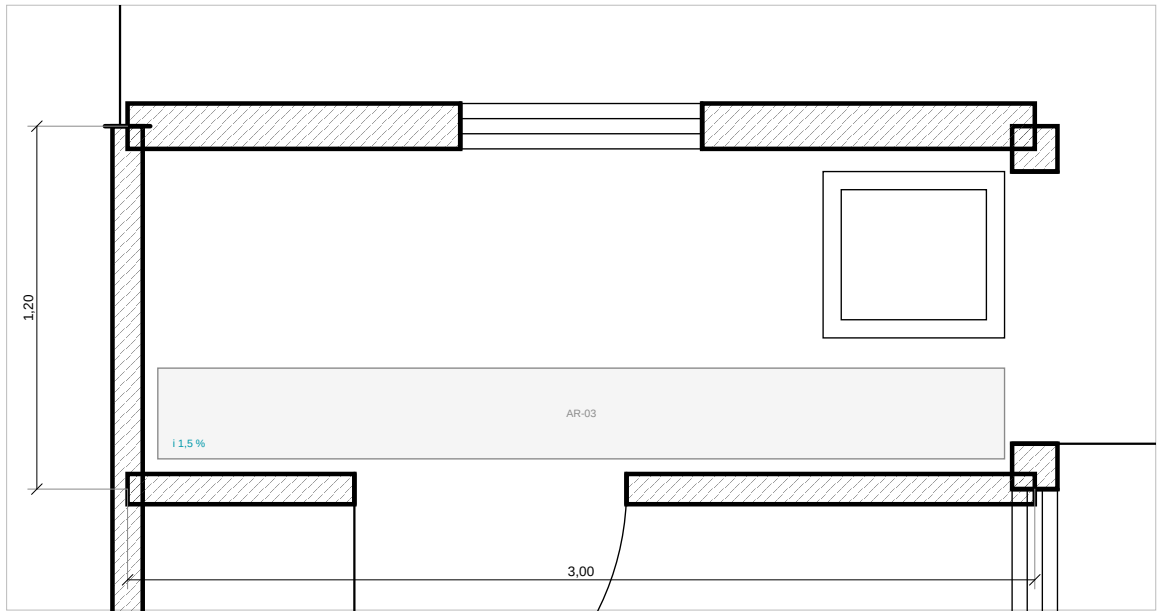

4 DEPOSITO / DML
ESCALA 1:25

PAGINACAO VERIFICADA — PECAS INTEIRAS + RECORTE EM CADA PONTA

AMB	AMBIENTE	ZONA	PEÇA	EXTO X	EXTO Y	ALTURA (mm)
T-CORR	LAVABO SOB A ESCADA	ZP-5	plac	2 + 990/994	0 + 990/994	---
T-LAV	LAVANDERIA	ZP-5	plac	9 + 9280	4 + 9590	1800 (2 fustes + 996)
T-COC	COZINHA	ZP-5	plac	3 + 2620	7 + 3120/310	---
T-DEP	DEPOSITO / DML	ZP-5	plac	9 + 9280	1 + 9596	1800 (2 fustes + 996)

NOTAS

- * Pignonicus de piso em linha fina, a malha vem da ZONA de pignonicus, não do canto do ambiente.
- * Pignonicus de piso porcelanado retificado 900 x 900, parede cerâmica retificada 300 x 600, junta 2 mm.
- * Cimento de 1,5 % para o piso em toda área molhada, soltura elevada 15 mm nos bicos.
- * Representação: marca igual em 2 dimensões, subindo 300 mm na parede e 1.800 mm nos bicos.

PROJETO PORTO REAL

RESIDENCIA UNIFAMILIAR (MARIAUS - AM) | SOUS TATIANA-PS

PROJETO ARQUITETONICO

AMPLIACOES DE AREA MOLHADA — TERREO

BASE GEOMETRICA Linha Consolidada Projeto (previsão) UNIDADE: METROS - MM	ESCALA 1:25 FORMATO A1 MILHA 600/600/600	EMISSAO ESTUDIO PRELIMINAR R07 NÃO LIBERADO PARA OBRA SEM ART / RNT	PROJETO 22 06-48 REV R07
--	---	--	--------------------------------