




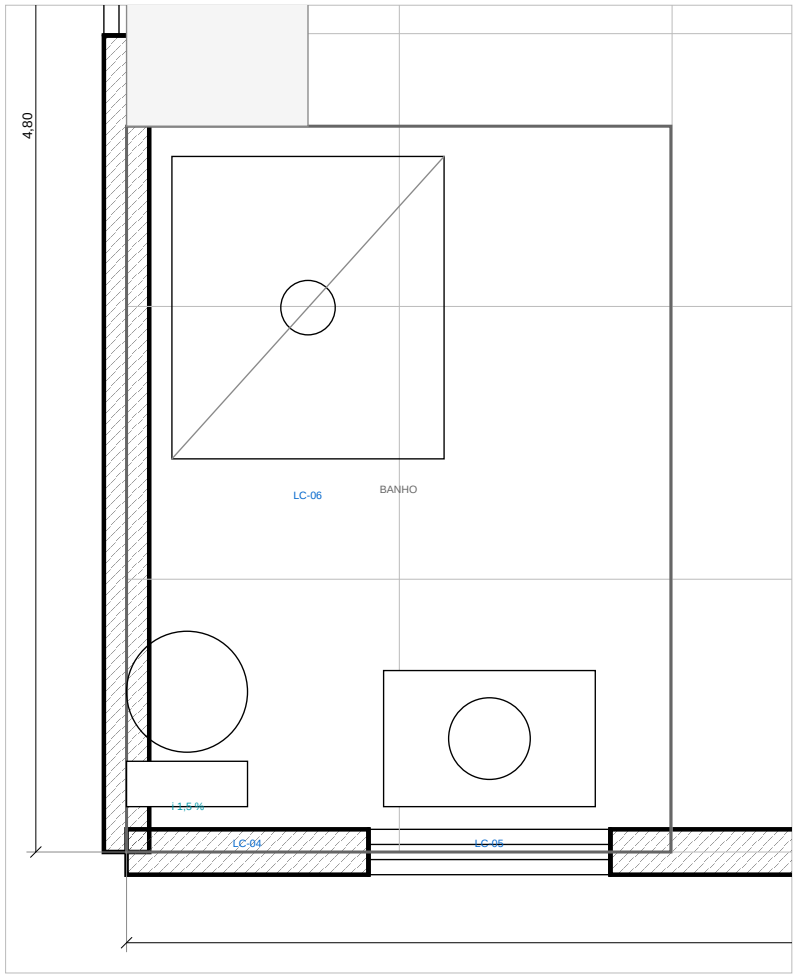


1 SUITE 02 — BANHO
ESCALA 1:25

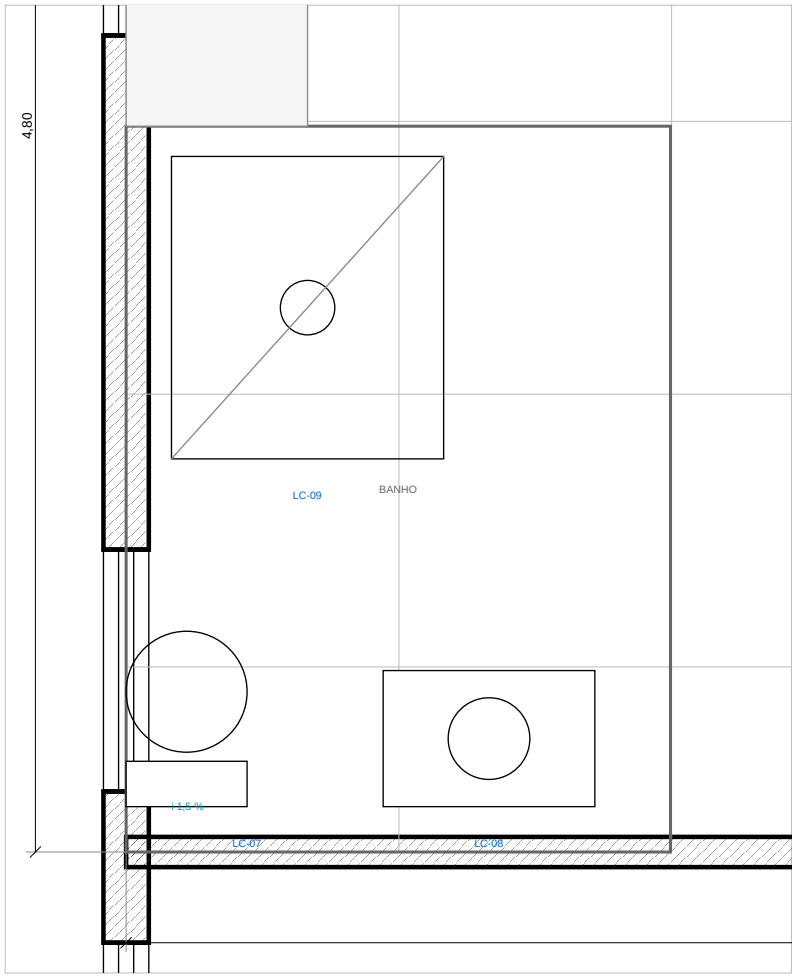

2 SUITE 03 — BANHO
ESCALA 1:25

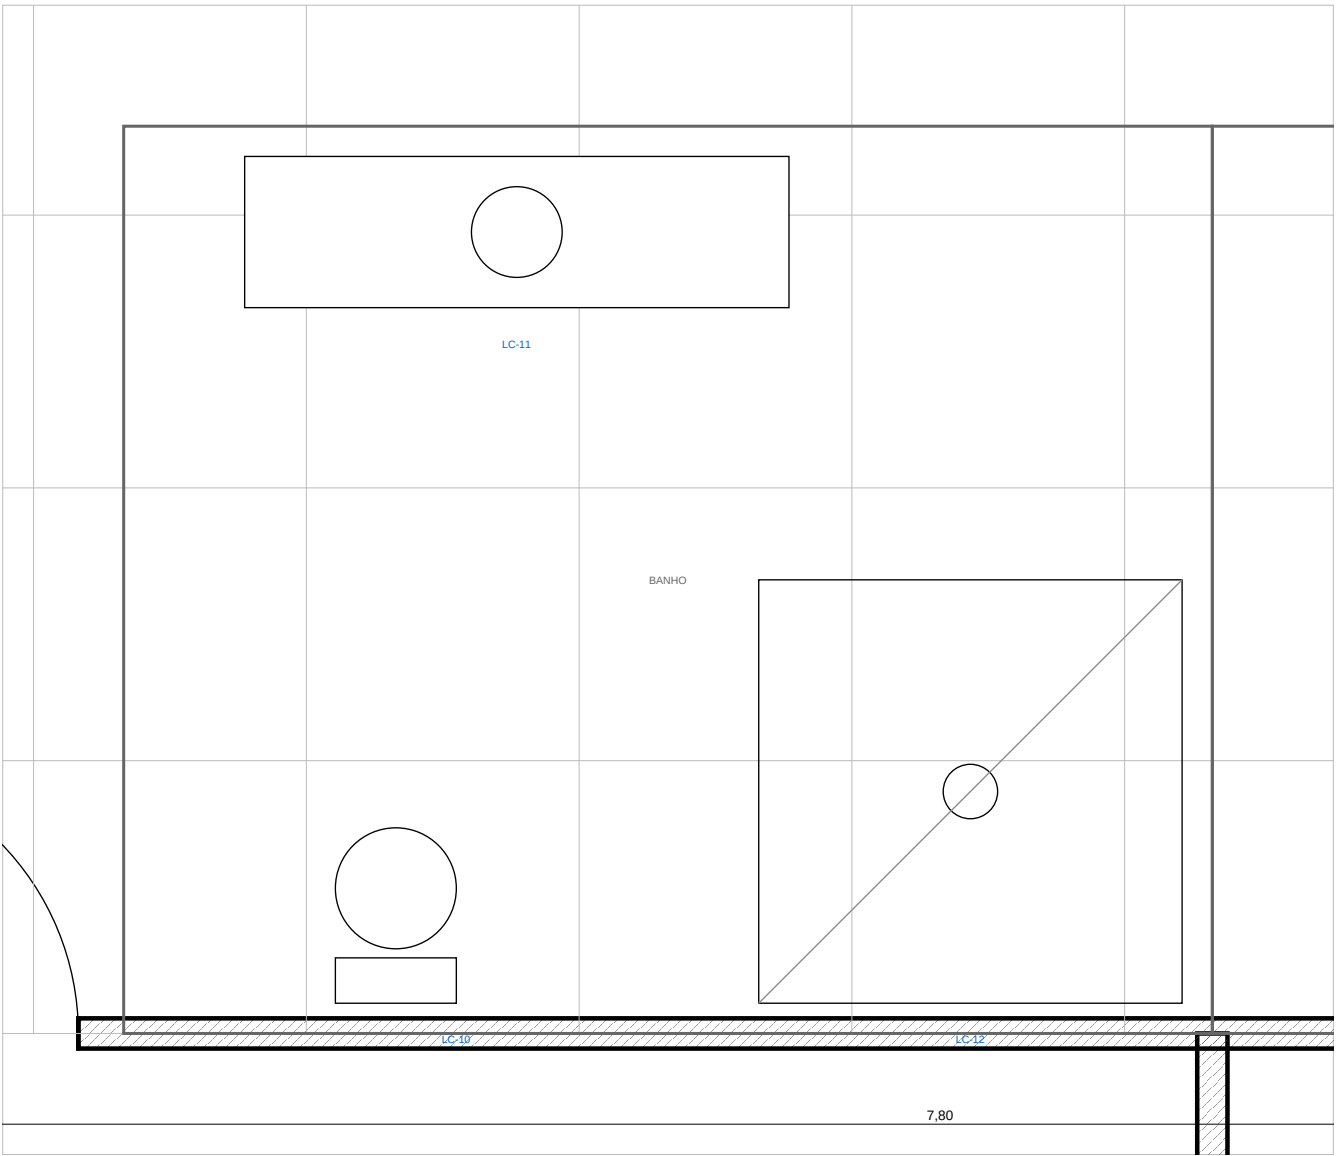

3 MASTER — BANHO
ESCALA 1:25

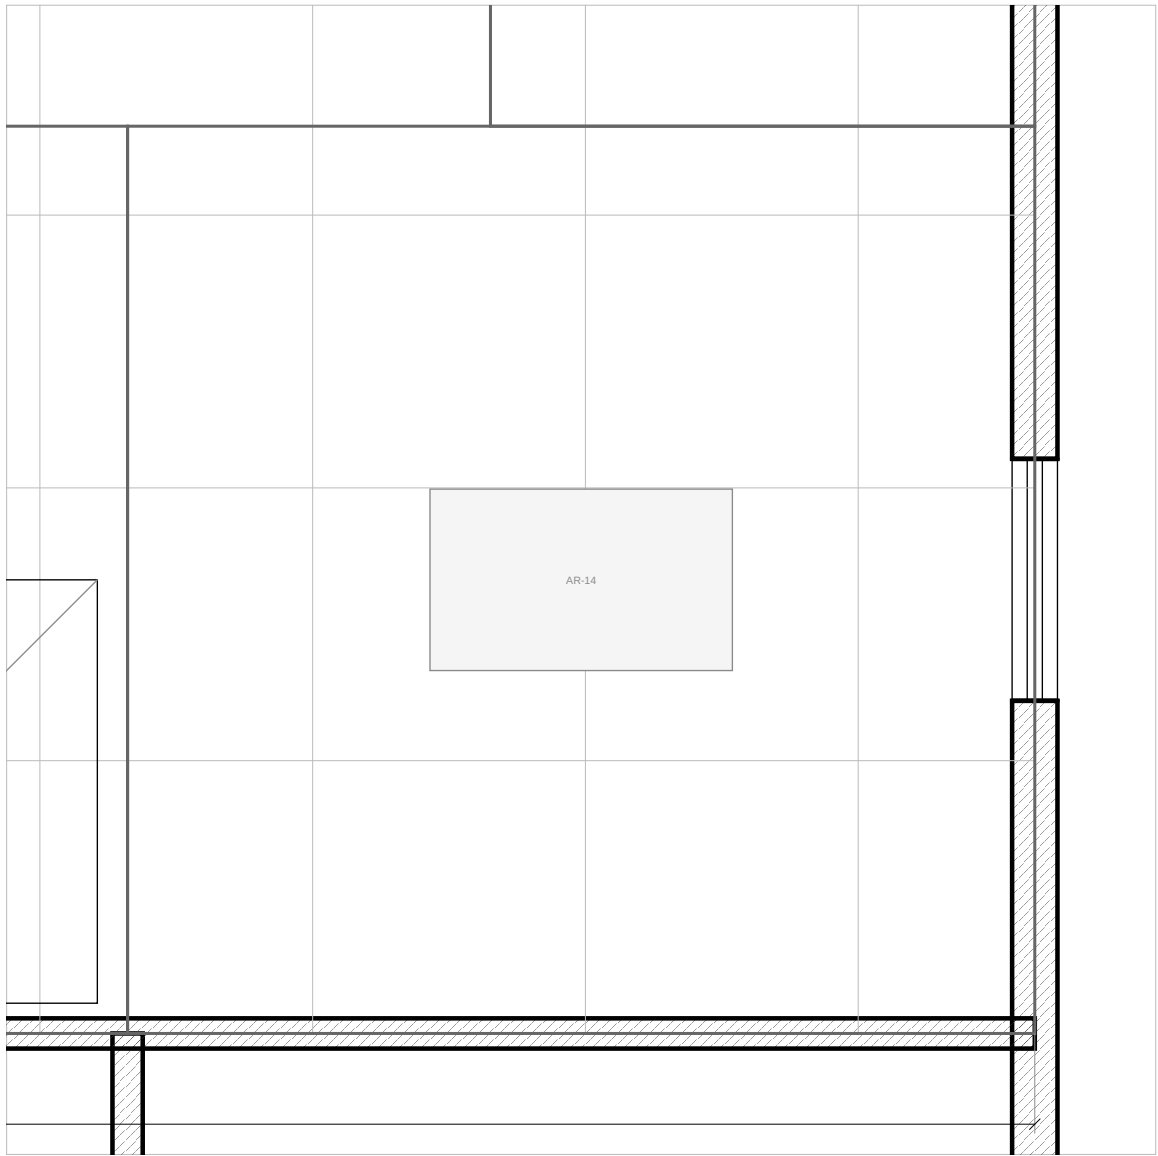

4 MASTER — CLOSET
ESCALA 1:25

PAGINACAO VERIFICADA — PECAS INTEIRAS + RECORTE EM CADA PONTA

AMB	AMBIENTE	ZONA	PEÇA	EXO X	EXO Y	ALTURA (mm)
S-002	SUITE 02 — BANHO	ZP-3	gno	S-0000	S-0000	—
S-003	SUITE 03 — BANHO	ZP-3	gno	S-0000	A-000007	—
S-005	MASTER — BANHO	ZP-2	gno	S-0000	C-0000	—
S-006	MASTER — CLOSET	ZP-2	gno	S-0000	S-0000	—

NOTAS

- Figuras de piso em linha fina, a linha verde da ZONA de paginação, não do canto do ambiente.
- Peça de piso porcelanado retificado 300 x 300, parede cerâmica retificada 300 x 600, porta 2 mm.
- Cimento de 1:3 para o piso em toda área molhada, solaria elevada 15 mm nos banhos.
- Representação: porta ligada em 2 dimensões, subindo 300 mm na parede e 1.800 mm nos banhos.

PROJETO PORTO REAL

RESIDENCIA UNIFAMILIAR (MANAUS - AM) | SUITE TATIANA-PS

PROJETO ARQUITETONICO

AMPLIACOES DE AREA MOLHADA — SUPERIOR

BASE GEOMETRICA Linha Consolidada Projeto (previsão) UNIDADE: METROS - MM	ESCALA 1:25 FORMATO A1 MILIMETROS (50/50/50)	EMISSAO ESTUDO PRELIMINAR R07 Linha Libertada PARA ORCA SEM ART / RNT	PROJETO 23 06-48 REV R07
--	---	--	--------------------------------