


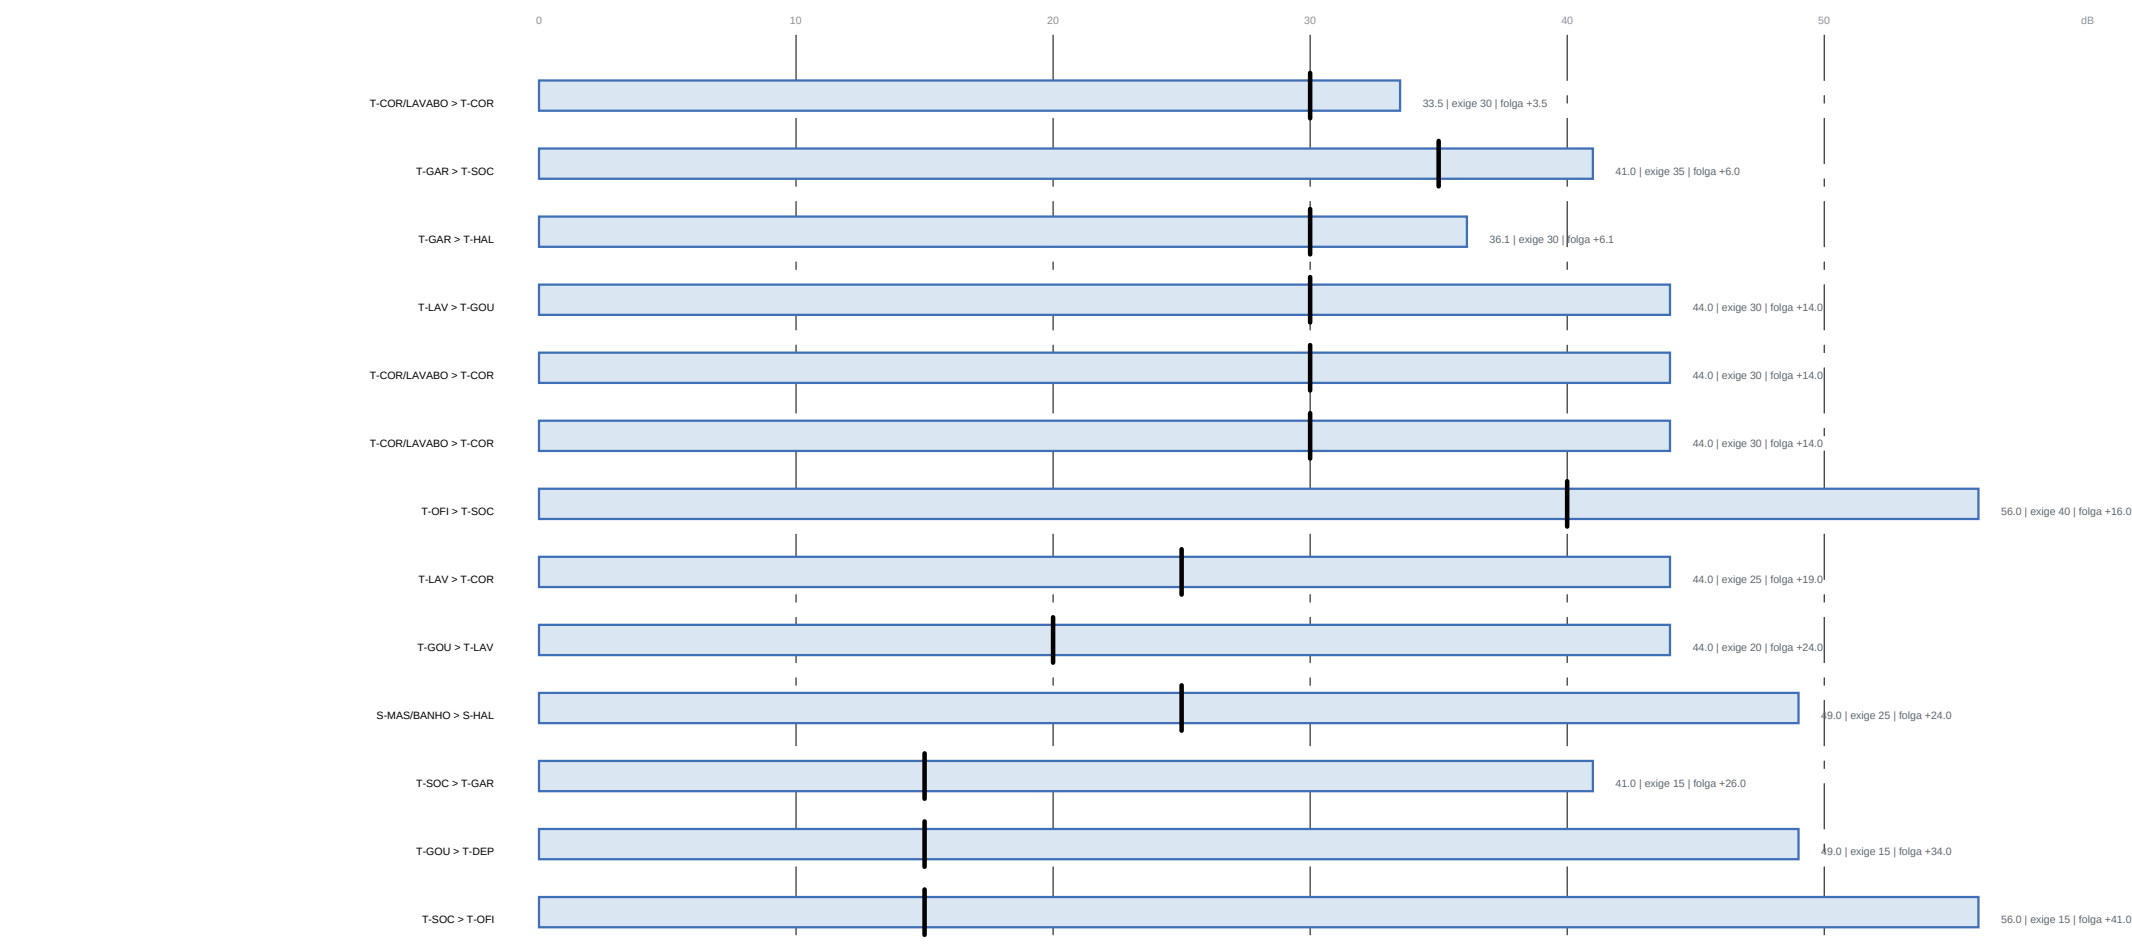

Fonte: s/ isolamento (dB); traço vertical = energia (dB) da fonte sonora frente do receptor. NBR 15102

O QUE MUDOU EM R52

ONDE	ANTES	DEPOIS	POR QUE
Banho compartilhado + hall de entrada	porta de correr (Pw 25) — conjunto de 20,2 dB	parede CEGSA, 44 dB	o acesso de volta passou para a circulação
Banho compartilhado + quarto eventual	porta com (Pw 25) — conjunto de 25,5 dB, energia 25	parede CEGSA, 44 dB	era a por passagem da casa, e não era a saída
Hall + garagem	porta com — 36,9 dB, energia 35	PdS isolada vedada — 36,9 dB	porta entre garagem e casa tem dupla função para ser morda
Banho compartilhado + circulação	não havia porta	PdS isolada vedada — 35,7 dB, energia 25	único acesso do banho, e abria para fora
Bloco do chuveiro	encostado na parede do hall	canto arredado, sob a janela alta	consequência da porta nova, a regra dos 900 cm de box obrigou a primeira tentativa

TABELAS ADOTADAS

ITEM	VALOR	FONTE
Fonte: caixa sanitária	15 dB(A)	prática corrente de acústica
Fonte: bloco do chuveiro	15 dB(A)	prática corrente de acústica
Fonte: cozinha e gourmet	15 dB(A)	prática corrente de acústica
Fonte: sala e jantar	15 dB(A)	prática corrente de acústica
Fonte: garagem	15 dB(A)	prática corrente de acústica
Fonte: máquina de lavar e secar	15 dB(A)	prática corrente de acústica
Fonte: oficina	55 dB(A)	prática corrente de acústica
Limite: banho	45 dB(A)	NBR 15102:2017 (circulação e entrada adiabática)
Limite: circulação	45 dB(A)	NBR 15102:2017 (circulação e entrada adiabática)
Limite: cozinha	45 dB(A)	NBR 15102:2017 (circulação e entrada adiabática)
Limite: depósito	55 dB(A)	NBR 15102:2017 (circulação e entrada adiabática)
Limite: dormitório	35 dB(A)	NBR 15102:2017 (circulação e entrada adiabática)
Limite: entrada	45 dB(A)	NBR 15102:2017 (circulação e entrada adiabática)
Limite: estar	45 dB(A)	NBR 15102:2017 (circulação e entrada adiabática)
Limite: garagem	55 dB(A)	NBR 15102:2017 (circulação e entrada adiabática)
Limite: office	45 dB(A)	NBR 15102:2017 (circulação e entrada adiabática)
Limite: oficina	55 dB(A)	NBR 15102:2017 (circulação e entrada adiabática)
Limite: serviço	55 dB(A)	NBR 15102:2017 (circulação e entrada adiabática)
Fonte: acústica	Pw 25 dB	Nota de mercado declarada
Fonte: sonar	Pw 25 dB	Nota de mercado declarada
Fonte: sala	Pw 25 dB	Nota de mercado declarada
Fonte: sala de	Pw 25 dB	Nota de mercado declarada
Fonte: sala de visita	Pw 30 dB	Nota de mercado declarada

NOTAS

1 Esta planilha está para que o proprietário pergunte e que 100 verificações não sabem responder: quem entra na casa ouve o chuveiro do banho da entrada?

2 Ouviu. A parede era box (Pw 1, Pw 4) e a porta era de correr (Pw 25), o conjunto entregava 20 dB. Em acústica o eixo físico DOMINA — não se faz média aritmética do isolamento, se soma energia que passa.

3 Isolamento se se engra ENTRE, mas. Dentro da file social o lado não e definido, e o programa.

4 O aditivo igual ao 10 compõe (significância declarada). Não e pre-verificação de projeto, mas ensaio de campo da NBR 15107-3.

PROJETO PORTO REAL

RESIDENCIA UNIFAMILIAR (MANSÃO - AM) | SOBR TATIANA-PS

PROJETO ARQUITETONICO

DESEMPENHO ACUSTICO ENTRE AMBIENTES

BASE GEOMETRICA	ESCALA	EMISSAO	PROVA
Lista Consolidada	s/ escala	ESTUDO PRELIMINAR R57	
ISO R52 (previsão)	FORMATO A1	ISO LIBERADO PARA CRIA	39
UNIDADE MESTRE: m/s	MILHA 655/500/500	SEM ART / RNT	06-48 REV R57