


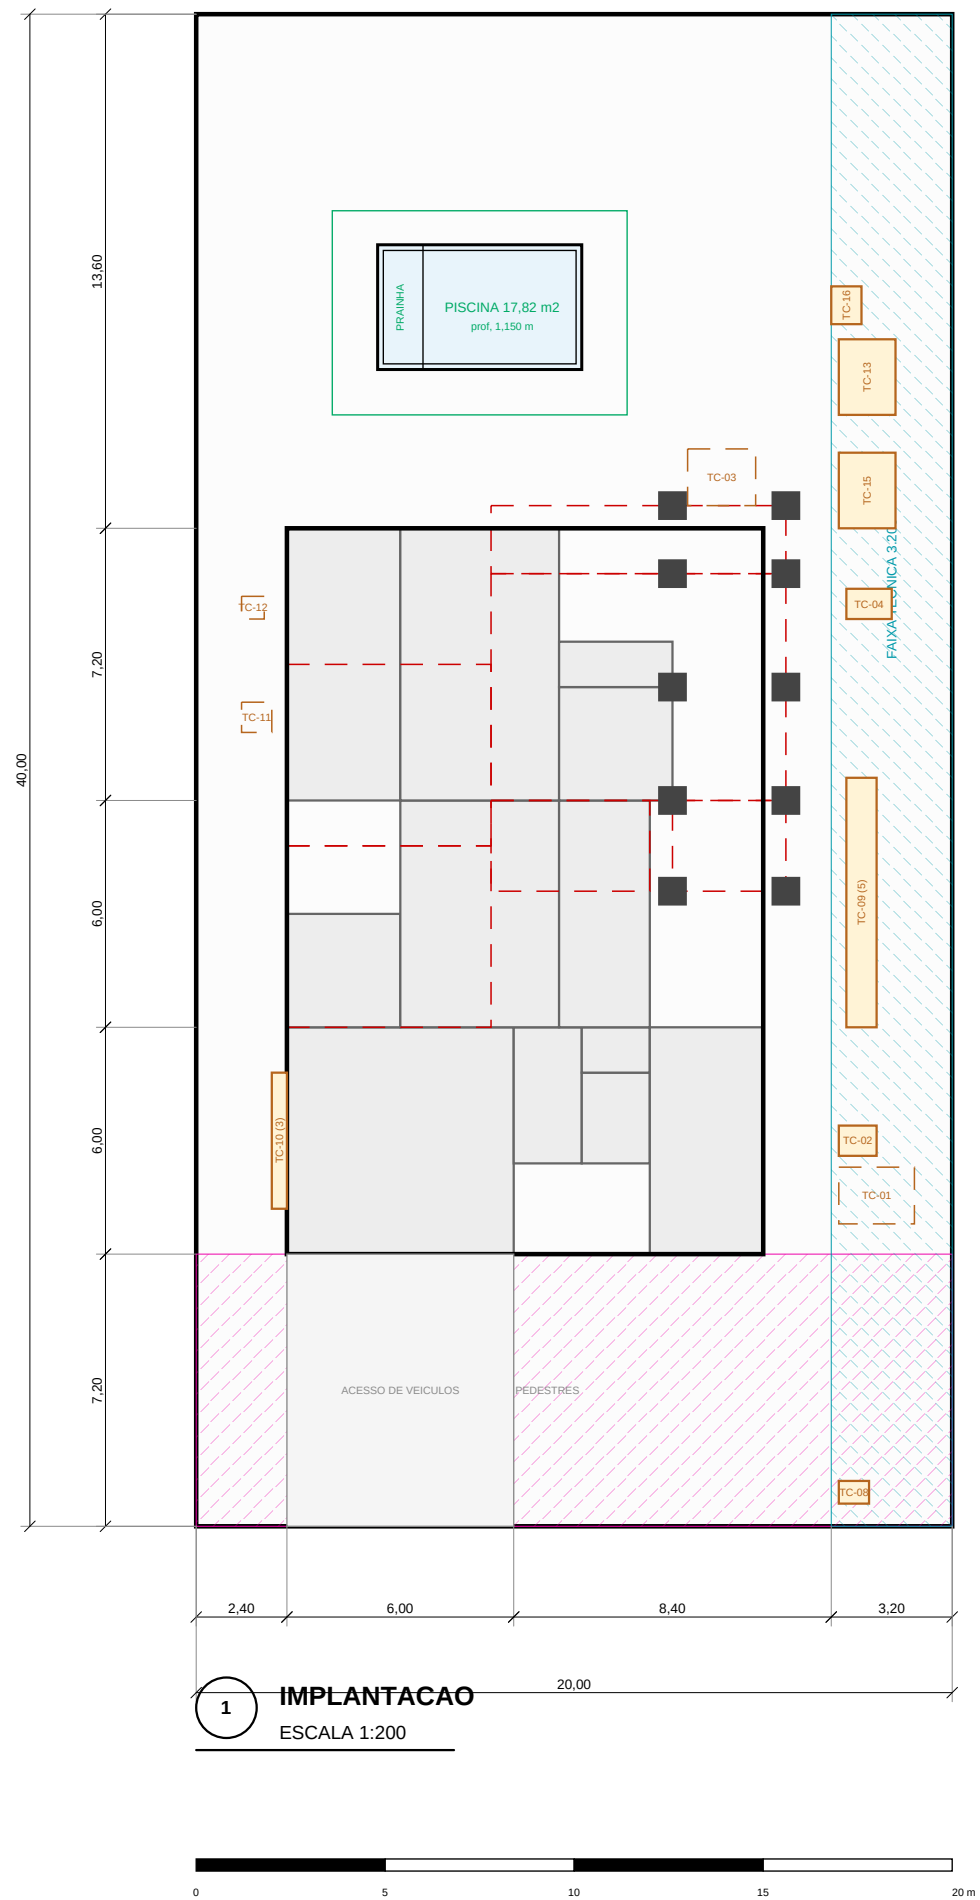

VERIFICACAO URBANISTICA (H)

PARAMETRO	PROJETO	LIMITE	
Taxa de ocupação	33,21 %	até 50 %	OK
Coeff. de aproveitamento	0,370	até 1,00	OK
Calçada	2 passeios	até 4	OK
Recuo frontal	7200 mm	conforme 50/00 [4]	OK
Recuo lateral esq.	2400 mm	sem limite no lado	OK
Recuo lateral dir.	3000 mm	até 3000 mm	OK
Recuo de fundo	13600 mm	até 5000 mm	OK



- NOTAS
- * Lote: 25.000 x 40.000 m² = 800.00 m².
 - * Recuo: frontal 7.200 / lateral esq. 2.400 / lateral dir. 3.000 / fundo 13.600 mm.
 - * Parâmetros do SUD: Taxa de Ocupação 33,21% / Coef. de Aproveitamento 0,370 / Recuo frontal 7.200 mm / Recuo lateral esq. 2.400 mm / Recuo lateral dir. 3.000 mm / Recuo de fundo 13.600 mm.
 - * Sem muro frontal, mural lateral e de fundo 0 a 2.000 mm.

PROJETO PORTO REAL

RESIDENCIA UNIFAMILIAR (MANSÃO) - AM | SOUS TATIANA-PS

PROJETO ARQUITETONICO

IMPLANTACAO E SITUACAO

BASE GEOMETRICA Linha Consolidada Projeto (previsão) UNIDADE: METRO - MM	ESCALA 1:200 FORMATO: A1 MATERIAL: 60/60/60/60	EMISSAO ESTUDO PRELIMINAR R4 Linha Consolidada PARA ORCA SEM ART / RNT	PROJETO 01
---	---	---	---------------