




COZINHA — PAREDE SUL (BANCADA PRINCIPAL)

- bancada em granito, 600 mm de profundidade

- circulação livre mínima de 1.000 mm (desagüa 1.100)


- 6 tomadas de bancada a 1.100 mm

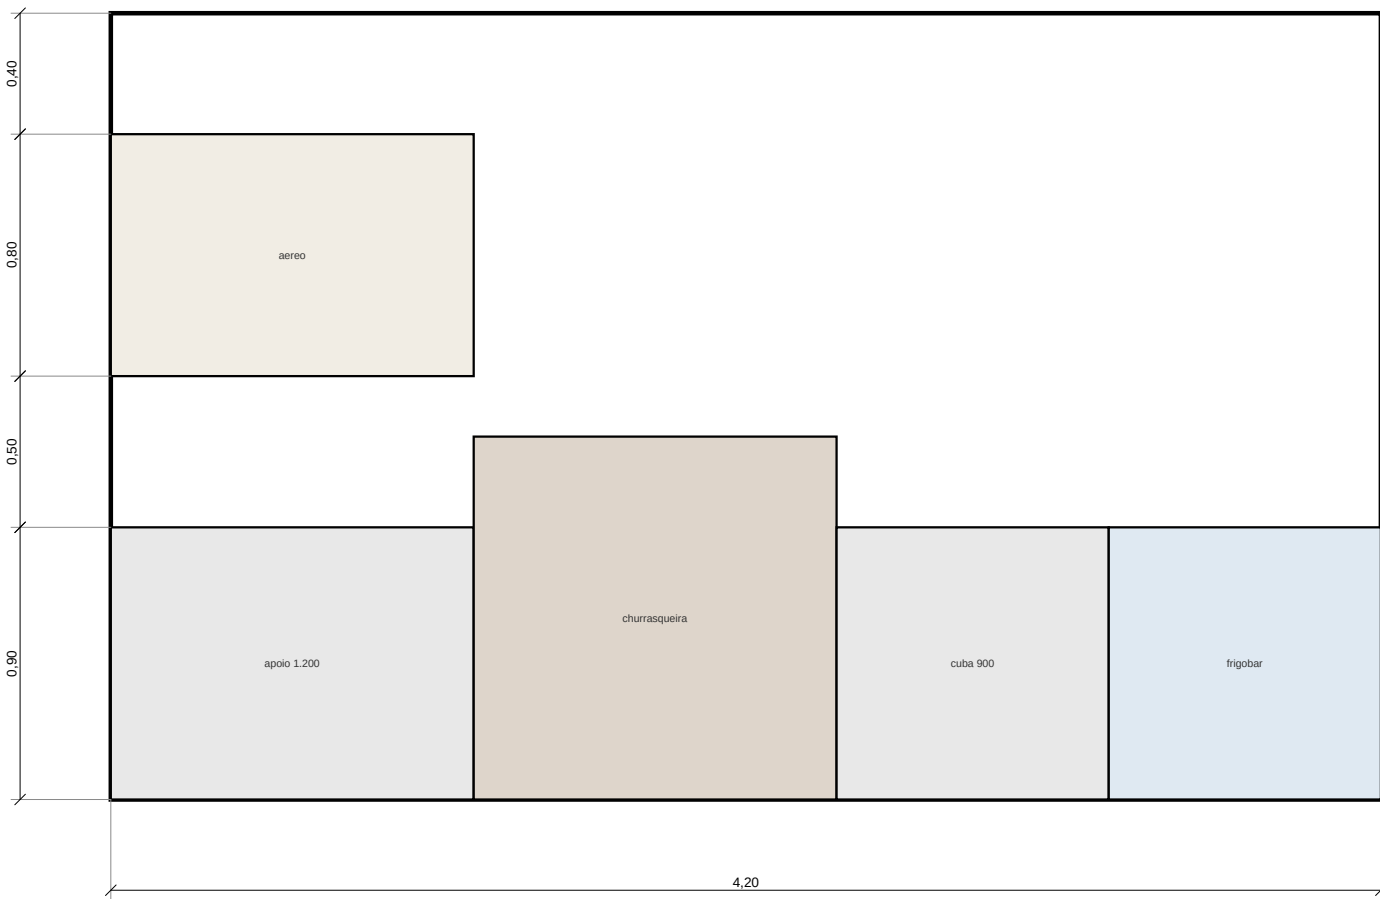

GOURMET — BANCADA E CHURRASQUEIRA

- cofa com vazão mínima de 20 litros por hora de volume


- bancada integrada a cozinha pelo vão livre

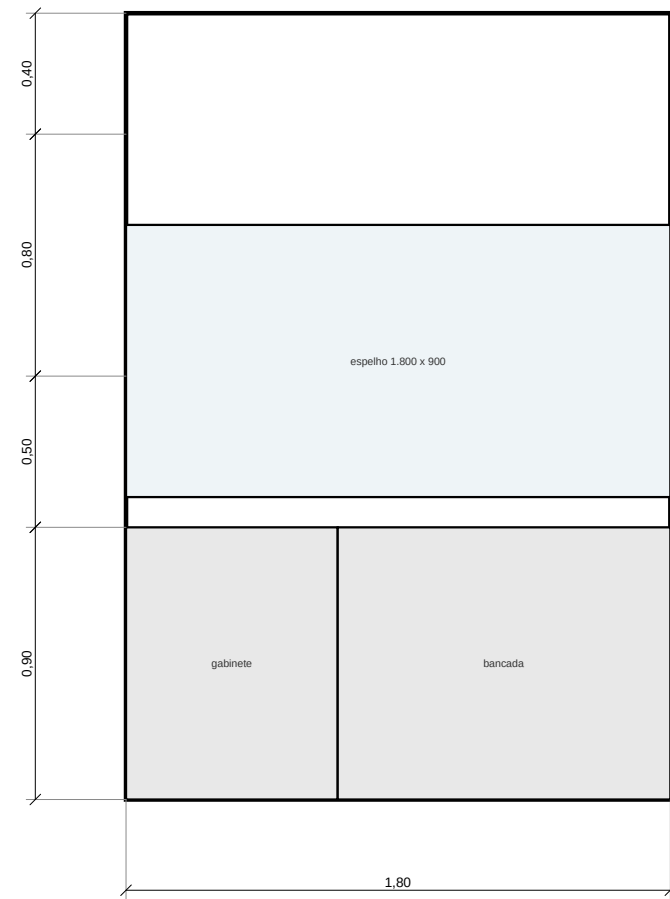

BANHO COMPARTILHADO — PAREDE DA BANCADA


- reforço embutido para barra de apoio de 1400 x 500

- porta de correr de 900 mm (barra e chuveiro de 900)

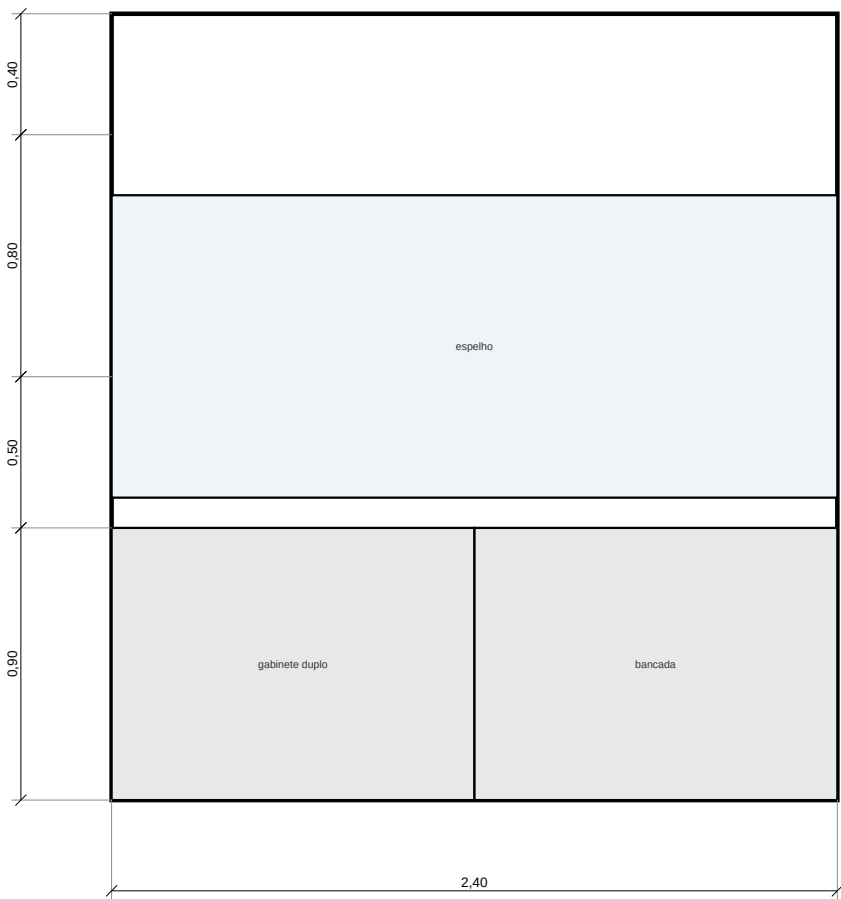

SUITE MASTER — BANHO

- revestimento cerâmico até o teto na área molhada

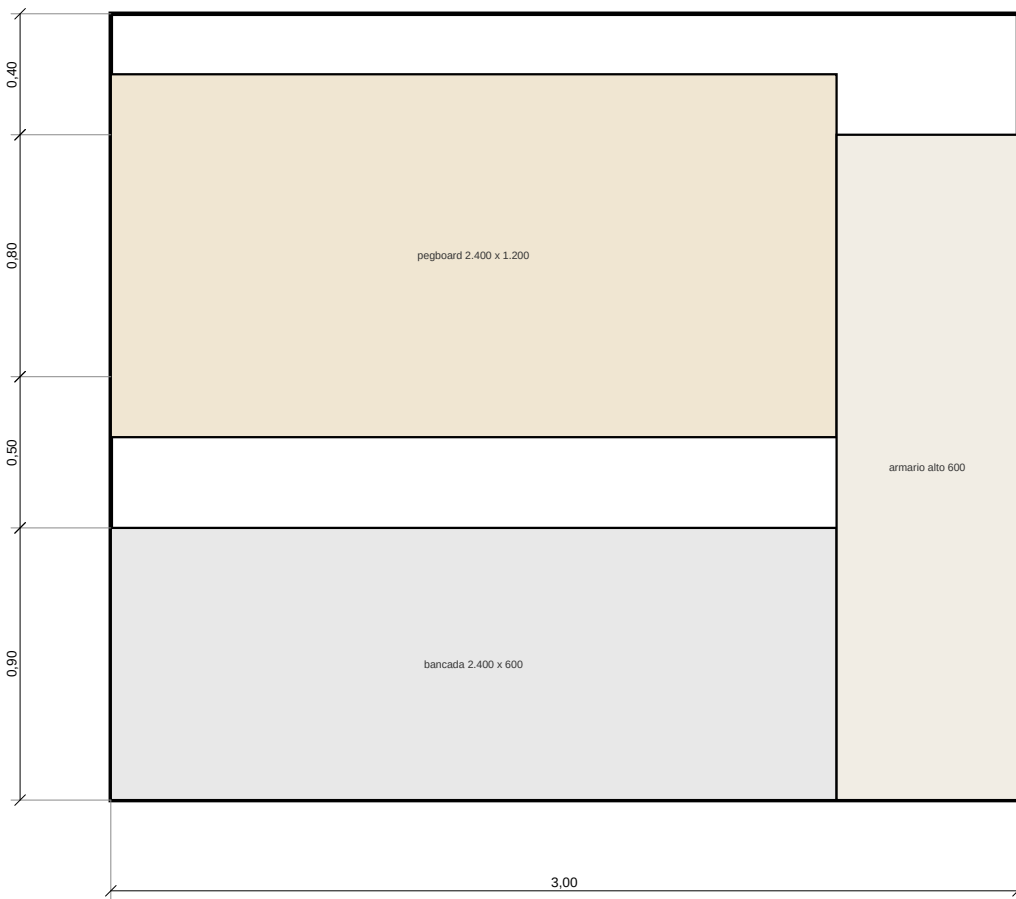


OFICINA — BANCADA DE TRABALHO

- 6 tomadas de bancada, circuito comum 20 A e máxima 32 A (p)

- iluminação geral 500 lux e 800 lux sobre a bancada, 4.000 K

- área central livre de 1.200 x 1.800 mm

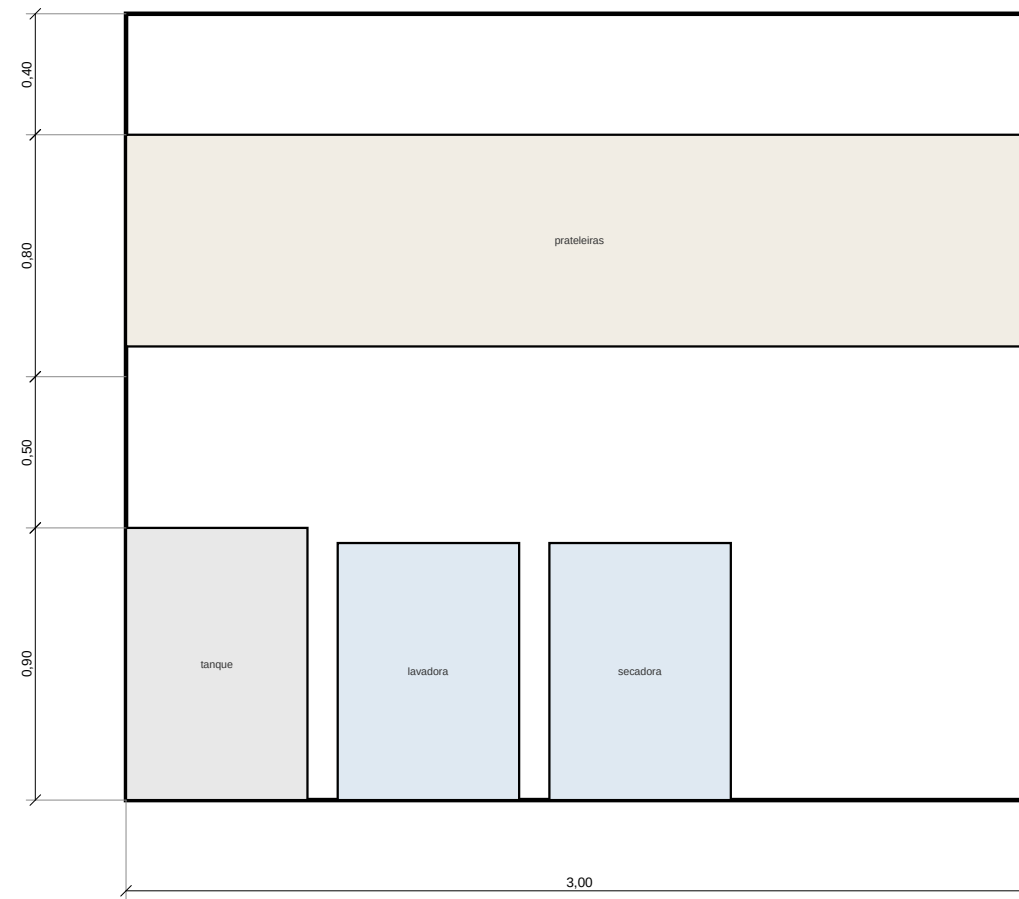

LAVANDERIA — TANQUE E MAQUINAS

- base antiderrapante sob as máquinas: tudo embutido

- graxado no parede de apoio, longe da oficina

NOTAS

- Visão de parede: base para marcenaria, revestimento e pontos elétricos.
- Modulo de marcenaria em 300 x 400 x 600 mm, conforme o briefing.
- Bancadas a 900 mm, área superior de 1.400 x 2.200 mm.
- Altura de bancada: 900 mm e profundidade 600 mm (com o apoio).

PROJETO PORTO REAL

RESIDENCIA UNIFAMILIAR (MANSÃO - AM) | SOLO TERTIÁRIO (P)

PROJETO ARQUITETONICO

ELEVACOES INTERNAS

BASE GEOMETRICA

União Consolidada

Projeto (preliminar)

UNIDADE: MESTRE: AM

ESCALA

1:25

FORMATO: A1

MAQUETA: 600x900mm

EXIBICAO

ESTUDO PRELIMINAR R4

NAO LIBERADO PARA OBRA

SEM ART / INT

PROJETO

15

06/25 REV/R4