




● luminária embuída, 3.000 K, RSC 90

□ alçapão técnico 600 x 600 mm

▨ forro absorvente (alfa 0,70)

FORROS POR AMBIENTE

AMBIENTE	SOLUÇÃO	ÁREA	NOTA
T.CC1	forro absorvente (α=0,70) e refletor no par	36,24	único ponto que demanda a instalação de 3,20 x 60
T.BC2	gesso liso + cantoneira e tapetes	25,20	abertura entre os módulos, forro técnico aqui não
T.CC2	gesso liso + refletor	18,00	superfície de fácil limpeza sem necessidade de manutenção
S.BC2	gesso liso + la mineral sobre o forro	25,80	la sobre o forro permite tudo de ruído no parafuso
S.BC3	gesso liso + la mineral sobre o forro	25,80	idem
S.BC4	gesso liso + la mineral sobre o forro	25,80	idem
T.GAR	sem forro (estrutura aparente)	36,00	ambiente semi-escuro, acústica não forçada
T.OP1	sem forro (estrutura aparente)	9,00	idem
T.CCP	sem forro (estrutura aparente)	3,00	idem

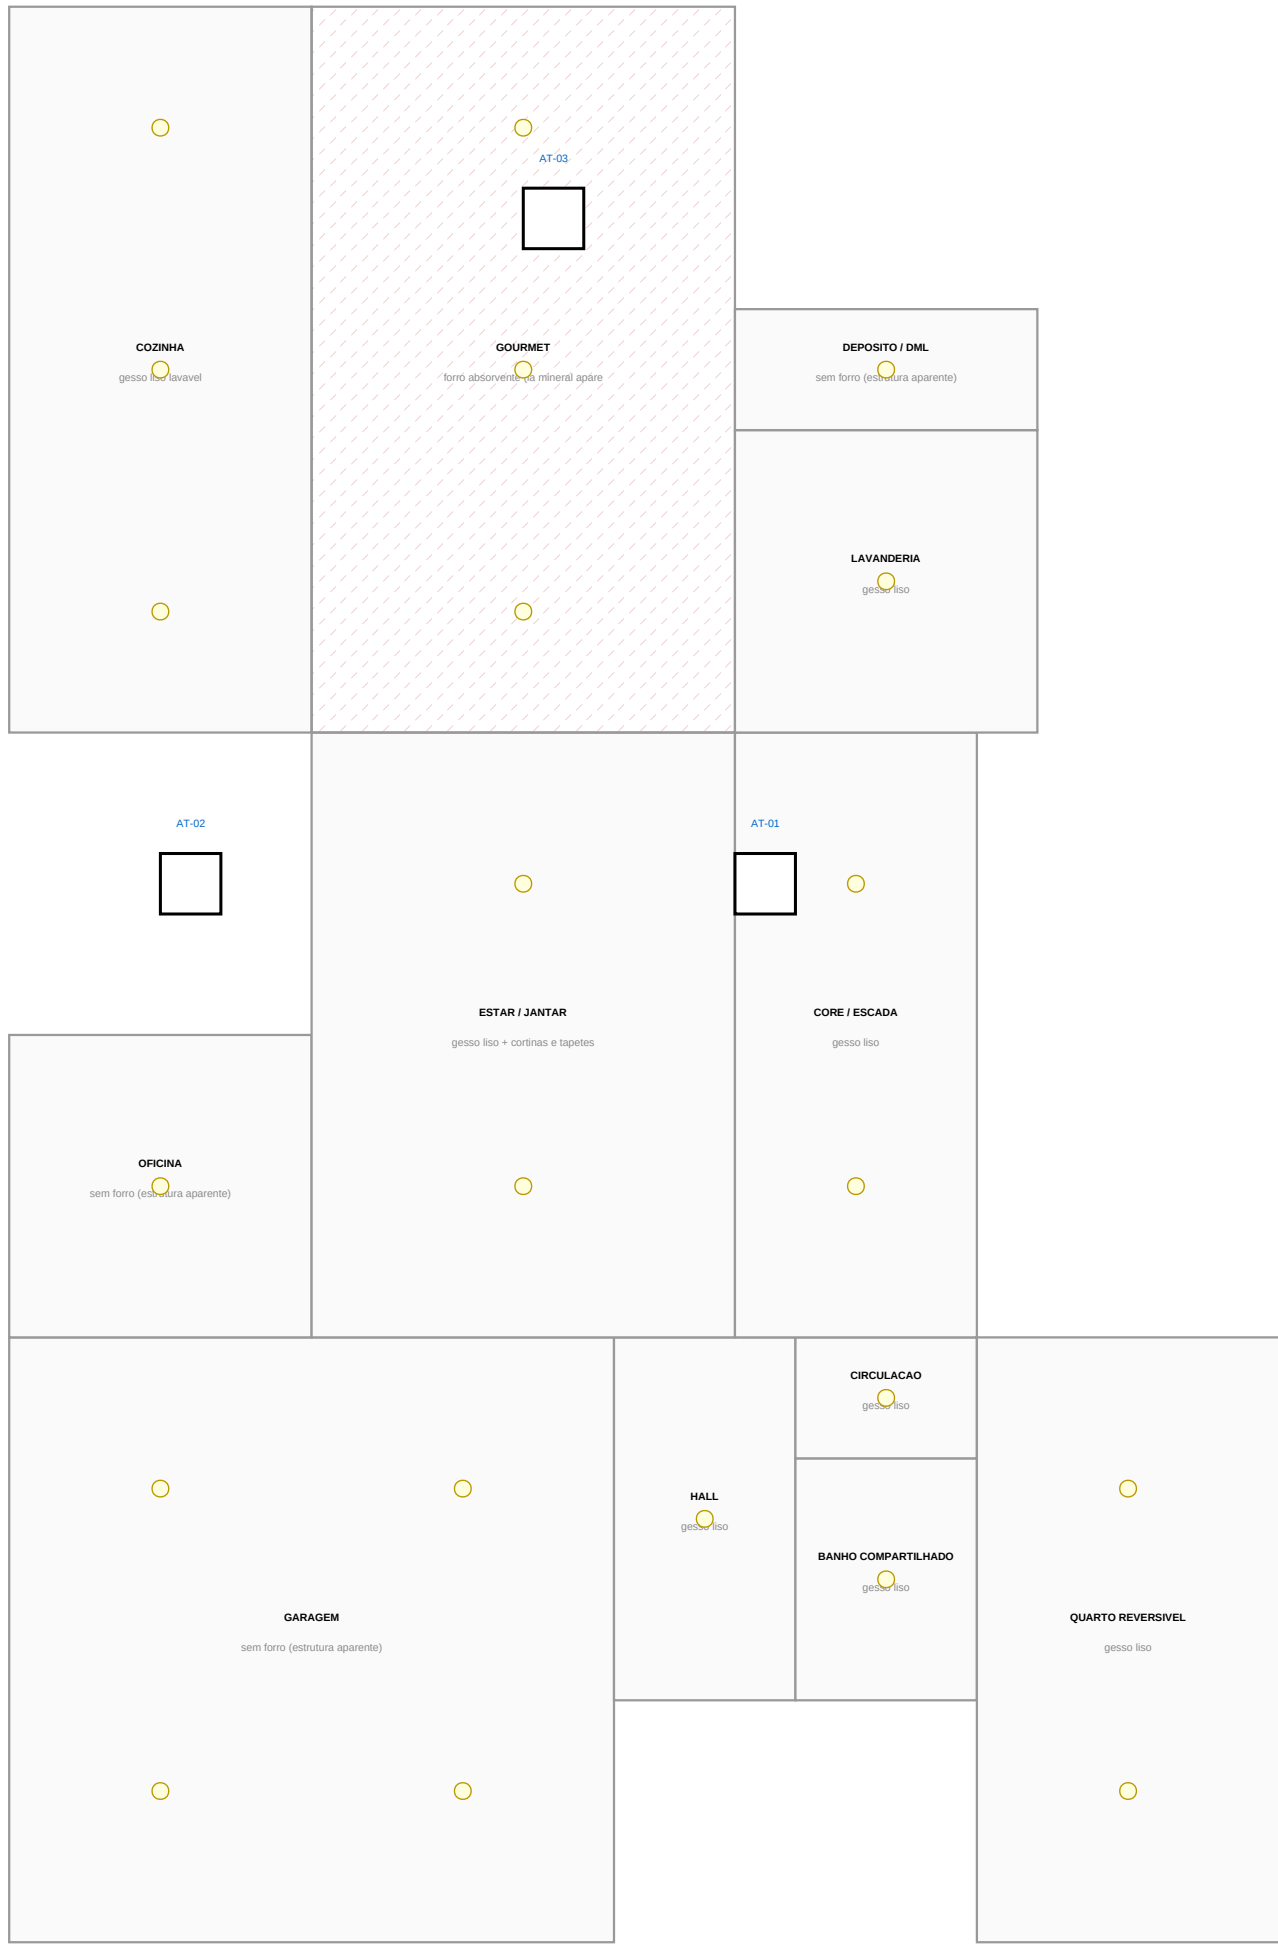

1 FORRO REFLETIDO — TERREO
ESCALA 1:75

NOTAS

- * Planta refletida: vista do forro projetada no plano horizontal.
- * Forro absorvente apenas no gourmet — único ponto com necessidade crítica.
- * Alçapão técnico de 600 x 600 mm, passando de cobertura de 600 mm.
- * Luminária geral 3.000 K, RSC modelo 90.

PROJETO PORTO REAL

RESIDÊNCIA UNIFAMILIAR (MANAUS - AM) | 2024 | TATIANA PI

PROJETO ARQUITETÔNICO

PLANTA DE FORRO E ILUMINAÇÃO

BASE GEOMÉTRICA Linha Consolidada ISO 15723 (previsão) UNIDADE: METROS - MM	ESCALA 1:75 FORMATO A1 MÁQUINA: 600/600/300	EMISSÃO ESTUDO PRELIMINAR R4 LADO LIBERADO PARA DRENAÇÃO SEM ART / RNT	PROVA 16 06-25 REV R44
--	---	---	-------------------------------------