




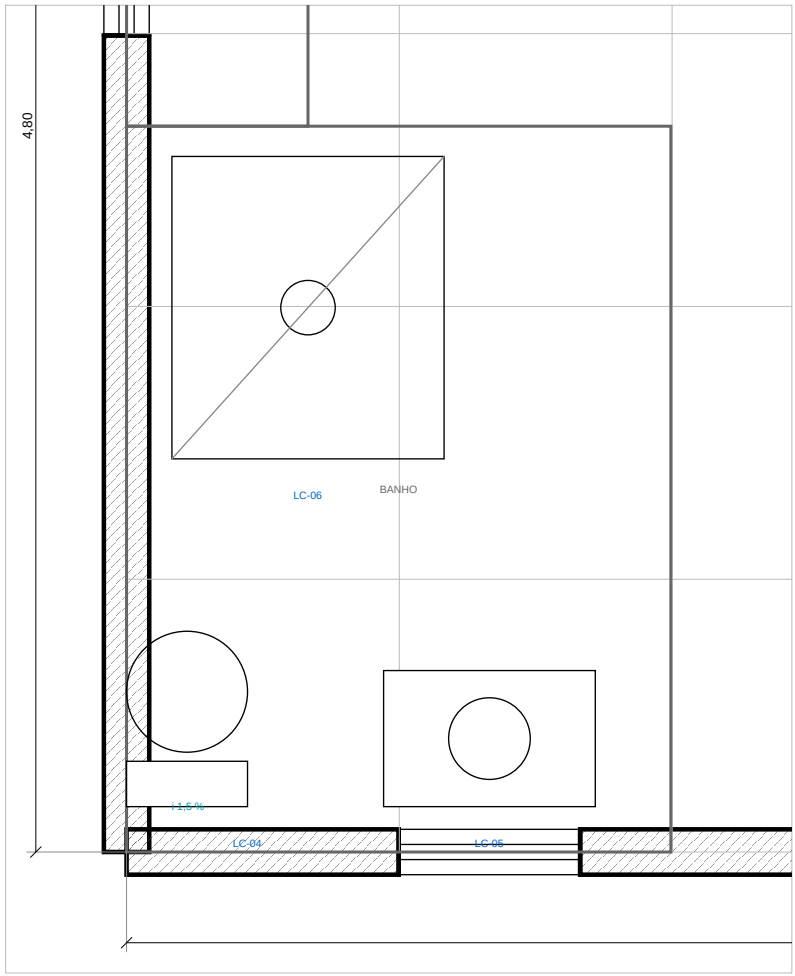


1 SUITE 02 — BANHO
ESCALA 1:25

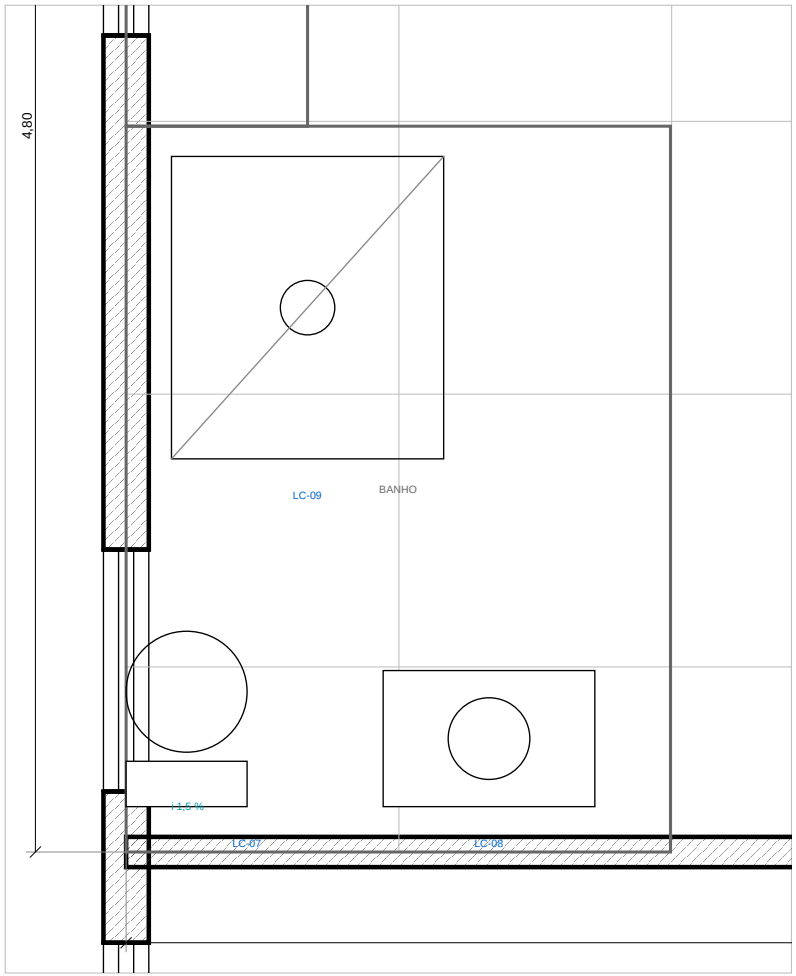

2 SUITE 03 — BANHO
ESCALA 1:25

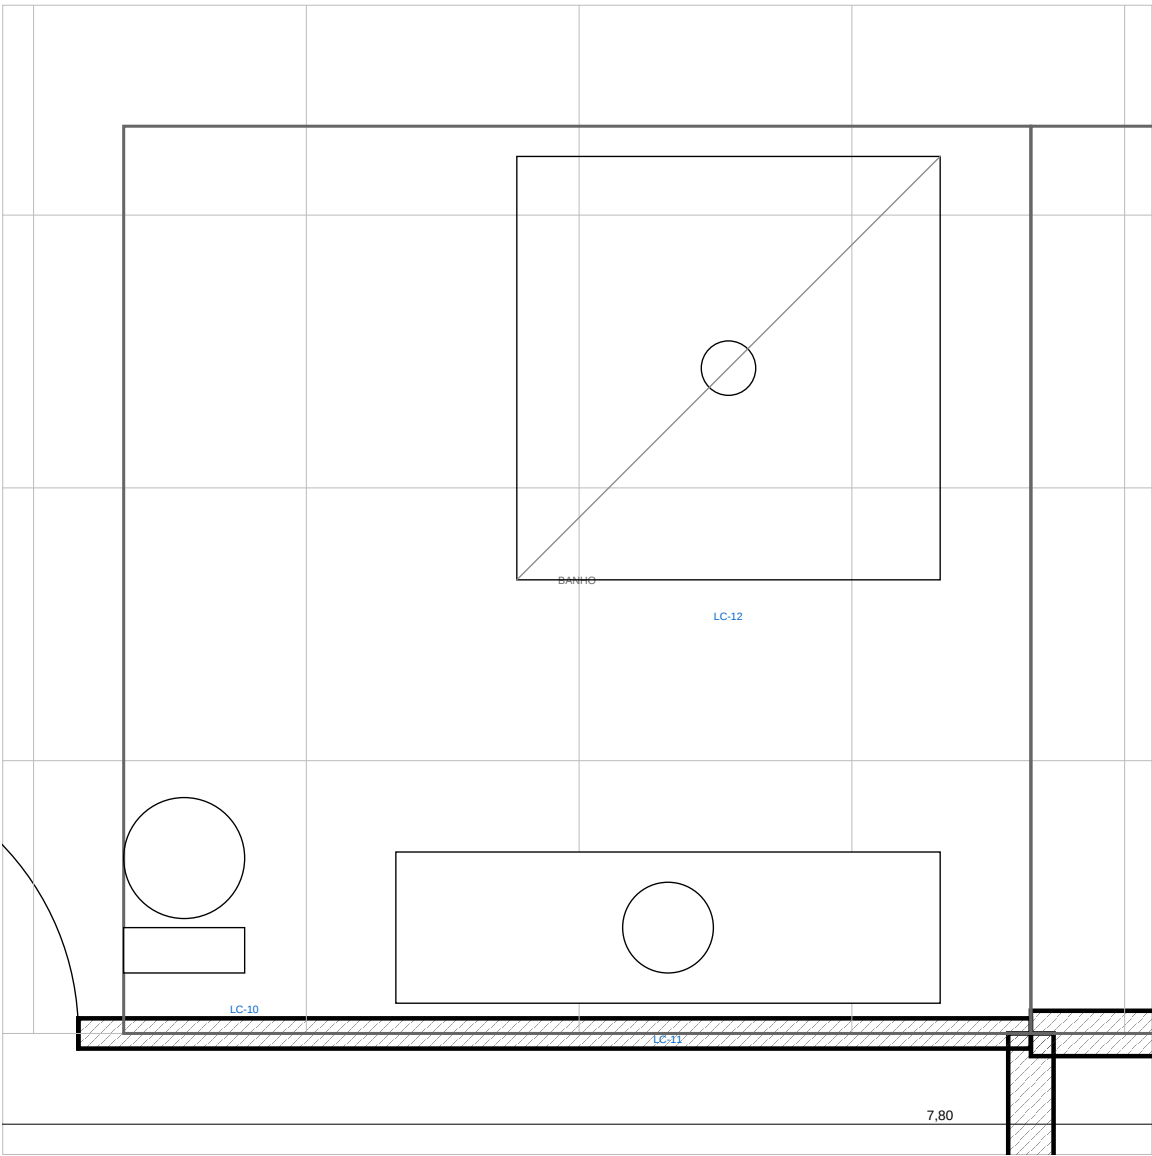

3 MASTER — BANHO
ESCALA 1:25

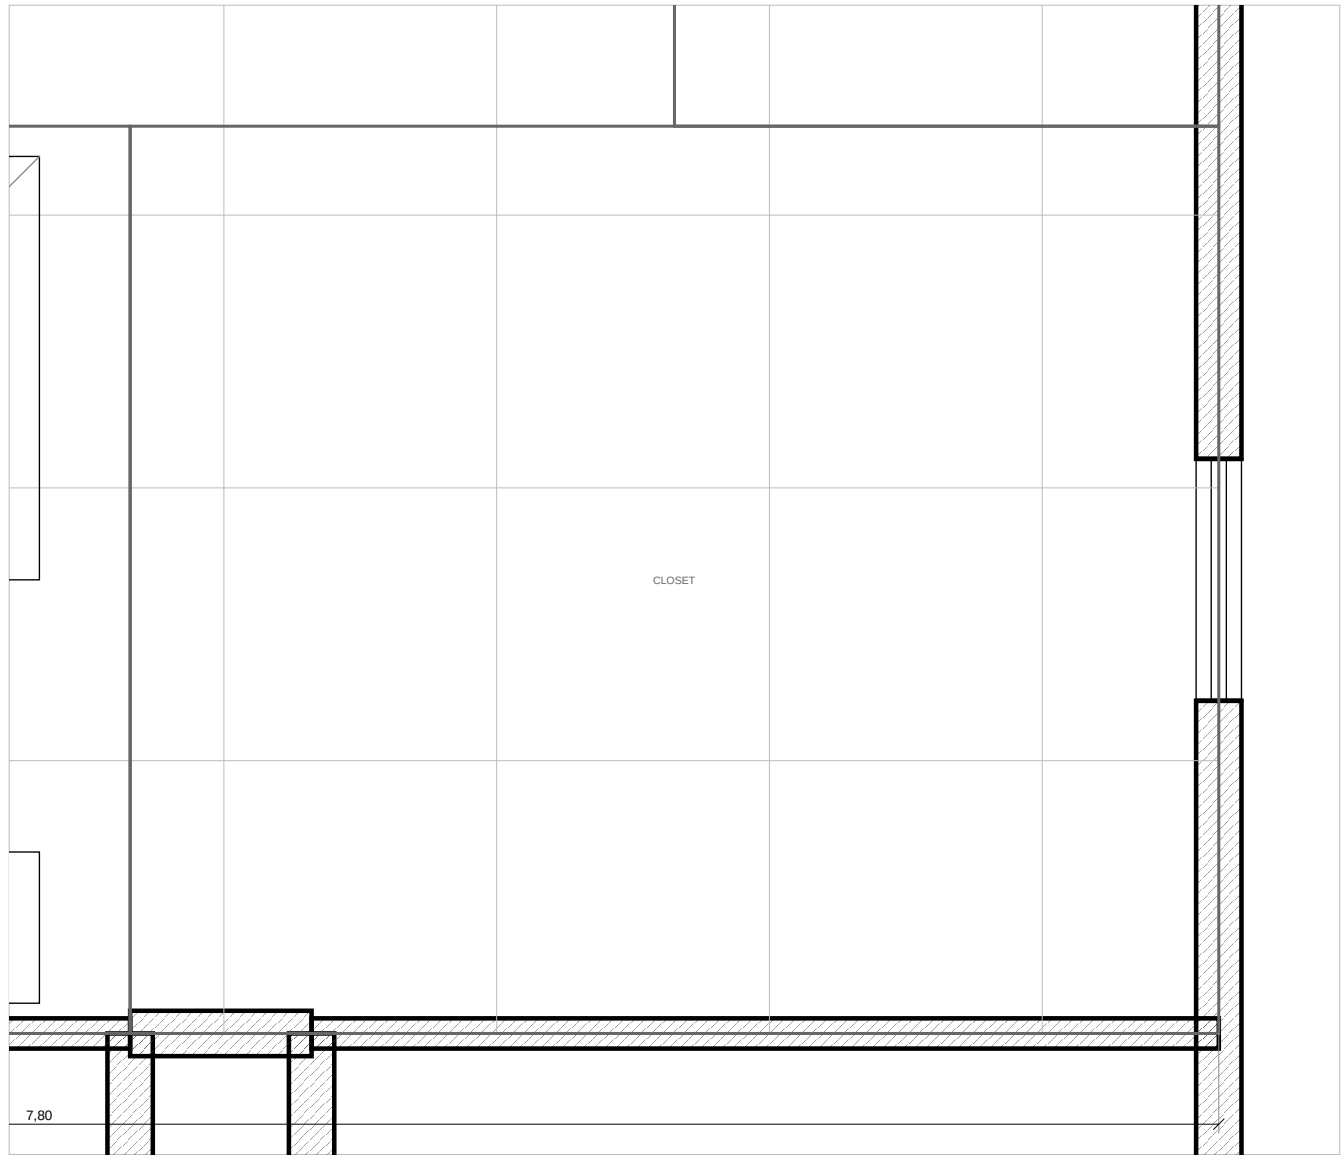

4 MASTER — CLOSET
ESCALA 1:25

PAGINACAO VERIFICADA — PECAS INTEIRAS + RECORTE EM CADA PONTA

AMB	AMBIENTE	ZONA	PEÇA	EXO X	EXO Y	ALTURA (mm)
S-002	SUITE 02 — BANHO	ZP-3	CH-02	S-002B	S-002B	—
S-003	SUITE 03 — BANHO	ZP-3	CH-03	S-003B	A-003D01	—
S-005	MASTER — BANHO	ZP-2	CH-01	S-005B	S-005B	—
S-006	MASTER — CLOSET	ZP-2	CH-01	S-006B	S-006B	—

- NOTAS
- * Pignoneus de piso em linha fina, a malha vem da ZONA de pignoneus, não do canto do ambiente.
 - * Peca de piso porcelanado retificado 300 x 300, parede ceramico retificado 300 x 600, jato 2 mm.
 - * Cimento de 1:3 para o piso em toda area molhada, soltura elevada 15 mm nos bicos.
 - * Representação: manta lquida em 2 demãos, subido 300 mm na parede e 1.800 mm nos bicos.

PROJETO PORTO REAL

RESIDENCIA UNIFAMILIAR (MANAUS - AM) | SUITE TUPA-M-01

PROJETO ARQUITETONICO

AMPLIACOES DE AREA MOLHADA — SUPERIOR

BASE GEOMETRICA Linha Consolidada Projeto (previsão) UNIDADE: METROS - MM	ESCALA 1:25 FORMATO A1 MILIMETROS (MM)	EMISSAO ESTUDIO PRELIMINAR R44 Linha LIBERADO PARA OBRA SEM ART / RNT	PROJETO 23 06-25 REV R44
--	---	--	--------------------------------