
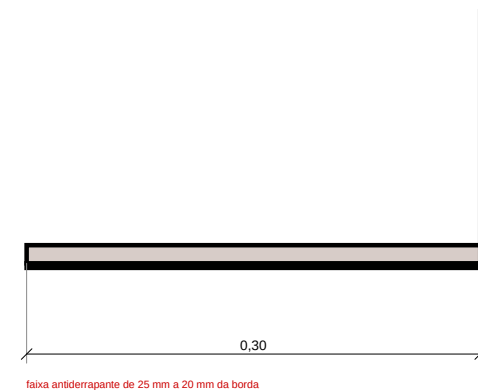
 
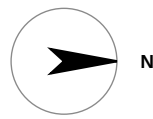


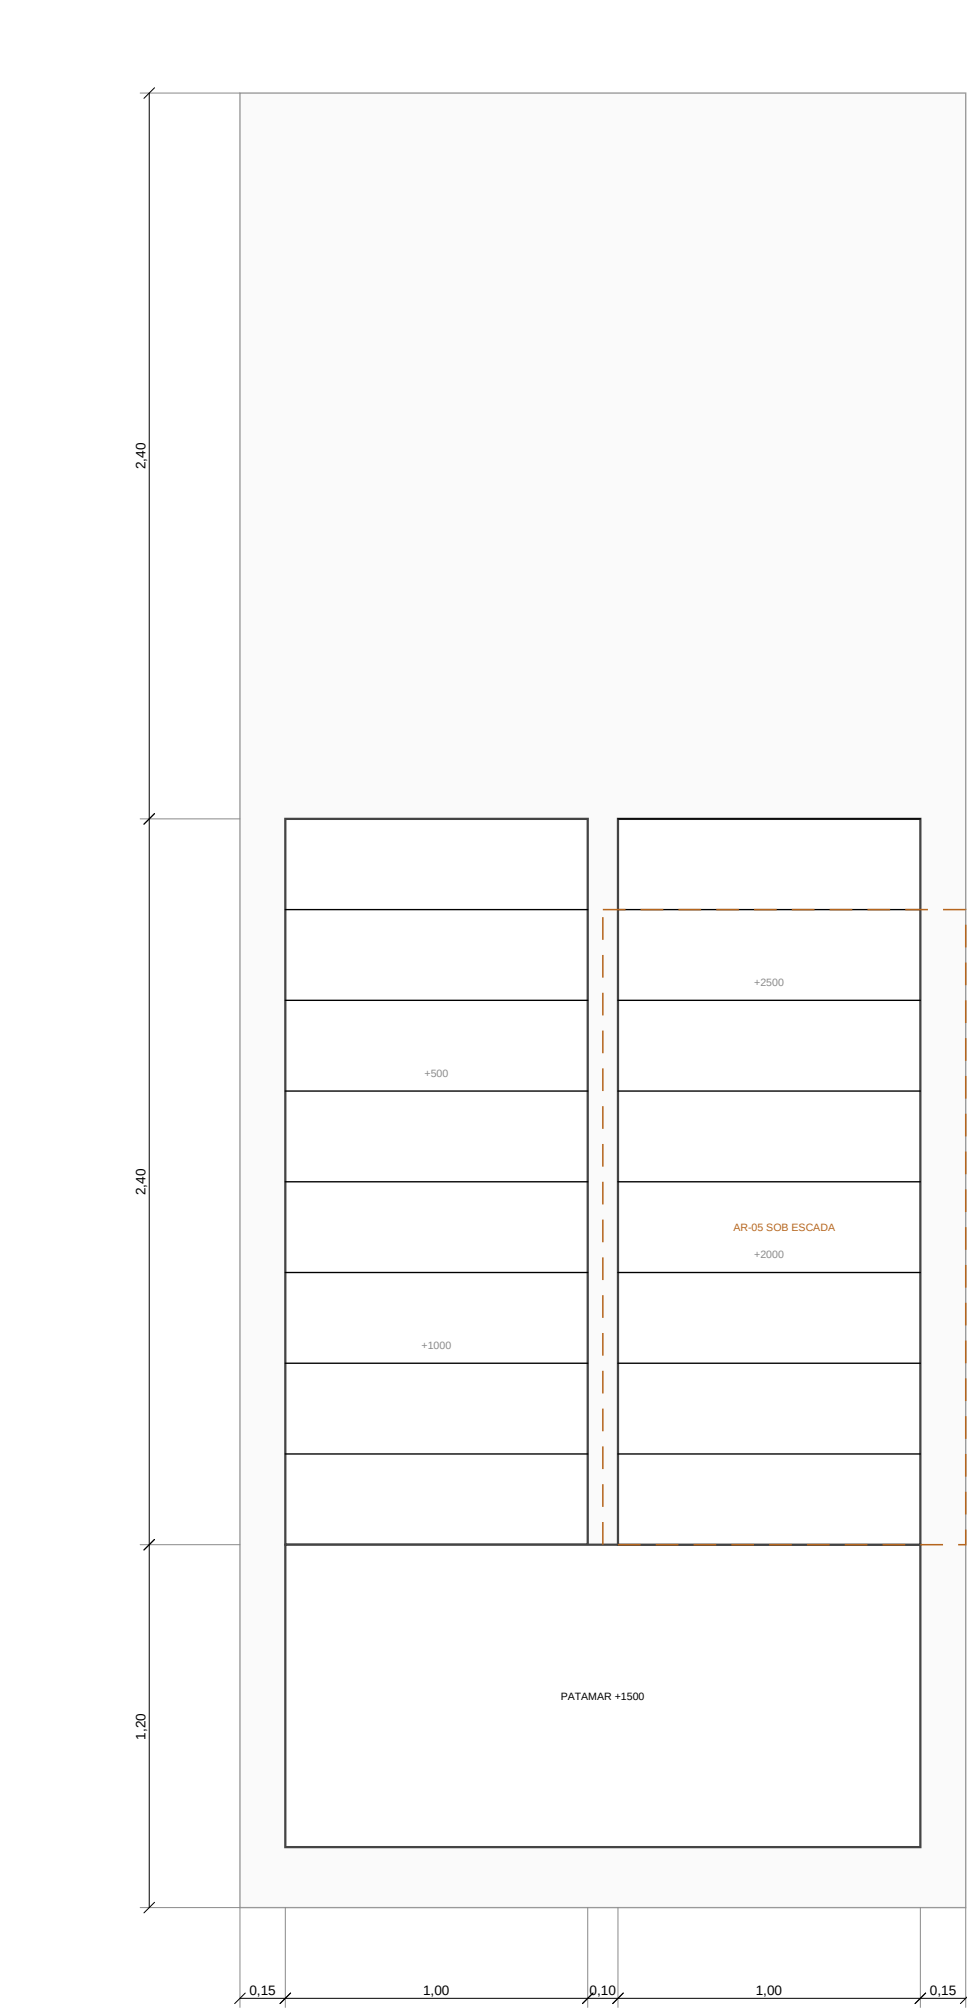

espelho fechado (NBR 9050)

chapa 80x80x3 mm - preenchido 90x x 300

1 PLANTA DA ESCADA

ITEM	PROJETO	NORMA	
Espelho	186,67 mm	18 a 18 cm (NBR 9077)	OK
Piso	300 mm	min 28 cm	OK
Bondex (2h + g)	633,3 mm	600 a 650 mm	OK
Largura útil do lance	1000 mm	min 1.200 mm (para edifícios) e 1.300 mm (para edifícios)	OK
Platamar	1000 mm	min largura do lance	OK
Altura livre mínima	0 mm	min 2100 mm	EXCETO
Guarda-corpo	1100 mm	min 1.200 mm (NBR 14738)	OK
Corrimão	920 x 700 mm	Acabado 92 cm x 70 cm (NBR 9050)	OK
Espelho fechado	sem	conformidade com esta norma	OK
Desnível vencido	3000 mm	18 x 186,67 mm	OK

O QUE A PLANTA NAO MOSTRA

QUESTAO	RESPOSTA
Por que o primeiro espelho sobre o y é 18,67?	o primeiro espelho sobre o y é 18,67 mm de altura livre, com 1.000 mm de altura livre — visto que a altura da calçada do quem termina o primeiro lance
Por que a verificação de altura livre é bidimensional?	altura livre da escada e o único critério que não aparece em planta horizontal, dependendo da cor do degrau e da cor do que há acima dele
O que há sob o segundo lance?	intergap com altura útil variável, destinada como amparo (NBR 9050) mas a circulação tem espaço livre
Por que espelho fechado?	degrau visado desde a porta do por de quem está chegando ou tem mobilidade reduzida (NBR 9050)
Por que corrimão duplo?	920 mm para adulto e 700 mm para criança, em caso com escada aberta para a sala, o segundo corrimão é o que realmente se usa

- NOTAS
- 18 espelho de 186,67 mm e piso de 300 mm. Bondex 2h + g = 633,3 mm (linha recomendada 600 a 650).
 - Altura livre mínima 2100 mm (NBR 9077), verificada desde o degrau contra a tape e o resto acima.
 - Guarda-corpo 1100 mm, corrimão duplo em 920 x 700 mm (NBR 9050).
 - dois perfis U 200 laterais com degraus em chapa aluminada 3 mm.

PROJETO PORTO REAL

RESIDENCIA UNIFAMILIAR (MARAUAS - AM) | 50x25 TATIANA-PS

PROJETO ARQUITETONICO

ESCADA — DESENHO EXECUTIVO

BASE GEOMETRICA	ESCALA	EMISSAO	PROJETO
União Consolidada	indicada	ESTUDIO PRELIMINAR R44	
ISO 1572 (previável)	FORMATO A1	NAO LIBERADO PARA OBRA	25
UNIDADE: METROS - MM	MILIMETROS (50/100)	SEM ART / RNT	06-25 REV R44