


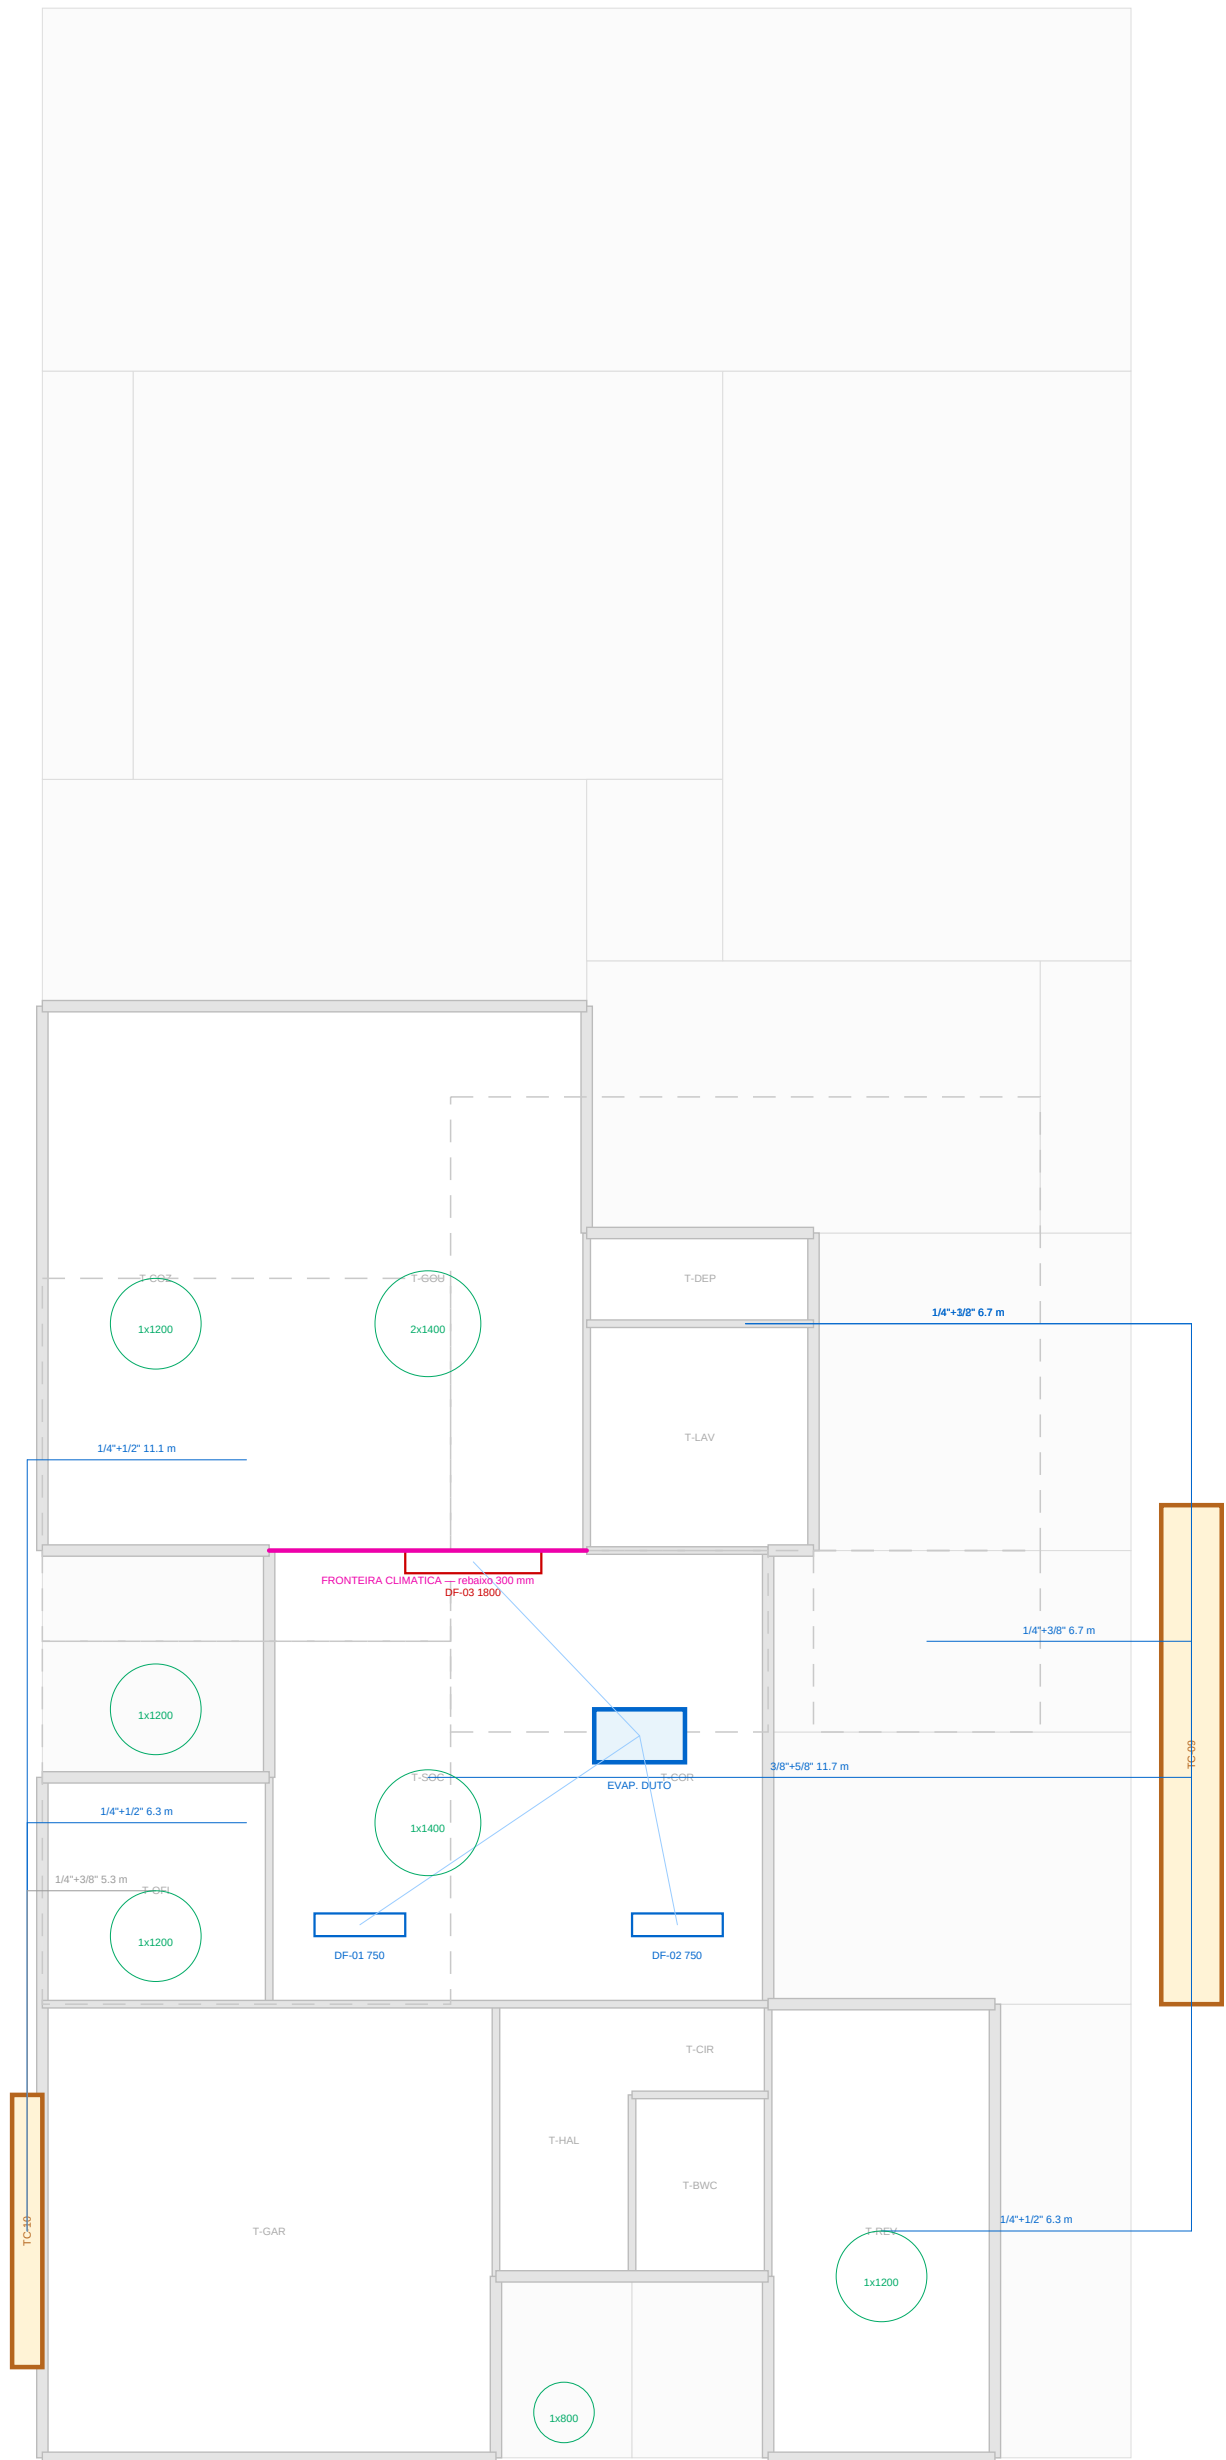

1 PERCURSO DAS LINHAS E DUTOS
ESCALA 1:100

LINHAS FRIGORÍGENAS — PERCURSO E BITOLA

Linha	AMB	INCHO	BTU/h	HORIZ (m)	VERT (m)	TOTAL (m)	SUCCASÃO	DRENO	CARGA EXTRA	FASE
S-MA5	S-MA5	TC-09	18.000	1,6	3,8	6,7	1/4" x 1/2"	DN25	—	ABR
T-REV	T-REV	TC-09	18.000	2,2	2,6	6,3	1/4" x 1/2"	DN25	—	ABR
S-SE2	S-SE2	TC-10	18.000	1,2	3,8	6,3	1/4" x 1/2"	DN25	—	ABR
S-SE3	S-SE3	TC-10	18.000	6,0	3,6	11,1	1/4" x 1/2"	DN25	R2 g	ABR
S-SDC	T-SDC	TC-08	20.000	1,6	2,8	11,7	3/8" x 1/2"	DN25	R2 g	ABR
S-UDV	S-UDV	TC-09	9.000	1,6	3,8	6,7	1/4" x 3/8"	DN25	—	ABR
PFCE	S-MA5	TC-09	9.000	1,6	3,8	6,7	1/4" x 3/8"	DN25	—	ABR
T-OR	T-OR	TC-10	9.000	1,2	2,8	9,3	1/4" x 3/8"	DN25	—	ABR

DUTOS, DIFUSORES E EXAUSTÃO

ELEMENTO	VIAJADA (m)	DNSE	OBSERVAÇÃO
DP-02 — insuflamento	750	T-SDC	gosto, parede sobre do motor
DP-02 — insuflamento	750	T-COR	com, sob o piso de luz

(continuação)

ELEMENTO	VIAJADA (m)	DNSE	OBSERVAÇÃO
EX-02 — banho mulher	85	T-RENC	DN200
EX-02 — banheiro	105	T-OR	DN200, rede unificada da cozinha e da cozinha
EX-02 — banho homem	125	S-MA5	DN200
EX-02 — banho homem	85	S-MA5	DN200, rede unificada da cozinha e da cozinha

- NOTAS
- Dots rictos de condensação. Linha mais longa 11,7 m, contra o limite de contorno de 15 m.
 - Drenos DN25 com calçamento mínimo de 2% e altura antes da descarga, nunca ligado a engoto sem alho.
 - Duto de insuflamento no comprimento de 400 m — nunca abreviar montado.
 - Isolamento contínuo na travessa de parede, com bucha de passagem; caso de isolamento na parede condensa dentro do montado.

PROJETO PORTO REAL

RESIDENCIA UNIFAMILIAR (MANUS - AM) (SUS TATIANA-PS)

PROJETO ARQUITETONICO

CLIMATIZACAO — LINHAS FRIGORIGENAS, DUTOS E DRENOS

BASE GEOMETRICA Linha Consolidada PROJETO (previsão) UNIDADE METRICA: mm	ESCALA 1:100 FORMATO A1 MILHA 655/555/555	EXATIDÃO ESTUDO PRELIMINAR R44 TWO LIBERADO PARA DESA SEM ART / INT	PROVA 28 06-25 REV R44
---	---	--	-------------------------------------