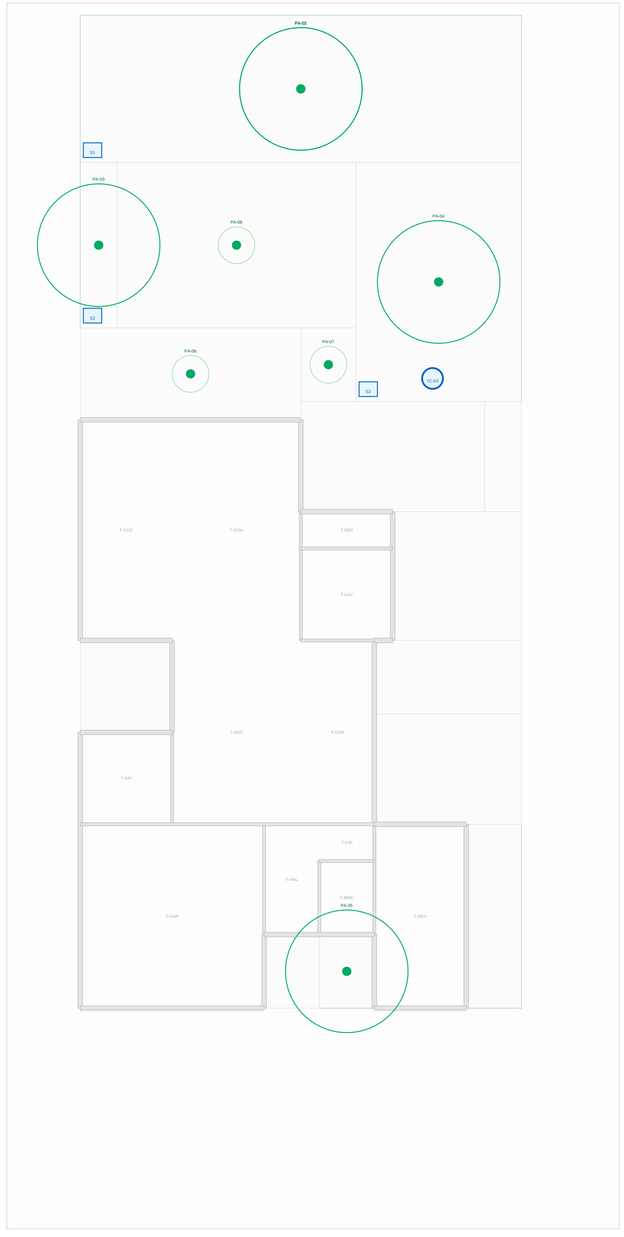


N

ESPECIES E FUNCAO

COD	AMB	ESPECIE	PORTE	QTD	FUNCAO	RAIZ	AFAST (mm)	CANTEIRO
PA-01	T-JFU	Ipe-amarelo (Handroanthus)	8 a 12 m	1	sombra alta no fundo e floracao de estacao	pivotante, nao agressiva	3000	4800
PA-02	T-JFU	Jabuticabeira (Plinia cauliflora)	6 a 9 m	1	sombra densa e fruto no proprio tronco	nao agressiva, crescimento lento	3000	4800
PA-03	T-JS2	Vasos com Sansevieria e Zamioculca	0,8 a 1,2 m	9	massa verde na faixa sul de 1.800 mm, sem canteiro com	em vaso	300	1200
PA-04	T-JN3	Palmeira-acai (Euterpe oleracea)	10 a 15 m	3	verticalidade e sombra pontual no jardim norte	fasciculada, proxima ao tronco	1500	5400
PA-05	T-JLE	Vasos com Formio e Agave	0,6 a 1,0 m	6	jardim de inverno leste, visto do banho	em vaso	300	1800
PA-06	T-ALP	Horta aromatica em vasos elevados	0,4 a 0,8 m	6	alecrim, manjericao e capim-limao na varanda, a dois pas	em vaso	300	3000
PA-07	T-JN2	Seixo rolado claro e vasos	—	3	acabamento permeavel sob a varanda, onde nao chega chuva	em vaso	0	1800
PA-08	T-DKP	Piso drenante claro	rasteira	0	permeabilidade e albedo alto no entorno do deck, no luga	—	0	5400

IRRIGACAO

ITEM	VALOR	RAZAO
Sistema	gotejamento em linha autocompensante, 2 L/h por gotejador	autocompensante mantem vazao igual em toda a linha, inclusive em declive
Setores	3 x 240 L/h	setorizar permite regar sombra e sol em tempos diferentes
Tempo e frequencia	20 min, 2 x por semana	rega profunda e espacada cria raiz funda; rega diaria cria raiz rasa
Demanda media	66.6 L/dia	antes era estimativa de 100 L/dia; agora e consequencia dos setores
Fonte	reservatorio pluvial TC-03, por gravidade com filtro de 130 mesh	gravidade dispensa bomba; filtro evita entupir gotejador
Por que gotejamento	gotejamento e nao aspersao: evapora menos, nao molha fachada e nao leva	aspersao perderia metade para evaporacao e molharia a fachada
Area de jardim	137.16 m2	0.50 L/m2 por dia

BALANCO DO REUSO — ATUALIZADO

ITEM	VALOR
Area de captacao (projecao coberta)	265.68 m2
Captacao anual liquida	522.46 m3
Demanda diaria total	237.6 L/dia
Demanda anual	86.72 m3
Aproveitamento da chuva captado	17%
Autonomia do reservatorio	10.5 dias
Volume adotado	2500 L
Restricao de uso	vasos sanitarios

1 **PAISAGISMO — IMPLANTACAO**
ESCALA 1:100

NOTAS

- Paisagismo aqui e a ultima camada do projeto termico: a arvore sombreia ANTES de o sol chegar na parede, e transpira em vez de reirradiar.
- Em faixa de 1.800 mm nao cabe arvore: a copa invade o vizinho e a raiz encontra o radier. Ali a sombra vem de trelica e sebe.
- Irrigacao: gotejamento em linha autocompensante, 2 L/h por gotejador, 3 setores, 66.6 L/dia em media.
- Fonte: reservatorio pluvial TC-03, por gravidade com filtro de 130 mesh

PROJETO PORTO REAL

RESIDENCIA UNIFAMILIAR | MANAUS - AM | SUSI TARUMA (H)

PROJETO ARQUITETONICO

PAISAGISMO E IRRIGACAO

BASE GEOMETRICA	ESCALA	EMISSAO	PRANCHA
Lista Consolidada pos-R32 (prevalece)	1:100	ESTUDO PRELIMINAR R44	32
UNIDADE MESTRE: mm	FORMATO A3 MALHA 600/300/150	NAO LIBERADO PARA OBRA SEM ART / RRT	de 35 REV R44