
 
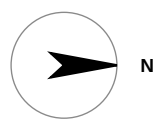


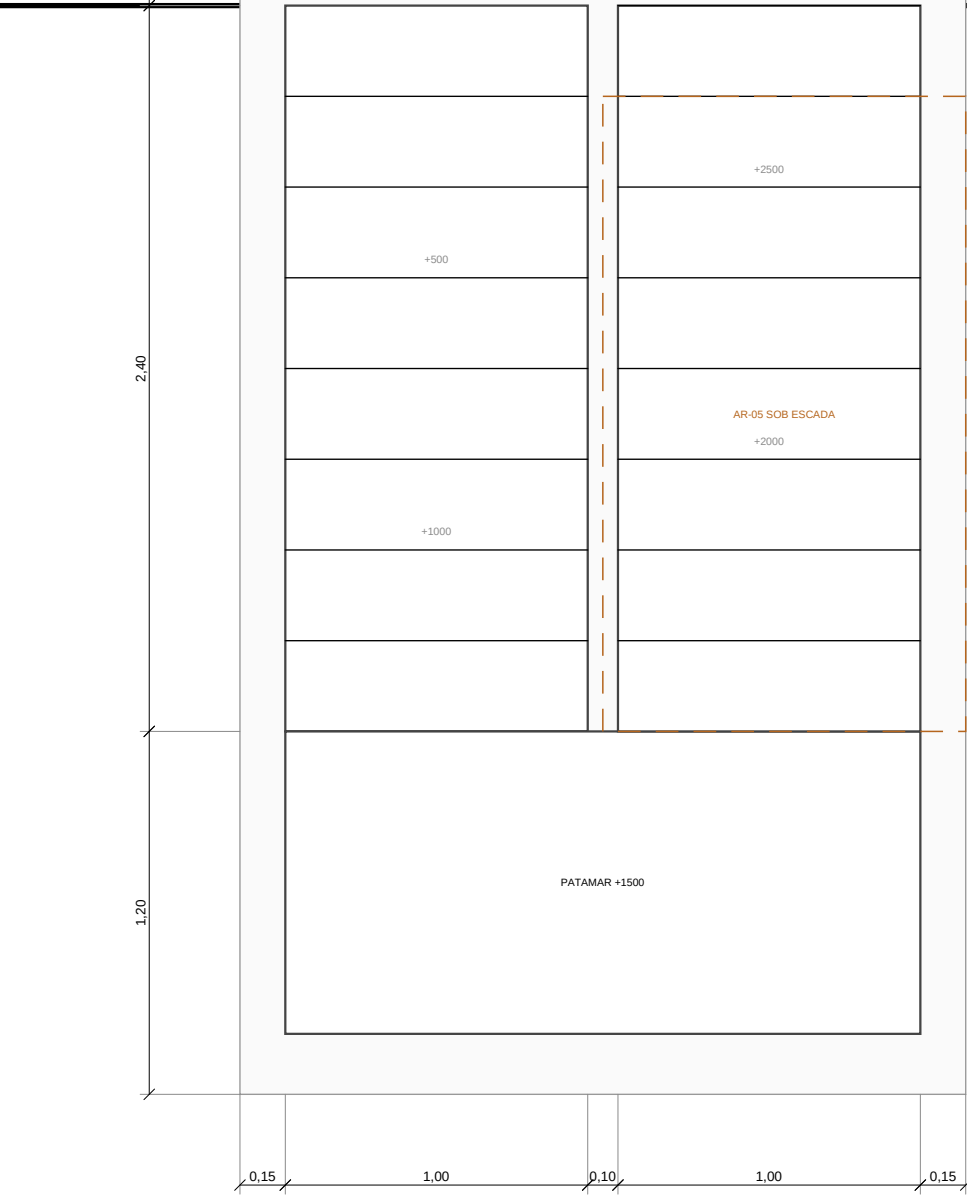

espelho fechado (NBR 9050)

chapa 800x400 3 mm + preenchido 900 x 300

faixa antideslizante de 25 mm x 25 mm de borda

2 CORTE LONGITUDINAL — ALTURA LIVRE

ESCALA 1:25

3 DETALHE DO DEGRAU

ESCALA 1:5

VERIFICACAO DA ESCADA

ITEM	PROJETO	NORMA	
Espelho	186.67 mm	18 a 18 cm (NBR 9071)	OK
Piso	300 mm	min 28 cm	OK
Bondex (2h + g)	633.3 mm	600 a 650 mm	OK
Largura útil do lance	1000 mm	min 1.200 mm (uso coletivo) / 1.000 mm (particular)	OK
Platamar	1000 mm	→ largura do lance	OK
Altura livre mínima	0 mm	min 2100 mm	EXCETO
Guarda-corpo	1100 mm	min 1.200 mm (NBR 14738)	OK
Corrimão	920 a 1000 mm	Acima 92 cm e 10 cm (NBR 9050)	OK
Espelho fechado	sem	conformidade com esta norma	OK
Desnível vencido	3000 mm	18 a 186.67 mm	OK

O QUE A PLANTA NAO MOSTRA

QUESTAO	RESPOSTA
Por que o primeiro espelho sobre o x e y é 1.8.000?	o primeiro espelho sobre o x e y é 1.8.000 mm de altura livre — visto que a altura da calçada de quem sobe o primeiro lance
Por que a verificação de altura livre é bidimensional?	altura livre da escada e o único critério que não aparece em planta horizontal, depende da cota do degrau e da cota do que há acima dele
O que há sob o segundo lance?	intergalo com altura variável, dimensionado como amarrado (NBR 9050) mas a circulação tem espaço livre
Por que espelho fechado?	alguma vez você prende a porta do por de quem usa largura ou tem mobilidade reduzida (NBR 9050)
Por que corrimão duplo?	920 mm para adulto e 700 mm para criança, em caso com escada aberta para a sala, o segundo corrimão é o que realmente se usa

NOTAS

- 18 espelho de 186.67 mm e piso de 300 mm. Bondex 2h + g = 633.3 mm (falso recomendado 600 a 650).
- Altura livre mínima 2100 mm (NBR 9071), verificado degrau a degrau contra a tija e o vazio acima.
- Guarda-corpo 1100 mm, corrimão duplo em 920 e 700 mm (NBR 9050).
- dois porões 1.200 mm com degrau em chapa antiderrapante 3 mm.

PROJETO PORTO REAL

RESIDENCIA UNIFAMILIAR (MANSÃO - AM) | SOUS TATIANA-PS

PROJETO ARQUITETONICO

ESCALA — DESENHO EXECUTIVO

BASE GEOMETRICA	ESCALA	EMISSAO	PROJECION
Unidade Consolidada	indicada	ESTUDIO PRELIMINAR	25
Projeto (previsão)	FORMATO A1	NAO LIBERADO PARA OBRA	05.25
UNIDADE: METRO - MM	MILHA 400/500/600	SEM ART / RNT	