



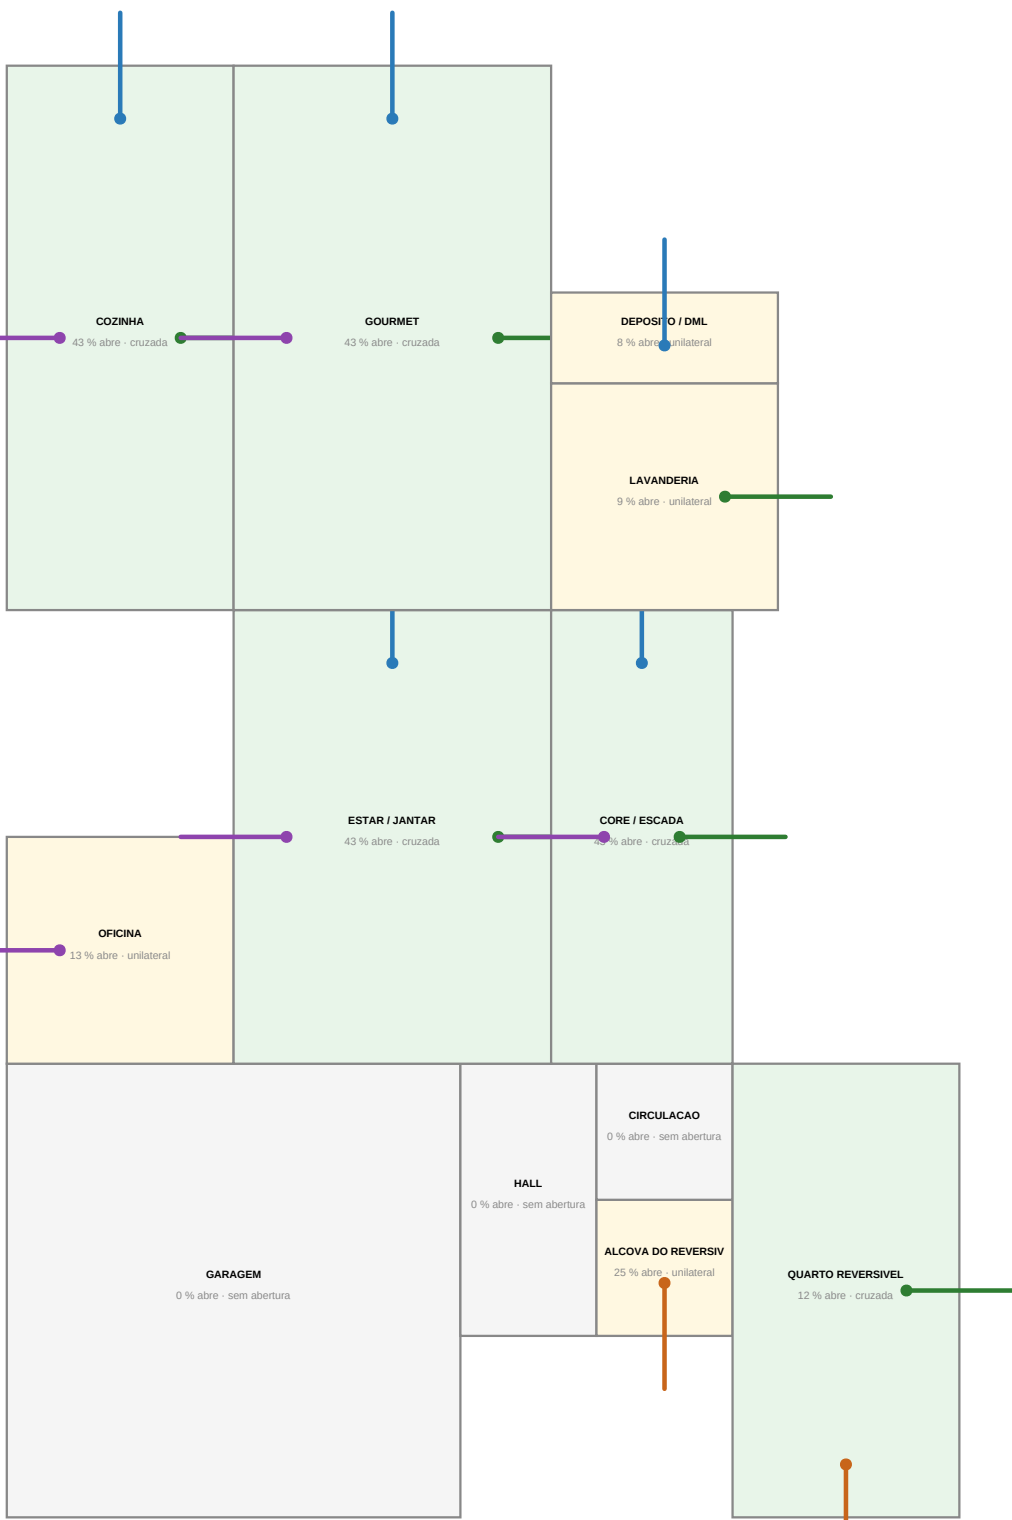

1 TERREO — faces que abrem
ESCALA 1:100

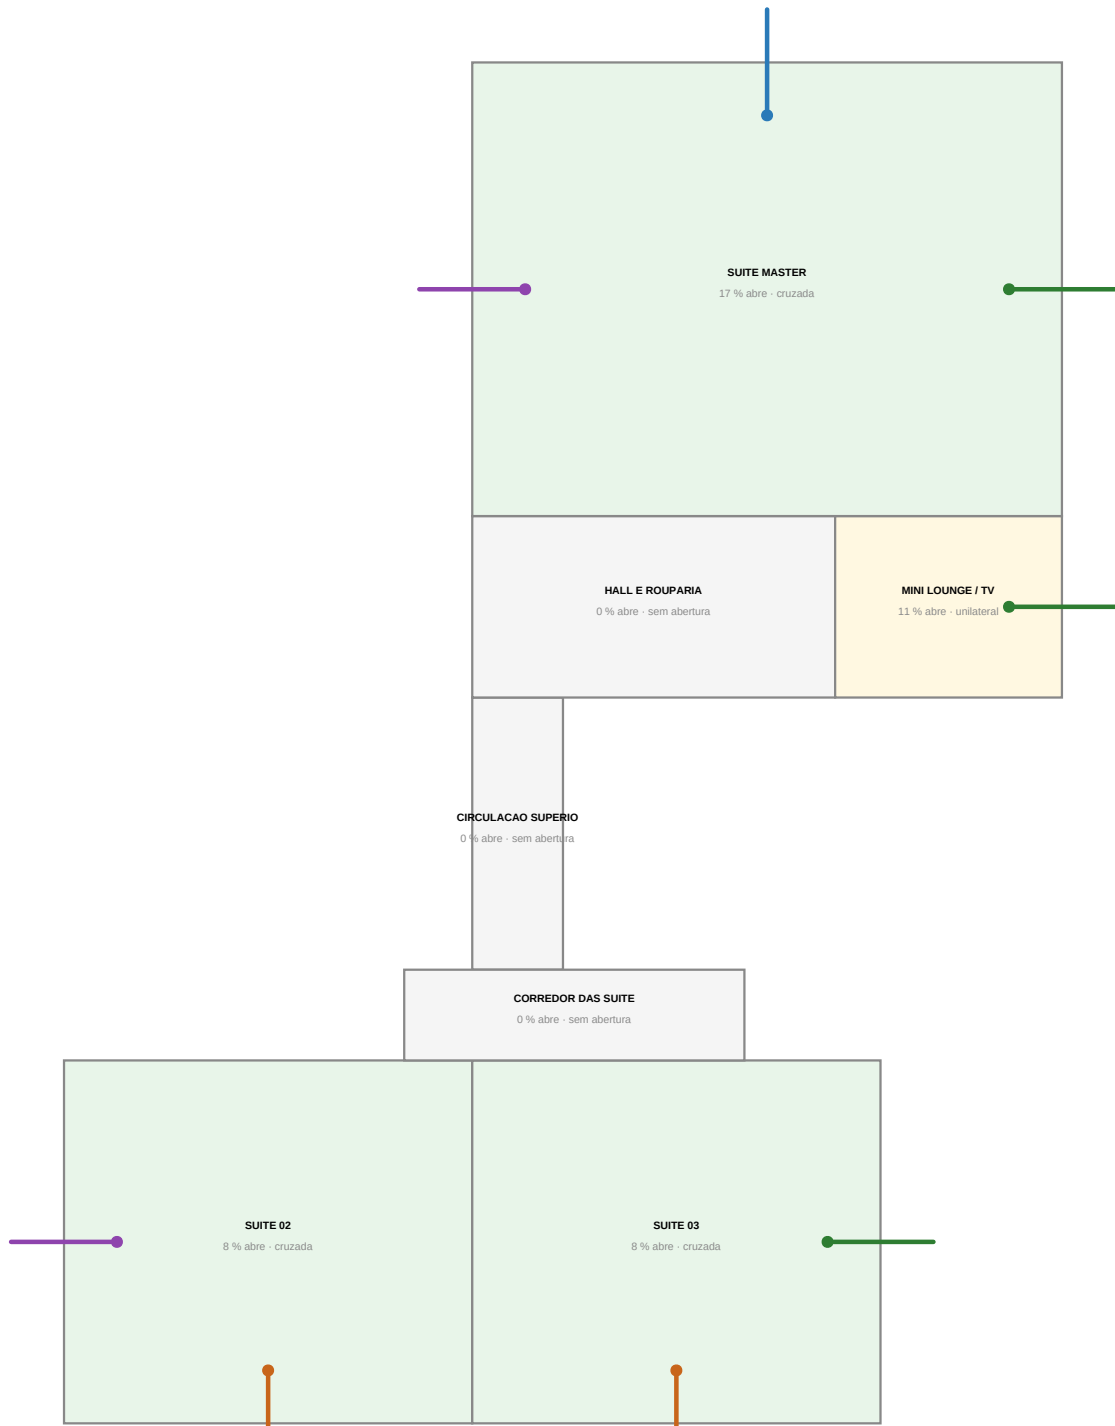

2 SUPERIOR — faces que abrem
ESCALA 1:100

VENTILACAO POR AMBIENTE

COD	AMBIENTE	CAT.	PROJE	ABREJE	PERIM	FACES	TIPO	STATUS
T-001	COZINHA	INTERIO	34,3	0,00	0%	—	—	YES
T-002	HALL	INTERIO	9,8	0,00	0%	—	—	YES
T-003	ALCOVA DO REVERSIVEL	INTERIO	2,8	0,72	25%	L	unidirecional	OK
T-004	CIRCULACAO	INTERIO	2,8	0,00	0%	—	—	YES
T-005	QUARTO REVERSIVEL	INTERIO	26,7	2,04	22%	L, N	cruzada	OK
T-006	OFICINA	INTERIO	43	1,08	23%	S	unidirecional	YES
T-007	ESTAR/JANTAR	INTERIO	86,7	36,86	42%	N, D, S	cruzada	OK
T-008	CORR. ESCADA	INTERIO	86,7	36,86	42%	N, D, S	cruzada	YES
T-009	COZINHA	INTERIO	86,7	36,86	42%	N, D, S	cruzada	OK
T-010	GOURMET	INTERIO	86,7	36,86	42%	N, D, S	cruzada	OK
T-011	LAVANDERIA	INTERIO	8,3	0,72	9%	N	unidirecional	YES
T-012	DEPOSITO DmL	INTERIO	3,1	0,24	8%	O	unidirecional	YES
S-001	SUITE 02	INTERIO	26,5	2,04	8%	L, S	cruzada	OK
S-002	SUITE 03	INTERIO	26,7	2,04	8%	L, N	cruzada	OK
S-003	CIRCULACAO SUPERIOR	INTERIO	3,8	0,00	0%	—	—	YES
S-004	CORREDOR DAS SUITES	INTERIO	4,6	0,00	0%	—	—	YES
S-005	HALL E ROUPARIA	INTERIO	10,6	0,00	0%	—	—	YES
S-006	MINI LOUNGE / TV	INTERIO	9,5	0,72	11%	N	unidirecional	OK
S-007	SUITE MASTER	INTERIO	44,9	7,60	17%	N, D, S	cruzada	OK

PRIVACIDADE — CADA JANELA CONTRA A DIVISA QUE OLHA (art. 1.301 CC)

VAO	AMB	FACE	DIST. m	MIN. m	PROTEC.	BRSE	LEITURA	
004	T-REV	N	8,00	1,50	1500	—	distante	OK
002	T-COR	N	8,00	1,50	1500	—	distante	OK
005	T-REV	L	7,20	—	1100	BR-L	fus	OK
001	T-REV	N	8,00	1,50	1100	—	distante	OK
003	T-ALC	L	9,60	—	1000	—	fus	OK
006	T-CO1	S	3,40	1,50	1100	—	exposta ao vento	OK
001	T-CO2	S	3,40	1,50	1100	—	exposta ao vento	OK
001	T-LAV	N	7,40	1,50	1100	—	distante	OK
004	T-DEP	O	35,80	1,50	1500	—	distante	OK
P-001	T-COR	N	8,00	1,50	9	—	distante	OK
P-002	T-GOU	N	30,40	1,50	9	—	distante	OK
P-003	T-GOU	O	33,60	1,50	9	BR-O	protetida por telas	OK
P-002	T-DOC	S	5,40	1,50	9	—	distante	OK
001	S-GOU	N	4,40	1,50	1100	—	distante	OK
005	S-002	S	3,40	1,50	1100	—	exposta ao vento	OK
001	S-002	L	7,20	—	1100	BR-L	fus	OK
004	S-002	L	7,20	—	1000	BR-L	fus	OK
005	S-003	N	6,80	1,50	1100	—	distante	OK
001	S-003	L	7,20	—	1100	BR-L	fus	OK
004	S-003	N	6,80	1,50	1000	—	distante	OK
005	S-005	S	7,80	1,50	1100	—	distante	OK
P-002	S-005	O	14,80	1,50	9	—	distante	OK
004	S-005	N	4,40	1,50	1000	—	distante	OK
001	S-005	N	4,40	1,50	1100	—	distante	OK

- NOTAS
- ¹ Área que ABRE por ambiente contra a área do piso. NBR 15275-4 exige 0% na região Norte. NBR 15229-3 recomenda 40% na ZSB (abertura garantida).
 - ² Fritas que abrem por janela (JC) contra a parede lateral 200%, janela de corte 50%, basculante 33%, porta opaca 0%.
 - ³ Privacidade pelo art. 1.301 do Código Civil: janela que olha a divisa a menos de 2,50 m é proibida. O brisa que protege esta norma.
 - ⁴ Seis em cada face com abertura, duas de mais faces = ventilação cruzada.

PROJETO PORTO REAL

RESIDENCIA UNIFAMILIAR (MANSÃO - AM) | SOUS TATIANA PI

PROJETO ARQUITETONICO

VENTILACAO NATURAL, CRUZADA E PRIVACIDADE

BASE GEOMETRICA Linha Consolidada por R2D (previsão) UNIDADE MESTRE: mm	ESCALA 1:100 FORMATO A1 MILIMETROS (50/50/50)	EMISSAO ESTUDIO PRELIMINAR RIB Linha LIBERADO PARA OBRA SEM ART / RNT	PRIVACIDADE 49 em 7% REVISAO
--	---	--	---