



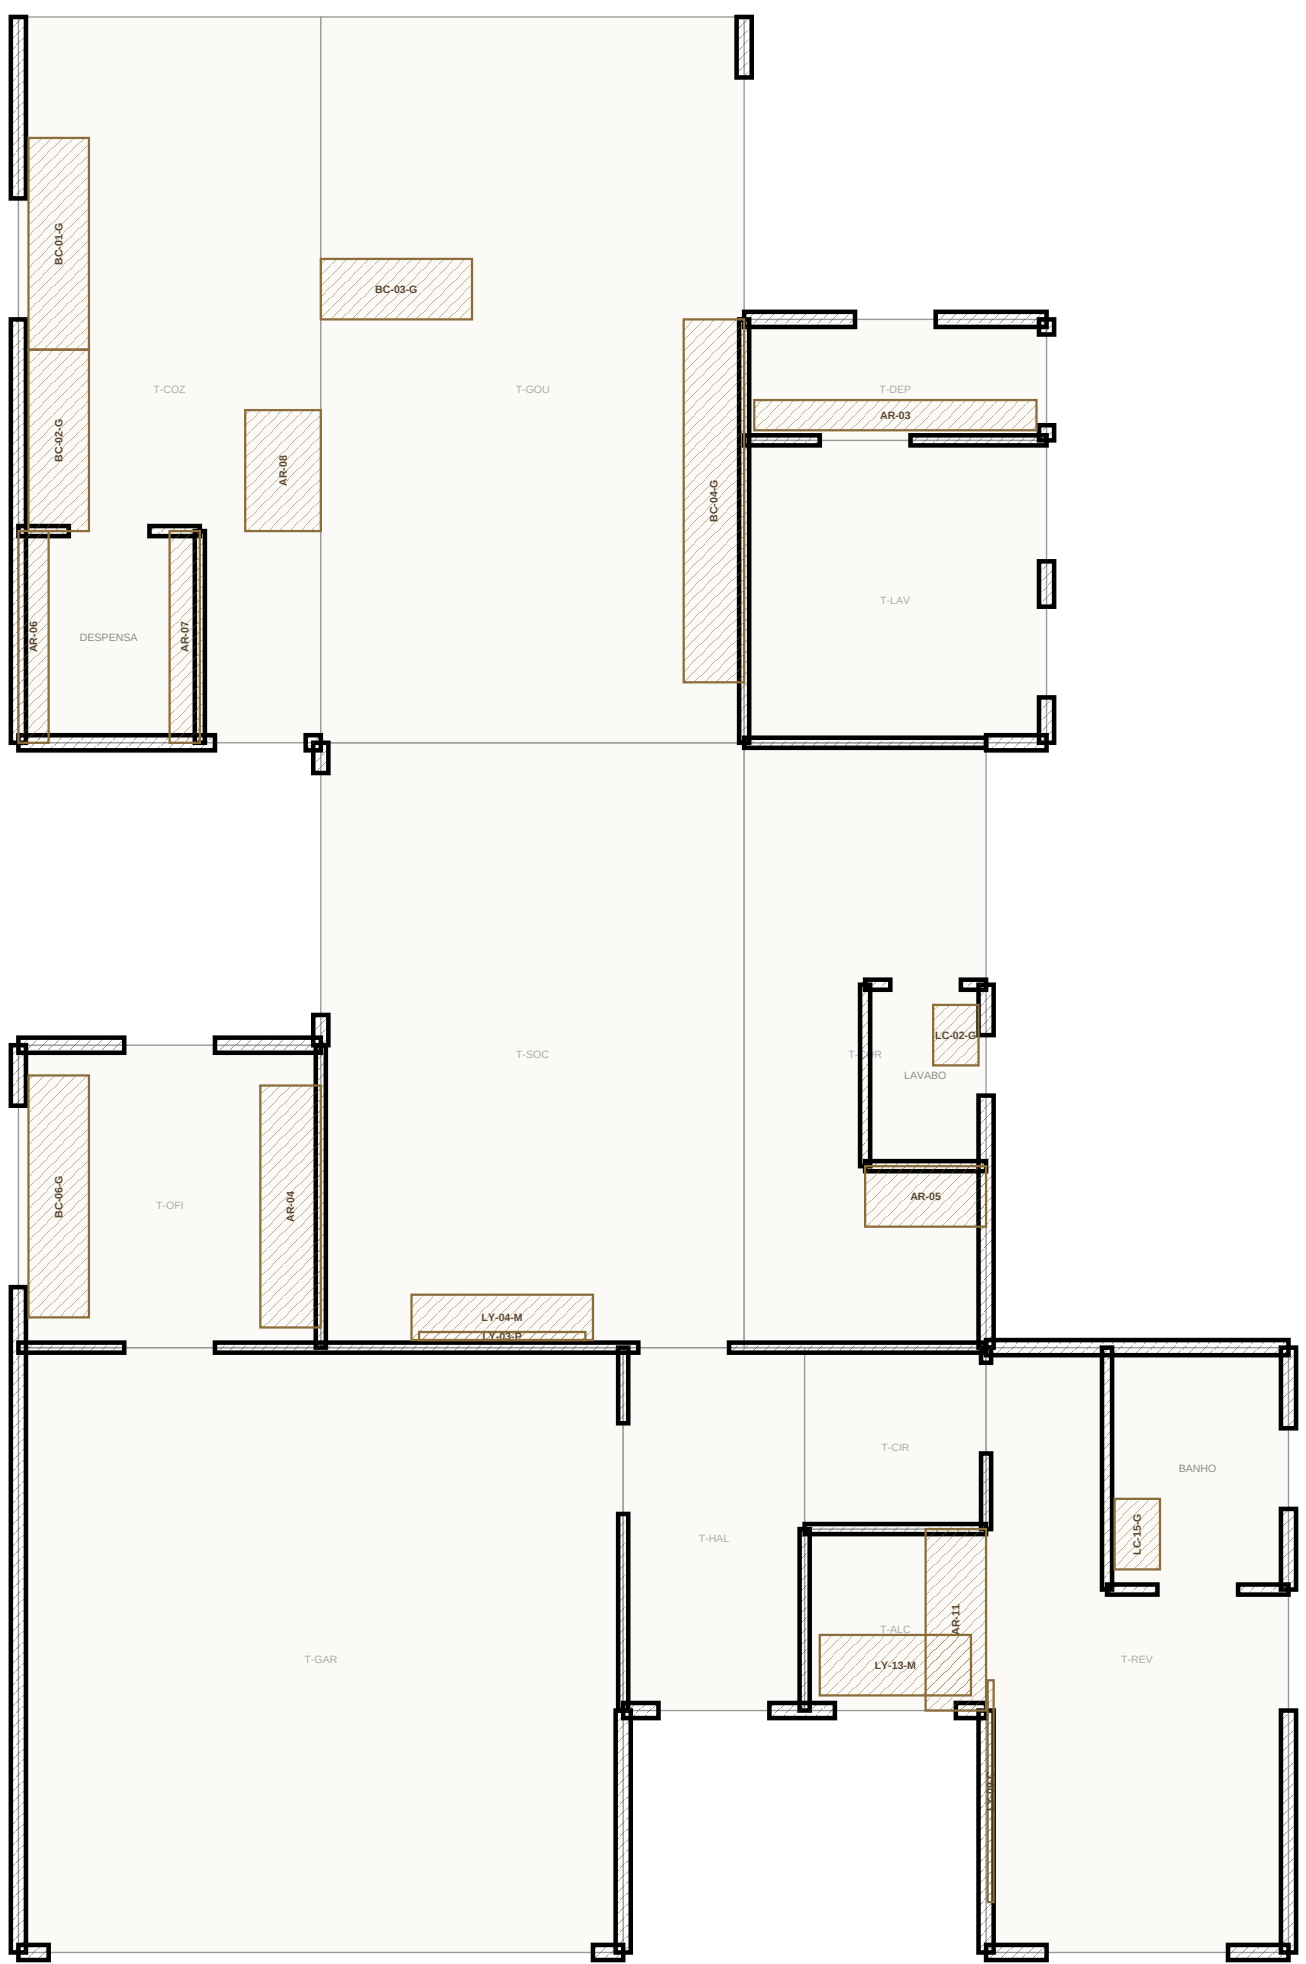

1 TERREO — MARCENARIA  
ESCALA 1:75

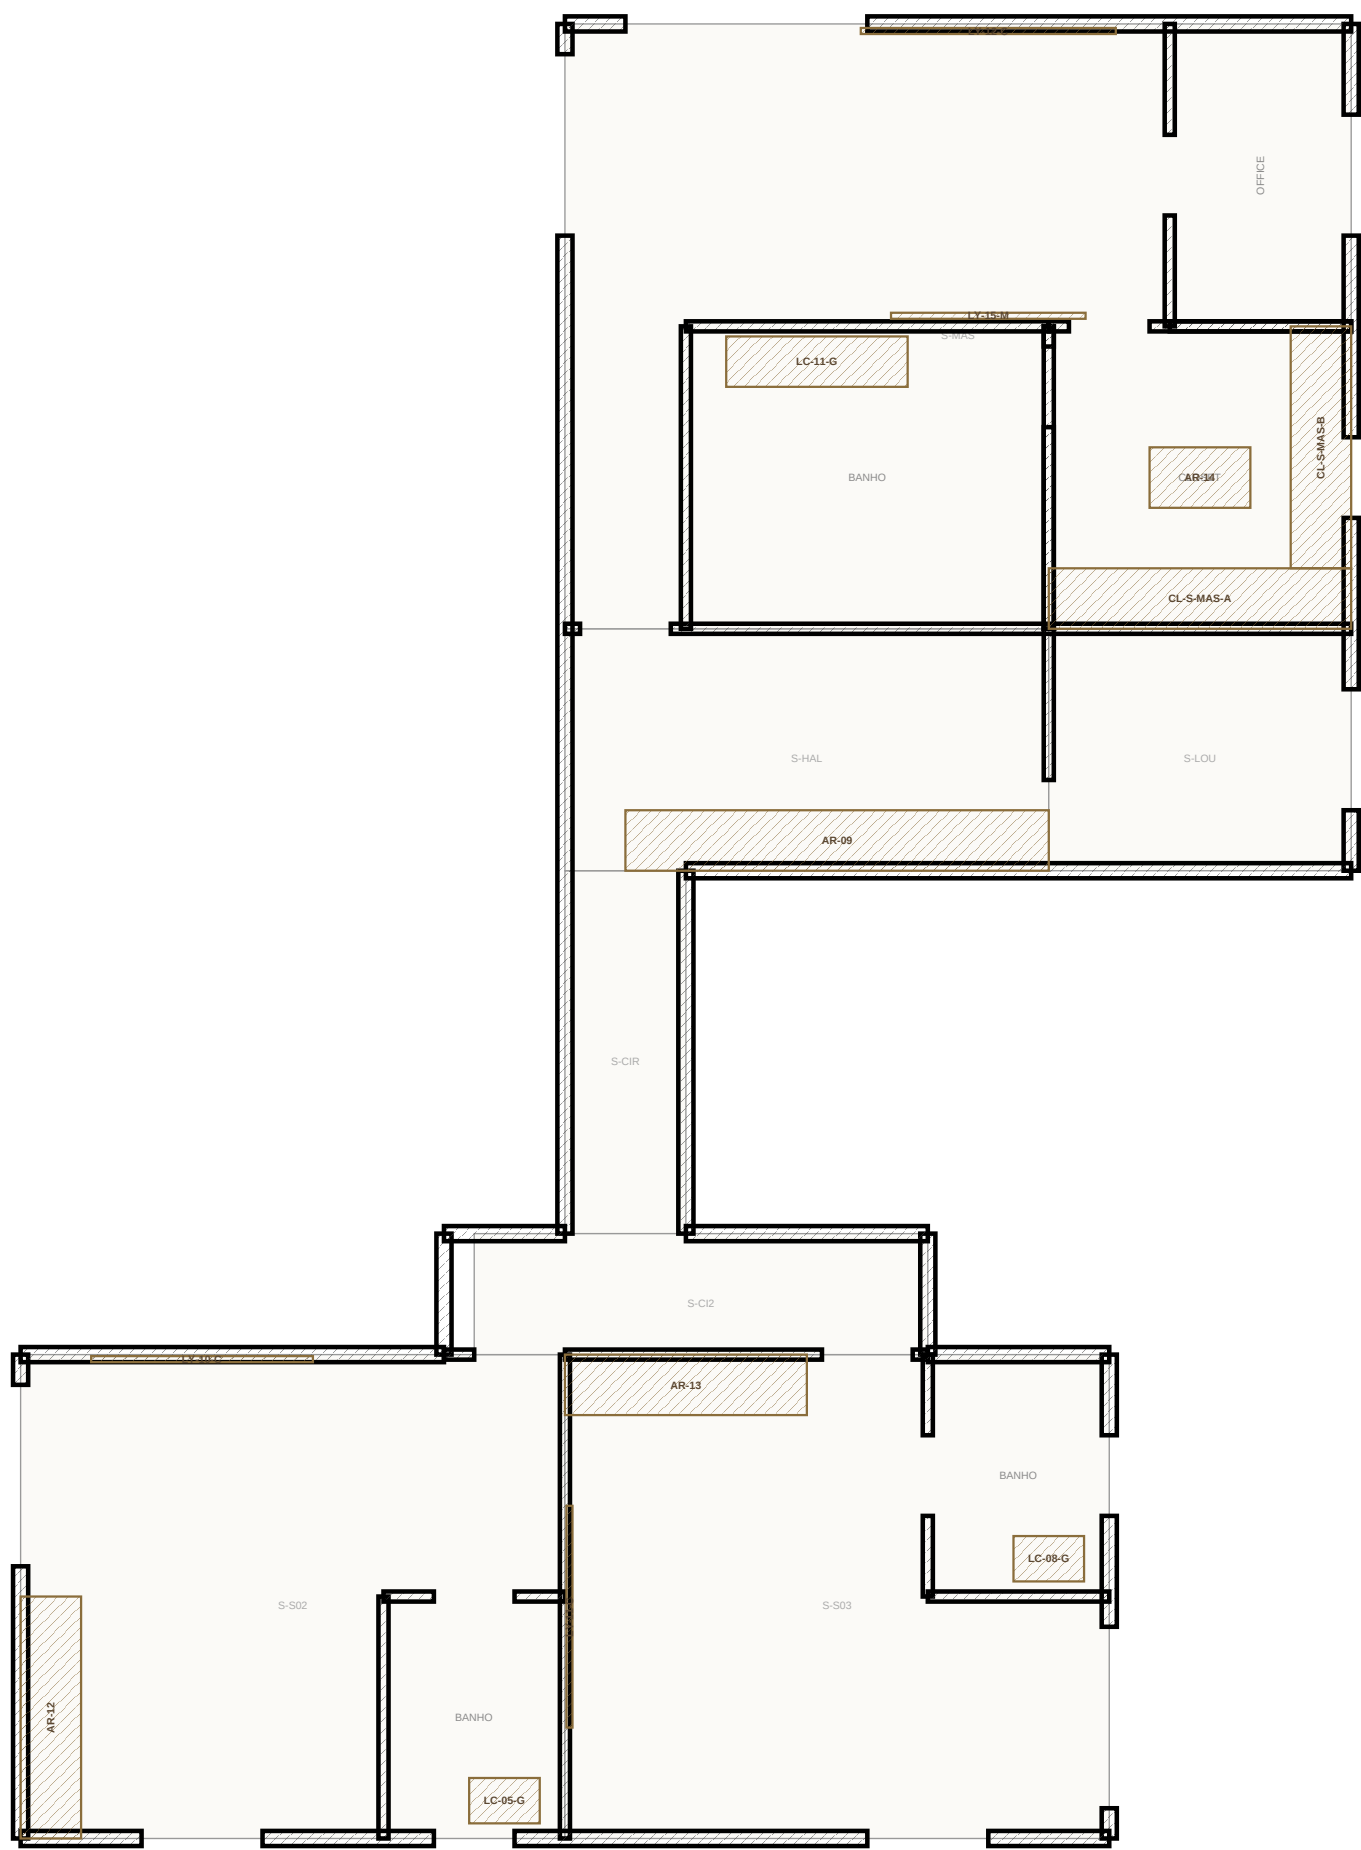

2 SUPERIOR — MARCENARIA  
ESCALA 1:75

QUADRO DE MOVEIS — TUDO O QUE E MARCENARIA NA CASA

| COD        | AMB   | FAMILIA       | FRENTE | PROF | ALT   | MOD | PORTAS | QAV | m2 FR |
|------------|-------|---------------|--------|------|-------|-----|--------|-----|-------|
| AB-05      | T-COR | prateleira    | 1.200  | 800  | 1.200 | 2   | 0      | 0   | 1,44  |
| AB-06      | T-COZ | prateleira    | 2.100  | 300  | 2.100 | 4   | 0      | 0   | 4,42  |
| AB-07      | T-COZ | prateleira    | 2.100  | 300  | 2.100 | 4   | 0      | 0   | 4,42  |
| AB-08      | T-COZ | armario alto  | 1.200  | 750  | 2.200 | 2   | 2      | 0   | 2,64  |
| AB-09      | T-DEP | prateleira    | 2.800  | 300  | 2.200 | 5   | 0      | 0   | 6,16  |
| AB-04      | T-GR  | armario alto  | 2.400  | 600  | 2.200 | 4   | 4      | 0   | 5,28  |
| AB-09      | S-HAL | rouparia      | 4.200  | 600  | 2.200 | 7   | 7      | 0   | 9,24  |
| AB-11      | T-ALC | guarda-roupa  | 1.800  | 600  | 2.200 | 3   | 3      | 8   | 3,96  |
| AB-12      | S-SO2 | guarda-roupa  | 2.400  | 600  | 2.200 | 4   | 4      | 8   | 5,28  |
| AB-13      | S-SO3 | guarda-roupa  | 2.400  | 600  | 2.200 | 4   | 4      | 8   | 5,28  |
| AB-14      | S-MAS | guarda-roupa  | 1.800  | 600  | 900   | 2   | 0      | 8   | 0,60  |
| BC-01-G    | T-COZ | patente       | 2.100  | 580  | 770   | 4   | 4      | 0   | 1,62  |
| BC-02-G    | T-COZ | patente       | 1.800  | 580  | 770   | 3   | 3      | 0   | 1,36  |
| BC-03-G    | T-COZ | patente       | 1.500  | 580  | 770   | 3   | 3      | 0   | 1,18  |
| BC-04-G    | T-COZ | patente       | 1.800  | 580  | 770   | 4   | 4      | 0   | 2,17  |
| BC-05-G    | T-GR  | patente       | 2.400  | 580  | 770   | 4   | 4      | 0   | 1,46  |
| LC-05-G    | T-COR | patente banho | 800    | 450  | 580   | 1   | 0      | 2   | 0,38  |
| LC-06-G    | T-REV | patente banho | 700    | 450  | 580   | 2   | 0      | 2   | 0,38  |
| LC-08-G    | S-SO2 | patente banho | 700    | 450  | 580   | 2   | 0      | 2   | 0,38  |
| LC-08-G    | S-SO3 | patente banho | 700    | 450  | 580   | 2   | 0      | 2   | 0,38  |
| LC-11-G    | S-MAS | patente banho | 1.800  | 580  | 760   | 3   | 0      | 2   | 0,65  |
| LV-03-P    | T-DEC | panel tv      | 1.800  | 55   | 1.800 | 1   | 0      | 5   | 3,24  |
| LV-04-M    | T-SOC | rack          | 1.800  | 450  | 450   | 3   | 0      | 3   | 0,81  |
| LV-06-C    | T-REV | cabineira     | 2.200  | 65   | 1.200 | 1   | 0      | 5   | 2,64  |
| LV-12-M    | T-ALC | mesa          | 1.500  | 600  | 750   | 1   | 0      | 3   | 1,12  |
| LV-13-C    | S-SO2 | cabineira     | 2.200  | 65   | 1.200 | 1   | 0      | 5   | 2,64  |
| LV-13-C    | S-SO3 | cabineira     | 2.200  | 65   | 1.200 | 1   | 0      | 5   | 2,64  |
| LV-13-C    | S-MAS | cabineira     | 2.200  | 65   | 1.200 | 1   | 0      | 5   | 3,04  |
| LV-15-M    | S-MAS | panel tv      | 1.800  | 55   | 1.800 | 1   | 0      | 5   | 3,47  |
| CL-S-MAS-A | S-MAS | closet        | 3.000  | 600  | 2.200 | 5   | 0      | 10  | 6,60  |
| CL-S-MAS-B | S-MAS | closet        | 2.400  | 600  | 2.200 | 4   | 0      | 8   | 5,28  |

TOTAIS

|                  |          |
|------------------|----------|
| moveis           | 25       |
| rodapeis         | 85       |
| portas           | 584      |
| portas / guarda  | 44 164   |
| fronte total     | 91,34 m2 |
| chapeis 15,16 m2 | 66 1,20  |

NOTAS

· Cada movei vem de nucleos/marcenarias: ARMARIOS, gabinete de cada BANCADA de granito, gabinete suspenso de cada bancada, rack, painel de TV e mesa de LAYOUT, cabineira de cada cama e os dois painéis do CLOSET.

· Modelo maximo 500 mm (altura da parede), altura por familia (2).

· Frente e a dimensao ao longo da parede, profundidade e o outro. Elevacoes nas PR-05 e 07.

· Posicao por categoria de ambiente: sala de aluminio grafico nos areas sociais e de servico, cama e 60 gram nos dormitorios.

PROJETO PORTO REAL

RESIDENCIA UNIFAMILIAR (MARIAUS - AM) | SOUS TATIANA-PS

PROJETO ARQUITETONICO

PLANTA DE MARCENARIA — TERREO E SUPERIOR

|                                                                                   |                                                   |                                                                              |                                |
|-----------------------------------------------------------------------------------|---------------------------------------------------|------------------------------------------------------------------------------|--------------------------------|
| BASE GEOMETRICA<br>Linha Consolidada<br>REV-022 (previável)<br>UNIDADE MESTRE: MM | ESCALA<br>1:75<br>FORMATO A1<br>MILHA 655/550/550 | ENTRADA<br>ESTUDO PRELIMINAR RMB<br>TUDO LIBERADO PARA OBRA<br>SEM ART / RNT | PROJETO<br>55<br>04-78 REV-008 |
|-----------------------------------------------------------------------------------|---------------------------------------------------|------------------------------------------------------------------------------|--------------------------------|