


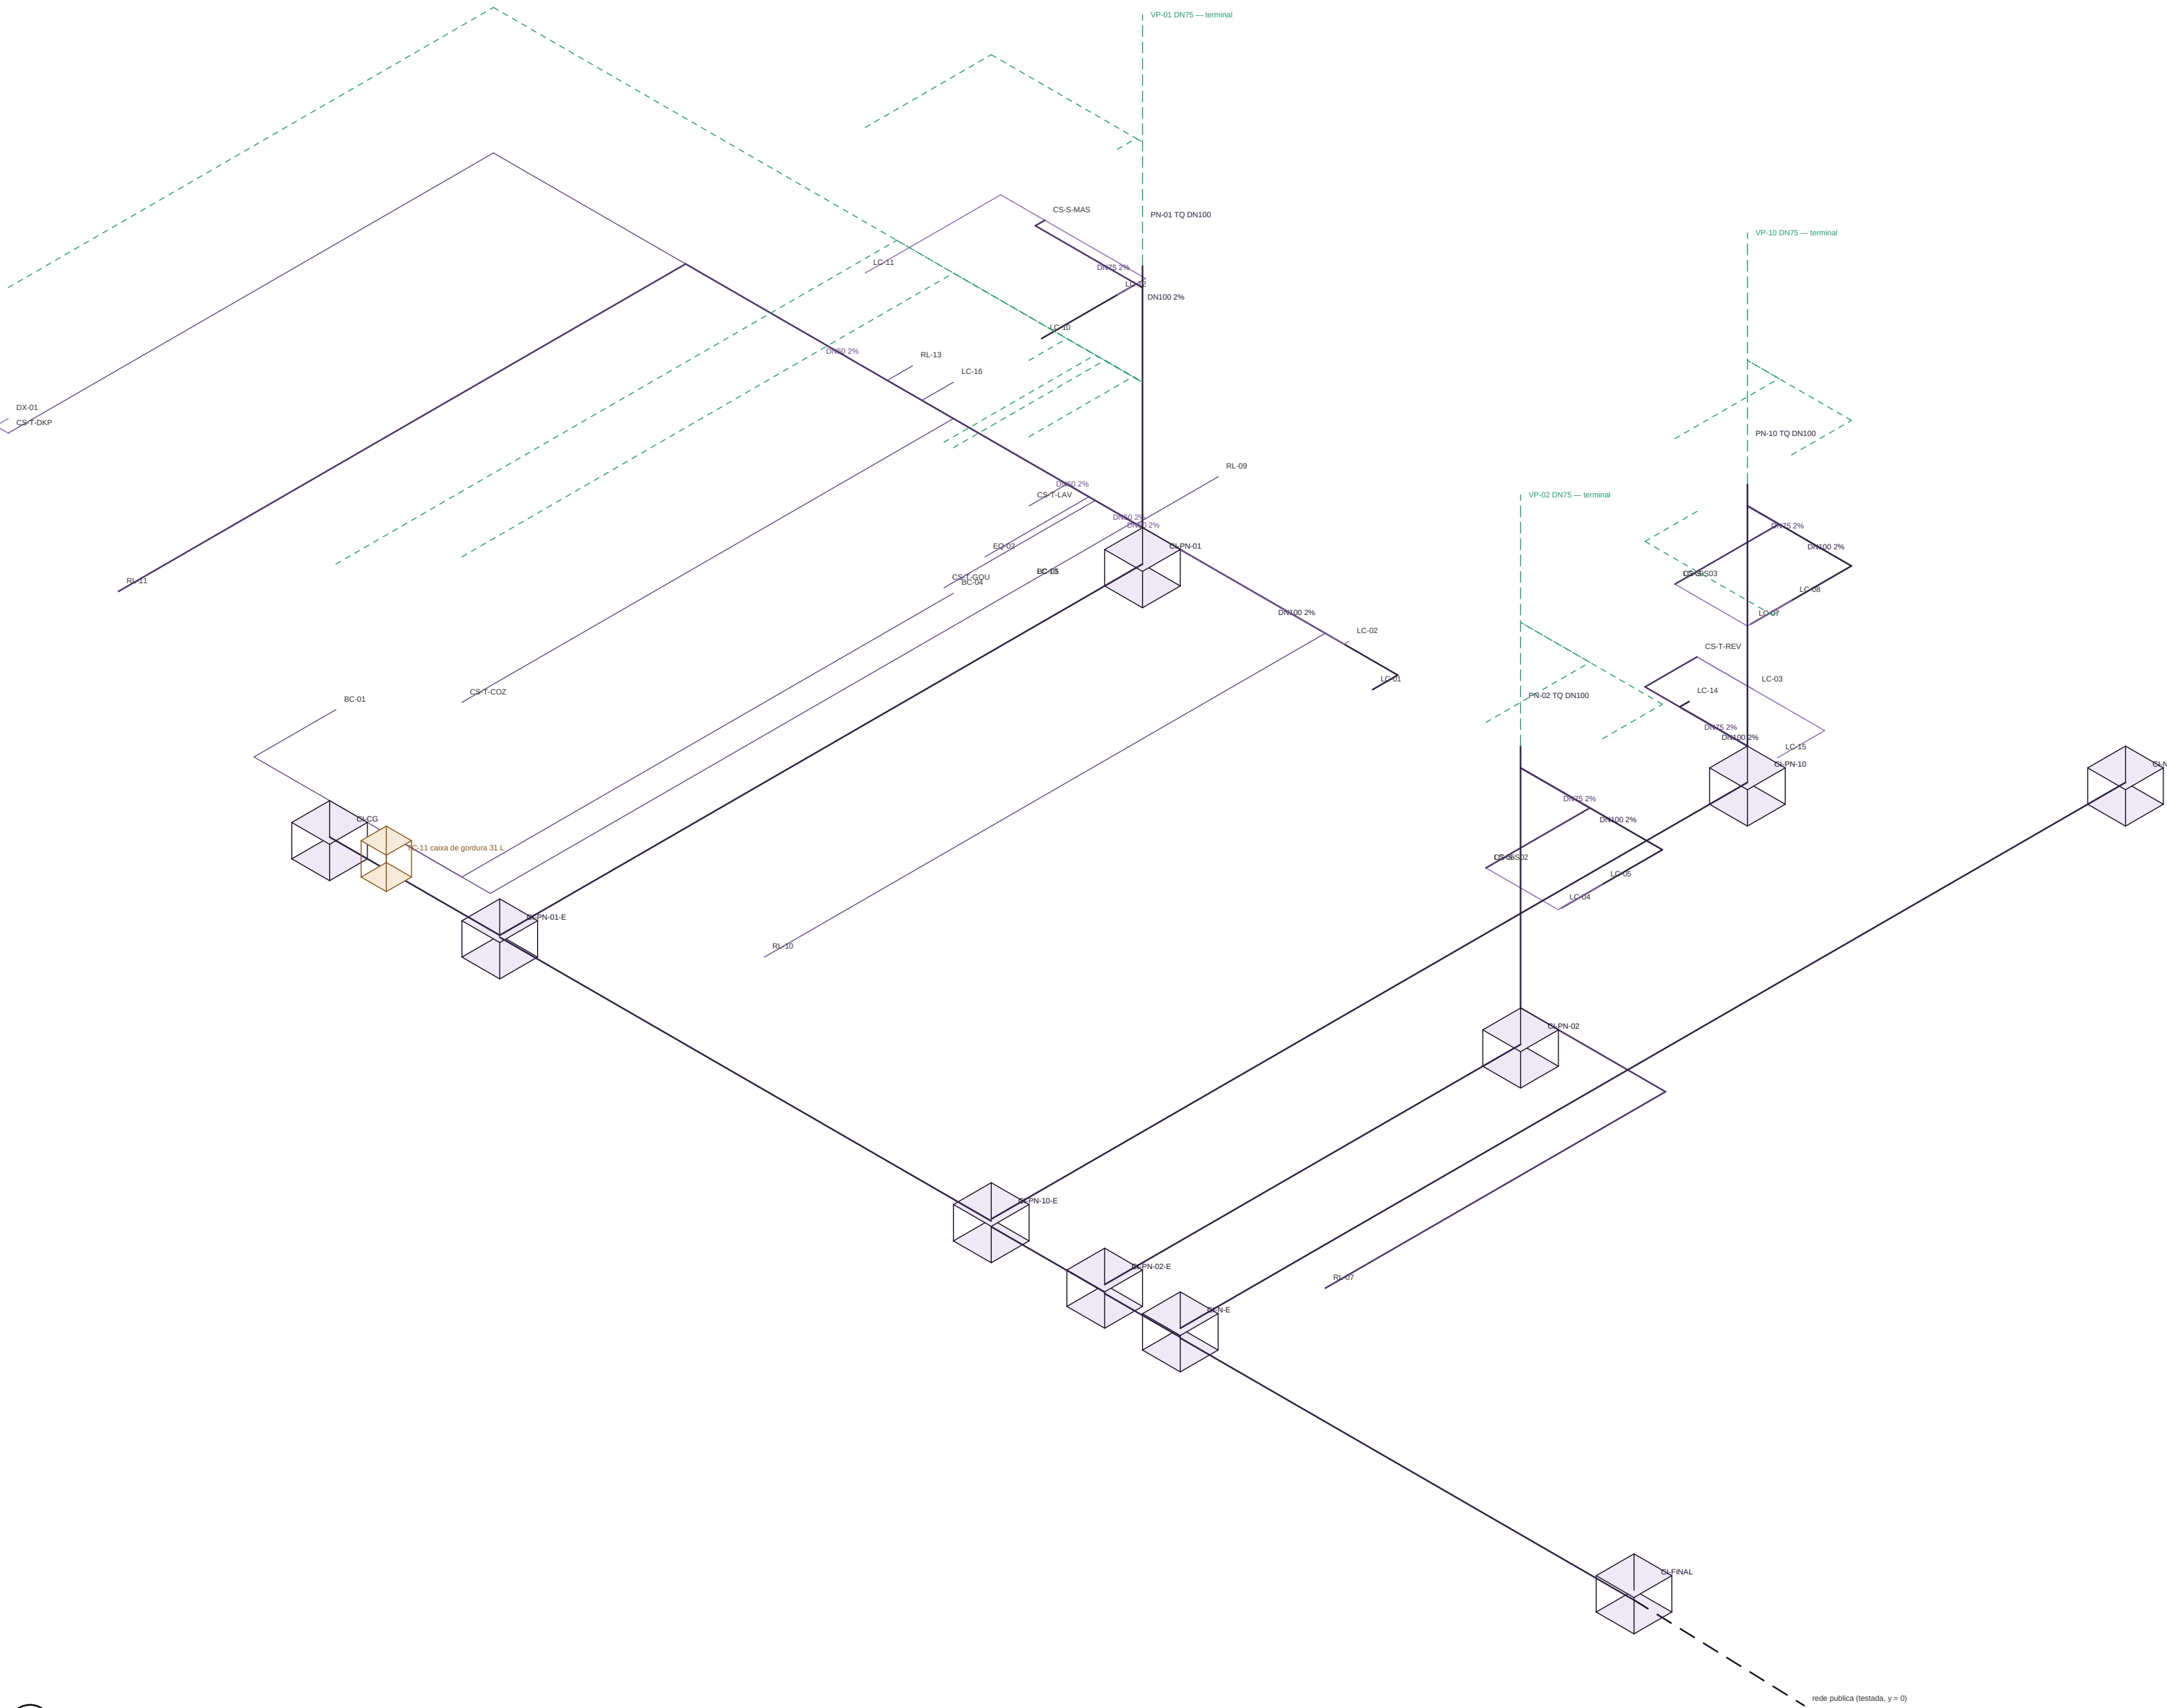


1 ISOMETRICO DE ESGOTO E VENTILACAO  
ESCALA 1:75

2 PLANTA DE CAIXAS DE INSPECCAO E COLETOR  
ESCALA 1:150

COLETOR — COTA DE FUNDO (mm, RN = piso do terreno)

| DE        | PARA      | DN    | L.m  | 1  | FUNDO MONT. | FUNDO AIS. | PROF. AIS. |
|-----------|-----------|-------|------|----|-------------|------------|------------|
| CPIN-01   | CPIN-02 E | DN100 | 18,2 | 2% | —           | —          | —          |
| CPIN-02   | CPIN-02 E | DN100 | 6,6  | 2% | —           | —          | —          |
| CPIN-10   | CPIN-02 E | DN100 | 12,0 | 2% | —           | —          | —          |
| CH-E      | CH-E      | DN100 | 15,0 | 2% | —           | —          | —          |
| CH-02     | CPIN-02 E | DN100 | 2,7  | 1% | 405         | 427        | 588        |
| CPIN-02 E | CPIN-02 E | DN100 | 7,9  | 1% | 307         | 405        | 527        |
| CPIN-02 E | CPIN-02 E | DN100 | 1,8  | 1% | 405         | 423        | 495        |
| CPIN-02 E | CH-E      | DN100 | 1,2  | 1% | 423         | 439        | 423        |
| CH-E      | CPIN-02   | DN100 | 7,2  | 1% | 405         | 397        | 435        |

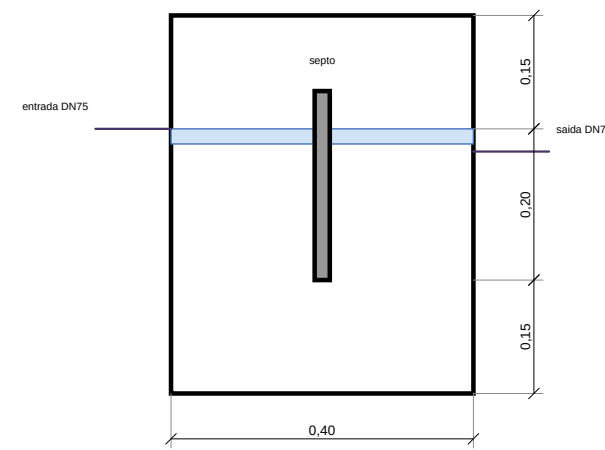

3 CAIXA DE GORDURA 31 L — hermetica, inspecionavel  
ESCALA 1:10

RAMAIS — 34

| PEÇA     | AMB   | TIPO       | DN    | UMC | 1  | L.m  | DESTINO  | VENT. |
|----------|-------|------------|-------|-----|----|------|----------|-------|
| LC-01    | T-02P | vento      | DN100 | 6   | 2% | 5,1  | CPIN-01  | sem   |
| LC-02    | T-02P | ventoso    | DN60  | 1   | 2% | 3,9  | CPIN-01  | sem   |
| LC-03    | T-REV | box        | DN60  | 2   | 2% | 1,1  | CS-T-REV | sem   |
| LC-14    | T-REV | vento      | DN100 | 6   | 2% | 1,5  | CPIN-10  | sem   |
| LC-15    | T-REV | ventoso    | DN60  | 1   | 2% | 3,1  | CS-T-REV | sem   |
| LC-04    | S-002 | vento      | DN100 | 6   | 2% | 4,4  | PM-02    | sem   |
| LC-05    | S-002 | ventoso    | DN60  | 1   | 2% | 2,2  | CS-S-002 | sem   |
| LC-06    | S-002 | box        | DN60  | 2   | 2% | 0,9  | CS-S-002 | sem   |
| LC-07    | S-002 | vento      | DN100 | 6   | 2% | 3,9  | PM-10    | sem   |
| LC-08    | S-003 | ventoso    | DN60  | 1   | 2% | 2,2  | CS-S-003 | sem   |
| LC-09    | S-003 | box        | DN60  | 2   | 2% | 0,9  | CS-S-003 | sem   |
| LC-10    | S-003 | vento      | DN100 | 6   | 2% | 3,9  | PM-01    | sem   |
| LC-11    | S-003 | ventoso    | DN60  | 1   | 2% | 3,4  | CS-S-003 | sem   |
| LC-12    | S-003 | box        | DN60  | 2   | 2% | 2,5  | CS-S-003 | sem   |
| LC-13    | T-LAV | sanita     | DN60  | 3   | 2% | 2,2  | CPIN-01  | sem   |
| LC-16    | T-02P | sanita     | DN60  | 3   | 2% | 4,4  | CPIN-01  | sem   |
| BC-01    | T-02P | sem        | DN60  | 3   | 2% | 4,4  | TC-11    | sem   |
| BC-04    | T-02P | sem        | DN60  | 3   | 2% | 10,8 | TC-11    | sem   |
| BC-05    | T-LAV | sem        | DN60  | 3   | 2% | 12,2 | TC-11    | sem   |
| BC-09    | T-LAV | sanita     | DN60  | 3   | 2% | 3,9  | CPIN-01  | sem   |
| BC-01    | T-02P | sanita     | DN60  | 2   | 2% | 0,9  | CS-T-02P | sem   |
| CS-T-REV | T-REV | caixa sif. | DN75  | 4   | 2% | 2,9  | CPIN-10  | sem   |
| CS-S-002 | S-002 | caixa sif. | DN75  | 4   | 2% | 3,1  | PM-02    | sem   |
| CS-S-003 | S-003 | caixa sif. | DN75  | 4   | 2% | 2,6  | PM-10    | sem   |
| CS-S-003 | S-003 | caixa sif. | DN75  | 4   | 2% | 2,2  | PM-01    | sem   |
| CS-T-LAV | T-LAV | caixa sif. | DN60  | 1   | 2% | 2,2  | CPIN-01  | sem   |
| CS-T-02P | T-02P | caixa sif. | DN60  | 1   | 2% | 15,9 | CPIN-01  | sem   |
| CS-T-02P | T-02P | caixa sif. | DN60  | 3   | 2% | 21,4 | CPIN-01  | sem   |
| CS-T-02P | T-02P | caixa sif. | DN60  | 1   | 2% | 3,8  | CPIN-01  | sem   |
| RL-13    | T-02P | sem        | DN60  | 1   | 2% | 5,1  | CPIN-01  | sem   |
| RL-07    | S-003 | sem        | DN75  | 1   | 2% | 9,2  | CPIN-01  | sem   |
| RL-11    | T-LAV | sem        | DN75  | 1   | 2% | 15,5 | CPIN-01  | sem   |
| RL-09    | T-VBL | sem        | DN60  | 1   | 2% | 1,7  | CPIN-01  | sem   |
| RL-10    | T-L00 | sem        | DN60  | 1   | 2% | 14,2 | CPIN-01  | sem   |

NOTAS

- 1. Ramal de descarga por peça com DN da NBR 5200; comprimento 2% em toda a rede predial (a norma permite 1% em DN100) — a decisão "sem nos entupir" — coleta enterrada a 1%.
- 2. Lavatório, box e vaso de cada banheiro caem em caixa sifonada 120 x 120 x 50 mm, vaso direto ao tubo de queda ou a caixa de inspeção. 15 ramais de ventilação DN60 onde a altura fica além da distância da tabela 5.
- 3. 12 caixas de inspeção 900 x 600 que de cada tubo de queda, frente, encanimento de 20 x 10. Fundo final a 0,75 mm no total, no sentido em que o tubo desce (P000) a profundidade não cresce.
- 4. Caixa de gordura CG30 — caixa de gordura sempre de 30 L a partir de dois pontos, tubos de queda DN100 com terminal de ventilação 300 mm acima da cobertura.

PROJETO PORTO REAL

RESIDENCIA UNIFAMILIAR (MANSÃO - AM) | SOBR TURTURA-PI

PROJETO ARQUITETONICO

ESGOTO SANITARIO E VENTILACAO — ISOMETRICO, CAIXAS E COLETOR

|                                                                                    |                                                                       |                                                                 |                              |
|------------------------------------------------------------------------------------|-----------------------------------------------------------------------|-----------------------------------------------------------------|------------------------------|
| BASE GEOMETRICA<br>Linha Consolidada<br>Projeto (preliminar)<br>UNIDADE: METRO: mm | ESCALA<br>1:75 • 1:150 • 1:10<br>FORMATO: A1<br>MATERIAL: 60/60/60/60 | ESTUDO PRELIMINAR RIB<br>MATERIAL: 60/60/60/60<br>SEM ART / RIB | PROJETO<br>62<br>60/60/60/60 |
|------------------------------------------------------------------------------------|-----------------------------------------------------------------------|-----------------------------------------------------------------|------------------------------|