



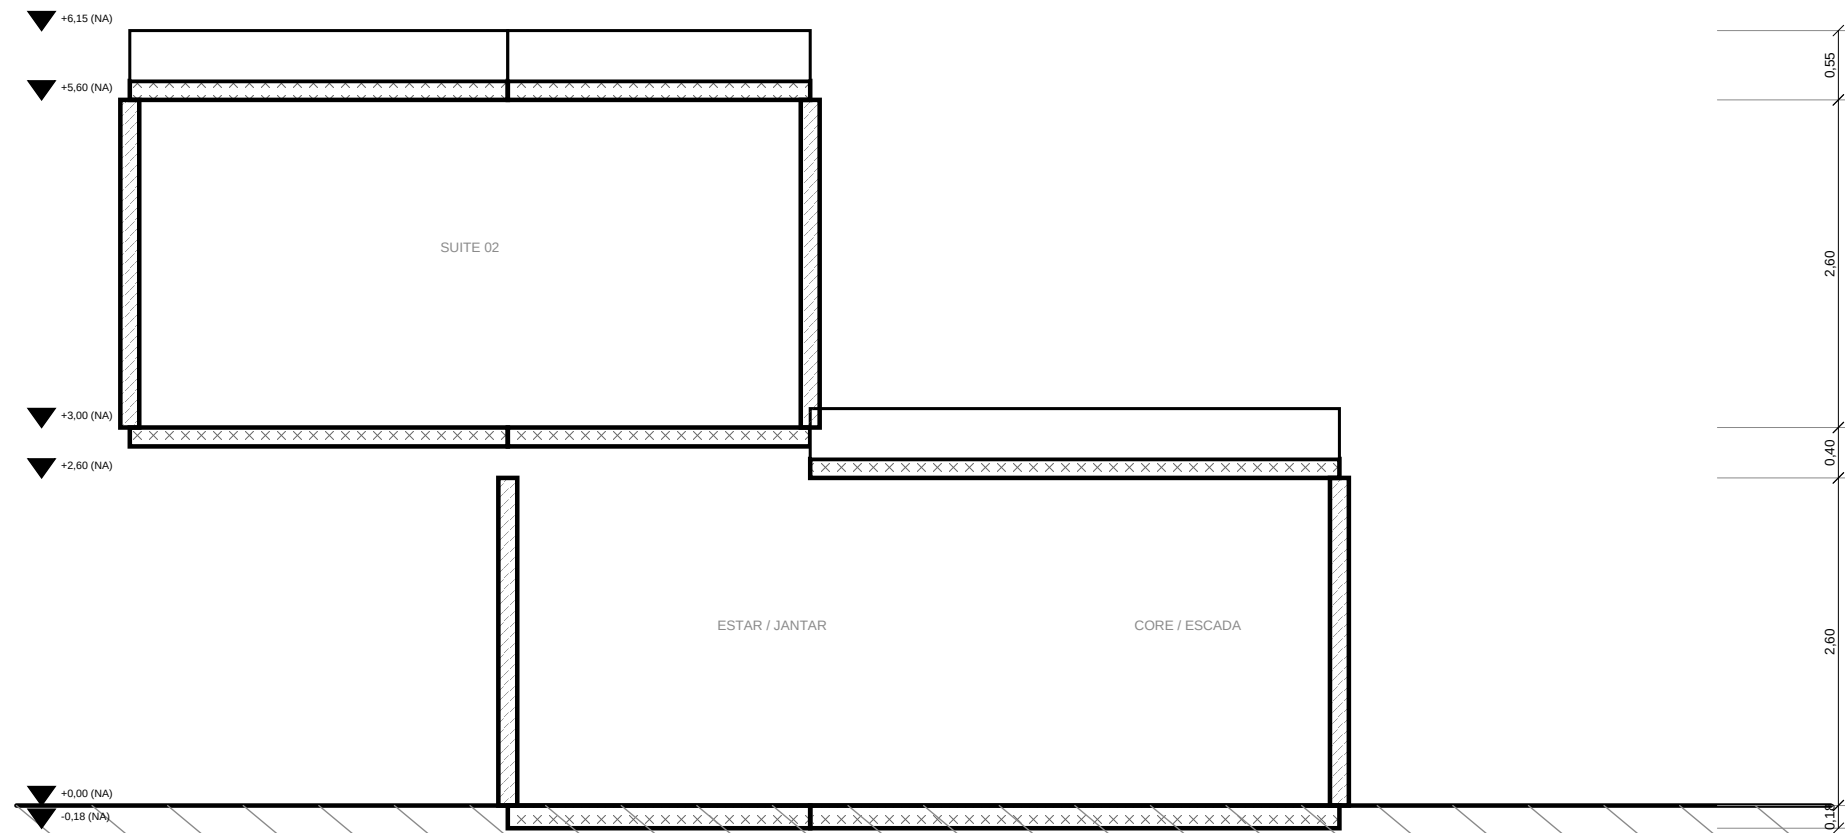

1 CORTE AA — TRANSVERSAL
ESCALA 1:60

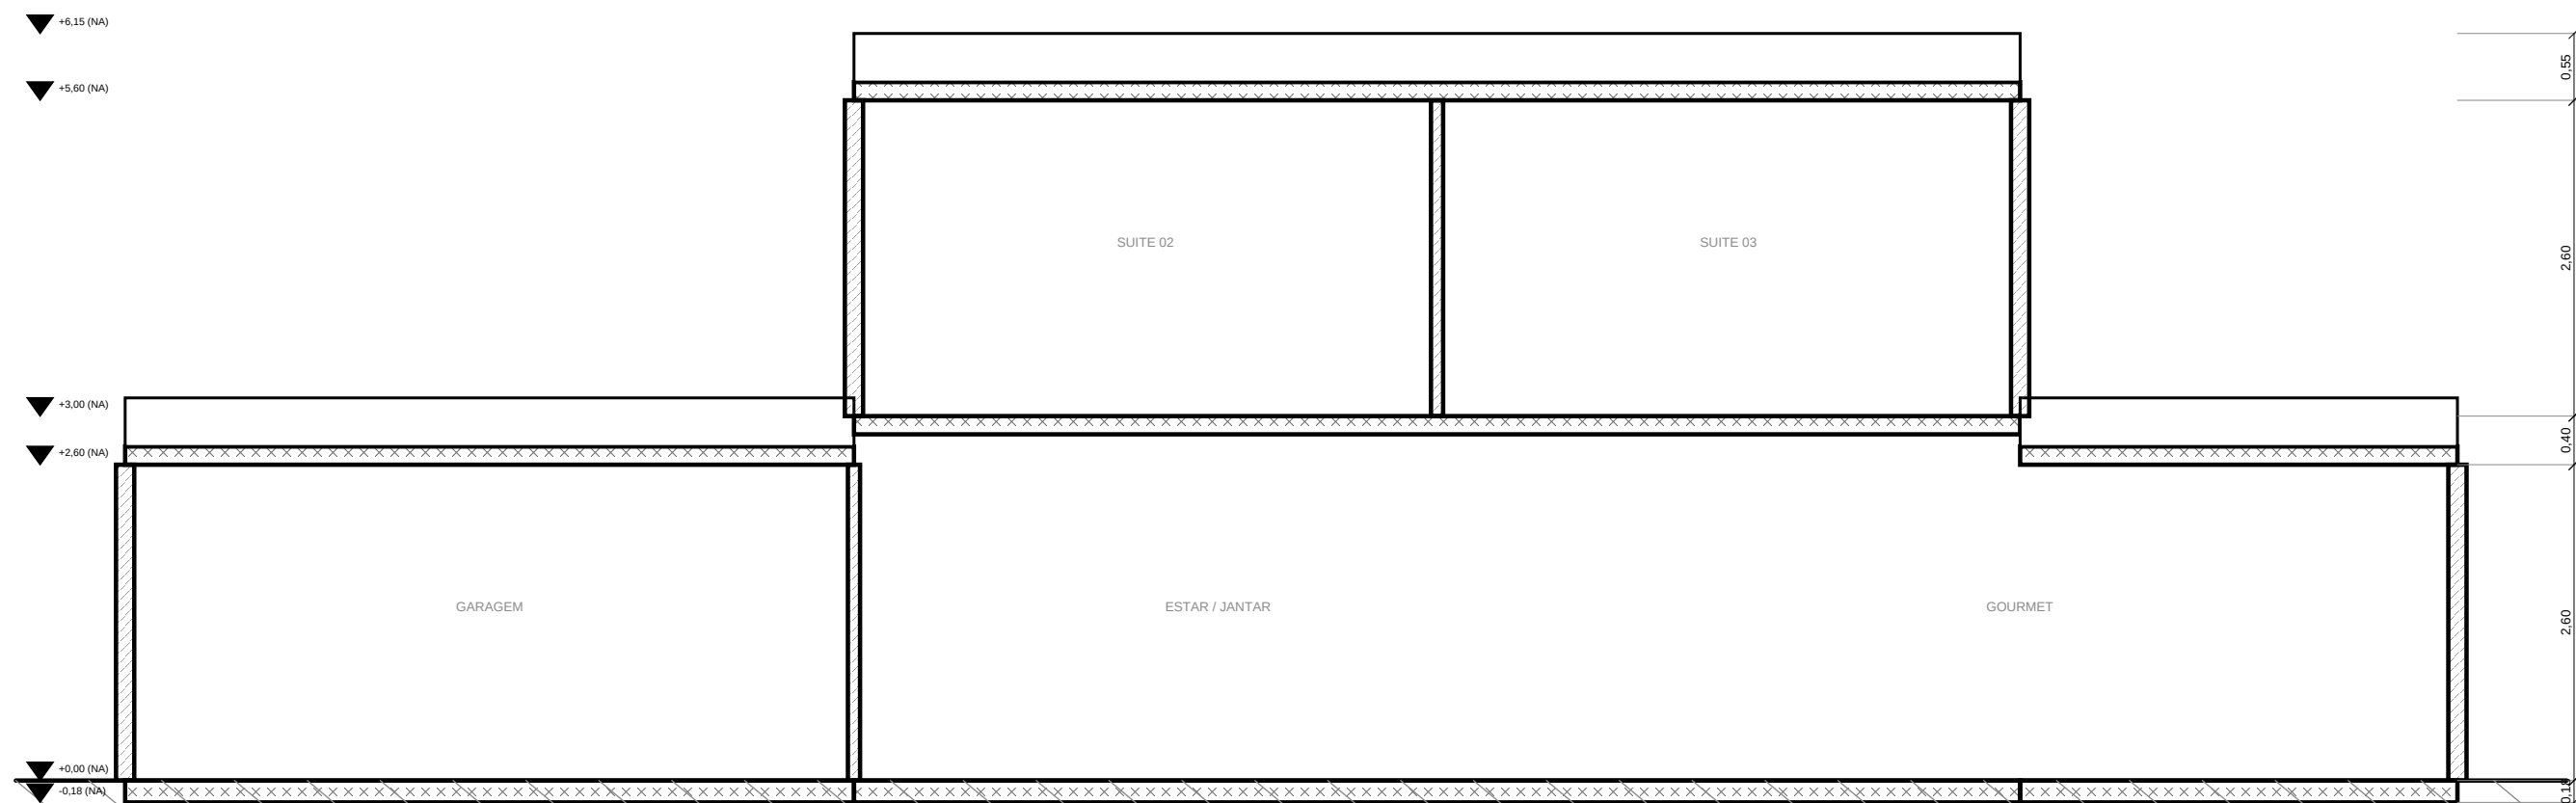

2 CORTE BB — LONGITUDINAL
ESCALA 1:60



- NOTAS
- * Piso drenado acabado 2500 mm x piso a piso 3000 mm.
 - * Topo da platibanda +0.250 m (não pavimentado) e +0.100 m (pavimentado) — H.
 - * Fundação em radier 180 mm, taxa 30 MPa, aço CA-50 (S).
 - * Vedação em Light Steel Frame, vãos grandes em perfil metálico estrutural.

PROJETO PORTO REAL

RESIDENCIA UNIFAMILIAR (MANAUS - AM) | SUELO TATIANA (S)

PROJETO ARQUITETONICO

CORTES AA E BB

BASE GEOMETRICA	ESCALA	EMISSAO	PROJECION
União Consolidada	1:60	ESTUDIO PRELIMINAR	06
Projeto (previsão)	FORMATO A1	NAO LIBERADO PARA OBRA	06.13
UNIDADE METRICA: MM	MILHA 600/000000	SEM ART / INT	