



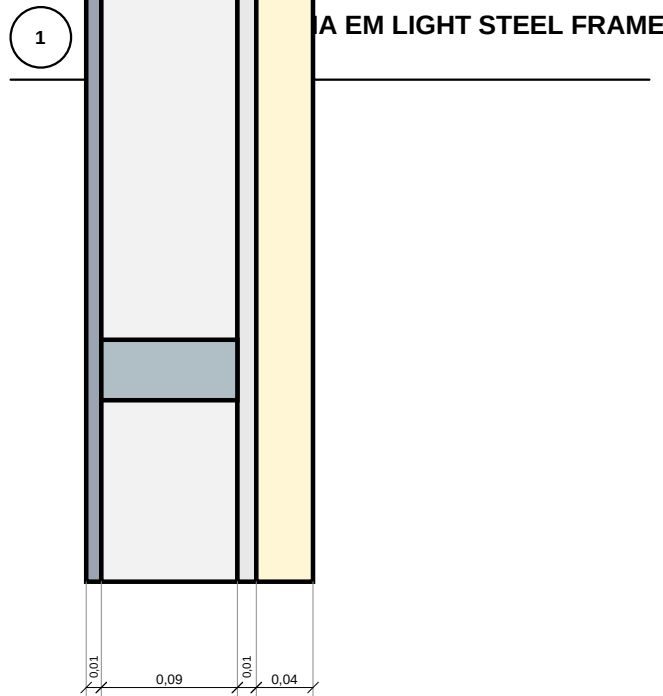


esp. total 150 mm


2 ESCADA — CORTE ESQUEMATICO
ESCALA 1:25

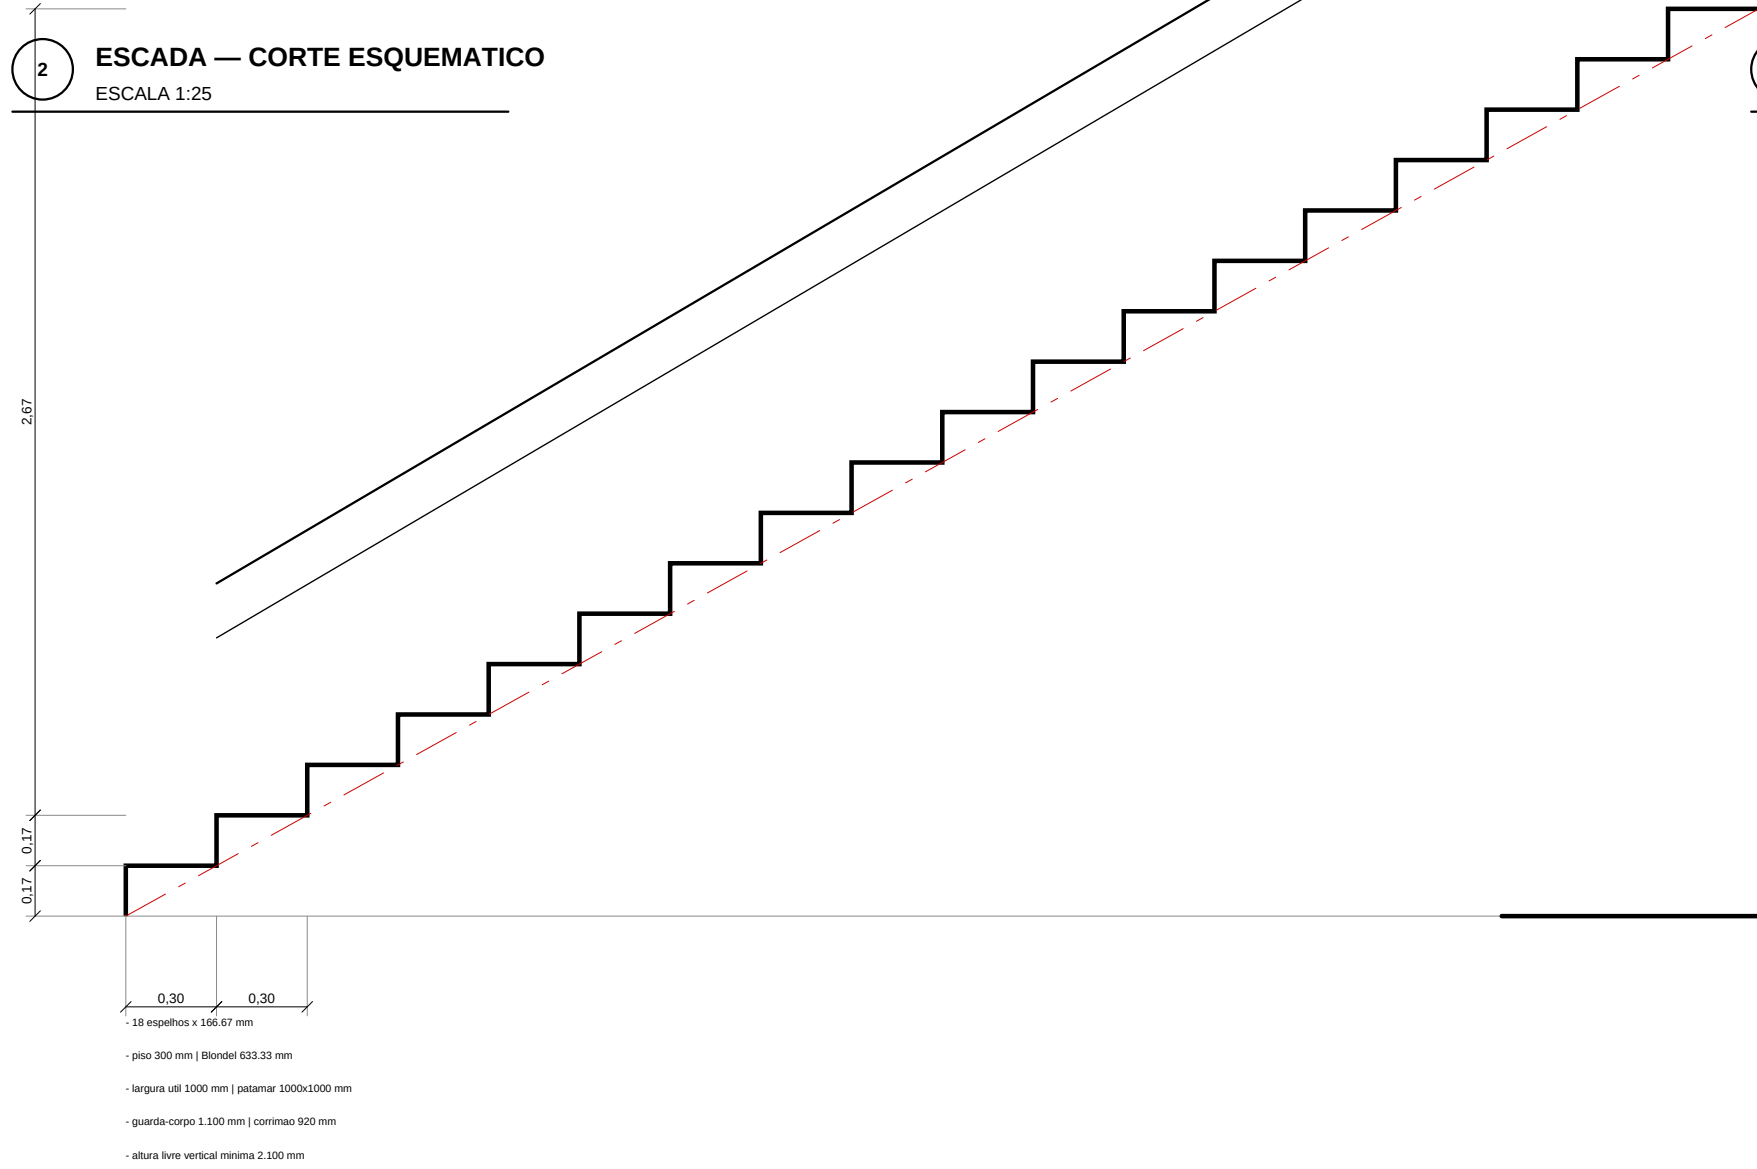

3 PISCINA — CORTE
ESCALA 1:25

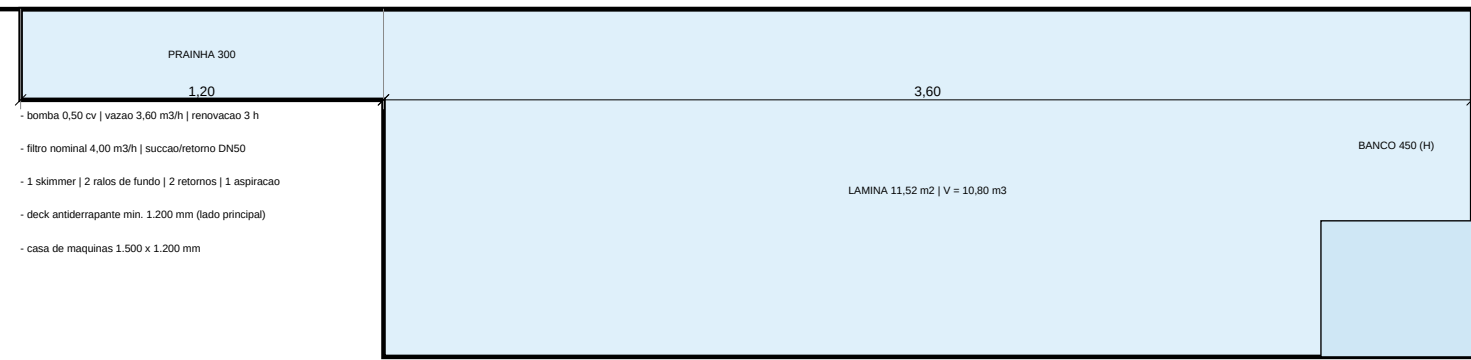

4 FAIXA TECNICA LATERAL — CORTE
ESCALA 1:25

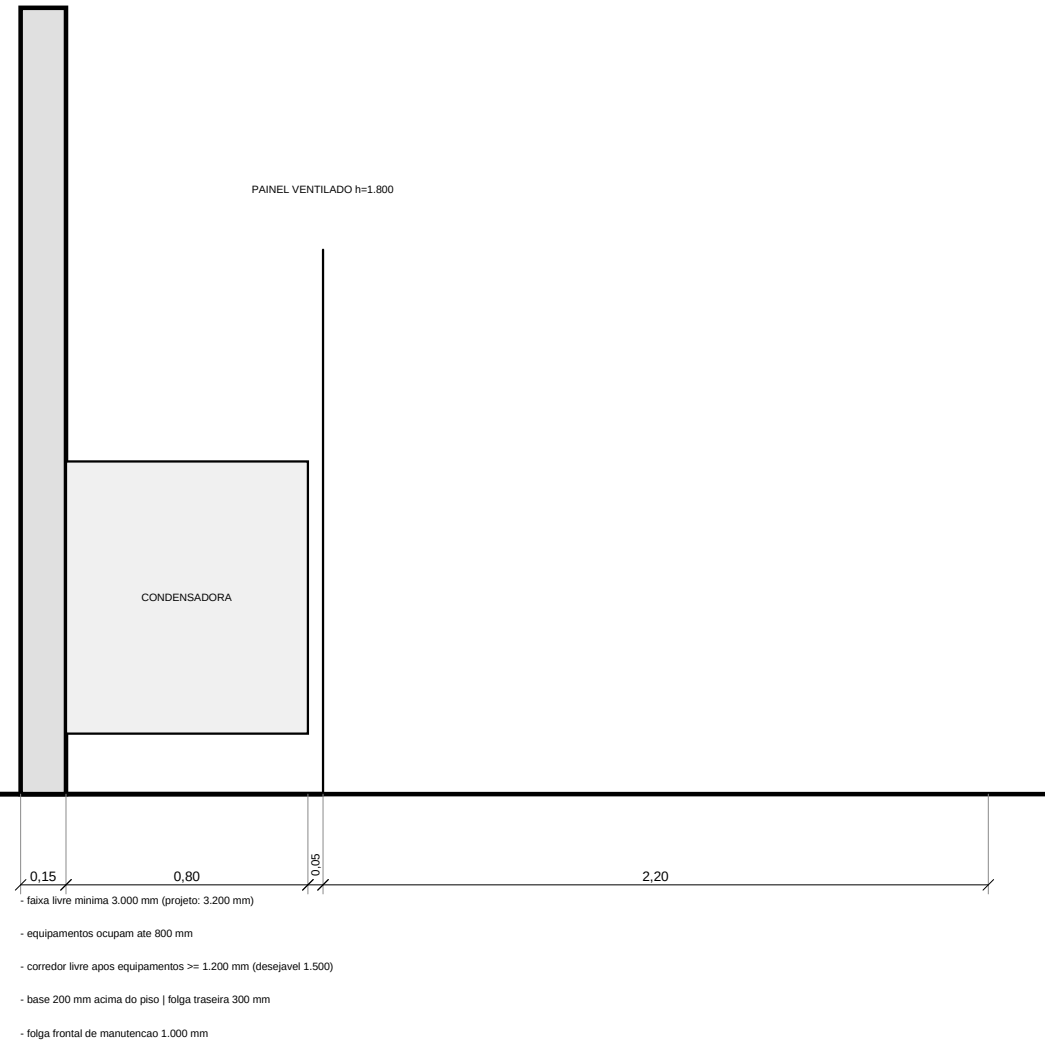

NOTAS

- Detalhes de estado — não liberados para fabricação ou corte (sem revisão confirmada).
- Paralelo externo consolidado em 120 mm, distância interna em 120 mm (95).
- Escada reconstruída com estrutura, guarda-corpo e espessura de acabamento antes da entrega.

PROJETO PORTO REAL

RESIDENCIA UNIFAMILIAR (MANGUS - AM) | SOUS TATIANA (PS)

PROJETO ARQUITETONICO

DETALHES CONSTRUTIVOS AMPLIADOS

BASE GEOMETRICA	ESCALA	EMISSAO	PROJECION
União Consolidada	indicada	ESTUDIO PRELIMINAR	10
PS-PS2 (previsto)	FORMATO A1	NAO LIBERADO PARA OBRA	
UNIDADE METRICA: mm	MAQUETA: 1/50 (1/50)	SEM ART / RNT	06.13