


| FORROS POR AMBIENTE |                                            |       |                                                        |
|---------------------|--------------------------------------------|-------|--------------------------------------------------------|
| ANEXOS              | SOLUCIO                                    | AREA  | FOR QUE                                                |
| T-GCOV              | forro aluminado (a mineral aparente ou par | 20,24 | casco preto que deturba a continuidade de 2,10 p       |
| T-ROD               | gesso liso + corantes e papéis             | 25,20 | aluminado sem di. moldados, forro branco aqua linc     |
| T-COD               | gesso liso lustrado                        | 18,00 | superfície de fácil limpeza sem ornamentação sobre ois |
| S-ROD               | gesso liso + la mineral sobre o forro      | 25,52 | la sobre o forro aluminado ludo de chaco no panel mto  |
| S-ROD               | gesso liso + la mineral sobre o forro      | 25,52 | leito                                                  |
| S-MAS               | gesso liso + la mineral sobre o forro      | 28,80 | leito                                                  |
| T-GAR               | sem forro (positivos aparentes)            | 36,00 | anteriores sem exigência acústica nem térmica          |
| T-QR1               | sem forro (positivos aparentes)            | 9,00  | leito                                                  |
| T-QAR               | sem forro (positivos aparentes)            | 3,60  | leito                                                  |

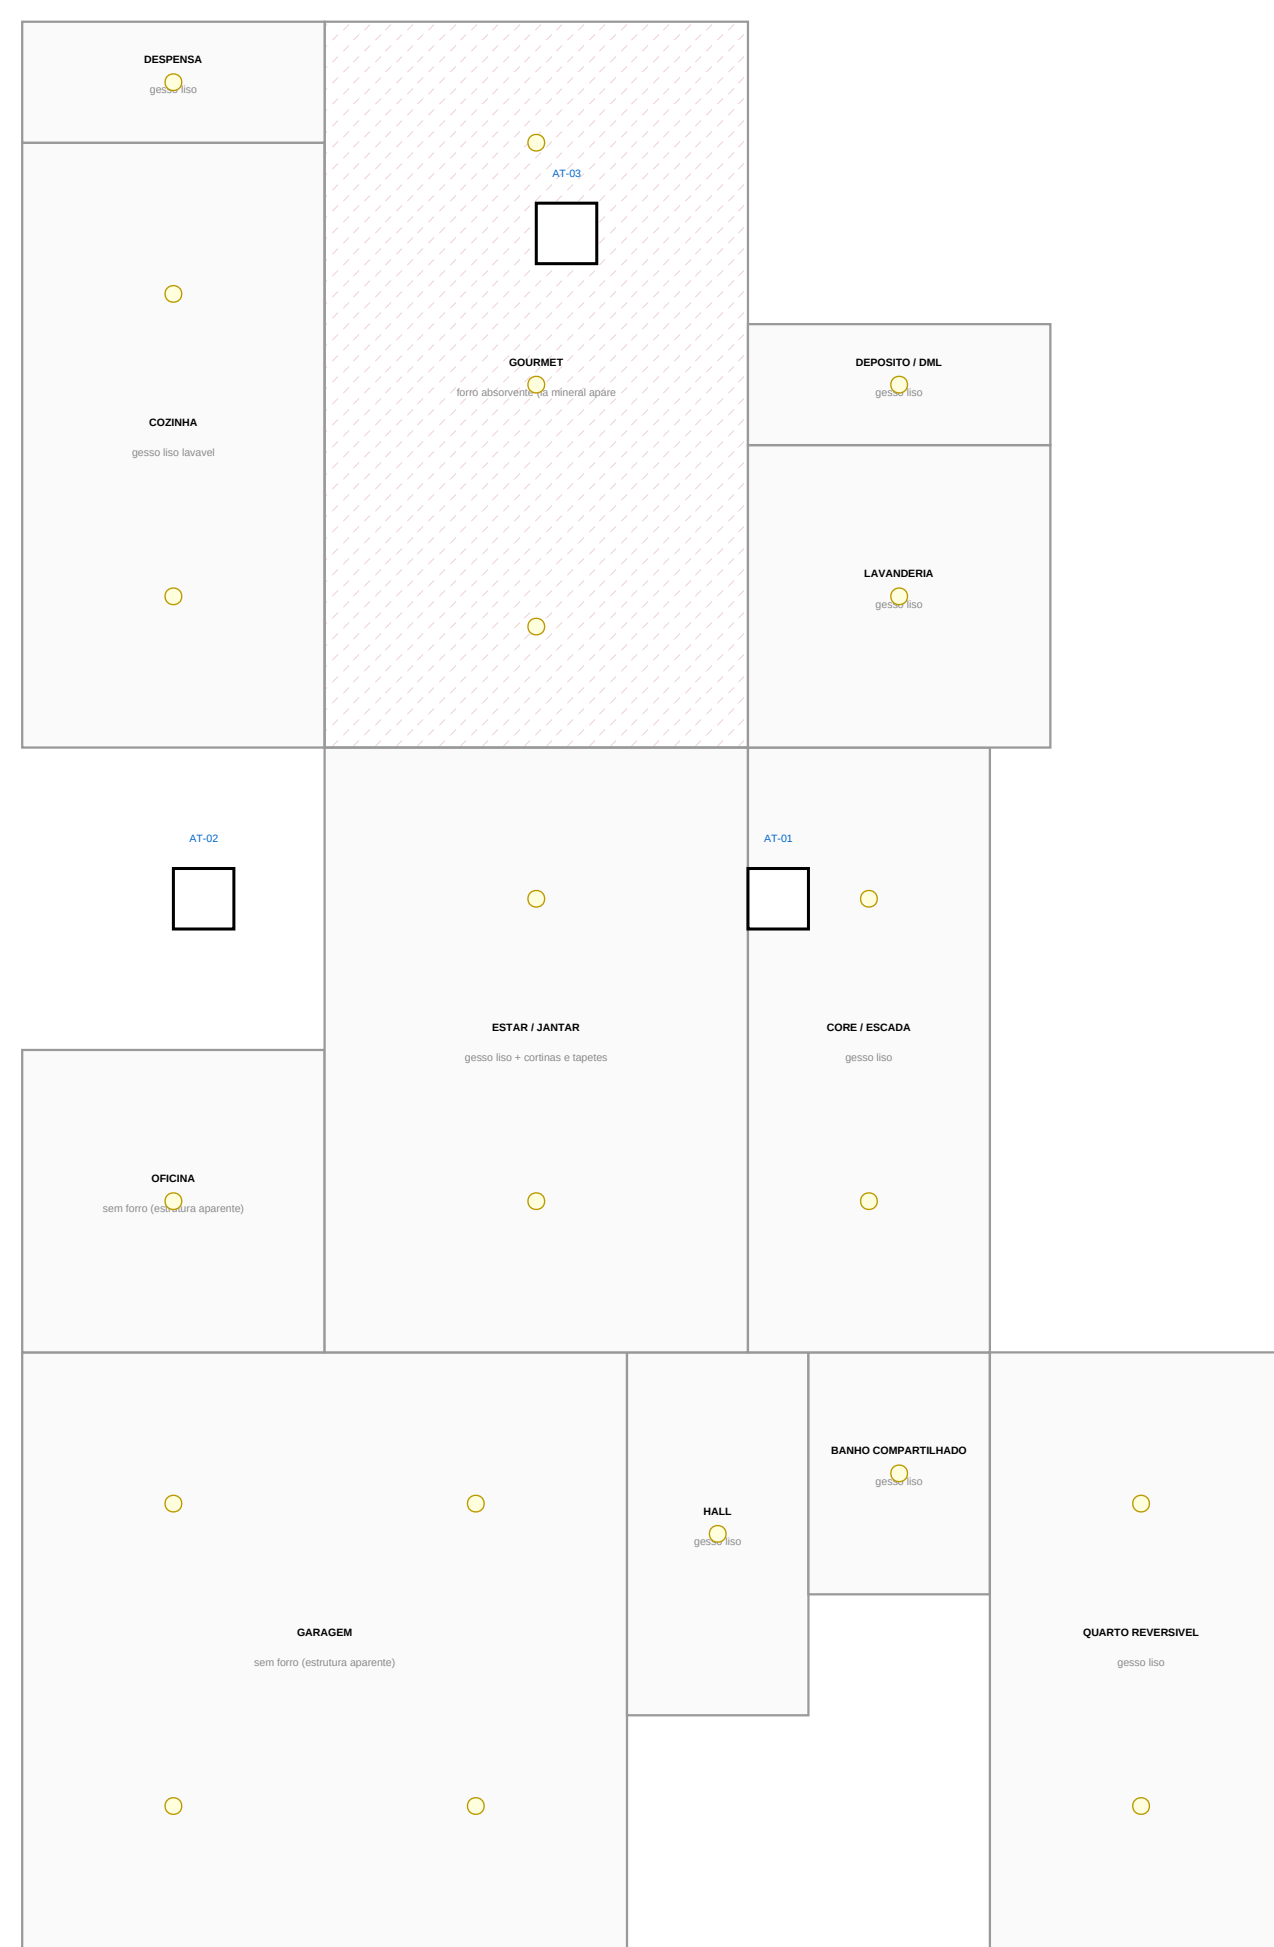

1 FORRO REFLETIDO — TERREO  
ESCALA 1:75

**NOTAS**

- Planta refletida: vista do forno projetada no plano horizontal.
- Forno absorvente apenas no gourmet — único ponto com reverberação crítica.
- Alçapões técnicos de 600 x 600 mm; passarela de cobertura de 600 mm.
- Iluminação geral 3.000 K, IRC mínimo 90.

|   |                                                                                        |   |                                                     |
|---|----------------------------------------------------------------------------------------|---|-----------------------------------------------------|
| <div>PROJETO PORTO REAL</div> <div>RESIDENCIA UNIFAMILIAR   MANAUS - AM   51215 TAPARIUA PS</div>                          |                                                                                        |   |                                                     |
| <div>PROJETO ARQUITETONICO</div> <div>PLANTA DE FORRO E ILUMINACAO</div>                                                   |                                                                                        |   |                                                     |
| <div>BASE GEOMETRICA</div> <div>Lista Consolidada</div> <div>por(R2) [projetado]</div> <div>ORÇAMENTO MESTRE - 04/24</div> | <div>ESCALA</div> <div>1:75</div> <div>FORMATO A1</div> <div>MALHA: 600X900(ISO)</div> | <div>DESENHO</div> <div>ESTUDO PRELIMINAR</div> <div>NÃO USADO PARA OBRA</div> <div>SEM ART / IMPR</div> | <div>FRONTEIRA</div> <div>16</div> <div>06/13</div> |