




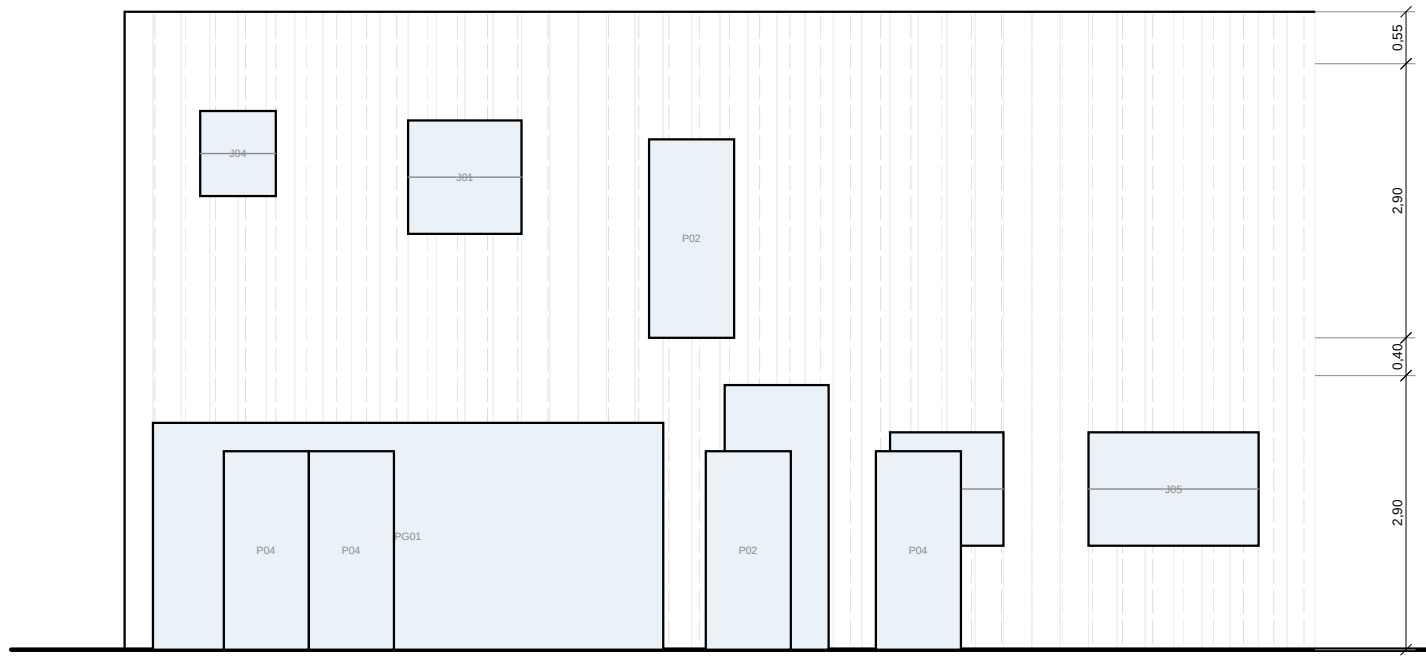


FACHADA FRONTAL (LESTE — RUA)

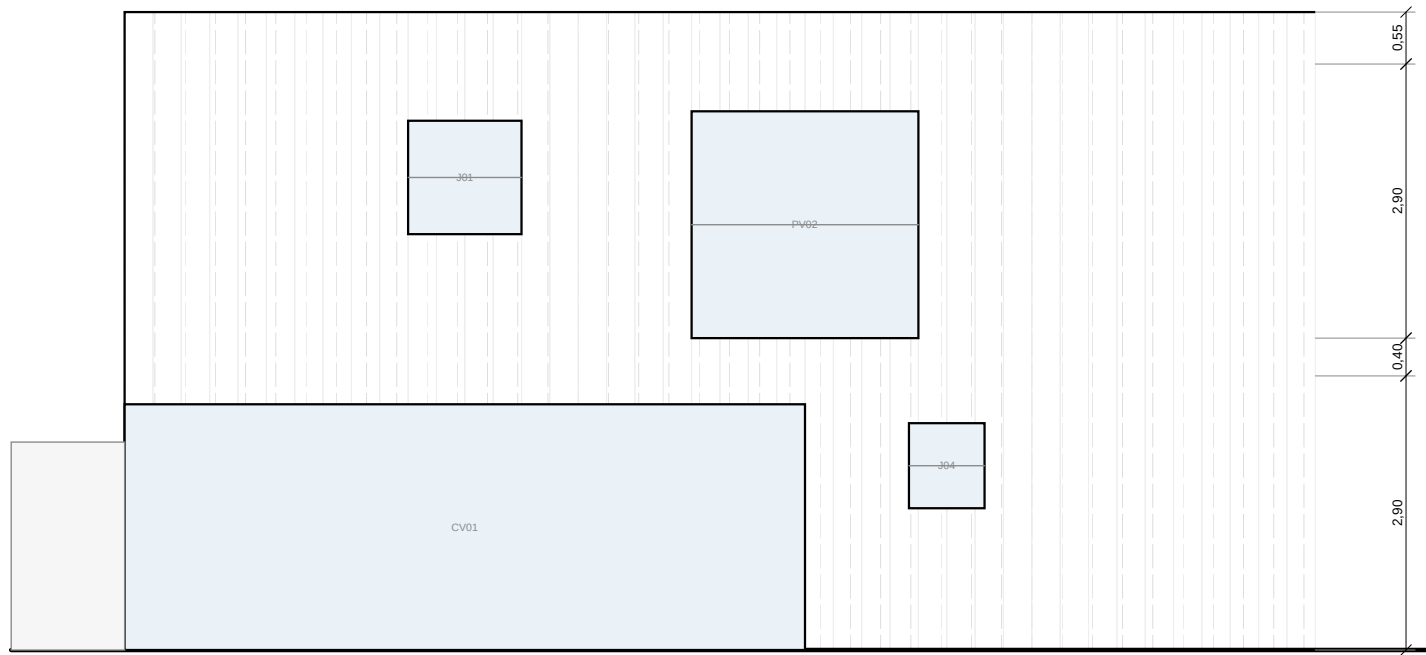

FACHADA POSTERIOR (OESTE — PISCINA)

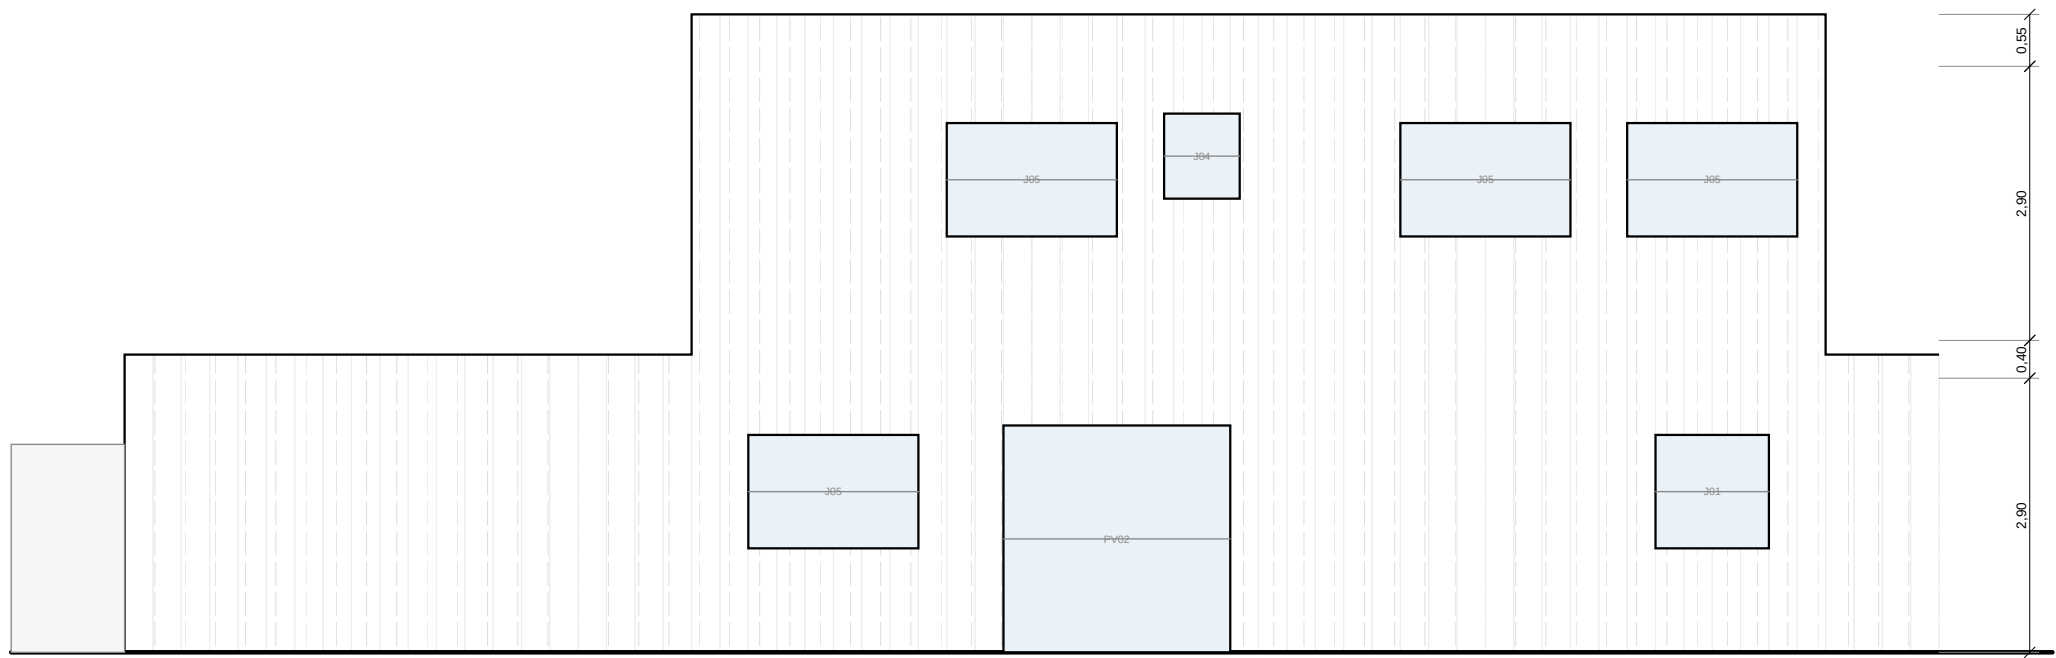

FACHADA LATERAL ESQUERDA (SUL)

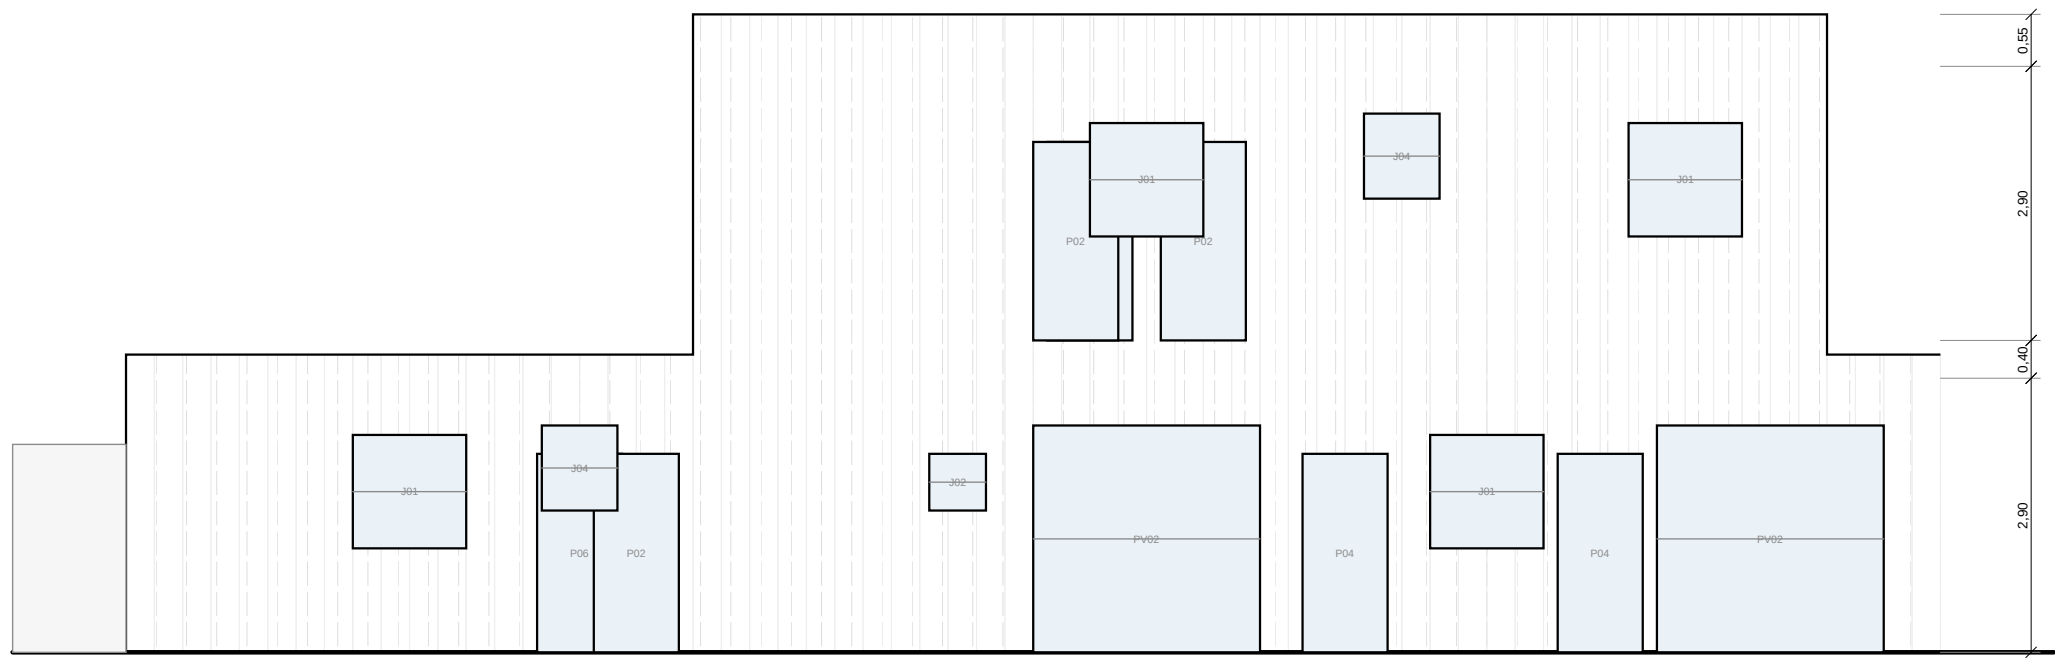

FACHADA LATERAL DIREITA (NORTE)

1 FACHADAS
ESCALA 1:80



- NOTAS
- Maximo de 2 fachadas de acabamento: material c/aco, aluminio perfilado, aluminio anodizado.
 - Vidro reduzido na frente e concentrado na social posterior.
 - Condensadores concentrados na fachada lateral direita, ocultos por painéis verticais 1x1.800 mm.
 - Muros laterais, de fundo e de testada 1x1.200 mm; painéis de vedação e de proteção na testada (PORTÃO, TESTADA).

PROJETO PORTO REAL

RESIDENCIA UNIFAMILIAR (MANSÃO - AM) | SOUS TATIANA-PS

PROJETO ARQUITETONICO

FACHADAS

BASE GEOMETRICA	ESCALA	EMISSAO	PROJETO
Unidade Consolidada	1:80	ESTUDO PRELIMINAR R74	07
Projeto (preliminar)	FORMATO A1	IMAGEM LIBERADO PARA ORCA	SEM ART / RNT
UNIDADE MESTRE: AM	MALHA 600/600/600	SEM ART / RNT	06-08-REV074