


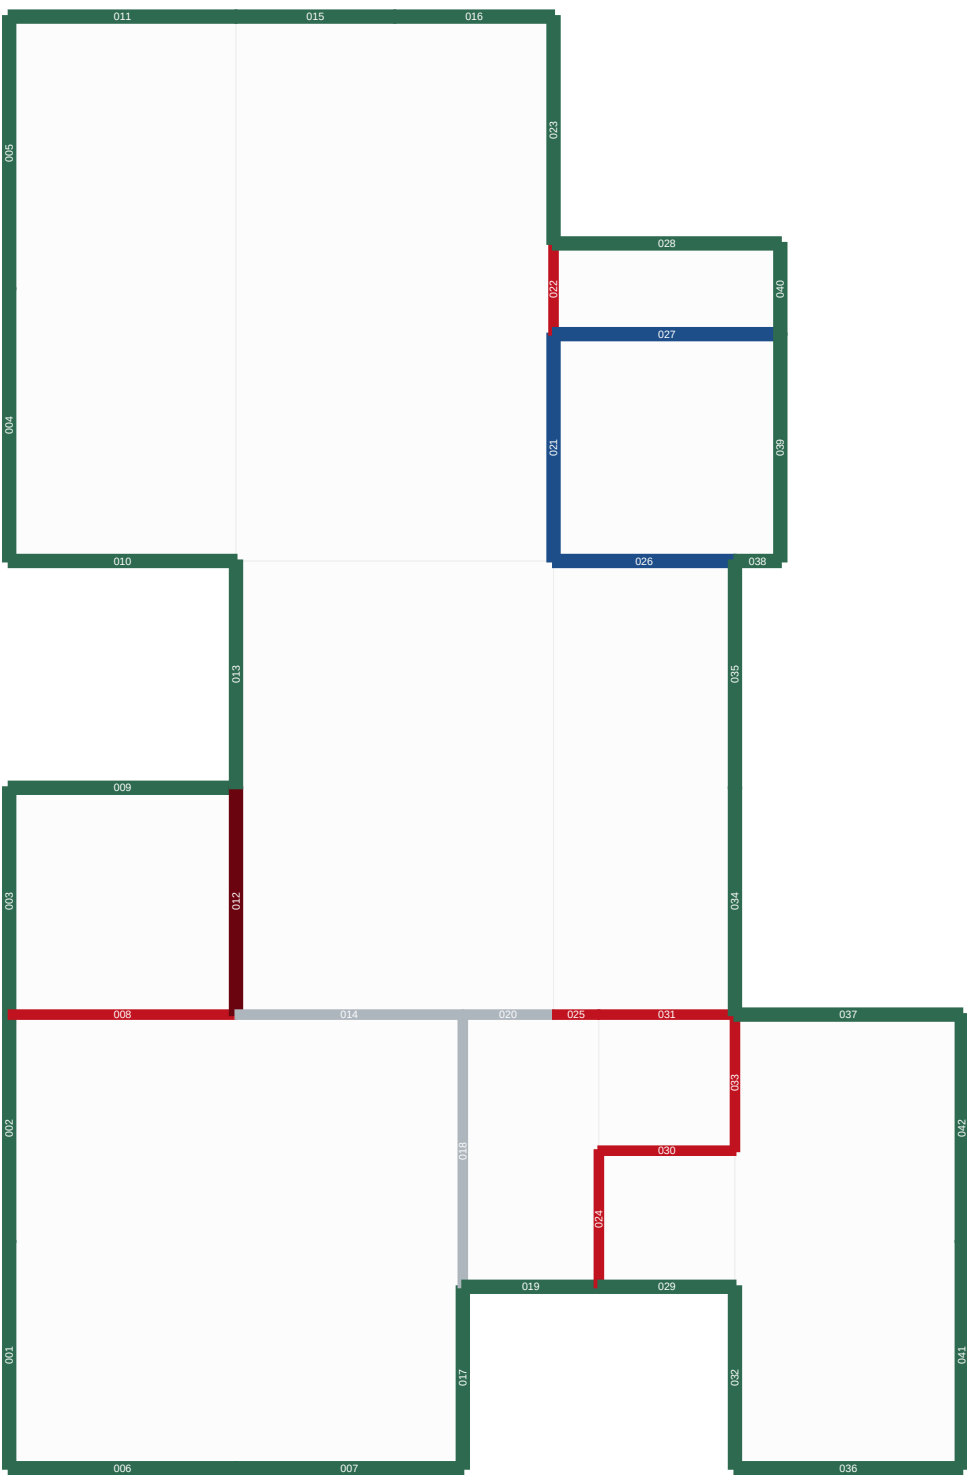

1 PAGINACAO — TERREO
ESCALA 1:100

QUANTITATIVO DE PAINES E MONTANTES

FAMILIA	PAINES	MONTANTES	PI de perfil	COMPOSICAO
PA-1	16	71	205,9	dupla chapa 12,5 + montante 48 x 16 x 40 + dupla chapa 12,5
PA-2	1	6	17,4	dupla chapa 12,5 + perfil oculto + montante 70 x 16 x 80
PE-1	47	253	733,7	linhas 32 x 80 x 50 (SDO enca) + montante 90 x 16 x 50 +
PA-3	3	17	49,3	perfil 60 x 12,5 + montante 90 x 16 x 50 + perfil 12,5 + rebordo
PI-1	3	16	46,4	perfil 12,5 + montante 70 x 16 x 50 + perfil 12,5
TOTAL	70	363	1052,7	



EXTRATO DA LISTA DE PAINES (26 de 70)

CODIGO	FAMILIA	LARGO (mm)	ALT (mm)	MONT.	PROV.
PT-001	PE-1	3000	2900	6	T
PT-002	PE-1	3000	2900	6	T
PT-003	PE-1	3000	2900	6	T
PT-004	PE-1	3000	2900	7	T
PT-005	PE-1	3000	2900	7	T
PT-006	PE-1	3000	2900	6	T
PT-007	PE-1	3000	2900	6	T
PT-008	PA-1	3000	2900	6	T
PT-009	PE-1	3000	2900	6	T
PT-010	PE-1	3000	2900	6	T
PT-011	PE-1	3000	2900	6	T
PT-012	PA-2	3000	2900	6	T
PT-013	PE-1	3000	2900	6	T
PT-014	PI-1	3000	2900	6	T
PT-015	PE-1	2100	2900	4	T
PT-016	PE-1	2100	2900	4	T
PT-017	PE-1	2400	2900	5	T
PT-018	PA-1	3000	2900	7	T
PT-019	PE-1	1800	2900	4	T
PT-020	PA-1	1200	2900	3	T
PT-021	PA-1	3000	2900	6	T
PT-022	PA-1	1200	2900	3	T
PT-023	PE-1	3000	2900	6	T
PT-024	PA-1	1800	2900	4	T
PT-025	PA-1	600	2900	2	T
PT-026	PA-1	2400	2900	6	T

- NOTAS
- * Painéis limitados a 3000 mm por manuseio e transporte.
 - * Montantes a cada 600 mm, 400 mm onde cabido no revestimento exigido.
 - * Não houve placa entre em moldes sem código, largura, altura, espessura, material e revestido.
 - * Numeração por pavimento, a família define a composição interna do painel.

PROJETO PORTO REAL

RESIDENCIA UNIFAMILIAR (MANAUS - AM) | SOUZA TATIANA-PS

PROJETO ARQUITETONICO

PAGINACAO DE PAINES — LIGHT STEEL FRAME

BASE GEOMETRICA
Lista Consolidada
Rev. R122 (preliminar)
UNIDADE: METROS - MM

ESCALA
1:100
FORMATO A1
MILIMETROS (50/50/50/50)

EMISSAO
ESTUDIO PRELIMINAR RTA
TUDO LIBERADO PARA OBRA
SEM ART / RNT

PROJETO
18
06-08-REV004