




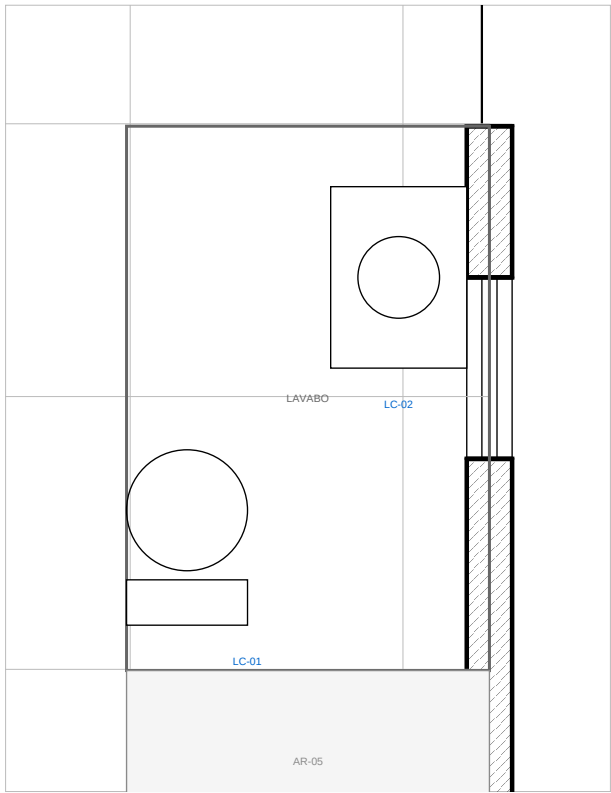


1 LAVABO SOB A ESCADA
ESCALA 1:25

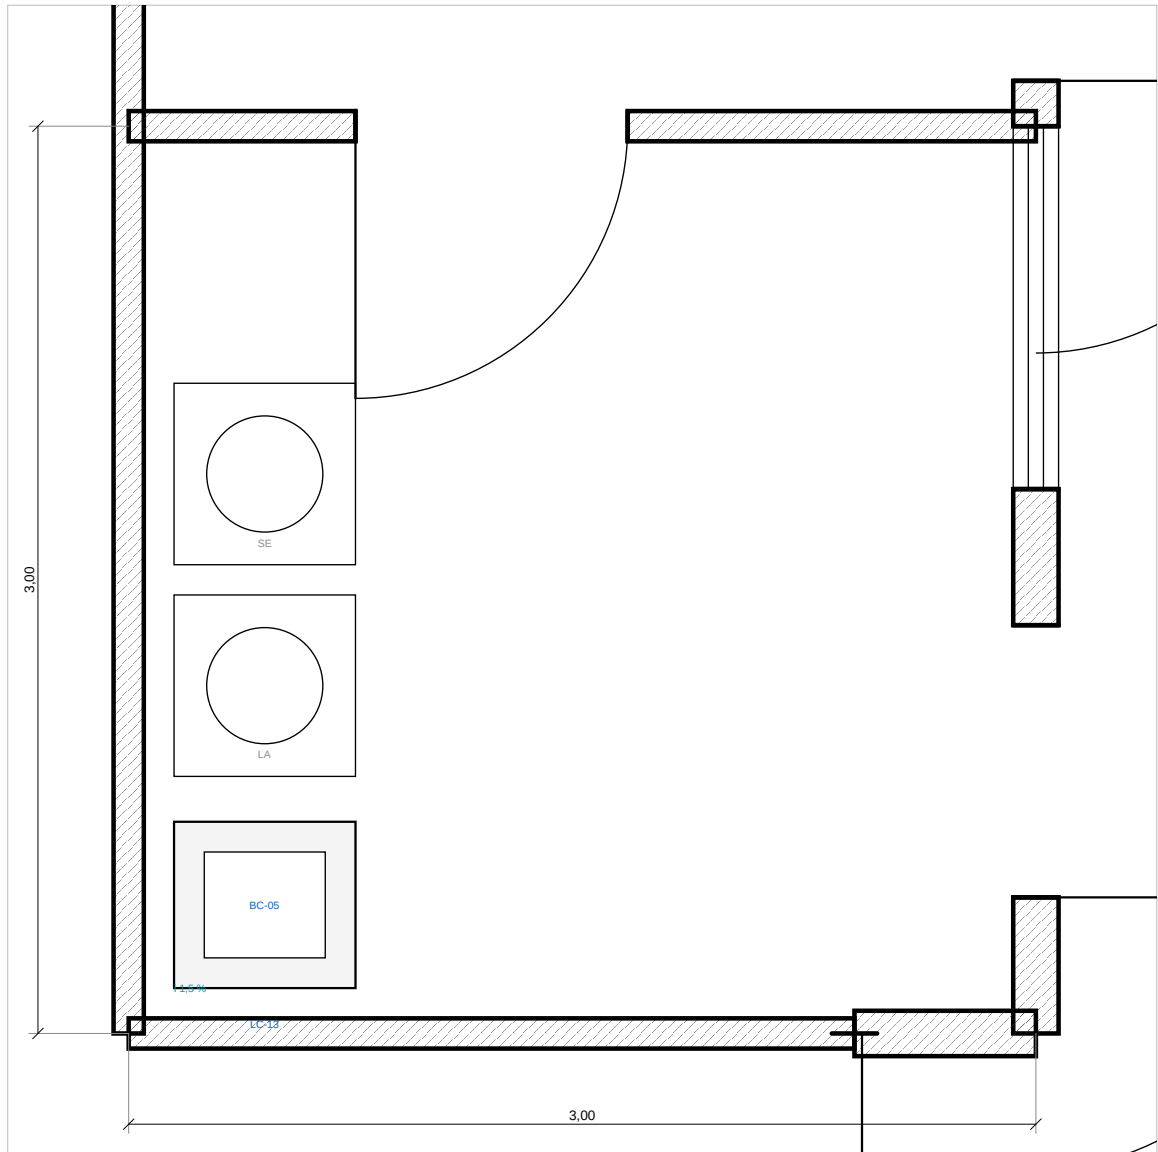

2 LAVANDERIA
ESCALA 1:25

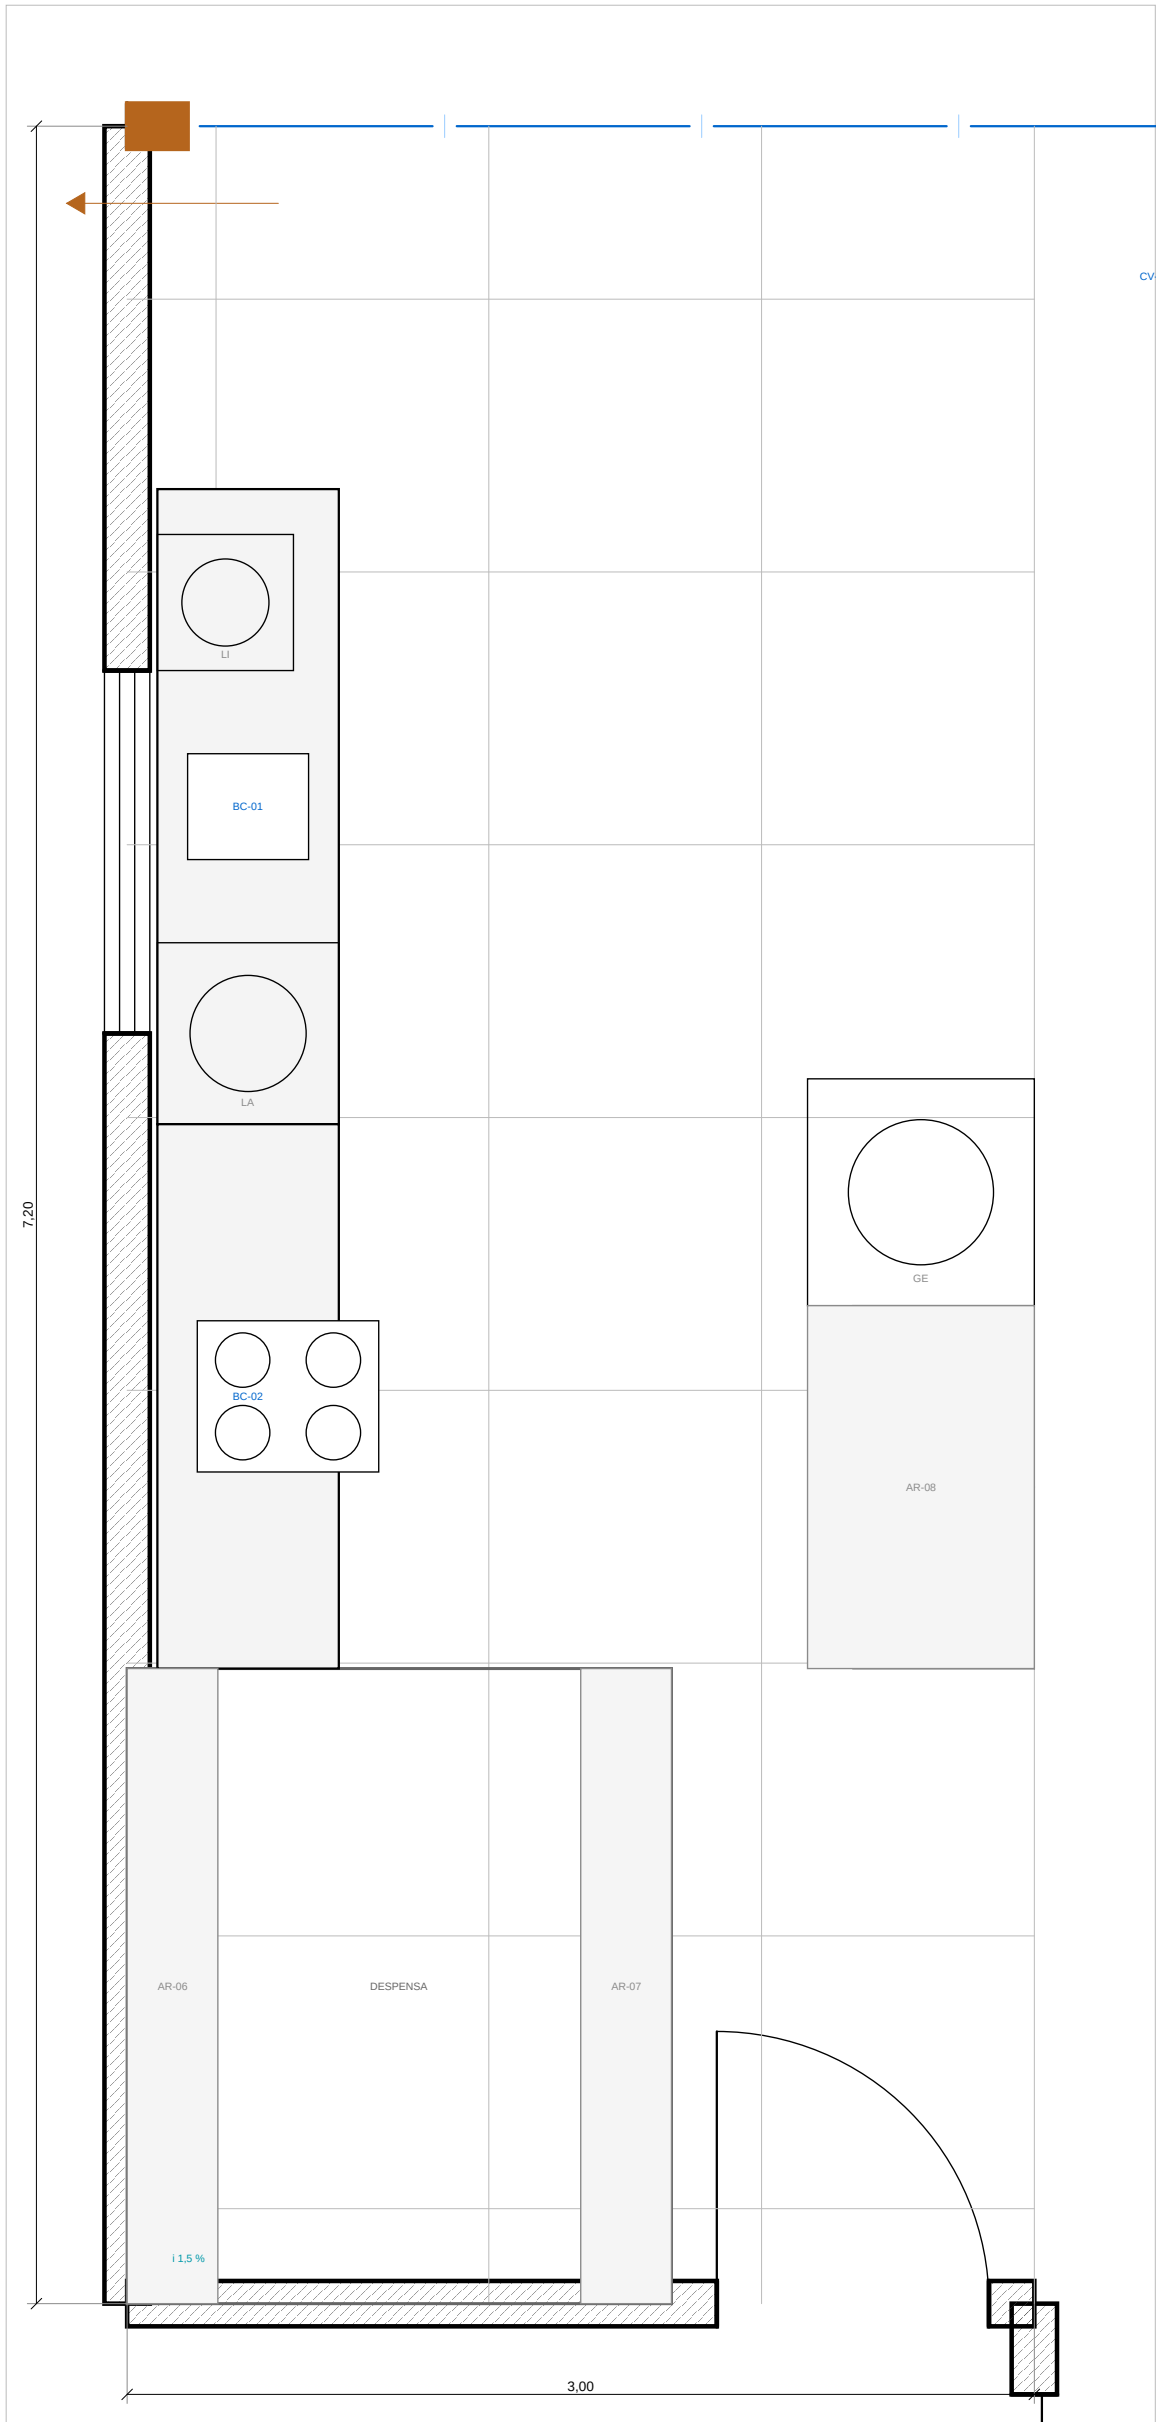

3 COZINHA
ESCALA 1:25

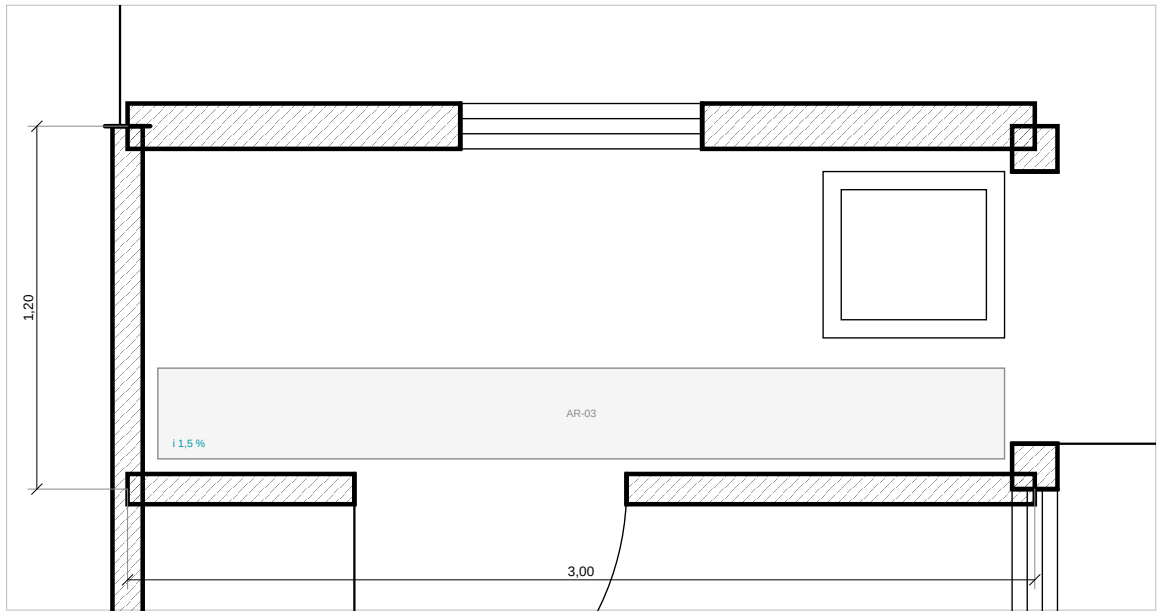

4 DEPOSITO / DML
ESCALA 1:25

PAGINACAO VERIFICADA — PECAS INTEIRAS + RECORTE EM CADA PONTA

AMB	AMBIENTE	ZONA	PEÇA	EXTO X	EXTO Y	ALTURA (mm)
T-001	LAVABO SOB A ESCADA	ZP-1	WC	2 x 900/900	0 x 900	—
T-002	LAVANDERIA	ZP-1	WC	9 x 900	4 x 900	1800 (2 Ruas + 100)
T-003	COZINHA	ZP-1	WC	3 x 2400	7 x 3120/10	—
T-004	DEPOSITO / DML	ZP-1	WC	9 x 900	1 x 900	1800 (2 Ruas + 100)

NOTAS

- Plano de piso em linha fina, a malha vem da ZONA de paginação, não do canto do ambiente.
- Plano de piso porcelanado retificado 900 x 900, parede cerâmica retificada 300 x 600, junta 2 mm.
- Cimento de 1,5 % para o piso em toda área molhada, solaria elevada 15 mm nos bicos.
- Representação: planta líquida em 2 dimensões, subindo 300 mm na parede e 1.800 mm nos bicos.

PROJETO PORTO REAL

RESIDENCIA UNIFAMILIAR (MARIA) - AM | 100% TATIANA-PS

PROJETO ARQUITETONICO

AMPLIACOES DE AREA MOLHADA — TERREO

BASE GEOMETRICA Linha Consolidada Projeto (previsão) UNIDADE: METRO - MM	ESCALA 1:25 FORMATO A1 MILHA 400/500/100	EXIBICAO ESTUDIO PRELIMINAR R74 Linha Consolidada PARA ORCA SEM ART / INT	PROJETO 22 06-08-REV014
---	---	--	-------------------------------