




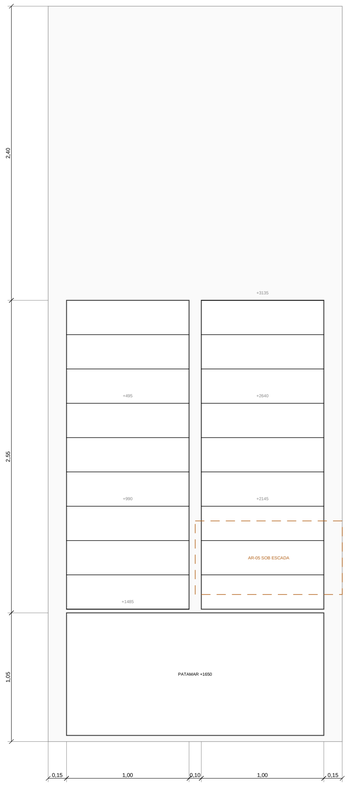

## 1 PLANTA DA ESCADA


ESCALA 1:25

**VERIFICACAO DA ESCADA**

| ITEM | PROJETO | NORMA | |
|---|---|---|---|
| Espelho | 165.00 mm | 16 a 18 cm (NBR 9077) | OK |
| Piso | 280 mm | min 28 cm | OK |
| Blondel (2h + p) | 610.0 mm | 600 a 650 mm | OK |
| Largura util do lance | 1000 mm | min 1.200 mm (uso coletivo) / 1.000 mm (unifamiliar) | OK |
| Patamar | 1000 mm | >= largura do lance | OK |
| Altura livre minima | 2979 mm | min 2100 mm | OK |
| Guarda-corpo | 1100 mm | min 1.100 mm (NBR 14718) | OK |
| Corrimao | 920 e 700 mm | duplo, 92 cm e 70 cm (NBR 9050) | OK |
| Espelho fechado | sim | obrigatorio em rota acessivel | OK |
| Desnivel vencido | 3300 mm | 20 x 165.00 mm | OK |


**O QUE A PLANTA NAO MOSTRA**

| QUESTAO | RESPOSTA |
|---|---|
| Por que o primeiro espelho sobe de y = 13.200 | o patamar terminava 100 mm dentro da projecao do hall superior, com 1.500 mm de altura livre — uma quina na altura da cabeca de quem termina o primeiro lance |
| Por que a verificacao de altura livre e tridimensional | altura livre de escada e o unico defeito que nao aparece em planta nenhuma: depende da cota do degrau e da cota do que ha acima dele |
| O que ha sob o segundo lance | triangulo com altura util variavel, declarado como armario (AR-05); nao e circulacao nem espaco morto |
| Por que espelho fechado | degrau vazado prende a ponta do pe de quem usa bengala ou tem mobilidade reduzida (NBR 9050) |
| Por que corrimao duplo | 920 mm para adulto e 700 mm para crianca; em casa com escada aberta para a sala, o segundo corrimao e o que realmente se usa |

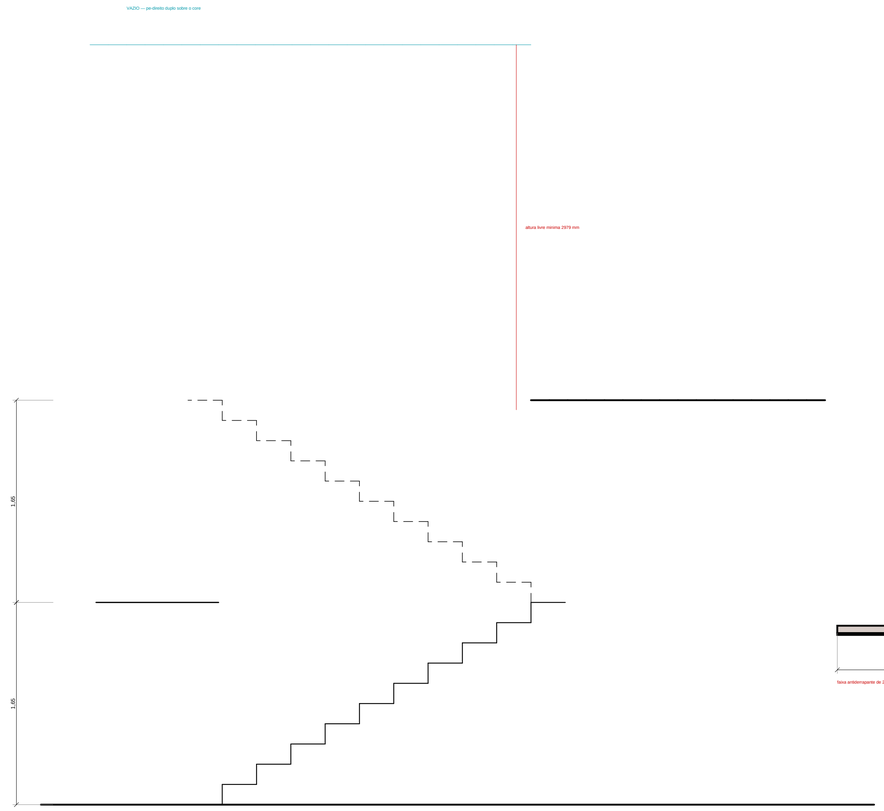


## 2 CORTE LONGITUDINAL — ALTURA LIVRE

ESCALA 1:25

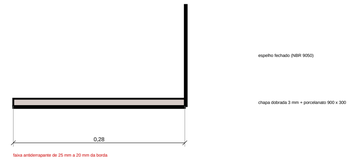


## 3 DETALHE DO DEGRAU

ESCALA 1:5

**NOTAS**

- 20 espelhos de 165.00 mm e piso de 280 mm. Blondel 2h + p = 610.0 mm (faixa recomendada 600 a 650).
- Altura livre minima 2100 mm (NBR 9077), verificada degrau a degrau contra a laje e o vazio acima.
- Guarda-corpo 1100 mm; corrimao duplo em 920 e 700 mm (NBR 9050).
- dois perfis U 200 laterais com degraus em chapa dobrada 3 mm

**PROJETO PORTO REAL**

RESIDENCIA UNIFAMILIAR | MANAUS - AM | SUSI TARUMA (H)

PROJETO ARQUITETONICO

**ESCADA — DESENHO EXECUTIVO**

| BASE GEOMETRICA | ESCALA | EMISSAO | PRANCHA |
|---|---|---|---|
| Lista Consolidada<br>pos-R32 (prevalece) | **indicada**<br>FORMATO A3<br>MALHA 600/300/150 | ESTUDO PRELIMINAR R74<br>NAO LIBERADO PARA OBRA<br>SEM ART / RRT | **25**<br>de 66 REV R74 |
| UNIDADE MESTRE: mm | | | |