



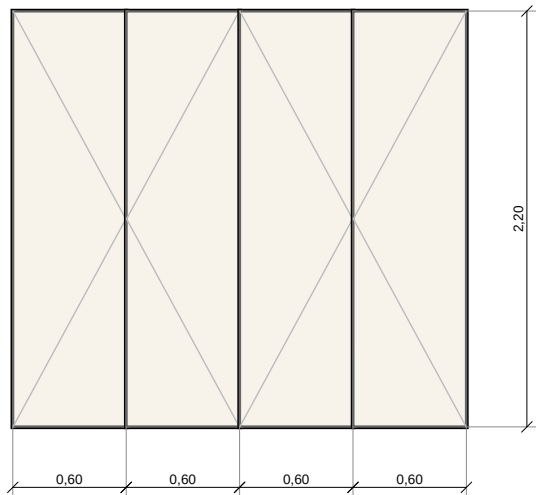


1 AR-12 GUARDA-ROUPA
ESCALA 1:40

4 mod. 4 pontos 0 gar 160 pontos - caixa colada a 40 graus (sem)

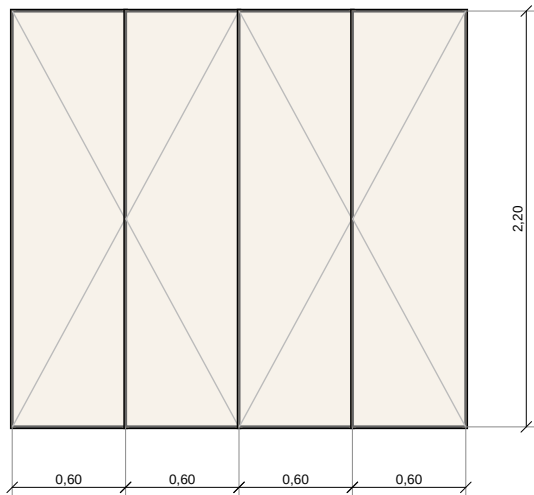


2 AR-13 GUARDA-ROUPA
ESCALA 1:40

4 mod. 4 pontos 0 gar 160 pontos - caixa colada a 40 graus (sem)

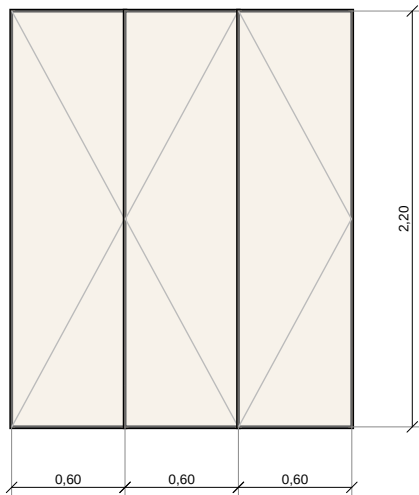


3 AR-11 GUARDA-ROUPA
ESCALA 1:40

3 mod. 3 pontos 0 gar 150 pontos - caixa colada a 40 graus (sem)

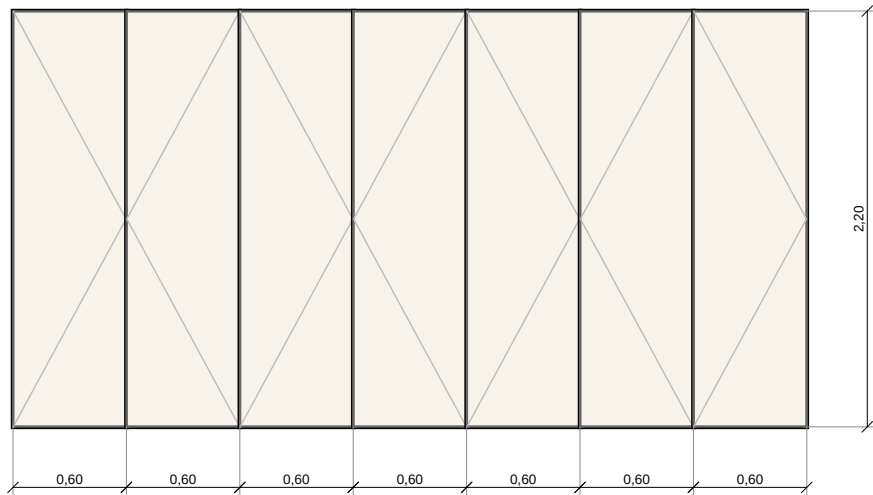


4 AR-09 ROUPARIA
ESCALA 1:40

7 mod. 7 pontos 0 gar 170 pontos - perfil galo de alumínio gal

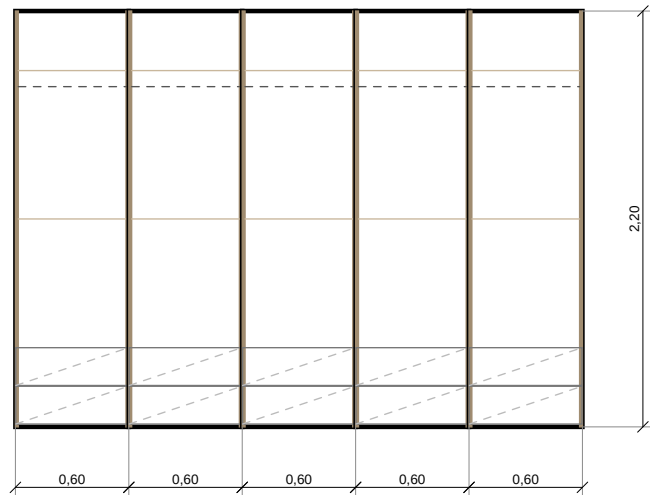


5 CLOSET — PAREDE DO FUNDO
ESCALA 1:40

5 mod. 5 pontos 10 gar 160 pontos - caixa colada a 40 graus (sem)

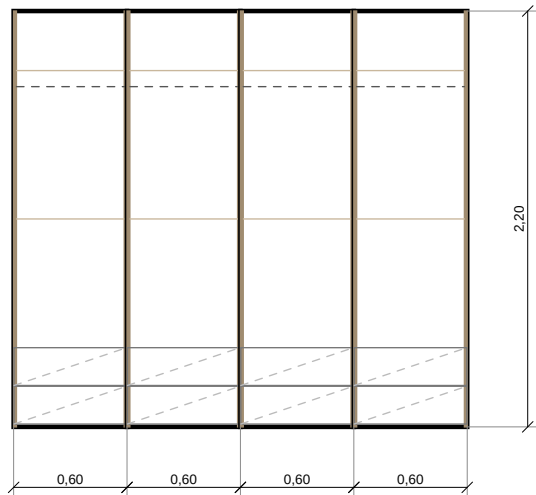


6 CLOSET — PAREDE LATERAL
ESCALA 1:40

4 mod. 4 pontos 0 gar 160 pontos - caixa colada a 40 graus (sem)

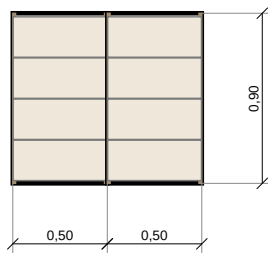

7 AR-14 GAVETEIRO
ESCALA 1:40

2 mod. 2 pontos 0 gar 160 pontos - caixa colada a 40 graus (sem)

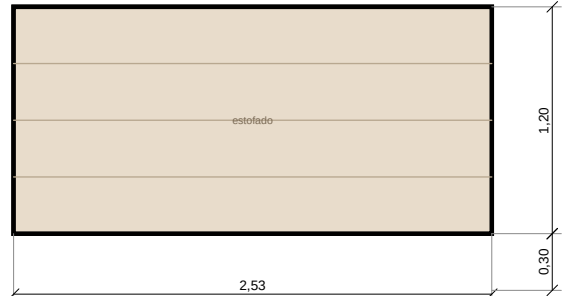


8 LY-12 CABECEIRA ESTOFADA
ESCALA 1:40

2 mod. 2 pontos 0 gar 160 pontos - caixa colada a 40 graus (sem)




9 LY-10 CABECEIRA ESTOFADA
ESCALA 1:40

1 mod. 1 pontos 0 gar 160 pontos - caixa colada a 40 graus (sem)

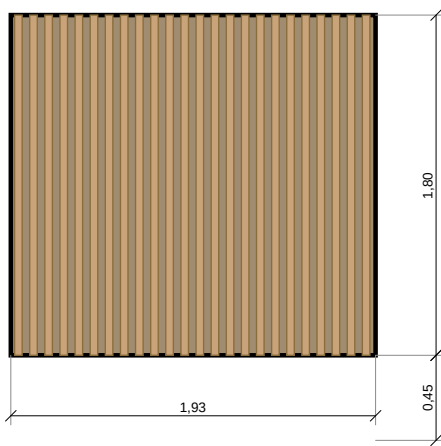


10 LY-15 PAINEL TV
ESCALA 1:40

1 mod. 1 pontos 0 gar 200 pontos - caixa colada a 40 graus (sem)

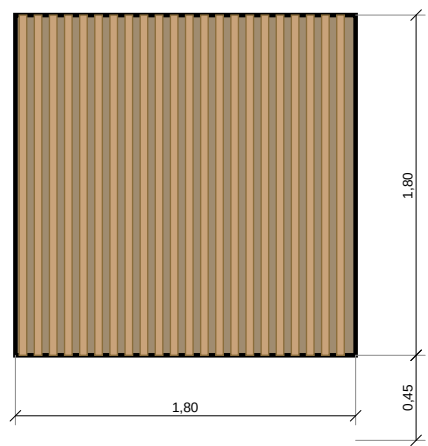


11 LY-03 PAINEL RIPADO DA TV
ESCALA 1:40

2 mod. 2 pontos 0 gar 160 pontos - perfil galo de alumínio gal

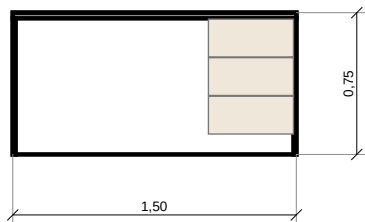


13 LY-13 MESA
ESCALA 1:40

1 mod. 1 pontos 0 gar 200 pontos - caixa colada a 40 graus (sem)

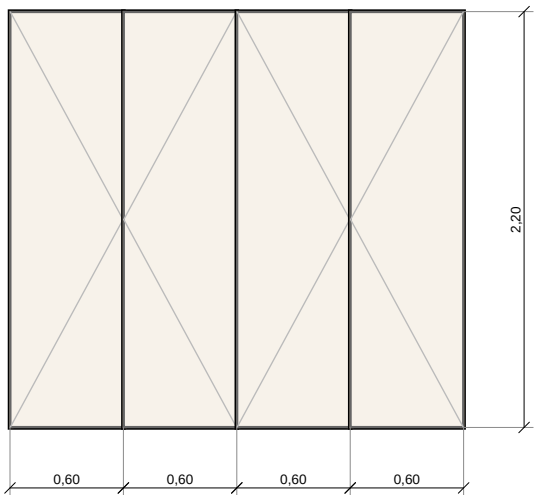


14 AR-04 ARMARIO ALTO
ESCALA 1:40

4 mod. 4 pontos 0 gar 160 pontos - perfil galo de alumínio gal

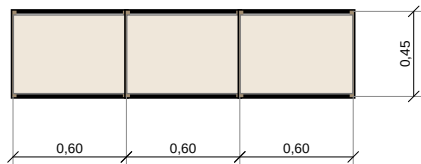

12 LY-04 RACK
ESCALA 1:40

3 mod. 3 pontos 0 gar 200 pontos - perfil galo de alumínio gal

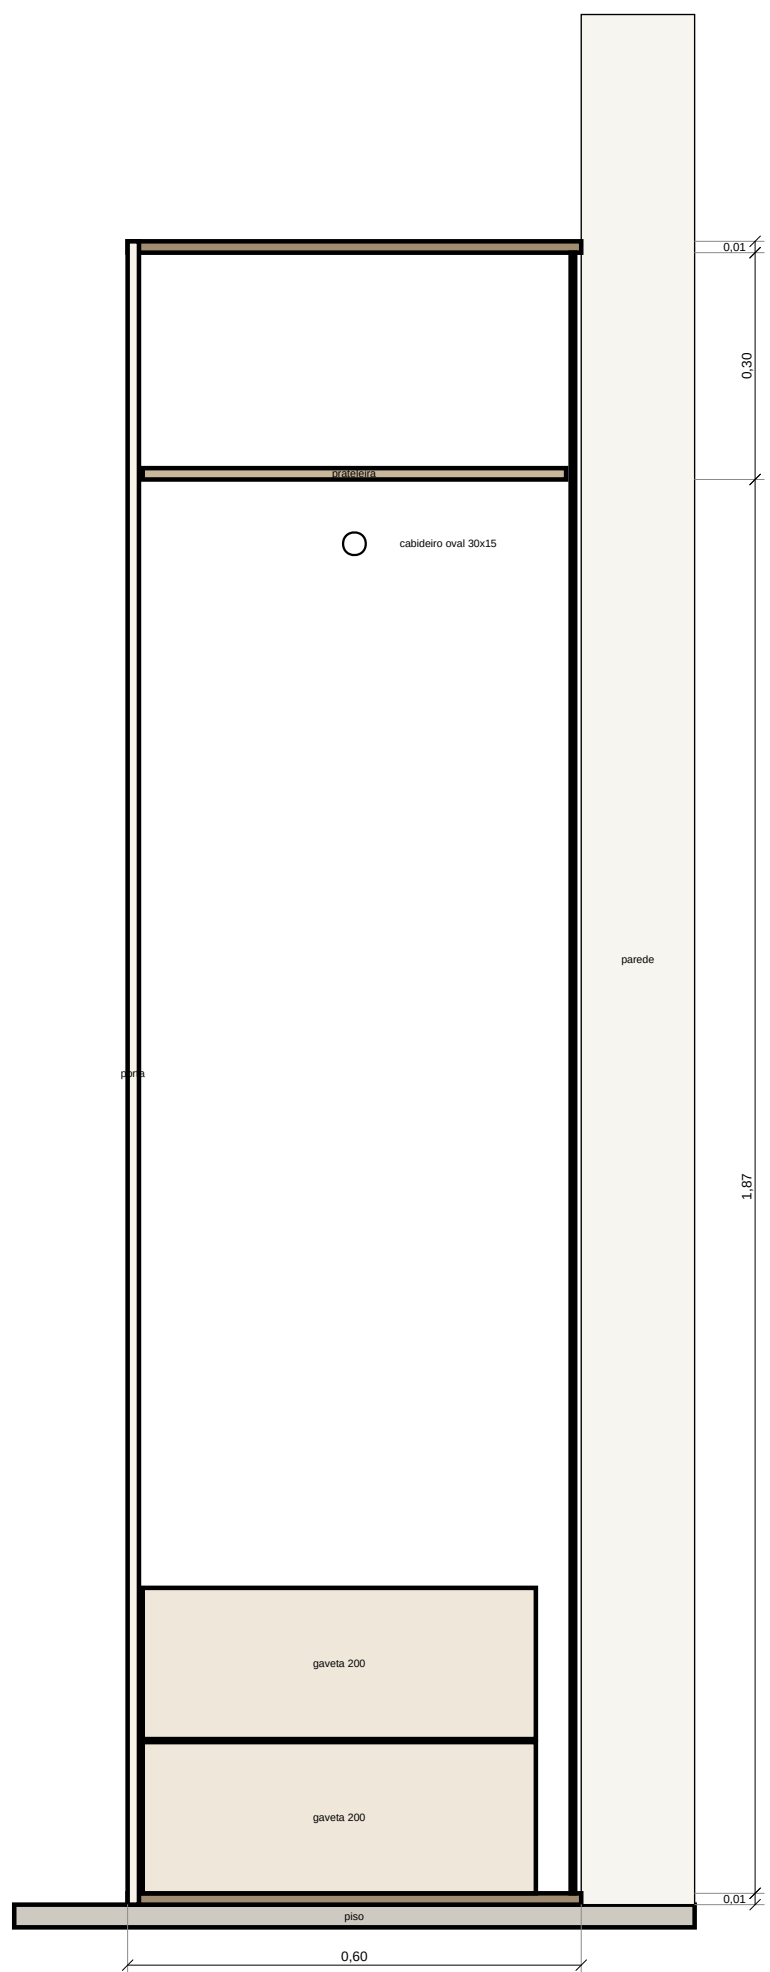

A SECAO DO MODULO DE GUARDA-ROUPA — 600 x 2.200
ESCALA 1:10

NOTAS

- * Guarda-roupa por modulo, cabideiro a 400 mm do topo, prateleira sobre ele e duas gavetas internas de 200 mm, porta interna.
- * Closet: os restantes modulos sem porta, mas duas portas declaradas em SUBDIVISÕES.
- * Cabeceira estofada: todo da cama mais 200 mm de cada lado, 1.200 mm de altura, sobre painel de MDF 15 mm fixado na parede.
- * Painel de TV ripado na largura do rack: ripos de 40 x 40 a cada 80 cm sobre fundo de 15 mm: cablo passa entre os ripos.
- * Mesa de trabalho da cozinha: sempre engastada (2 x 1,5 mm), paineis laterais e gaveteiro de 400.

PROJETO PORTO REAL

RESIDENCIA UNIFAMILIAR (MARAUAS - AM) | SOUZA TARTAGLIA-PS

PROJETO ARQUITETONICO

MARCENARIA II — ROUPEIROS, CLOSET, GAVETEIRO, CABECEIRAS E PAINELS

BASE GEOMETRICA	ESCALA	EMISSAO	PROJECION
Lista Consolidada	1:40	ESTUDIO PRELIMINAR RTA	
em PDF (previsão)	FORMATO A1	NAO LIBERADO PARA CRIA	
UNIDADE METRICA: mm	MILIMETROS (50/100/200)	SEM ART / RNT	57