


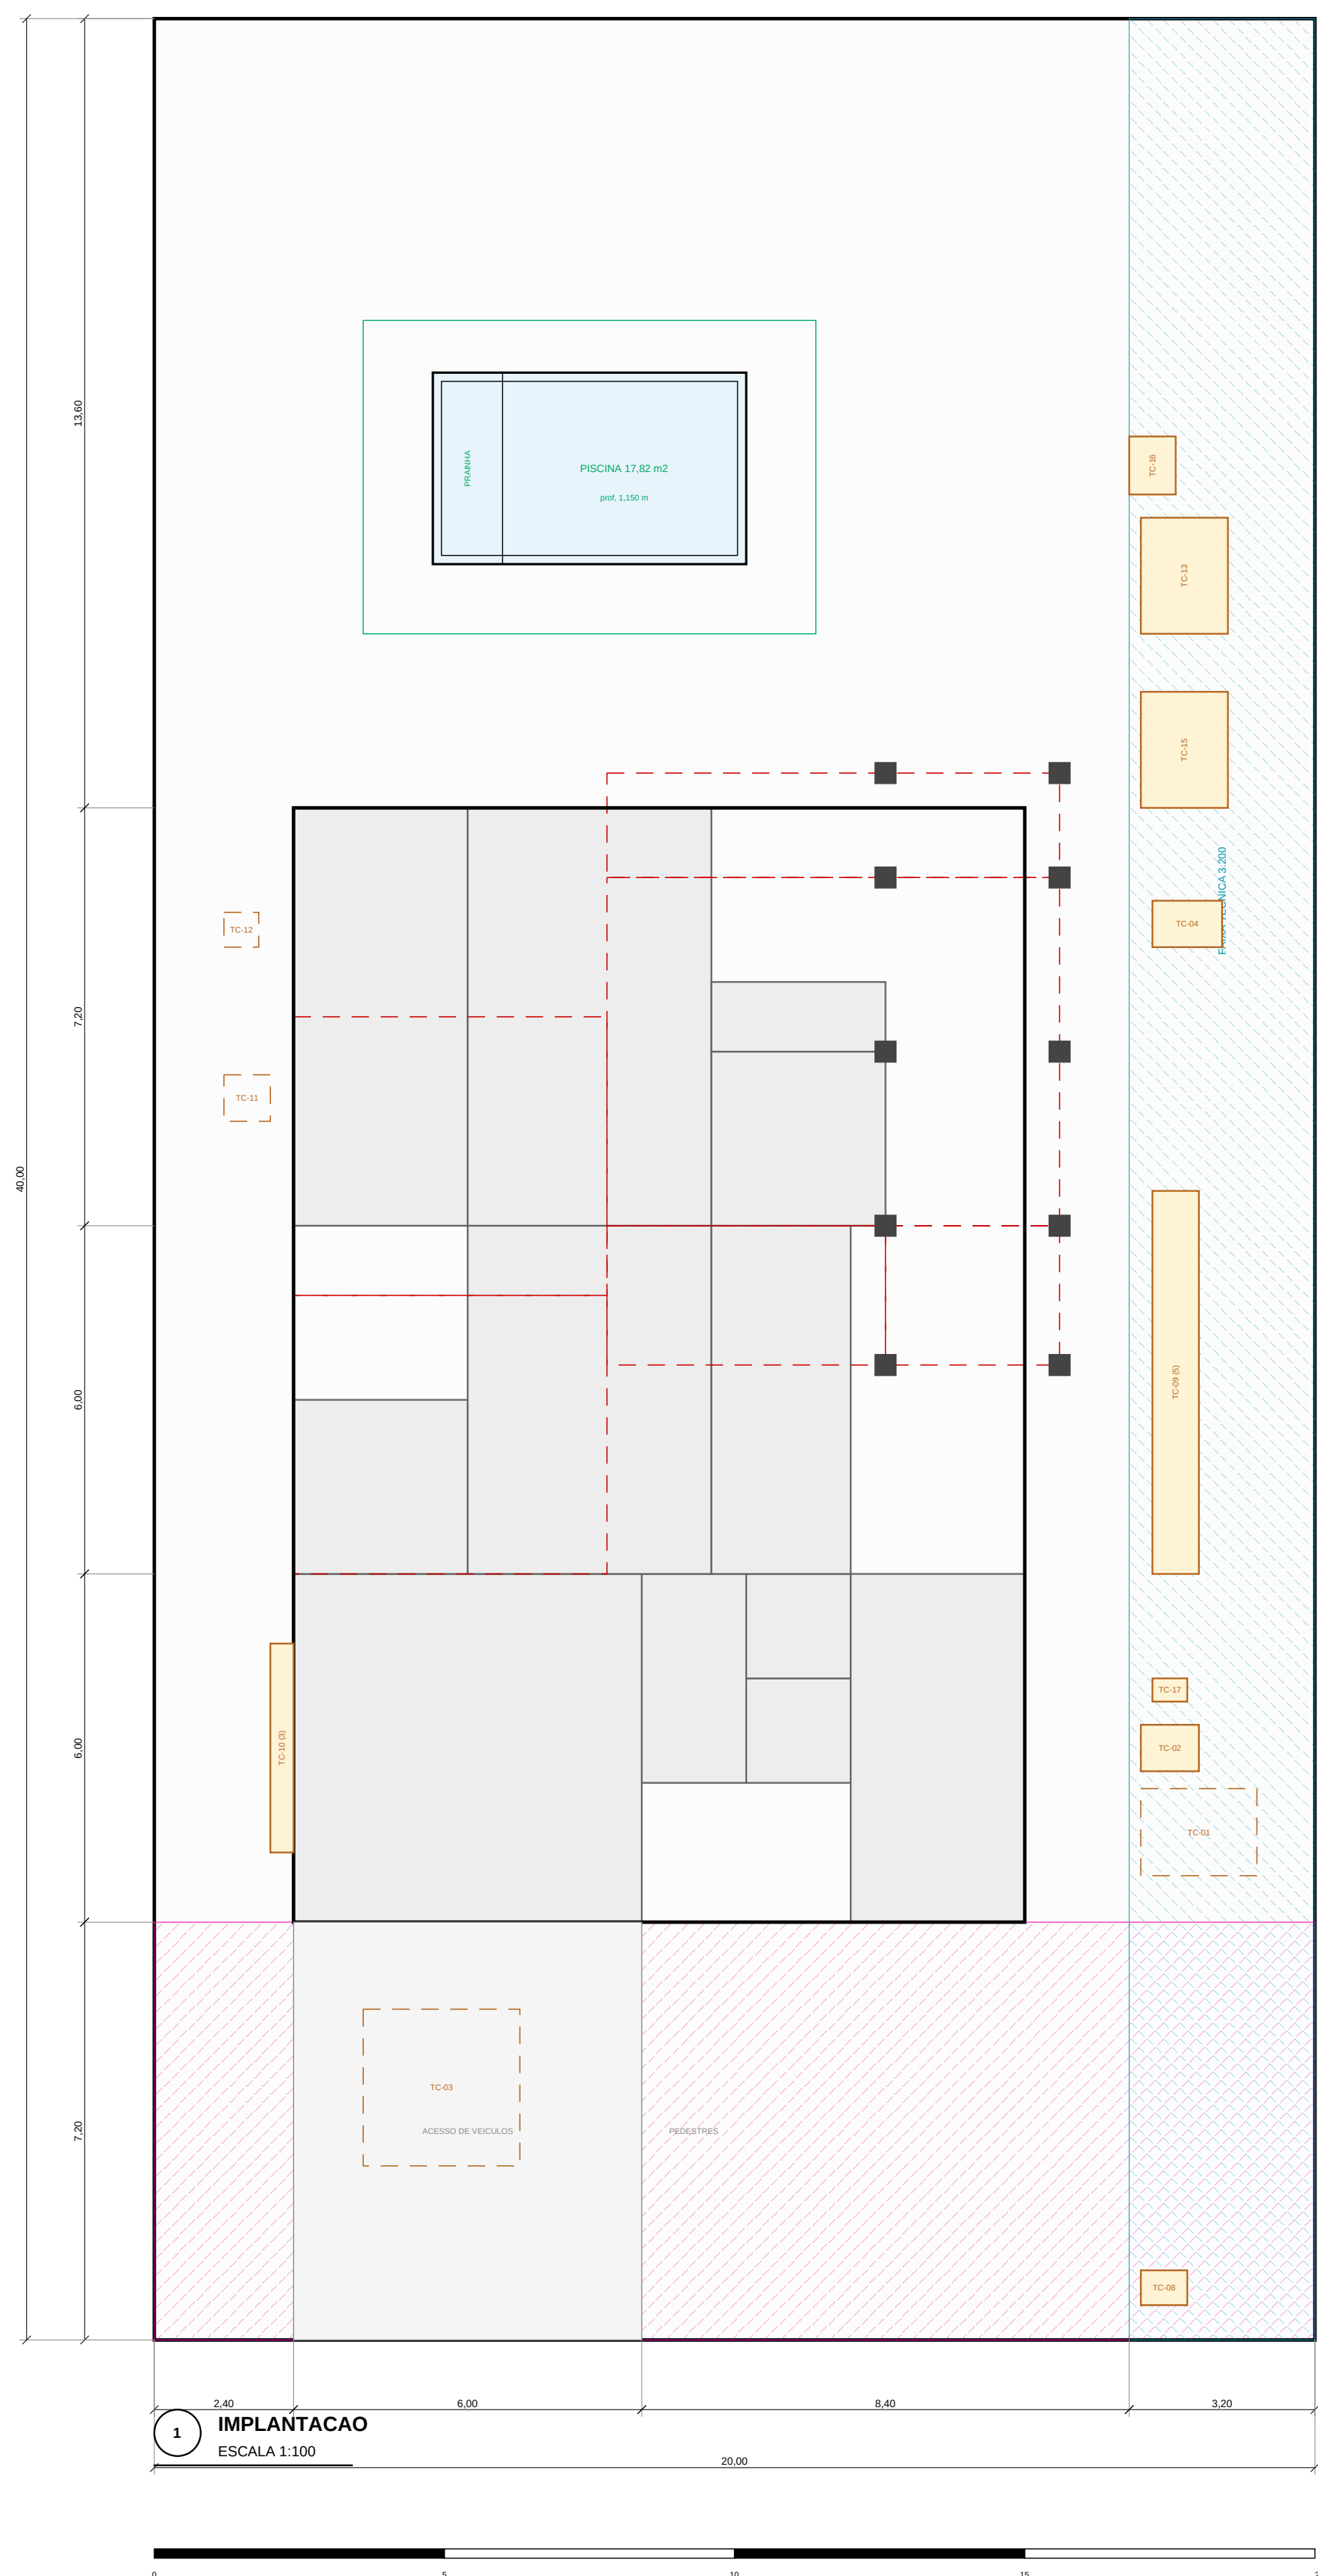

PARAMETRO	PROJETO	LIMITE	
Taxa de ocupação	32,21 %	max 50 %	OK
Coef. de aproveitamento	0,372	max 1,00	OK
Cobertura	2 pavimentos	max 4	OK
Recuo frontal	7000 mm	condomínios SGU2 (II)	OK
Recuo lateral eqs.	2400 mm	sem parâmetro definido	OK
Faixa bruta de div.	3300 mm	min 3000 mm	OK
Recuo de fundo	13500 mm	min 5000 mm	OK

NOTAS

- Lote 20.000 x 40.000 mm = 800.000 m².
- Recuos: frontal 7.200 / lateral esq. 2.400 / faixa técnica dir. 3.200 / fundo 13.600 mm.
- Parâmetros de 5/25 Tarumã/Tarumã-Açu são hipóteses (H) — pendente: certidão de uso do solo.
- Seis muro frontal, muros laterais e de fundo h = 2.200 mm.

PROJETO PORTO REAL

RESIDÊNCIA UNIFAMILIAR | MANAUS - AM | SU16 TARUMA (H)

PROJETO ARQUITETÔNICO

IMPLANTACAO E SITUACAO

BASE GEOMÉTRICA	ESCALA	EMISSÃO	PROJEÇÃO
Lista Consolidada	1:100	ESTUDO PRELIMINAR R77	01
pro-R22 (previável)	FORMATO A1	NÃO LIBERANDO PARA OBRA	
ENDEIXO MESTRE: 100	MAI/14 000/000/00	SER. ART. 1 / 001	
			de 18 REV R77