


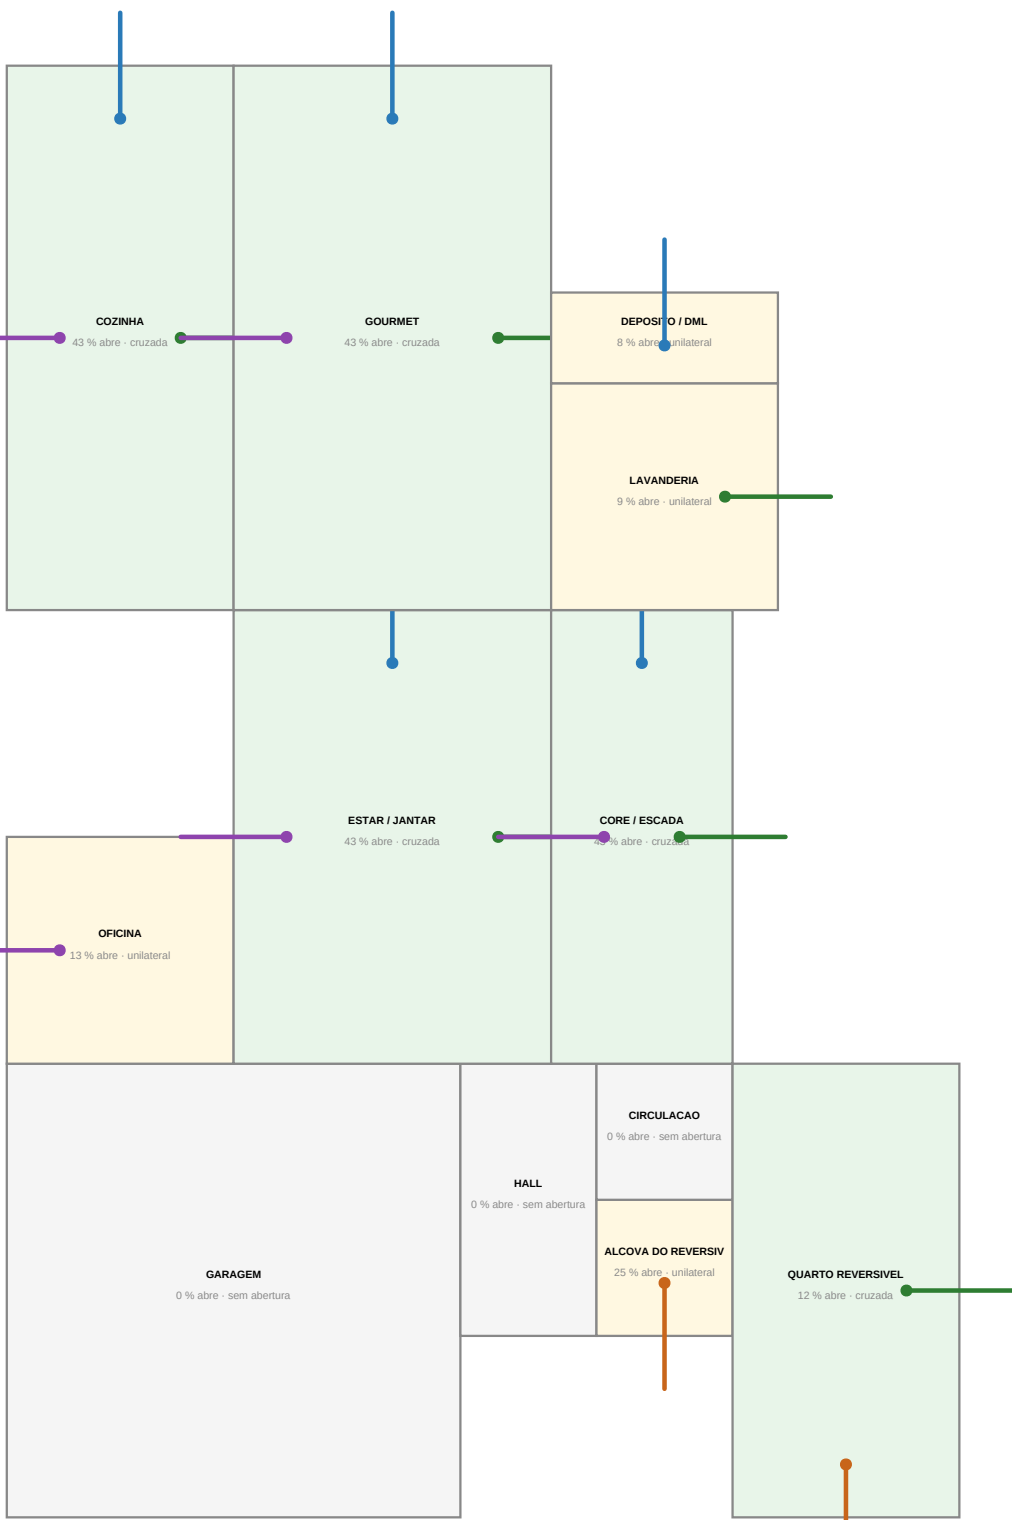


1 TERREO — faces que abrem
ESCALA 1:100

VENTILACAO POR AMBIENTE									
COD	AMBIENTE	CAT.	PROJE	ABRETE	PERIM	FACIES	TIPO	ISOV	
T-GAR	GARAGEM	INTER	34,3	0,00	0%	—	—	YES	
T-HALL	HALL	CRUZADA	9,8	0,00	0%	—	—	YES	
T-ALC	ALCOVA DO REVERSIVEL	INTER	2,8	0,72	25%	L	unidiret	OK	
T-COR	CIRCULACAO	CRUZADA	2,8	0,00	0%	—	—	YES	
T-REV	QUARTO REVERSIVEL	INTER	26,7	2,04	22%	L, N	cruzada	OK	
T-OFI	OFICINA	ALCOVA	4,3	1,08	22%	S	unidiret	YES	
T-BOC	ESTAR/JANTAR	ALCOVA	86,7	36,86	42%	N, D, S	cruzada	OK	
T-COR	CORR. E ESCADA	CRUZADA	86,7	36,86	42%	N, D, S	cruzada	YES	
T-COZ	COZINHA	ALCOVA	86,7	36,86	42%	N, D, S	cruzada	OK	
T-GOU	GOURMET	ALCOVA	86,7	36,86	42%	N, D, S	cruzada	OK	
T-LAV	LAVANDERIA	INTERIO	6,3	0,72	9%	N	unidiret	YES	
T-DEP	DEPOSITO DmL	INTERIO	3,1	0,24	8%	O	unidiret	YES	
S-S02	SUITE 02	INTER	26,5	2,04	8%	L, S	cruzada	OK	
S-S03	SUITE 03	INTER	26,7	2,04	8%	O, S	cruzada	OK	
S-HALL	HALL E REPOUSAR	CRUZADA	10,8	0,00	0%	—	—	YES	
S-LOU	MINI LOUNGE / TV	ALCOVA	6,5	0,72	11%	N	unidiret	OK	
S-MAST	SUITE MASTER	INTER	45,1	7,80	17%	N, D, S	cruzada	OK	

PRIVACIDADE — CADA JANELA CONTRA A DIVISA QUE OLHA (art. 1.301 CC)

VIAJ	AMB	FACIE	ISOV. m	AMB. m	PERIM. m	BRISA	LEITURA	
004	T-REV	N	0,00	1,00	1000	—	distante	OK
002	T-COR	N	0,00	1,00	1000	—	distante	OK
005	T-REV	L	7,20	—	1100	BR-L	nao	OK
001	T-REV	N	0,00	1,00	1100	—	distante	OK
001	T-ALC	L	0,00	—	1100	—	nao	OK
003	T-COR	S	3,40	1,00	1100	—	exposta ao vento	OK
001	T-COZ	S	3,40	1,00	1100	—	exposta ao vento	OK
001	T-LAV	N	7,40	1,00	1100	—	distante	OK
004	T-DEP	O	36,90	1,00	1000	—	distante	OK
PR02	T-COR	N	8,00	1,00	9	—	distante	OK
PR02	T-GOU	N	10,40	1,00	9	—	distante	OK
CR05	T-GOU	O	13,00	1,00	9	BR-O	protetida por terra	OK
PR02	T-BOC	S	9,40	1,00	9	—	distante	OK
001	S-LOU	N	4,40	1,00	1100	—	distante	OK
005	S-S02	S	3,40	1,00	1100	—	exposta ao vento	OK
001	S-S02	L	13,20	—	1100	BR-L	nao	OK
004	S-S02	L	13,20	—	1000	BR-L	nao	OK
005	S-S03	S	3,40	1,00	1100	—	exposta ao vento	OK
001	S-S03	O	17,20	1,00	1100	—	distante	OK
004	S-S03	S	2,40	1,00	1000	—	exposta ao vento	OK
005	S-MAST	S	7,80	1,00	1100	—	distante	OK
PR02	S-MAST	O	14,80	1,00	9	—	distante	OK
004	S-MAST	N	4,40	1,00	1000	—	distante	OK
001	S-MAST	N	4,40	1,00	1100	—	distante	OK

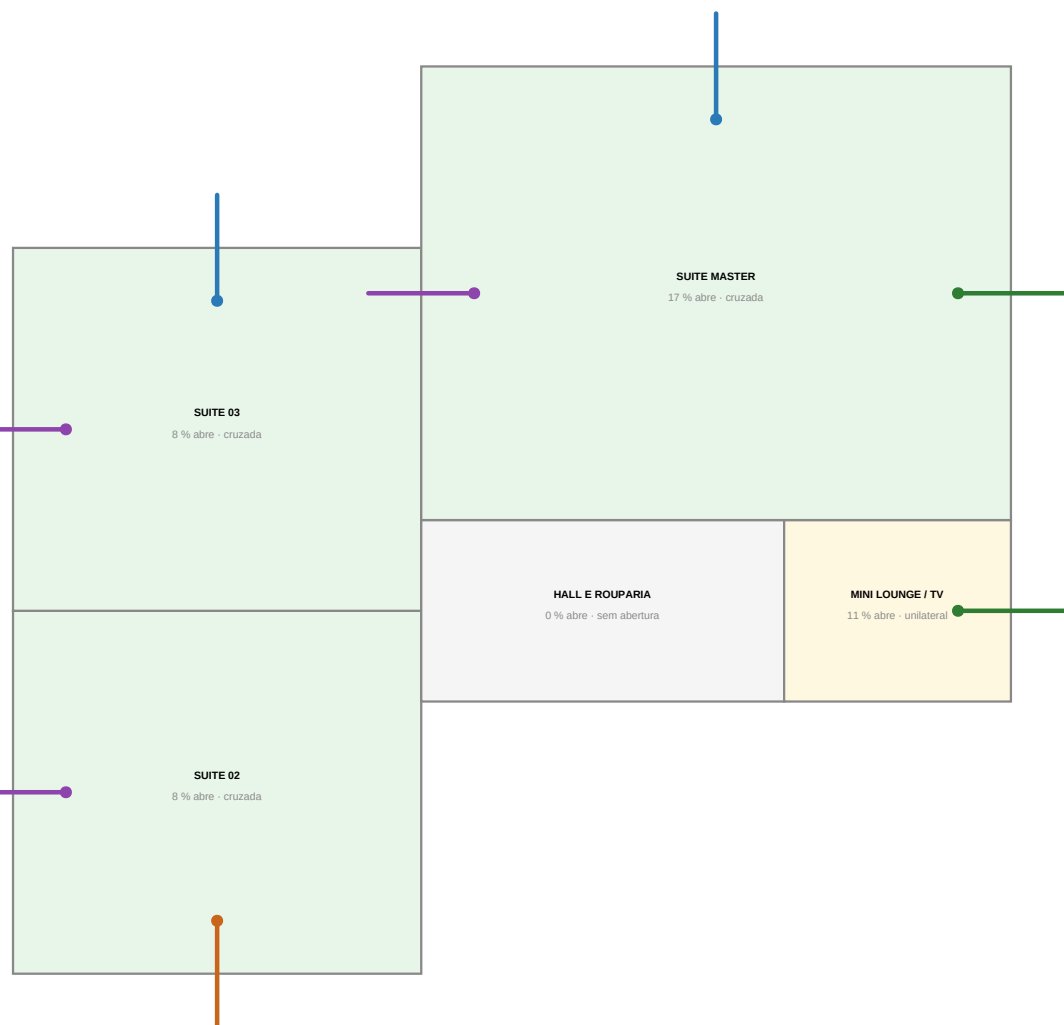

2 SUPERIOR — faces que abrem
ESCALA 1:100

NOTAS

* Área que ABRE por ambiente contra a área de piso. NBR 15275-4 exige 8% na região Norte. NBR 15275-3 recomenda 40% na ZSB (abertura grande).

* Facies que abre por fachada (FC) contra a parede lateral 200%, janela de corte 50%, basculante 33%, porta opaca 0%.

* Privacidade pelo art. 1.301 do Código Civil: janela que olha a divisa a menos de 2,50 m e protreta. O brisa que protege esta norma.

* Seis em cada face com abertura, duas de mais faces = ventilação cruzada.

PROJETO PORTO REAL

RESIDENCIA UNIFAMILIAR (MANAUS - AM) | SUE TATIANA PI

PROJETO ARQUITETONICO

VENTILACAO NATURAL, CRUZADA E PRIVACIDADE

BASE GEOMETRICA	ESCALA	EMISSAO	PRIVACIA
Unia Consolidada	1:100	ESTUDIO PRELIMINAR R77	49
Projeto (previsão)	FORMATO A1	NAO LIBERADO PARA OBRA	SEM ART / RNT
UNIDADE MESTRE: AM	MANAUS 65500000		06-09-REV077