


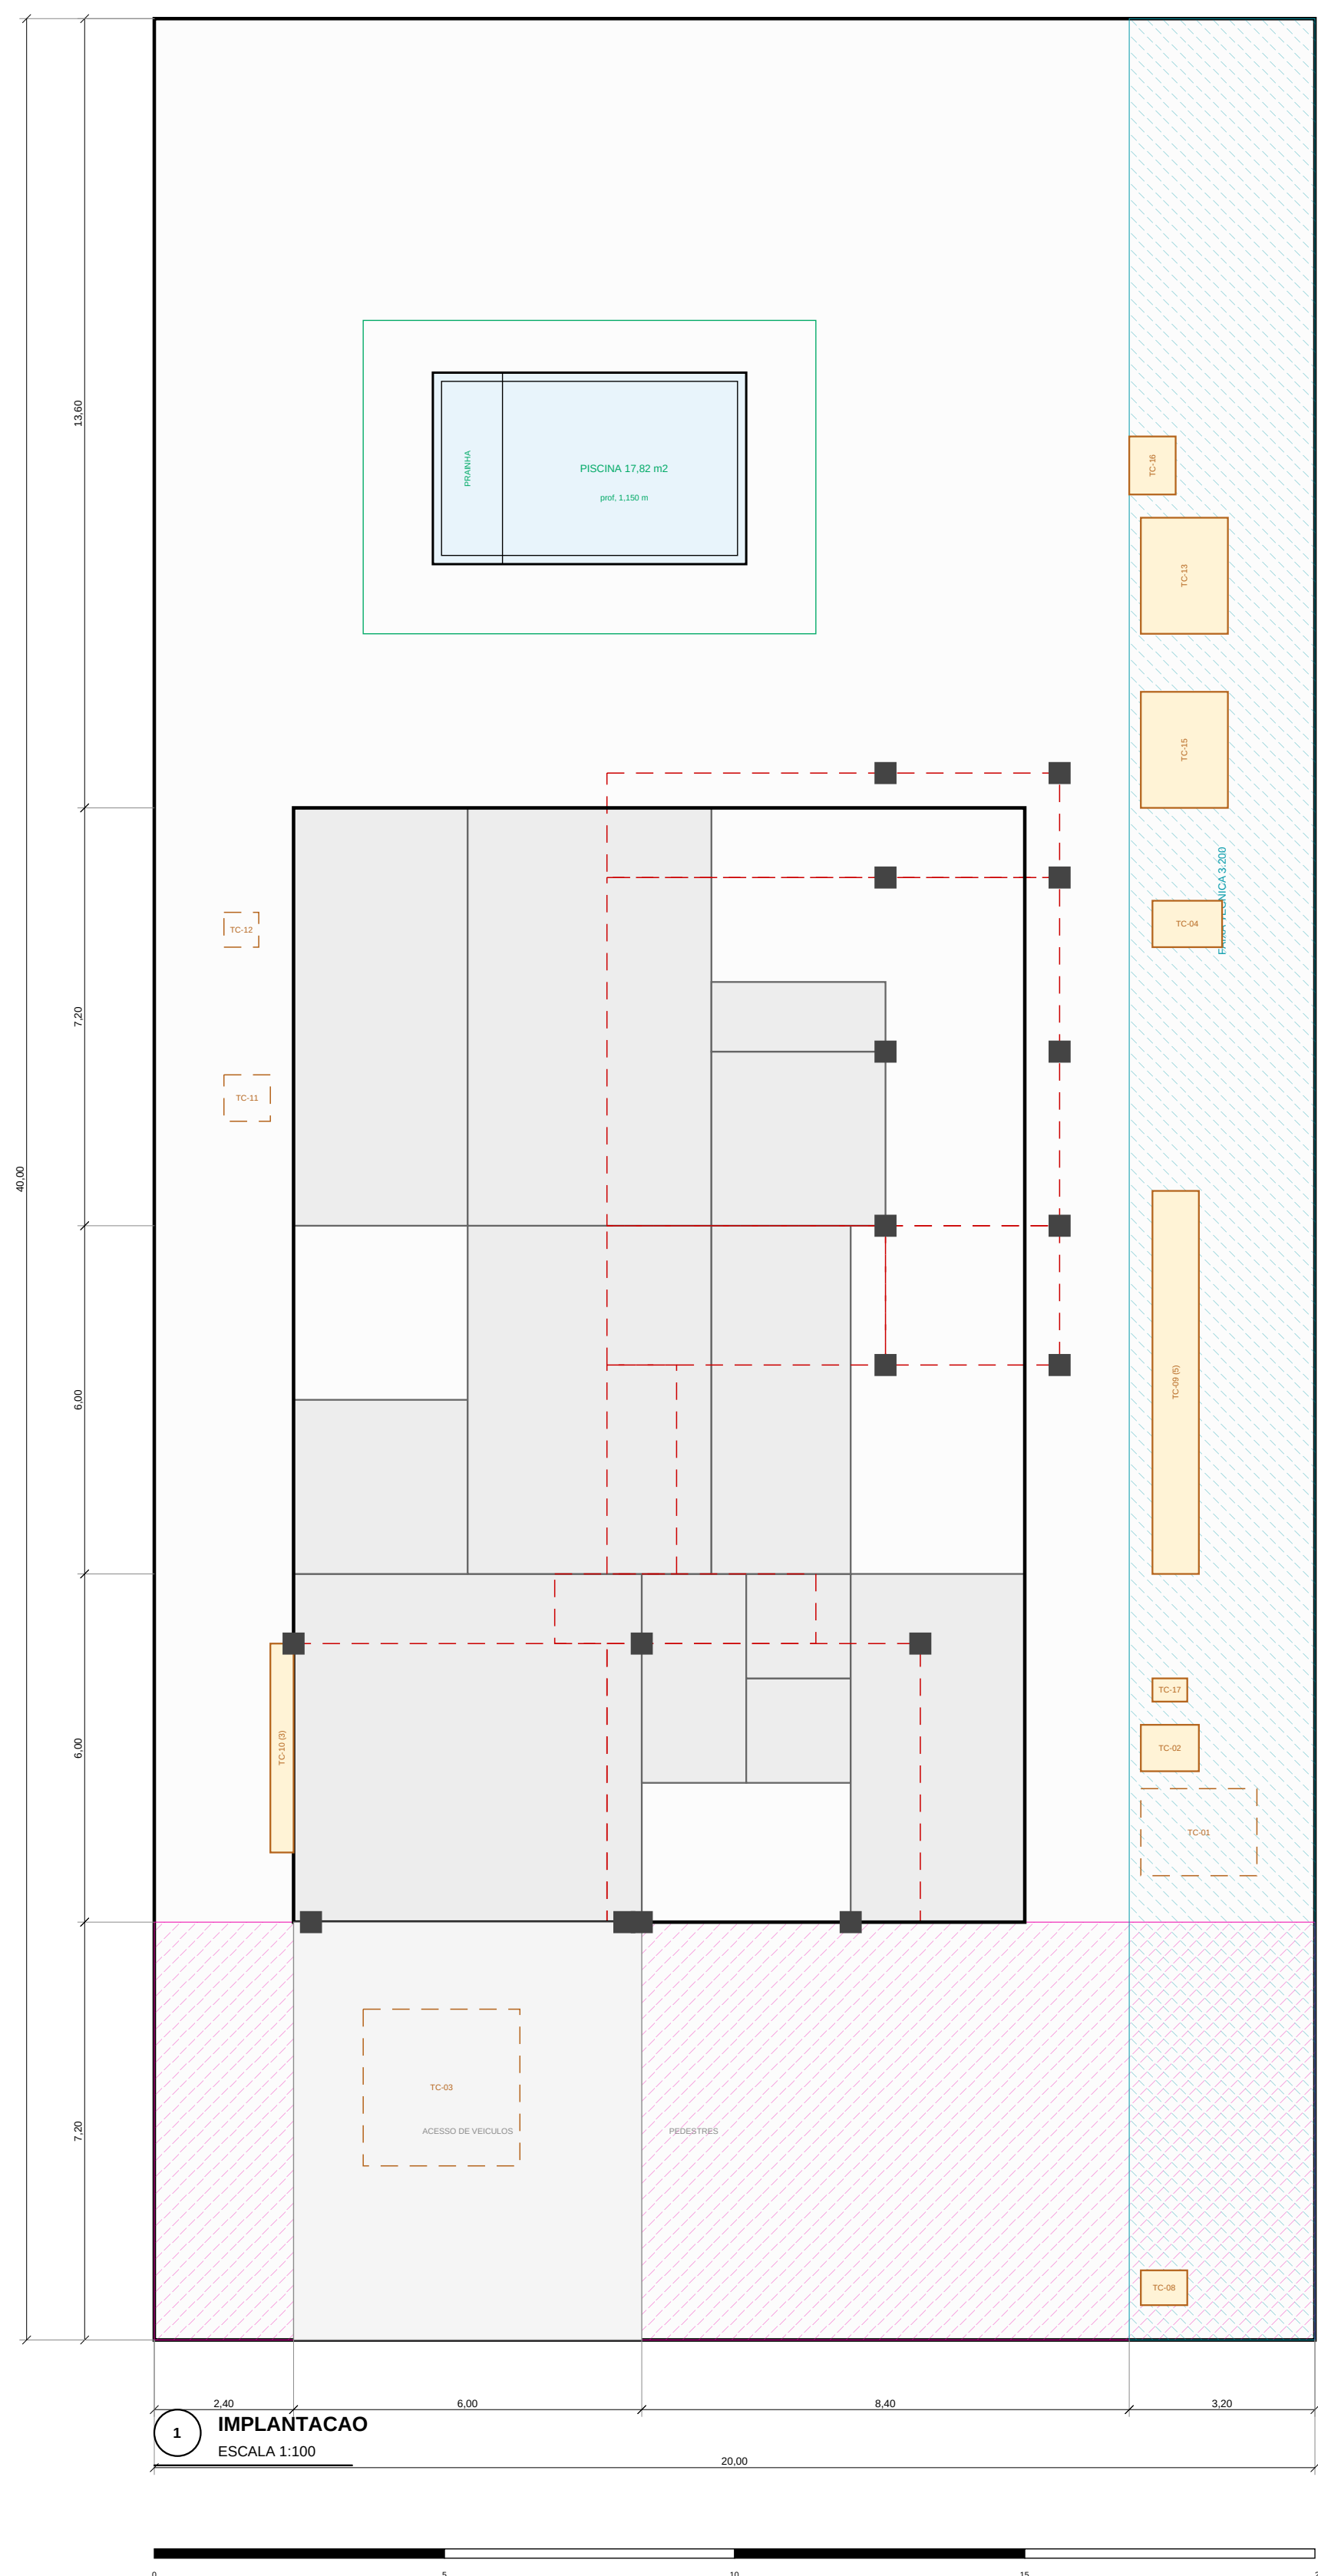

PARAMETRO	PROJETO	LIMITE	
Tipo de compoente	32,67 %	max 50 %	OK
Coef. de aproveitamento	0,284	max 1,00	OK
Cobertura	2 pavimentos	max 4	OK
Relevo frontal	7200 mm	confirma 5500 p/s	OK
Relevo lateral esq.	2400 mm	sem paralelo no diâto	OK
Faixa técnica dir.	3000 mm	sem 3000 mm	OK
Relevo de fundo	3300 mm	sem 3000 mm	OK

- Lote 20.000 x 40.000 mns = 800.000 m2.
- Recuos: frontal 7.200 / lateral esq. 2.400 / faixa técnica de: 3.200 / fundo 13.600 mns.
- Parâmetros de SU05 Tarumã/Tarumã-Açu são hipóteses (H) – pendente certidão de uso do solo.
- Caixa de condomínio: sem muro frontal; muros laterais e de fundo h = 2.200 mns; portões laterais PG06/PG03 na linha da frente da casa.

IMPLANTACAO E SITUACAO

FRANCHIA

01

de 75 REV RES