


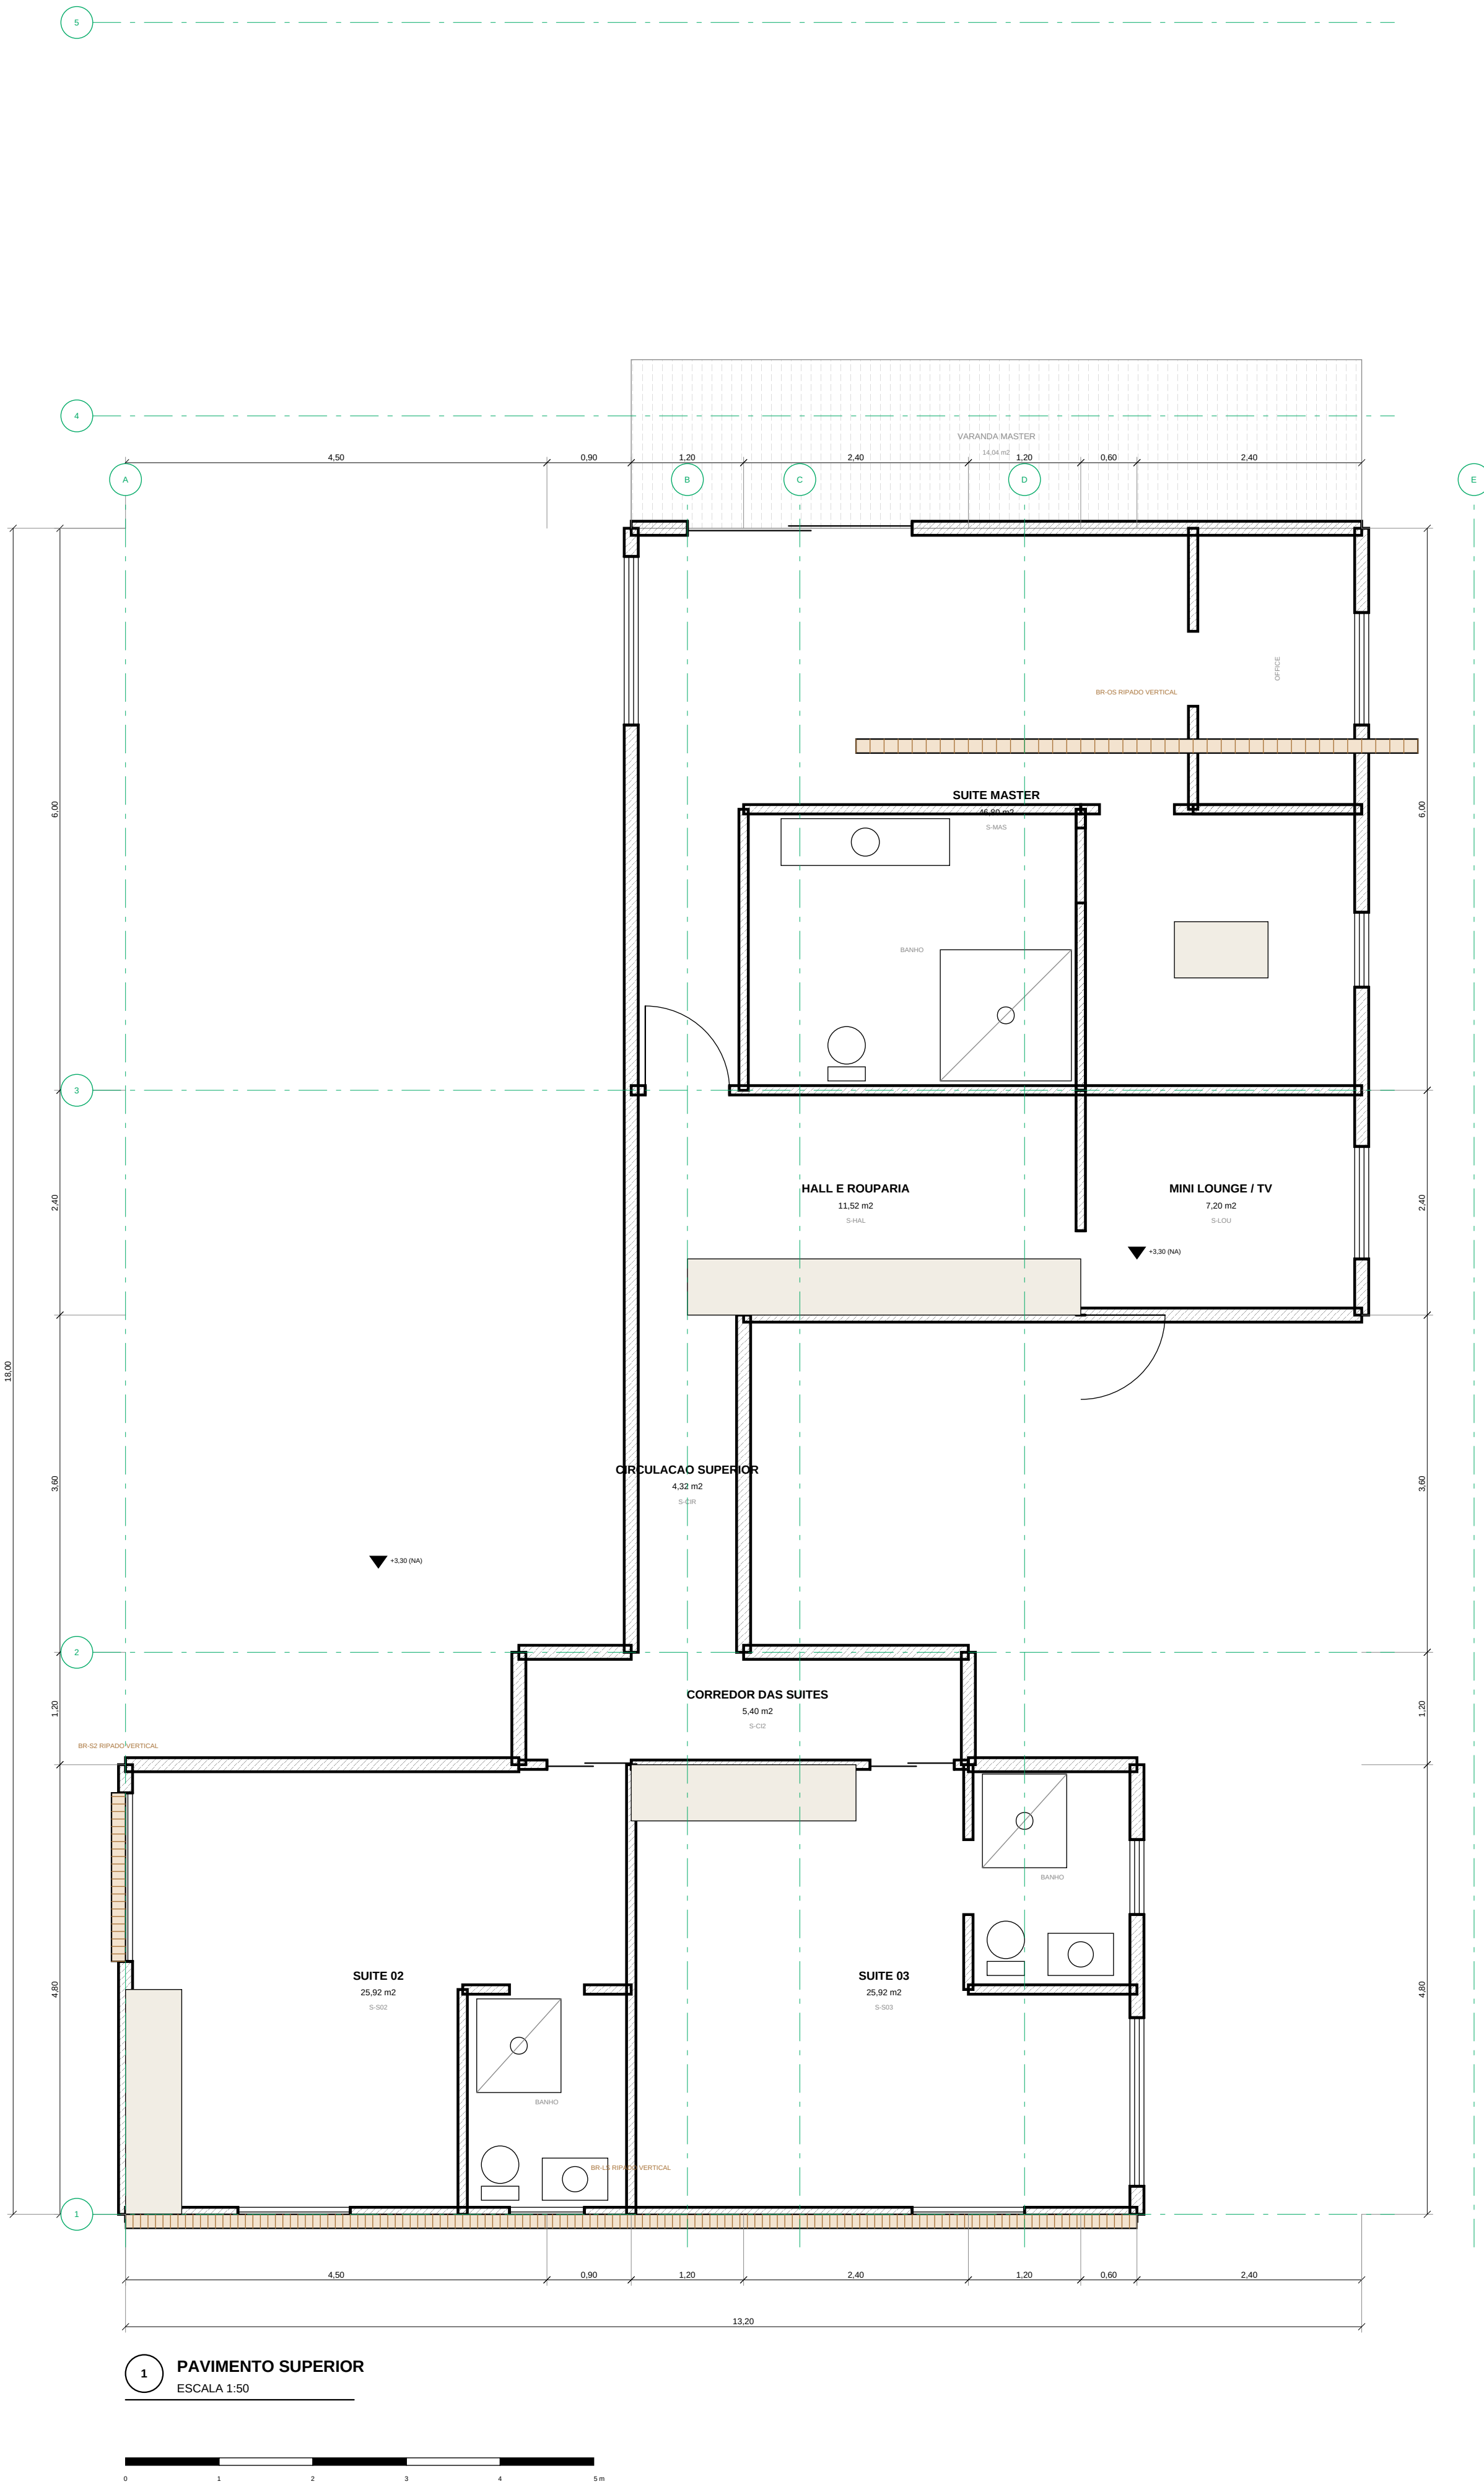


| QUADRO DE ÁREAS — PAVIMENTO SUPERIOR |                        |             |           |
|--------------------------------------|------------------------|-------------|-----------|
| COD                                  | AMBIENTE               | MÓDULO (mm) | ÁREA (m²) |
| S-02                                 | SUITE 02               | 5400x4800   | 25,92     |
| S-03                                 | SUITE 03               | 5400x4800   | 25,92     |
| S-CR                                 | CIRCULAÇÃO SUPERIOR    | 1200x3600   | 4,32      |
| S-C2                                 | CORREDOR DAS SUITES    | 4800x1200   | 5,40      |
| S-HAL                                | HALL E ROUPARIA        | 4800x2400   | 11,52     |
| S-LOU                                | MINI LOUNGE / TV       | 3600x2400   | 7,20      |
| S-MS                                 | SUITE MASTER           | 7800x4800   | 46,80     |
| TOTAL FECHADO                        |                        |             | 127,08    |
| S-BAL                                | VANDELA MASTER (banho) | 7800x1200   | 14,04     |

| MAPA DE ESQUADRIAS DO PAVIMENTO |           |      |     |                                                  |
|---------------------------------|-----------|------|-----|--------------------------------------------------|
| REF                             | VAR (mm)  | DET. | QTD | TPO                                              |
| J01                             | 1200x1200 | 1:30 | 4   | janela de dormitório, suíte                      |
| J04                             | 800x600   | 1:30 | 3   | janela alta de banheiro, banheiro                |
| J05                             | 1800x1200 | 1:30 | 3   | janela ampla de dormitório, suíte                |
| P02                             | 800x1200  | 0    | 2   | porta interna (abertura unilateral)              |
| P05                             | 800x1200  | 0    | 2   | porta DE CORREDOR — sem varão de varanda         |
| P003                            | 3000x4000 | 0    | 1   | porta-balcão de suíte (abertura adicional — var) |

#### LEGENDA E CONVENÇÕES (NBR 6492 / 8403)

- Elemento seccionado pelo plano de corte (N = 1:30 H)
- Ampla vista / linha de esquadria
- Mobiliário fixo, equipamentos e simbologia
- Projeto do pavimento superior e da cobertura
- Eixo modular e linha de corte
- Linha de corte e linha auxiliar

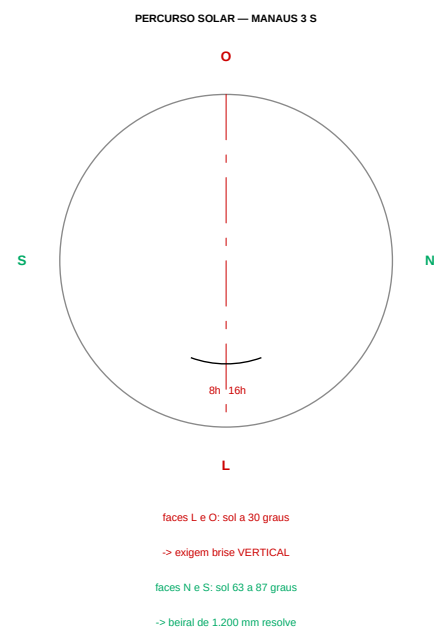

- NOTAS
- Dimensões em milímetros; cotas de nível em metros.
  - Malha modular 600 mm; cotas elev. a 0,00.
  - Planta externa 120 mm / distância interna 120 mm (S).
  - Mobiliário fixo indica pontos de água e energia (NBR 6492).

#### PROJETO PORTO REAL

RESIDÊNCIA UNIFAMILIAR (MANUS - AM) | SUITE TATIANA (PS)

PROJETO ARQUITETÔNICO

#### PLANTA BAIXA — PAVIMENTO SUPERIOR

| BASE GEOMÉTRICA     | ESCALA            | EMISSÃO                | PROVA |
|---------------------|-------------------|------------------------|-------|
| Unia Consolidada    | 1:50              | ESTÚDIO PRELIMINAR RIS | 03    |
| PS-RIS (previsão)   | FORMATO A1        | UNO LIBERADO PARA ORÇÁ | 03    |
| UNIDADE MÉTRICA: mm | MALHA 600/600 (S) | SEM ART / RNT          | 03    |