


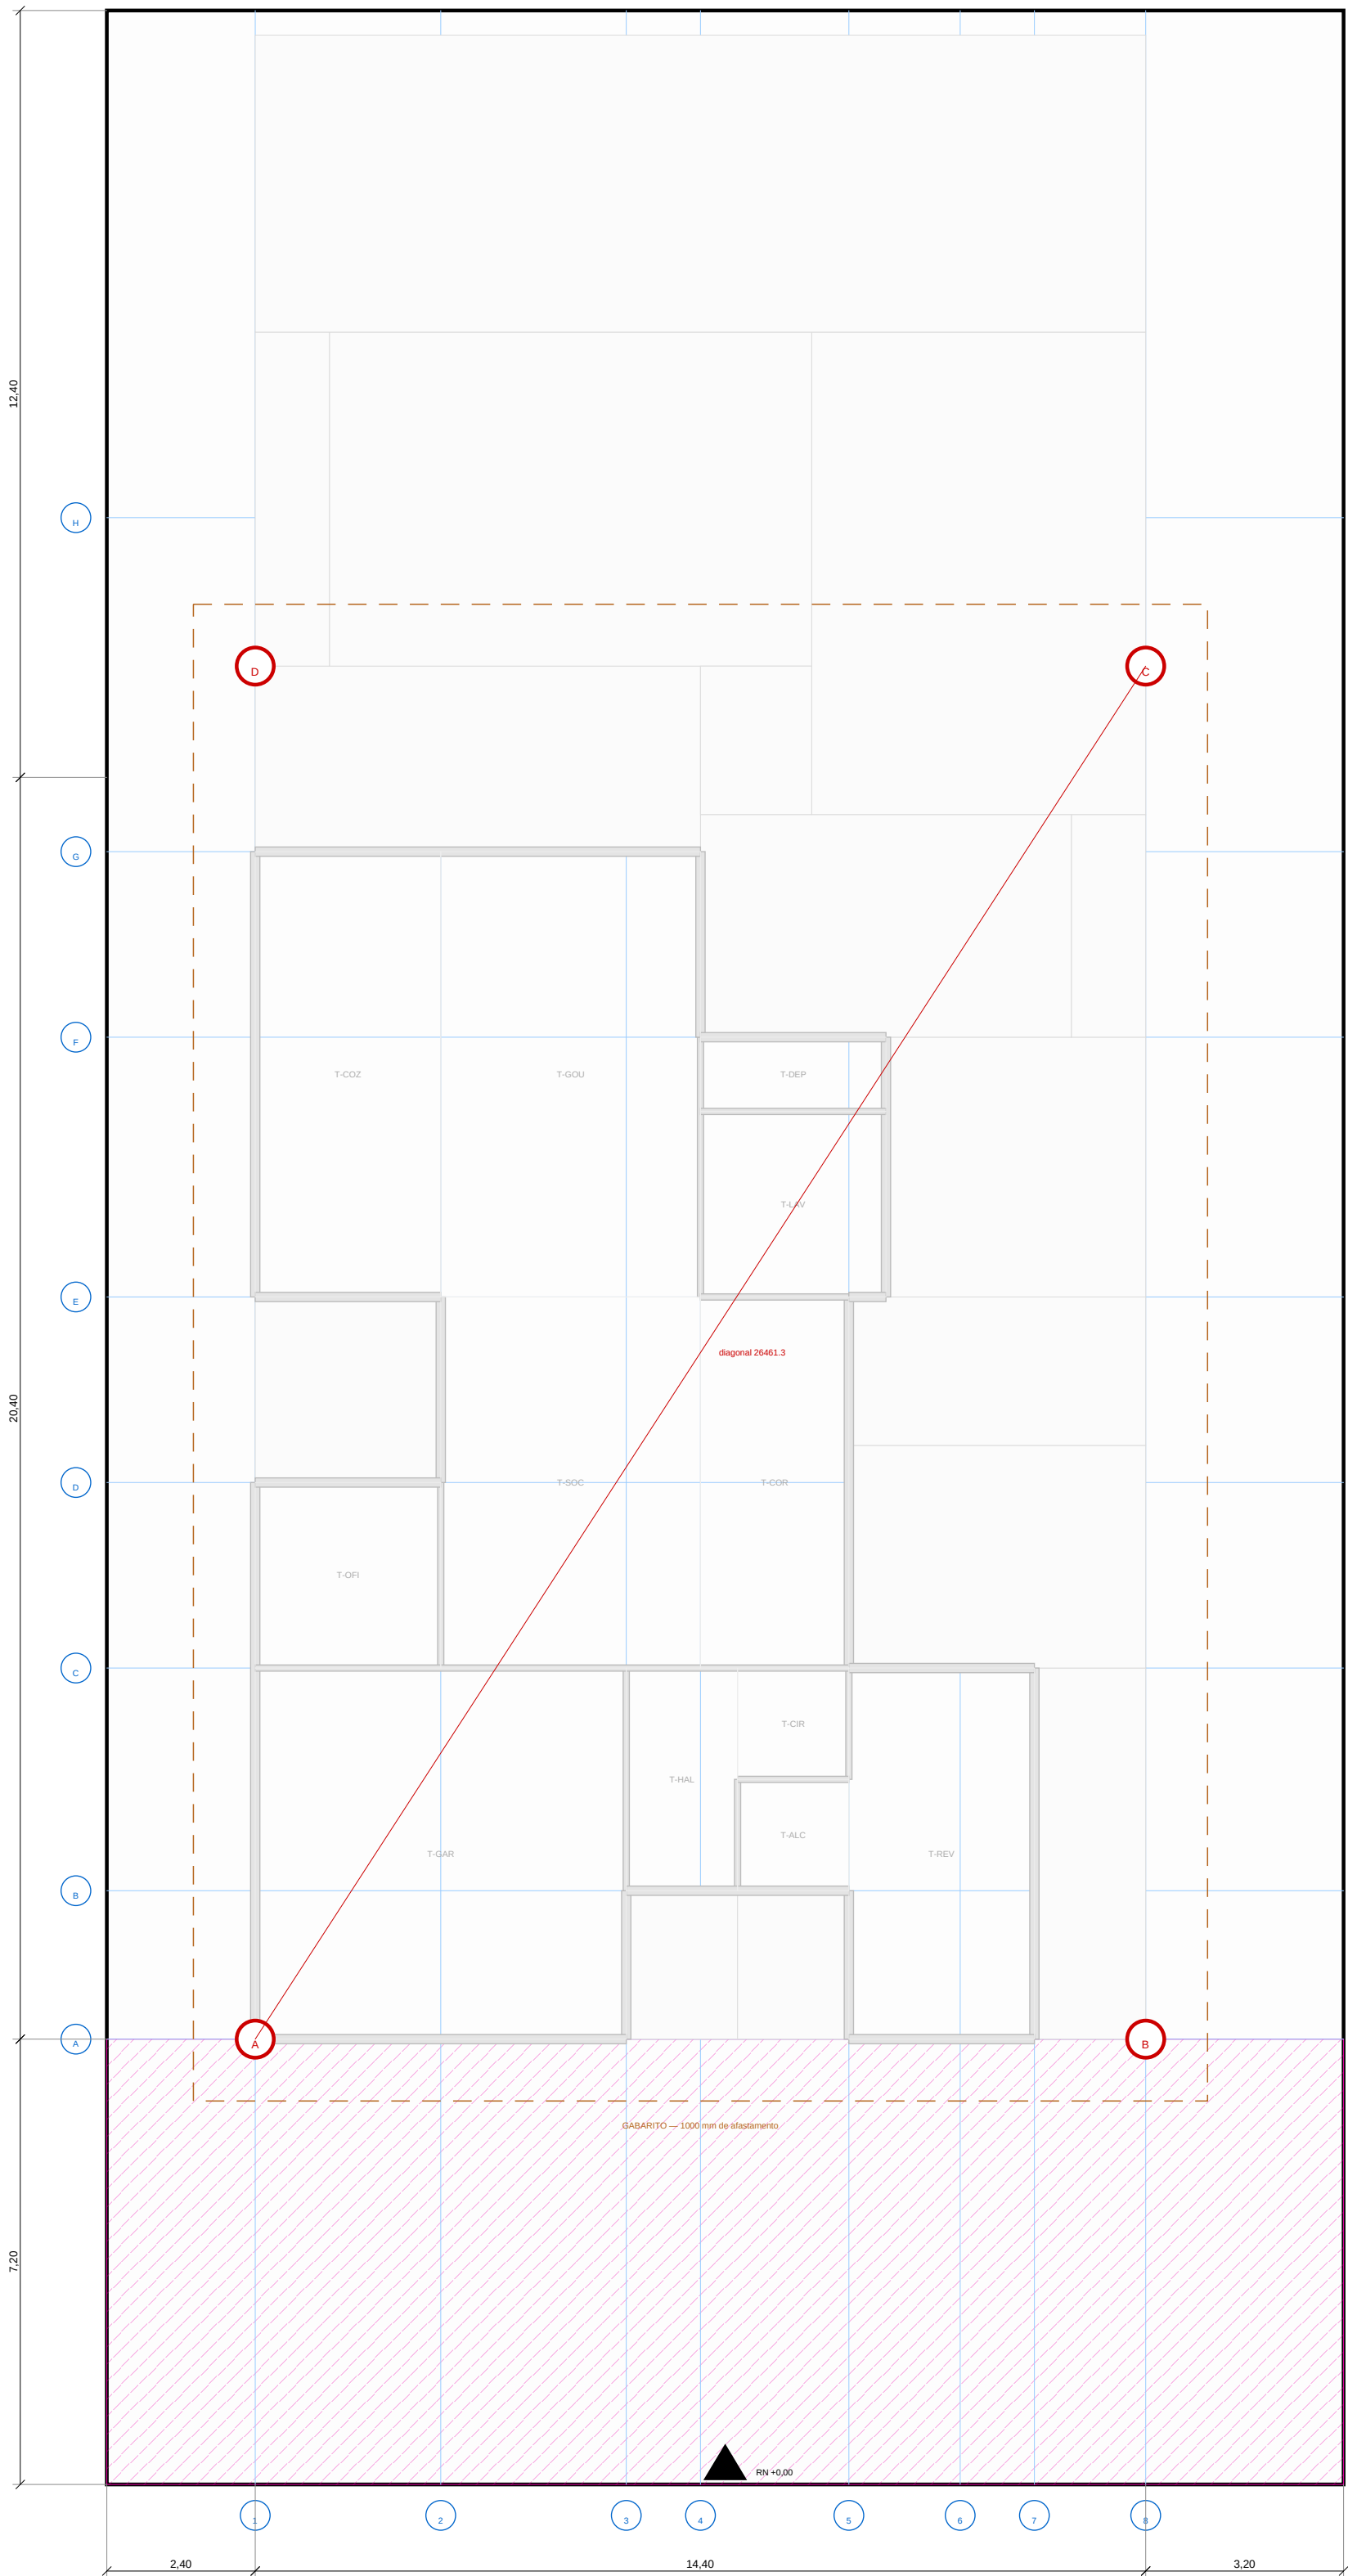

1. LOCALIZAÇÃO — EIXOS E COORDENADAS
ESCALA 1:100

COORDENADAS DOS CANTOS (mm)

CANTO	X	Y	DIVISA SUL	DIVISA NORTE	TESTADA	QUILÔMETRO	DIAGONAL
A	2400	7200	2400	17600	7200	32800	26461,3
B	18800	7200	18800	3200	7200	32800	26461,3
C	18800	28400	18800	3200	28400	19600	26461,3
D	2400	28400	2400	17600	28400	19600	26461,3

PROCEDIMENTO DE LOCALIZAÇÃO

#	PARÂMETRO	CRITÉRIO DE AVALIAÇÃO
1	Conferir as divisas com o matriculado e o memorial de lote	divergência acima de 10 mm interrompe a locação
2	Identificar o PNM (plano de concreto 200 x 200 x 100 mm) fora da área de obra	fora da área de obra
3	Montar o gabarito a 1000 mm do cantoneiro	perpendicular 75 x 75 x tubos 20 x 100
4	Marcar os eixos X (L) e Y (L) e X (L) e Y (L) no gabarito	linha coordenada múltipla de 200 mm
5	Colar cado canto dos QUADs (quadrantes)	verificar em cado: erro de cado de soma
6	Conferir a diagonal A-C	26461,3 mm com tolerância de 20 mm
7	Conferir o quadrado por 3-4-5 em cada canto	antes de qualquer concretagem
8	Registrar em ata com foto e modelo	gabarito continuo nos dois lados do lote, conferência

EIXOS MODULARES

DIREÇÃO	VALORES (mm)
X (L) e Y (L)	2400 - 5400 - 8400 - 9600 - 12600 - 13800 - 15000 - 18000
Y (L) e X (L)	7200 - 9600 - 13200 - 14200 - 15000 - 28400 - 29400 - 32800
Módulo	principal 600 mm - submúltiplo 300 mm
Origem	canto frontal esquerdo do lote
Unidade	milímetros

NOTAS

- 1. Localizar o eixo de referência em que o erro não tem impacto direto a casa de lotes.
- 2. Cada canto e cada um dos QUADs (quadrantes), marca em cado acumulada — erro de cado soma, erro de referência independente não.
- 3. Conferência obrigatória para diagonal 26461,3 mm entre A e C antes de concretar o lote.
- 4. Ats no ato de locação, alinhado ao medidor TC-06, com 0,001 m por acerto do terreno.

PROJETO PORTO REAL

RESIDÊNCIA UNIFAMILIAR (MANSÃO) - AM | 100% TUBO (PI)

PROJETO ARQUITETÔNICO

LOCALIZAÇÃO DE OBRA E GABARITO

BASE GEOMÉTRICA Linha Consolidada Projeto (previsão) Unidade: metros (m)	ESCALA 1:100 Formato A1 Módulo: 600/300 (mm)	EXIBIÇÃO ESTUDO PRELIMINAR RBS Linha Consolidada PARA OBRA SEM ART / RNT	PROJETO 31 em 18 REVIS
---	---	---	------------------------------