


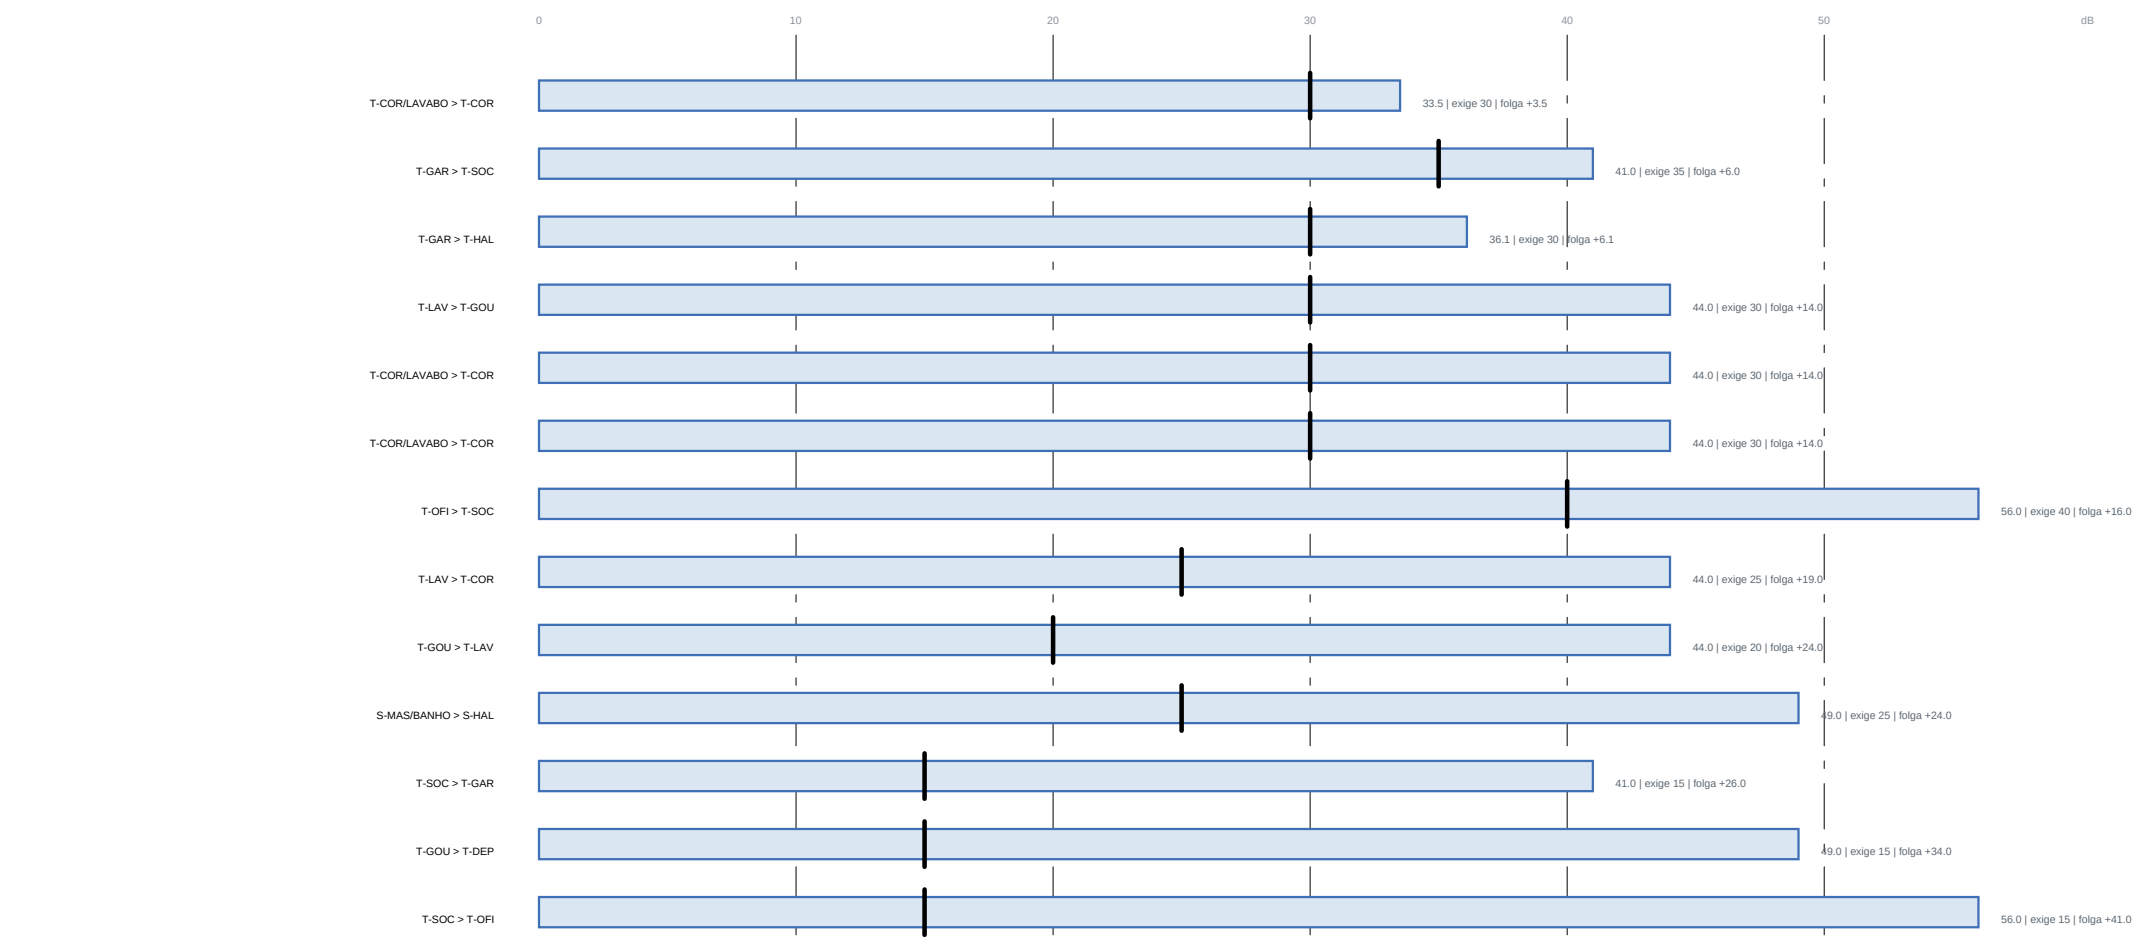

Barra = isolamento obtido; traço vertical = exigido (valor da fonte menos limite do receptor, NBR 15102)

O QUE MUDOU EM R52

ONDE	ANTES	DEPOIS	POR QUE
Banho compartilhado > hall de entrada	porta de correr (Rw 25) — conjunto de 20,2 dB	parede CEGSA, 44 dB	o acesso de volta passou para a circulação
Banho compartilhado > quarto eventual	porta com (Rw 25) — conjunto de 25,5 dB, exigia 25	parede CEGSA, 44 dB	era a por passagem da casa, e não era a saída
Hall > garagem	porta com — 36,9 dB, exigia 35	PIGIs todos vedada — 50,9 dB	porta entre garagem e casa tem todos todos para ser mudeia
Banho compartilhado > circulação	nao havia porta	PIGIs todos vedada — 35,7 dB, exigia 25	unico acesso do banho, e abria para fora
Bloco do chuveiro	encostado na parede do hall	canto arredondado, todo a janela alta	consequencia da porta nova, a regra dos 900 cm de bloco reaproveita a primeira bridade

TABELAS ADOTADAS

ITEM	VALOR	FONTE
Fonte: caixa sanitária	75 dB(A)	prática corrente de acústica
Fonte: bloco do chuveiro	75 dB(A)	prática corrente de acústica
Fonte: cozinha e gourmet	75 dB(A)	prática corrente de acústica
Fonte: sala e jantar	75 dB(A)	prática corrente de acústica
Fonte: garagem	75 dB(A)	prática corrente de acústica
Fonte: máquina de lavar e secar	75 dB(A)	prática corrente de acústica
Fonte: oficina	80 dB(A)	prática corrente de acústica
Limite: banho	45 dB(A)	NBR 15102:2017 (circulação e entrada adiabática)
Limite: circulação	45 dB(A)	NBR 15102:2017 (circulação e entrada adiabática)
Limite: cozinha	45 dB(A)	NBR 15102:2017 (circulação e entrada adiabática)
Limite: depósito	55 dB(A)	NBR 15102:2017 (circulação e entrada adiabática)
Limite: dormitório	35 dB(A)	NBR 15102:2017 (circulação e entrada adiabática)
Limite: entrada	45 dB(A)	NBR 15102:2017 (circulação e entrada adiabática)
Limite: estar	45 dB(A)	NBR 15102:2017 (circulação e entrada adiabática)
Limite: garagem	55 dB(A)	NBR 15102:2017 (circulação e entrada adiabática)
Limite: office	45 dB(A)	NBR 15102:2017 (circulação e entrada adiabática)
Limite: oficina	55 dB(A)	NBR 15102:2017 (circulação e entrada adiabática)
Limite: serviço	55 dB(A)	NBR 15102:2017 (circulação e entrada adiabática)
Fonte: acústica	Pin 25 dB	Nota de mercado declarada
Fonte: sonar	Pin 25 dB	Nota de mercado declarada
Fonte: sala	Pin 25 dB	Nota de mercado declarada
Fonte: sala de	Pin 25 dB	Nota de mercado declarada
Fonte: sala de visita	Pin 30 dB	Nota de mercado declarada

NOTAS

1 Esta planilha serve para o proprietário perguntar o que 100 verificações não sabem responder: quem entra na casa ouve o chuveiro do banheiro da entrada?

2 Ouviu. A parede era tipo (P) 1, Pin 44 e a porta era do tipo (P) 25, o conjunto entregava 20 dB. Em acústica o édo (P) 20 dB — não se faz media aritmética do isolamento, se soma energia que passa.

3 Isolamento se se exige ENTRE portas. Dentro da file social o lado não e definido, e o programa.

4 O aditivo igual ao 10 (compensação decorada), não e pre-verificação de projeto, não enviado de campo da NBR 15107-3.

PROJETO PORTO REAL

RESIDENCIA UNIFAMILIAR (MANSÃO - AM) | SOBR TATIANA-PS

PROJETO ARQUITETONICO

DESEMPENHO ACUSTICO ENTRE AMBIENTES

BASE GEOMETRICA	ESCALA	EMISSAO	PROVA
Lista Consolidada	s/ escala	ESTUDO PRELIMINAR RIB	
Pin R52 (previsão)	FORMATO A1	NAO LIBERADO PARA OBRA	39
UNIDADE MESTRE: mm	MILHA 605000000	SEM ART / RNT	60-70 REVIEWS