



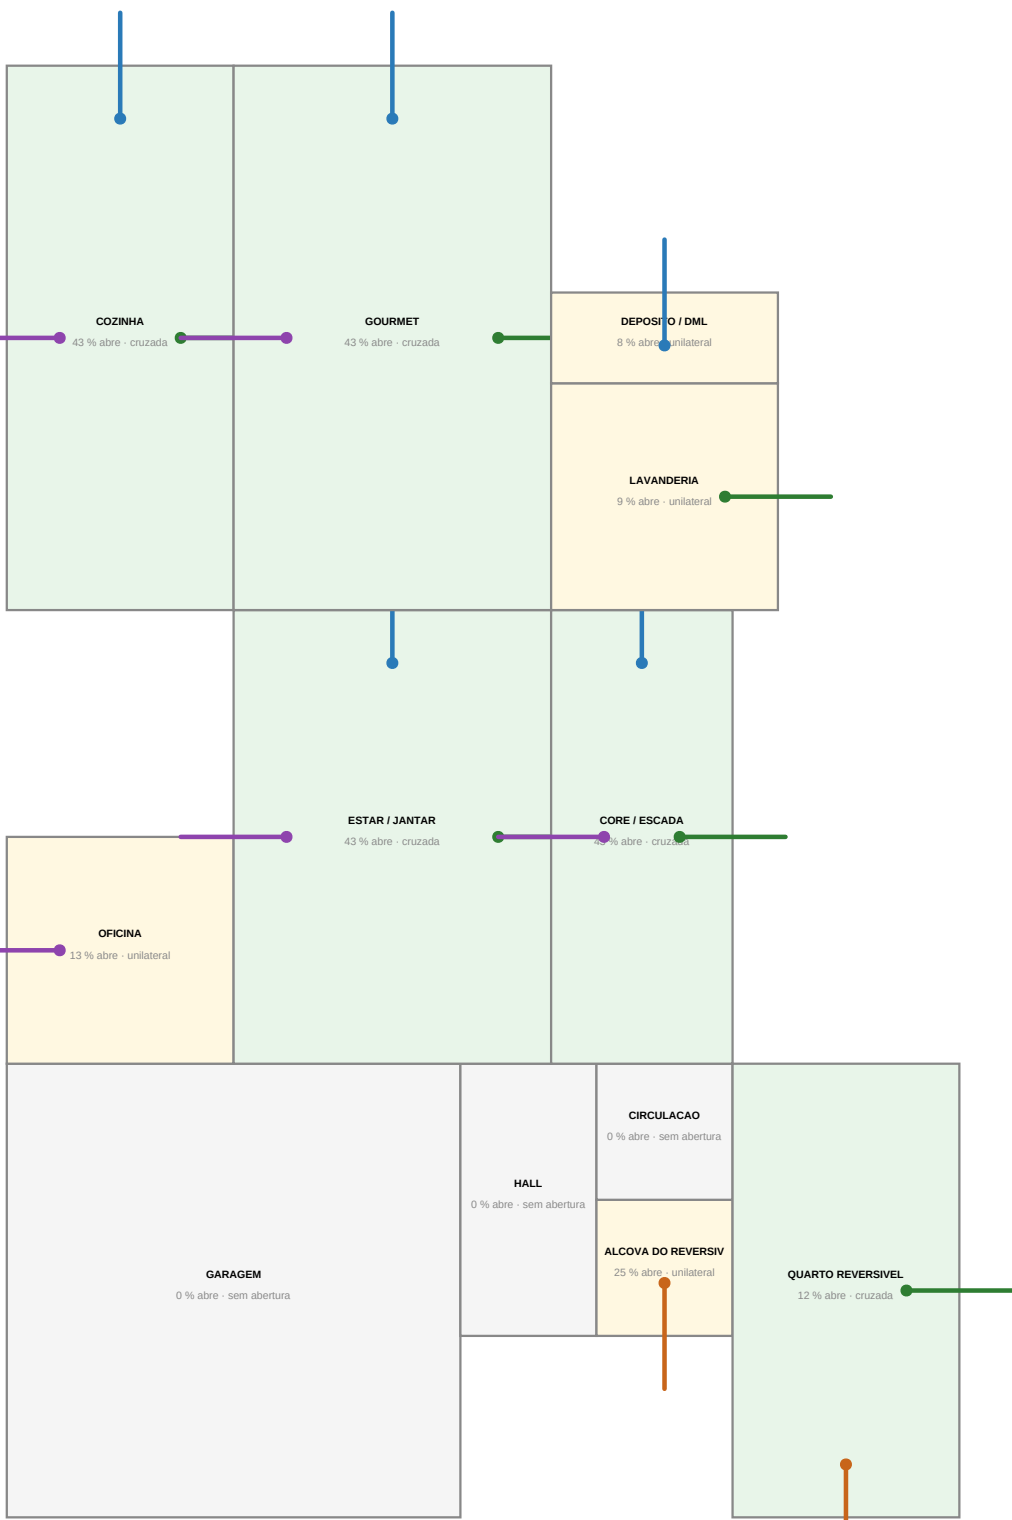

1 TERREO — faces que abrem
ESCALA 1:100

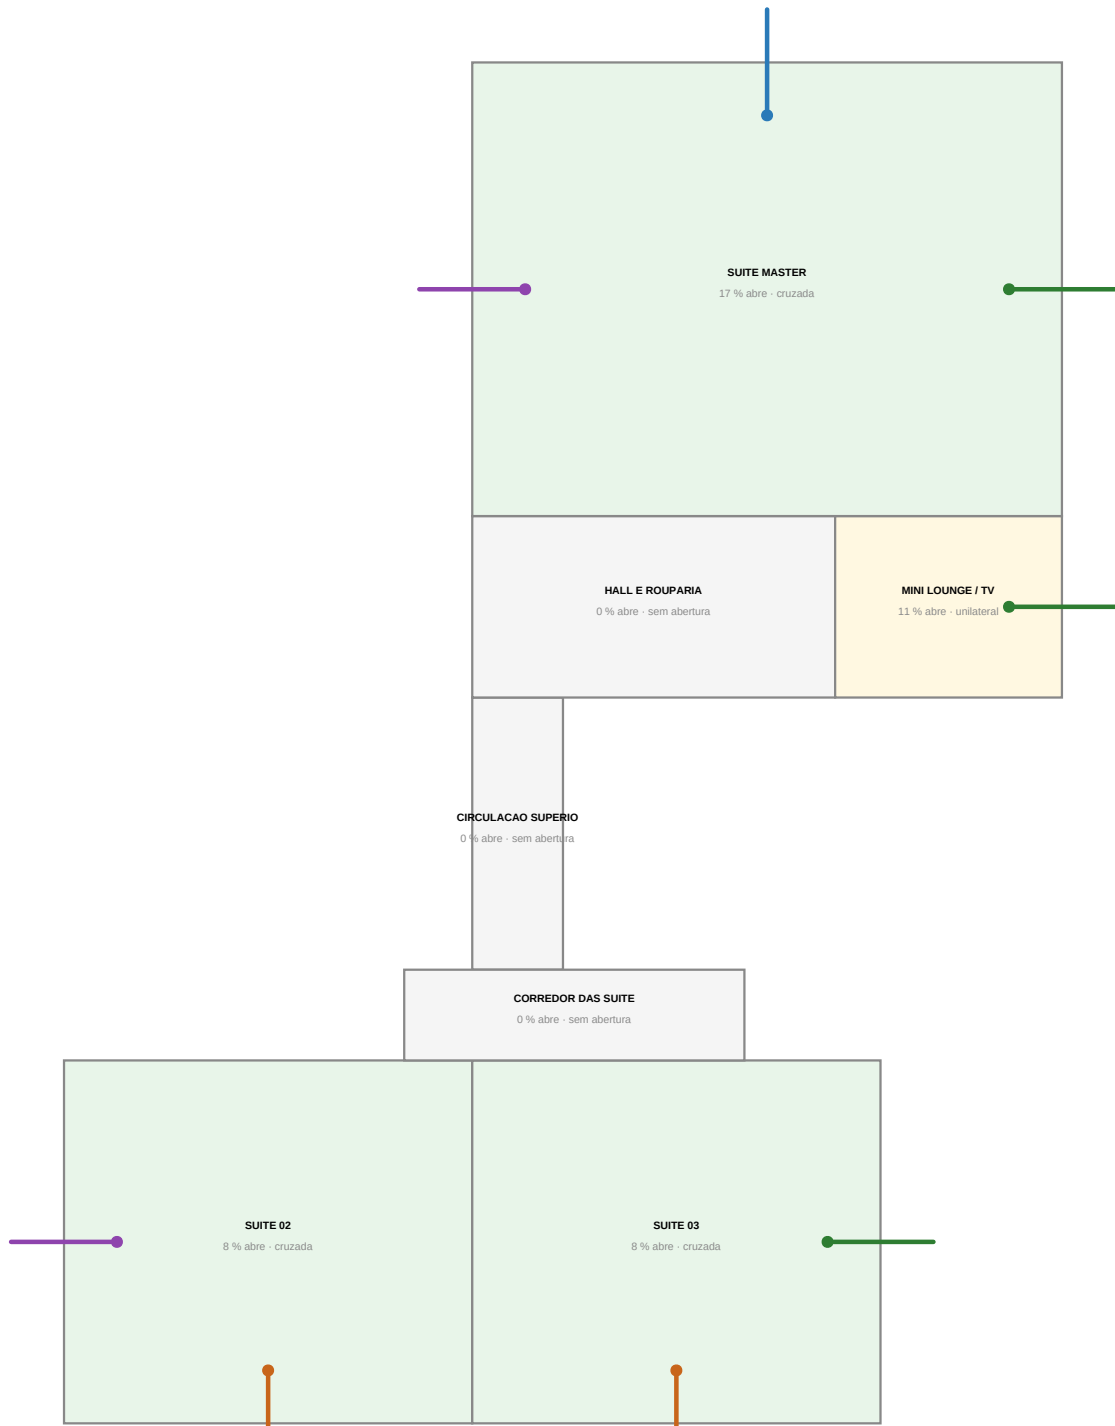

2 SUPERIOR — faces que abrem
ESCALA 1:100

VENTILACAO POR AMBIENTE

COD	AMBIENTE	CAT.	PRO. m²	ABRE. m²	PERÍM.	FACIES	TIPO	NOTA
T-GAR	GARAGEM	INTERIO	36,3	0,00	0 m	—	—	YES
T-HALL	HALL	INTERIO	5,8	0,00	0 m	—	—	YES
T-ALC.	ALCOVA DO REVERSIVEL	INTERIO	2,8	0,72	20 m	L	unidirecional	OK
T-COR	CIRCULACAO	INTERIO	2,8	0,00	0 m	—	—	YES
T-REV.	QUARTO REVERSIVEL	INTERIO	26,7	2,04	22 m	L, N	cruzada	OK
T-OFI	OFICINA	INTERIO	4,3	1,08	22 m	S	unidirecional	YES
T-BDC	ESTAR/JANTAR	INTERIO	86,7	36,86	43 m	N, D, S	cruzada	OK
T-COR	CORR. E ESCADA	INTERIO	86,7	36,86	43 m	N, D, S	cruzada	YES
T-COZ	COZINHA	INTERIO	86,7	36,86	43 m	N, D, S	cruzada	OK
T-GOU	GOURMET	INTERIO	86,7	36,86	43 m	N, D, S	cruzada	OK
T-LAV	LAVANDERIA	INTERIO	5,3	0,72	9 m	N	unidirecional	YES
T-DEP.	DEPOSITO DmL	INTERIO	3,1	0,24	8 m	O	unidirecional	YES
S-S02	SUITE 02	INTERIO	26,5	2,04	8 m	L, S	cruzada	OK
S-S03	SUITE 03	INTERIO	26,7	2,04	8 m	L, N	cruzada	OK
S-COR	CIRCULACAO SUPERIOR	INTERIO	3,8	0,00	0 m	—	—	YES
S-COZ	CORREDOR DAS SUITES	INTERIO	4,6	0,00	0 m	—	—	YES
S-HALL	HALL E ROUPARIA	INTERIO	10,6	0,00	0 m	—	—	YES
S-LOU	MINI LOUNGE / TV	INTERIO	9,5	0,72	11 m	N	unidirecional	OK
S-MAST	SUITE MASTER	INTERIO	44,9	7,60	17 m	N, D, S	cruzada	OK

PRIVACIDADE — CADA JANELA CONTRA A DIVISA QUE OLHA (art. 1.301 CC)

VAO	AMB	FACE	DIST. m	MIN. m	PROTEC.	BRSE	LEITURA	
004	T-REV	N	8,00	1,50	1500	—	distante	OK
002	T-COR	N	8,00	1,50	1500	—	distante	OK
005	T-REV	L	7,20	—	1100	BR-L	fus	OK
001	T-REV	N	8,00	1,50	1100	—	distante	OK
003	T-ALC.	L	9,60	—	1000	—	fus	OK
006	T-COZ	S	3,40	1,50	1100	—	aproxim do vidro	OK
001	T-COZ	S	3,40	1,50	1100	—	aproxim do vidro	OK
001	T-LAV	N	7,48	1,50	1100	—	distante	OK
004	T-DEP.	O	35,80	1,50	1500	—	distante	OK
PRO2	T-COR	N	8,00	1,50	9	—	distante	OK
PRO2	T-GOU	N	30,40	1,50	9	—	distante	OK
PRO1	T-GOU	O	33,60	1,50	9	BR-O	perseguido por fenda	OK
PRO2	T-BDC	S	5,40	1,50	9	—	distante	OK
001	S-GOU	N	4,40	1,50	1100	—	distante	OK
005	S-S02	S	3,40	1,50	1100	—	aproxim do vidro	OK
001	S-S02	L	7,20	—	1100	BR-L	fus	OK
004	S-S02	L	7,20	—	1200	BR-L	fus	OK
005	S-S03	N	6,80	1,50	1100	—	distante	OK
001	S-S03	L	7,20	—	1100	BR-L	fus	OK
004	S-S03	N	6,80	1,50	1200	—	distante	OK
005	S-MAS	S	7,80	1,50	1100	—	distante	OK
PRO2	S-MAS	O	14,80	1,50	9	—	distante	OK
004	S-MAS	N	4,40	1,50	1500	—	distante	OK
001	S-MAS	N	4,40	1,50	1100	—	distante	OK

NOTAS

* Área que ABRE por ambiente contra a área do piso. NBR 15275-4 exige 0 m na região Norte. NBR 15275-3 recomenda 40 m na ZSB (abertura grande).

* Facies que abrem por fachada (FC) contra a parede lateral 200 m, janela de corte 50 %, baseado 33 %, porta opaca 0 %.

* Privacidade pelo art. 1.301 do Código Civil: janela que olha a divisa a menos de 2,50 m e protegida. O brise que protege esta norma.

* Seis em cada face com abertura, duas de mais faces = ventilação cruzada.

PROJETO PORTO REAL

RESIDENCIA UNIFAMILIAR (MANSÃO - AM) | SOUS TATIANA-PS

PROJETO ARQUITETONICO

VENTILACAO NATURAL, CRUZADA E PRIVACIDADE

BASE GEOMETRICA	ESCALA	ENTRADA	PRIVACIDADE
União Consolidada	1:100	ESTUDO PRELIMINAR RBS	49
ISO-R2D (previsão)	FORMATO A1	ISO LIBERADO PARA OBRA	ISO 78 REVIEWS
UNIDADE MESTRE: AM	MALHA 6050X3050	SEM ART / RNT	