
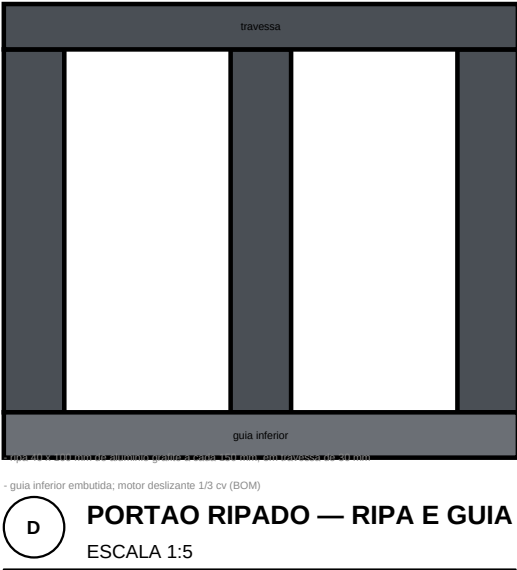
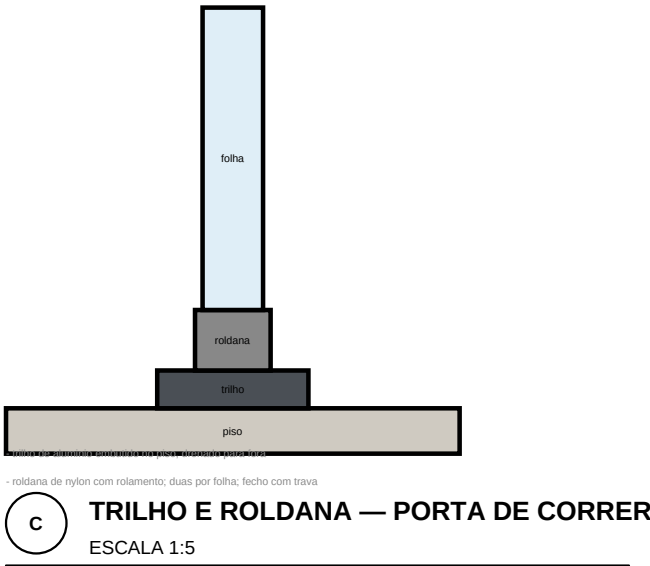
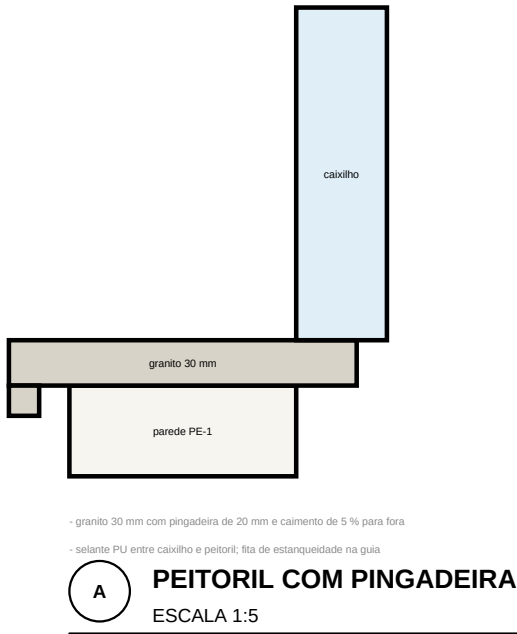
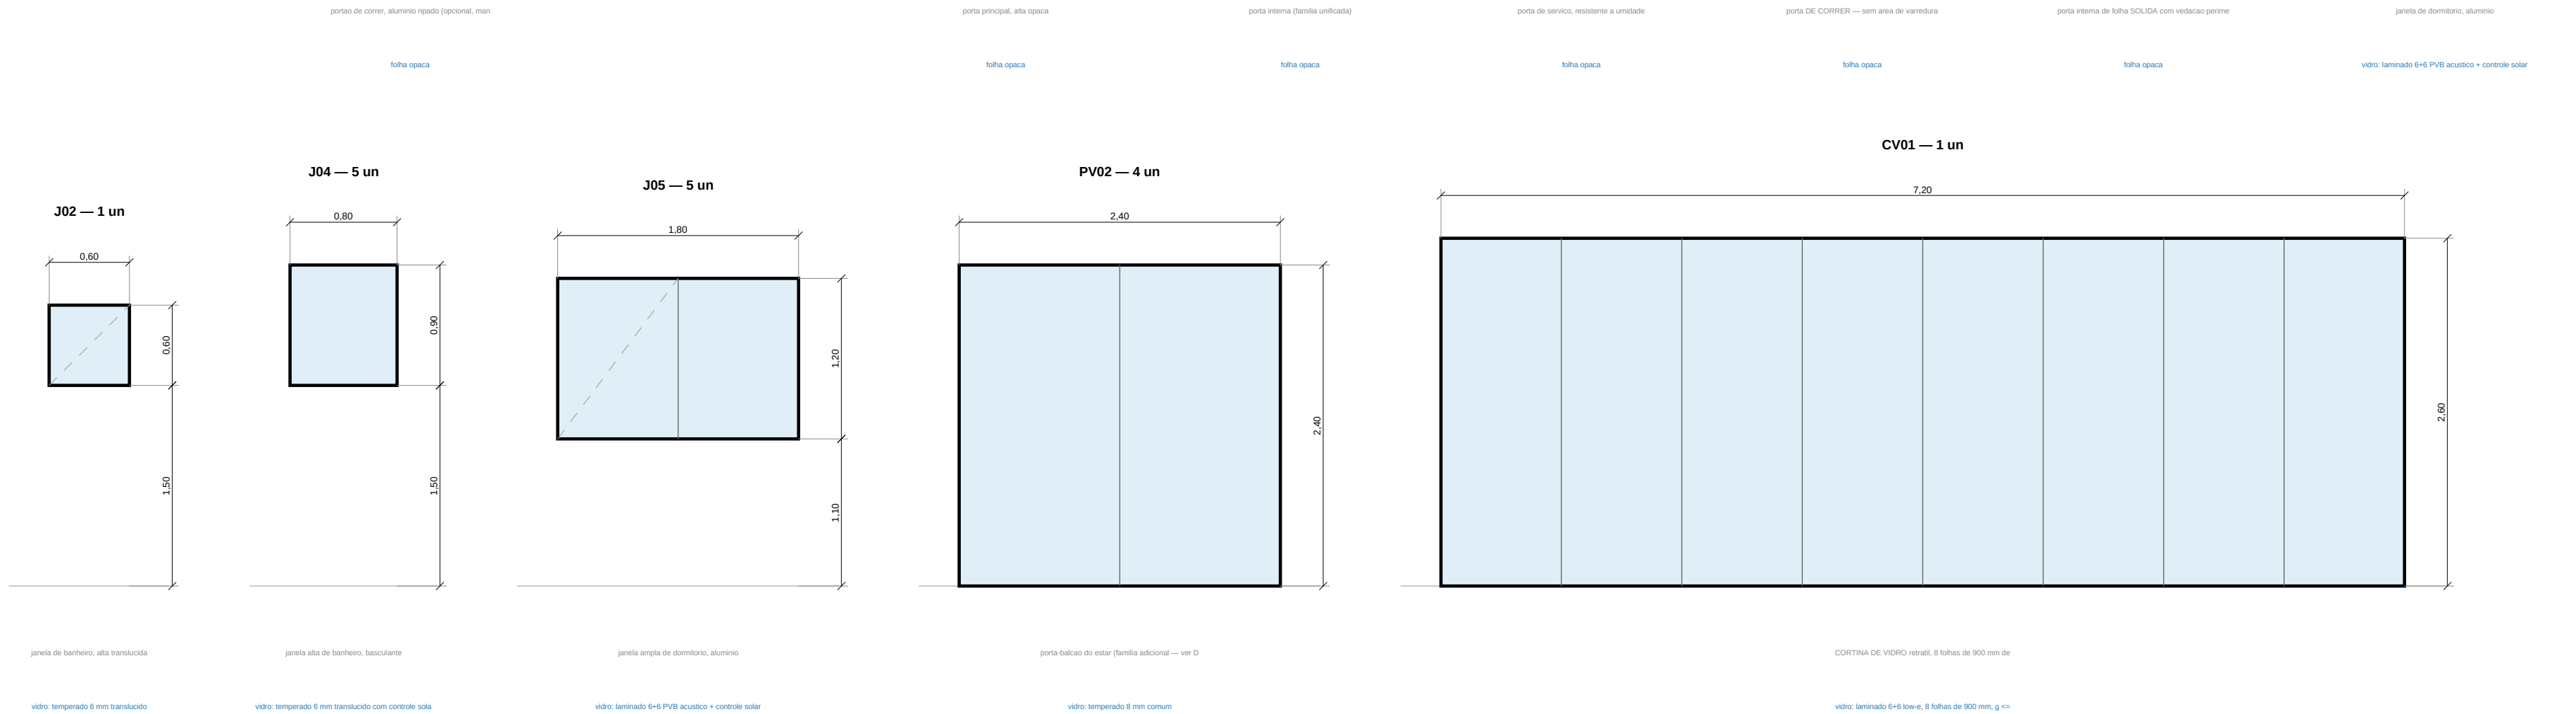


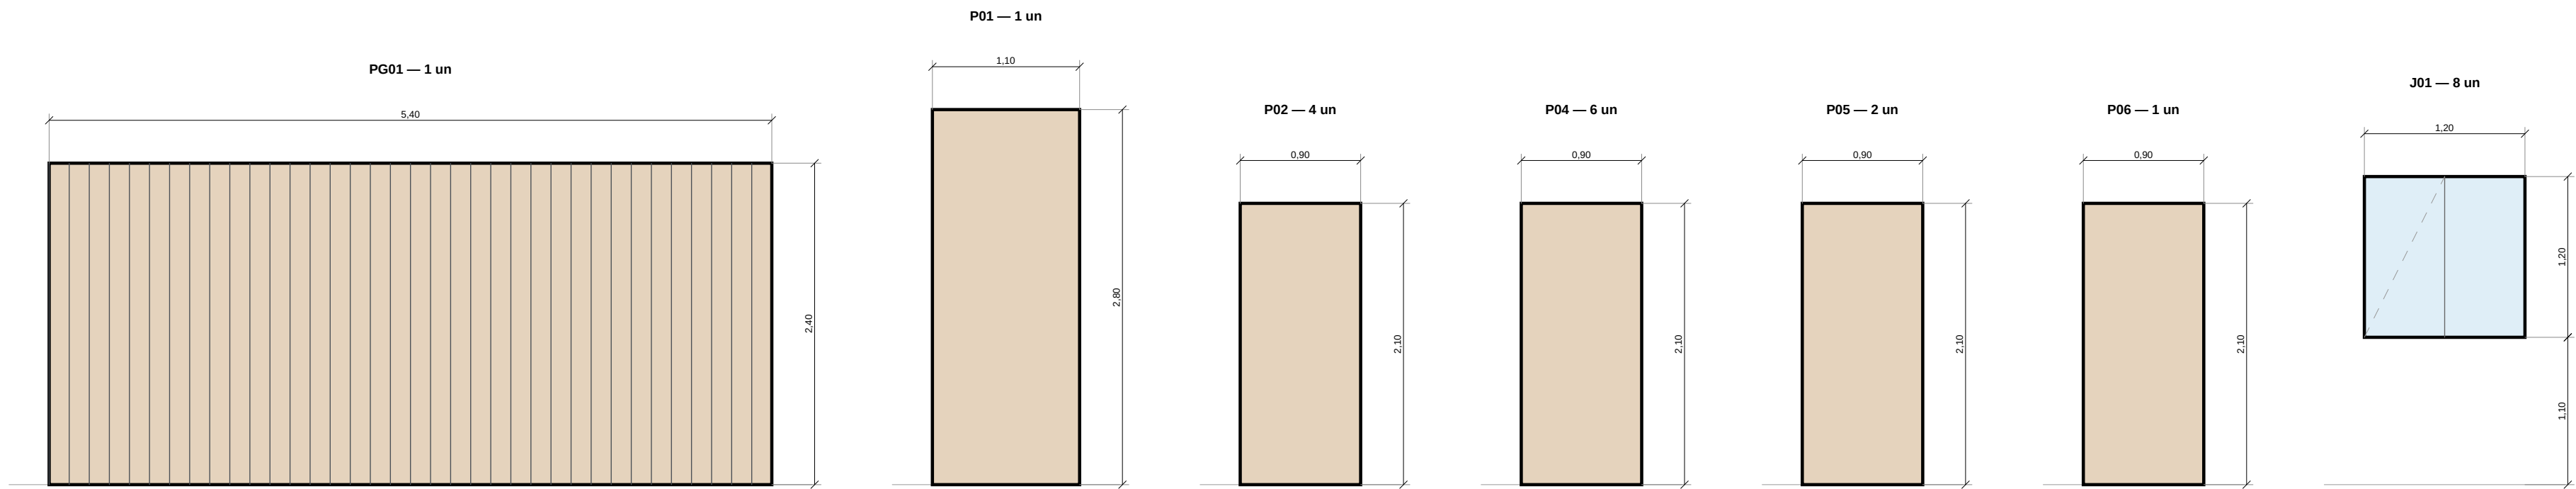

- NOTAS
- 1. Uma referência por família em uso, com largura e altura, perfil, quantidade e o vidro que a ripa de fator solar (perfil vidro_R_Vidro).
 - 2. Famílias declaradas SEM USO (J02, PV02) ficam fora, enquanto que não está em VACOS não é comprada.
 - 3. Detalhes 1:5 — perfil com pingadeira, sulcos de porta externa, trilho e sistema de porta de correr, ripa e guia de perfil — são os quatro elementos que decidem a estanqueidade.
 - 4. Acabamento grates em todas as famílias (ACABADA_MATEMATICA), sem PVC, sem venozado.

PROJETO PORTO REAL			
RESIDENCIA UNIFAMILIAR (MARIAUS - AM) SOUZA TATIANA-PS			
PROJETO ARQUITETONICO			
ESQUADRIAS — TIPOS, QUANTIDADES E DETALHES			
BASE GEOMETRICA	ESCALA	EMISSAO	PROJECION
Unia Consolidada	1:40 • 1:5	ESTUDIO PRELIMINAR RIB	52
Projeto (previsão)	FORMATO A1	NAO LIBERADO PARA OBRA	SEM ART / RNT
UNIDADE METRICA: mm	MILHA 405/500/500		6/18 REVISO